

1. IT IS NOT ALLOWED TO REPRODUCE THE SHEETS CONTENTS IN ANY FORM EXCEPT FOR THE PURPOSE FOR WHICH IT IS INTENDED.
2. THESE DRAWINGS ARE DIAGRAMMATIC AND SHALL NOT BE SCALED. ADDITIONAL DATA SHALL BE REQUESTED FROM THE CONSULTANCY THROUGH WRITTEN CLARIFICATION. VERIFY ALL EXISTING CONDITIONS AND DIMENSIONS BEFORE PROCEEDING WITH ANY PORTION OF ANY WORK.
3. NO CHANGES, MODIFICATIONS OR DEVIATIONS SHALL BE WRITTEN PERMISSION FROM **ALMASAH ENGINEERING CONSULTANTS**.
4. ALL WORK AS OUTLINED IN THESE DOCUMENTS, SHALL STRICTLY CONFORM TO ALL APPLICABLE CODES. IN THE EVENT OF A CONFLICT, THE MORE STRINGENT REQUIREMENT SHALL GOVERN AND BE MET.

حُكُومَةُ الشَّارِقَةِ
دائرة الشؤون الإسلامية

المحاسبة
للاستشارات الهندسية
مشاريع فقط
AL-Masah
Engineering Consultant
Drawings Only



SETTING OUT PLAN

STIA SM 02

<u>Built Up Area Schedule</u>			
S.NO	FLOOR DETAILS	AREA	
		SQ.M	SQ.FT
1	Masjid Area	180.20	1938.95
2	Ablution Block Area	72.16	776.44
3	Imam House Area	126.26	1358.56
Total Built Up Area		378.62	4073.95


[illegible]

SETTING OUT PLAN

SCALE 1:100

GROUND FLOOR PLAN

SCALE 1:100

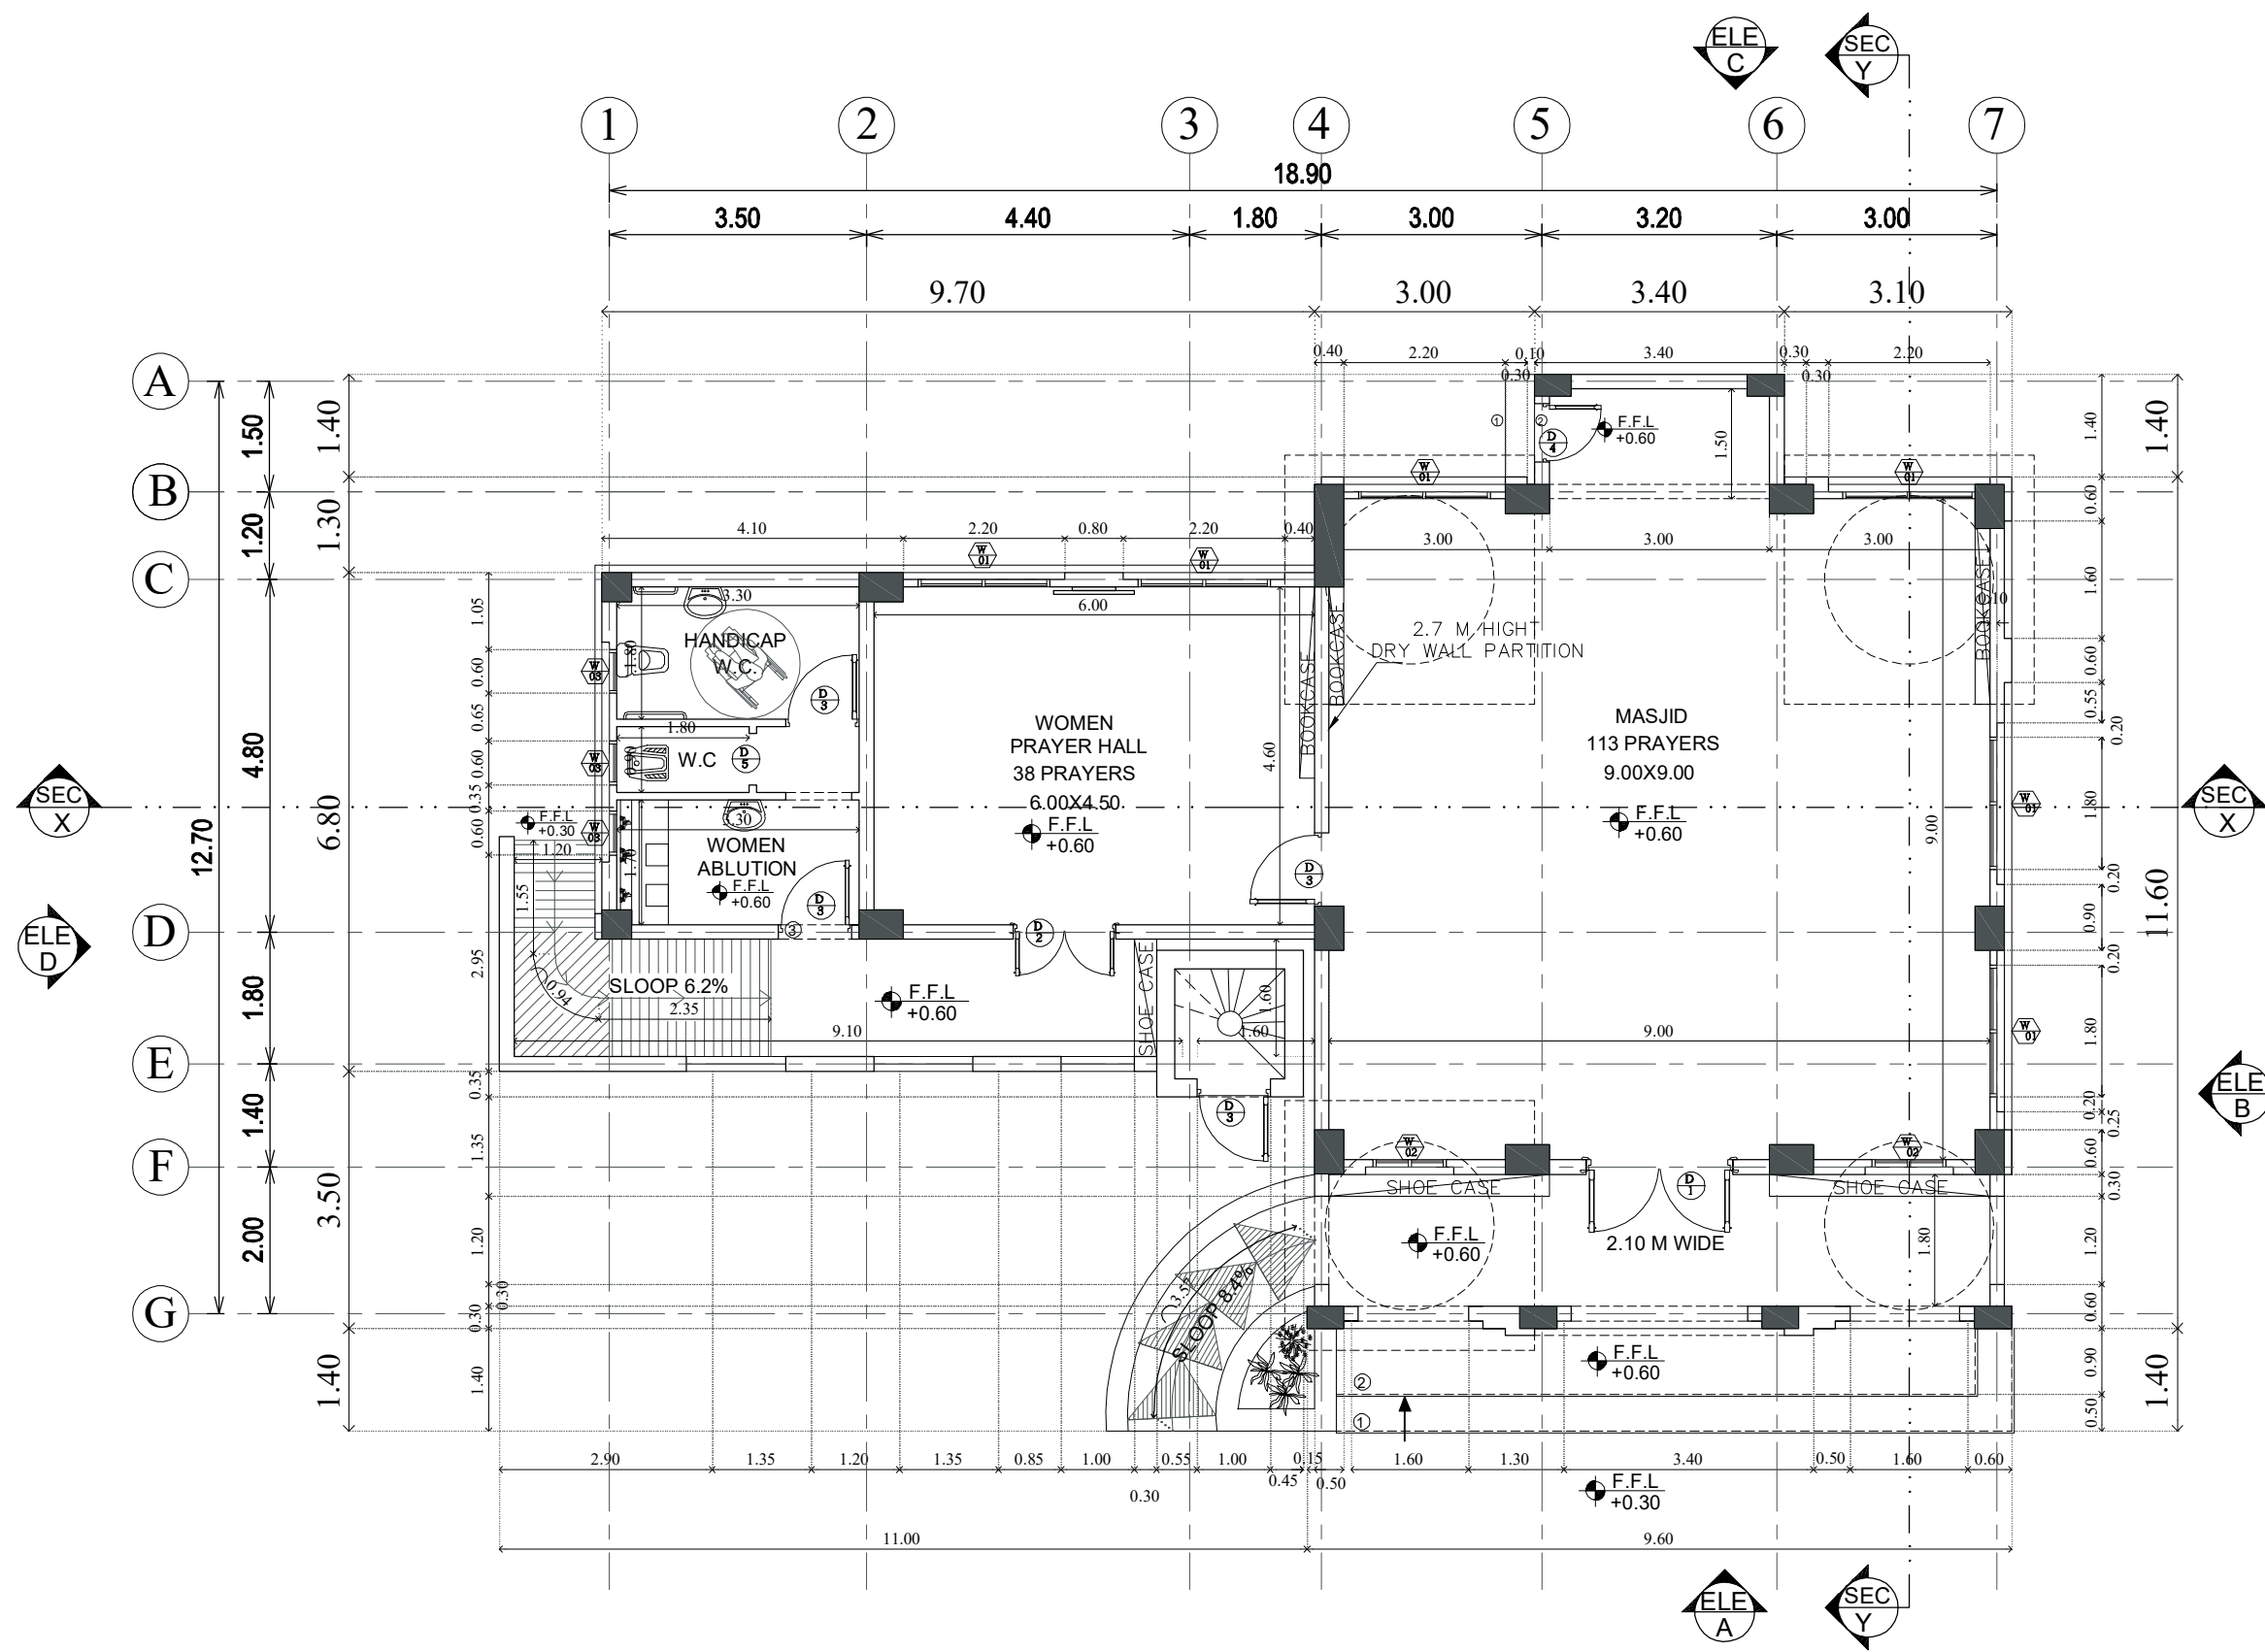

GENERAL NOTES:

- 1.IT IS NOT ALLOWED TO REPRODUCE THE SHEETS CONTENTS IN ANY FORM EXCEPT FOR THE PURPOSE FOR WHICH IT IS INTENDED.
2. THESE DRAWINGS ARE DIAGRAMMATIC AND SHALL NOT BE SCALED. ADDITIONAL DATA SHALL BE REQUESTED FROM THE CONSULTANCY THROUGH WRITTEN CLARIFICATION. VERIFY ALL EXISTING CONDITIONS AND DIMENSIONS BEFORE PROCEEDING WITH ANY PORTION OF ANY WORK.
3. NO CHANGES, MODIFICATIONS OR DEVIATIONS SHALL BE WRITTEN PERMISSION FROM **ALMASAH ENGINEERING CONSULTANTS**.
4. ALL WORK AS OUTLINED IN THESE DOCUMENTS, SHALL STRICTLY CONFORM TO ALL APPLICABLE CODES. IN THE EVENT OF A CONFLICT, THE MORE STRINGENT REQUIREMENT SHALL GOVERN AND BE MET.



SIA - SM-03



حكومة الشارقة
دائرة الشؤون الإسلامية

CONSULTANT STAMP



Sharjah ☎ 06 5 444 521 ☎ 06 5 444 523 ☎ Office: 306, Al Fisal 2 Bldg., King Fisal St.

CLIENT:

GOVERNMENT OF SHARJAH -
DEPARTMENT OF ISLAMIC AFFAIRS

PROJECT:

(SIA - SM-03)
PROPOSED MASJID + ABLUTION +
IMAM HOUSE

SHEET TITLE:

GROUND FLOOR PLAN

ARCHITECT

Arch. Mostafa Ramadan

TYPE

ARCHITECTURE

STRUCTURAL

Eng : Mohamed Gomaa

SHEET

No.

A -02

CHECKED BY

Eng : Mohamed Attia

Location :

Plot No :

SCALE

1:100

DATE

February - 2022


Project

No.

SIA - SM-03

ROOF FLOOR PLAN

SCALE 1:100

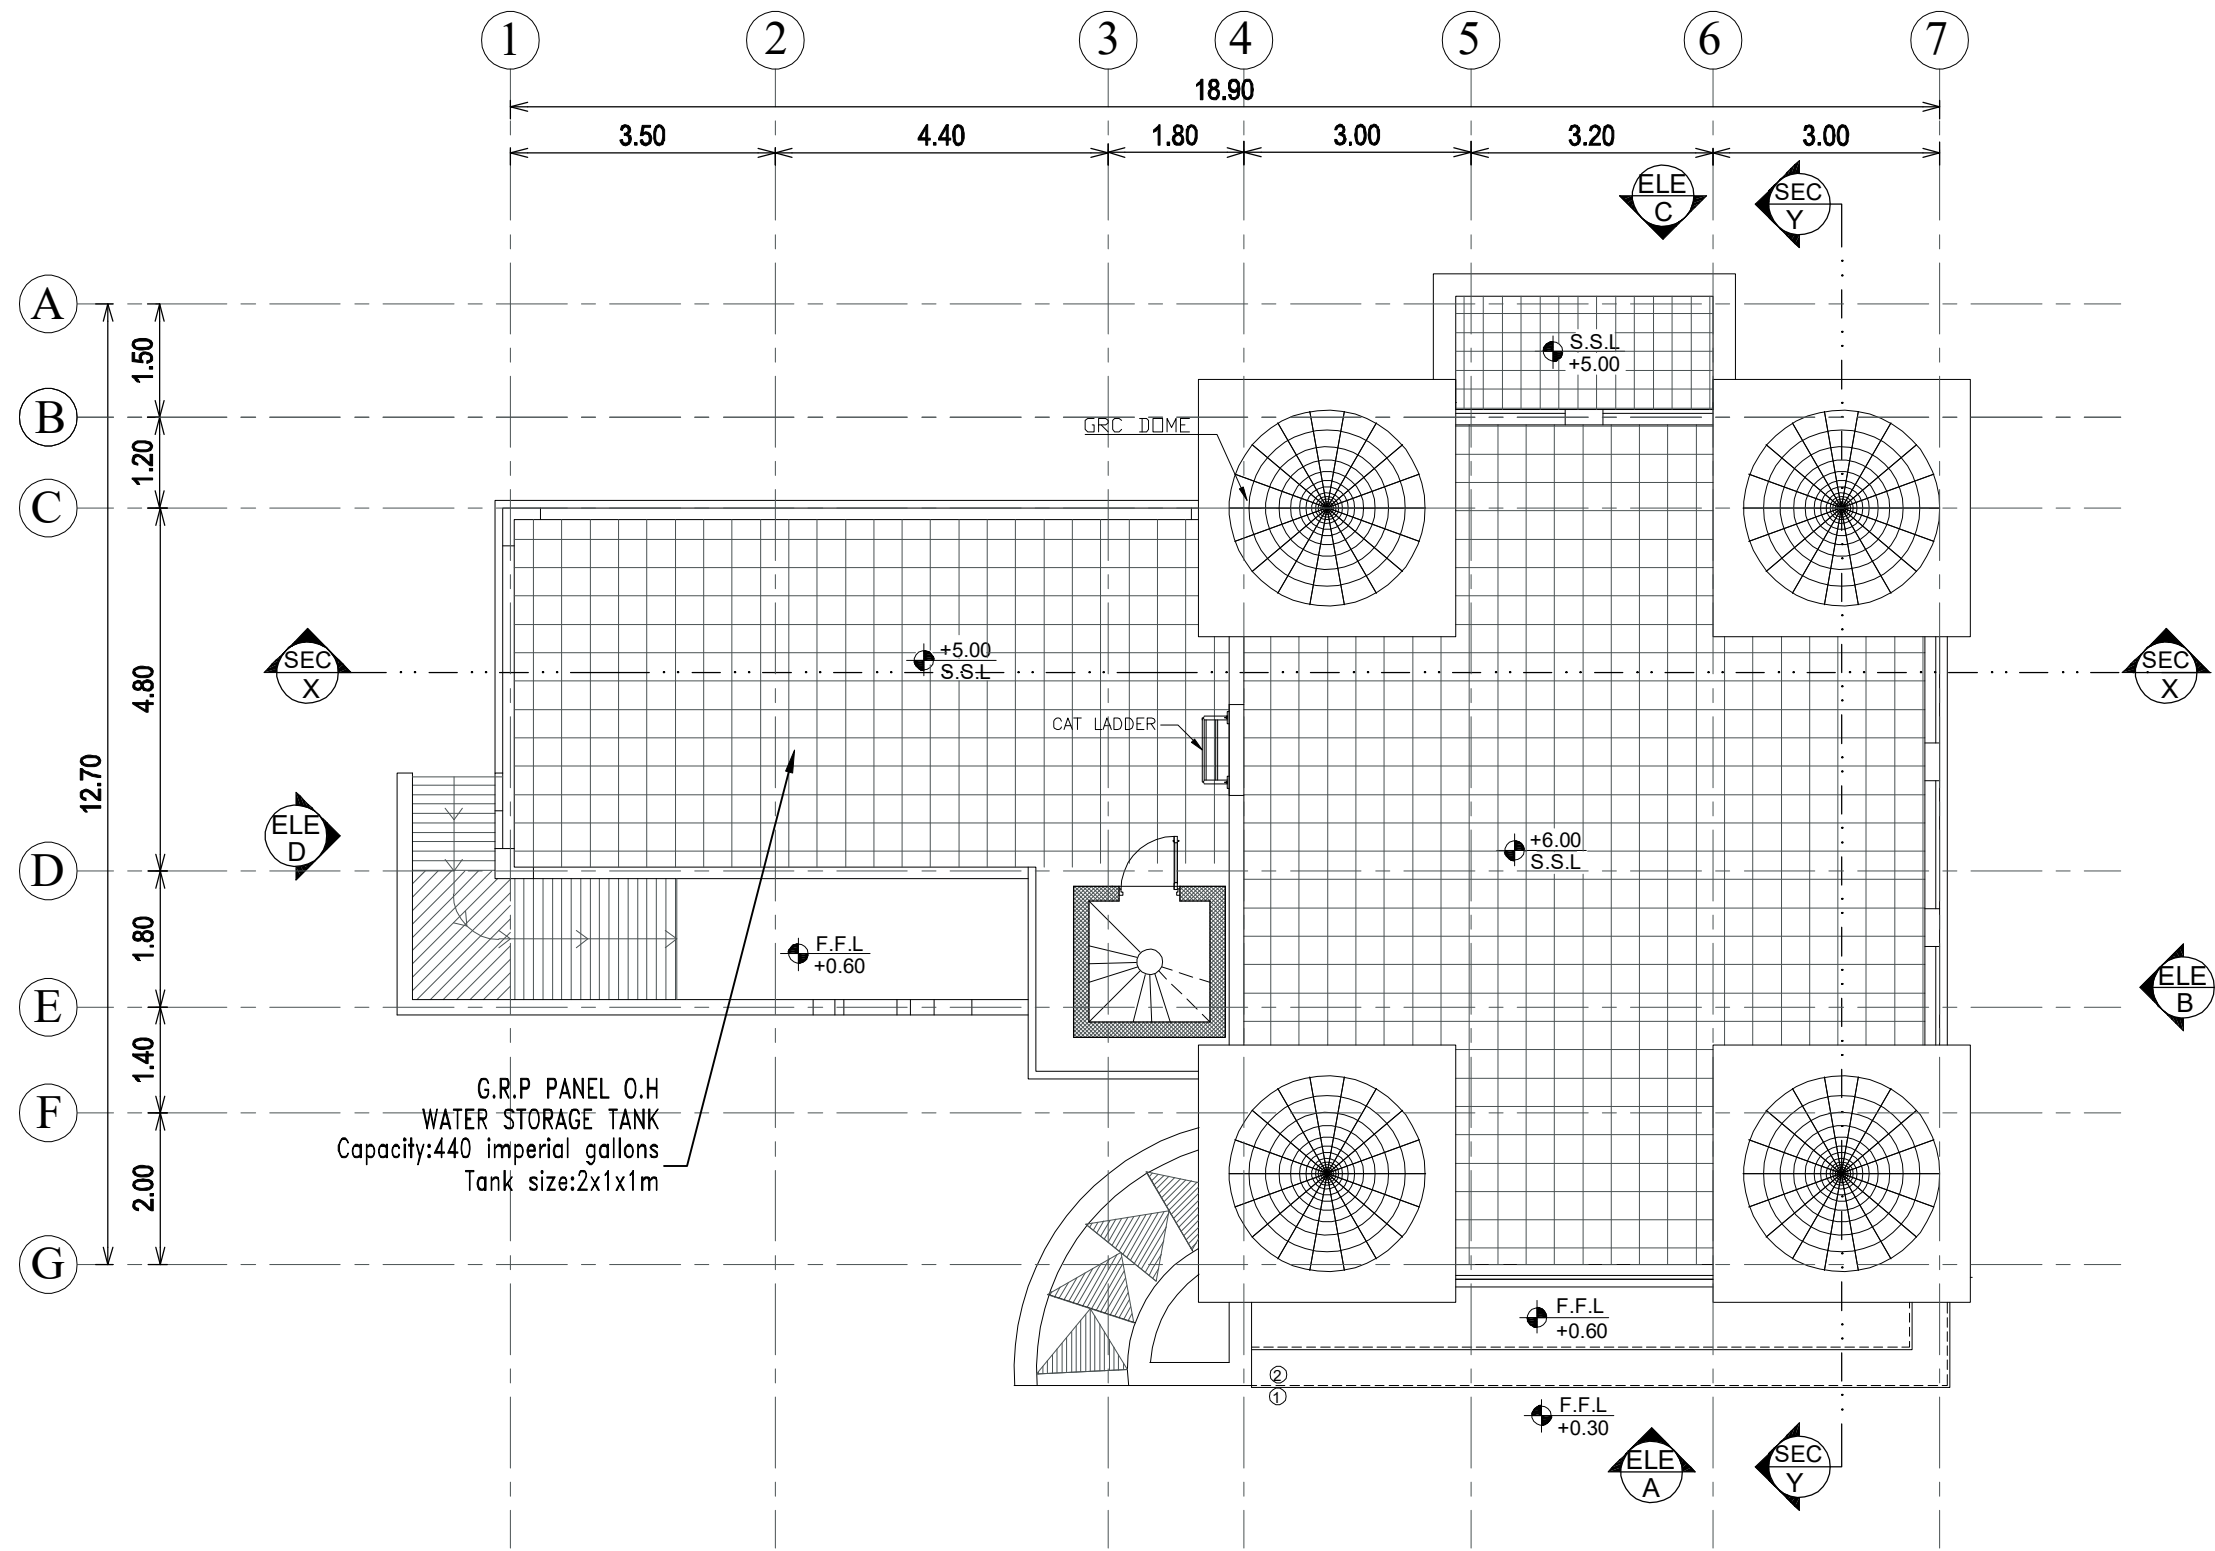

GENERAL NOTES:


- 1.IT IS NOT ALLOWED TO REPRODUCE THE SHEETS CONTENTS IN ANY FORM EXCEPT FOR THE PURPOSE FOR WHICH IT IS INTENDED.
2. THESE DRAWINGS ARE DIAGRAMMATIC AND SHALL NOT BE SCALED. ADDITIONAL DATA SHALL BE REQUESTED FROM THE CONSULTANCY THROUGH WRITTEN CLARIFICATION. VERIFY ALL EXISTING CONDITIONS AND DIMENSIONS BEFORE PROCEEDING WITH ANY PORTION OF ANY WORK.
3. NO CHANGES, MODIFICATIONS OR DEVIATIONS SHALL BE WRITTEN PERMISSION FROM **ALMASAH ENGINEERING CONSULTANTS**.
4. ALL WORK AS OUTLINED IN THESE DOCUMENTS, SHALL STRICTLY CONFORM TO ALL APPLICABLE CODES. IN THE EVENT OF A CONFLICT, THE MORE STRINGENT REQUIREMENT SHALL GOVERN AND BE MET.



SIA - SM-03



CONSULTANT STAMP

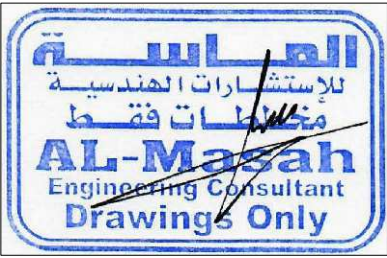

CLIENT: **GOVERNMENT OF SHARJAH - DEPARTMENT OF ISLAMIC AFFAIRS**


PROJECT: **(SIA - SM-03) PROPOSED MASJID + ABLUTION + IMAM HOUSE**

SHEET TITLE: **GROUND & ROOF FLOOR PLAN**

ARCHITECT Arch. Mostafa Ramadan	TYPE ARCHITECTURE
STRUCTURAL Eng : Mohamed Gomaa	SHEET No. A -03
CHECKED BY Eng : Mohamed Attia	Location : Plot No :
SCALE 1:100	DATE February - 2022
Project No.	SIA - SM-03

ELEVATIONS - A

SCALE 1:100

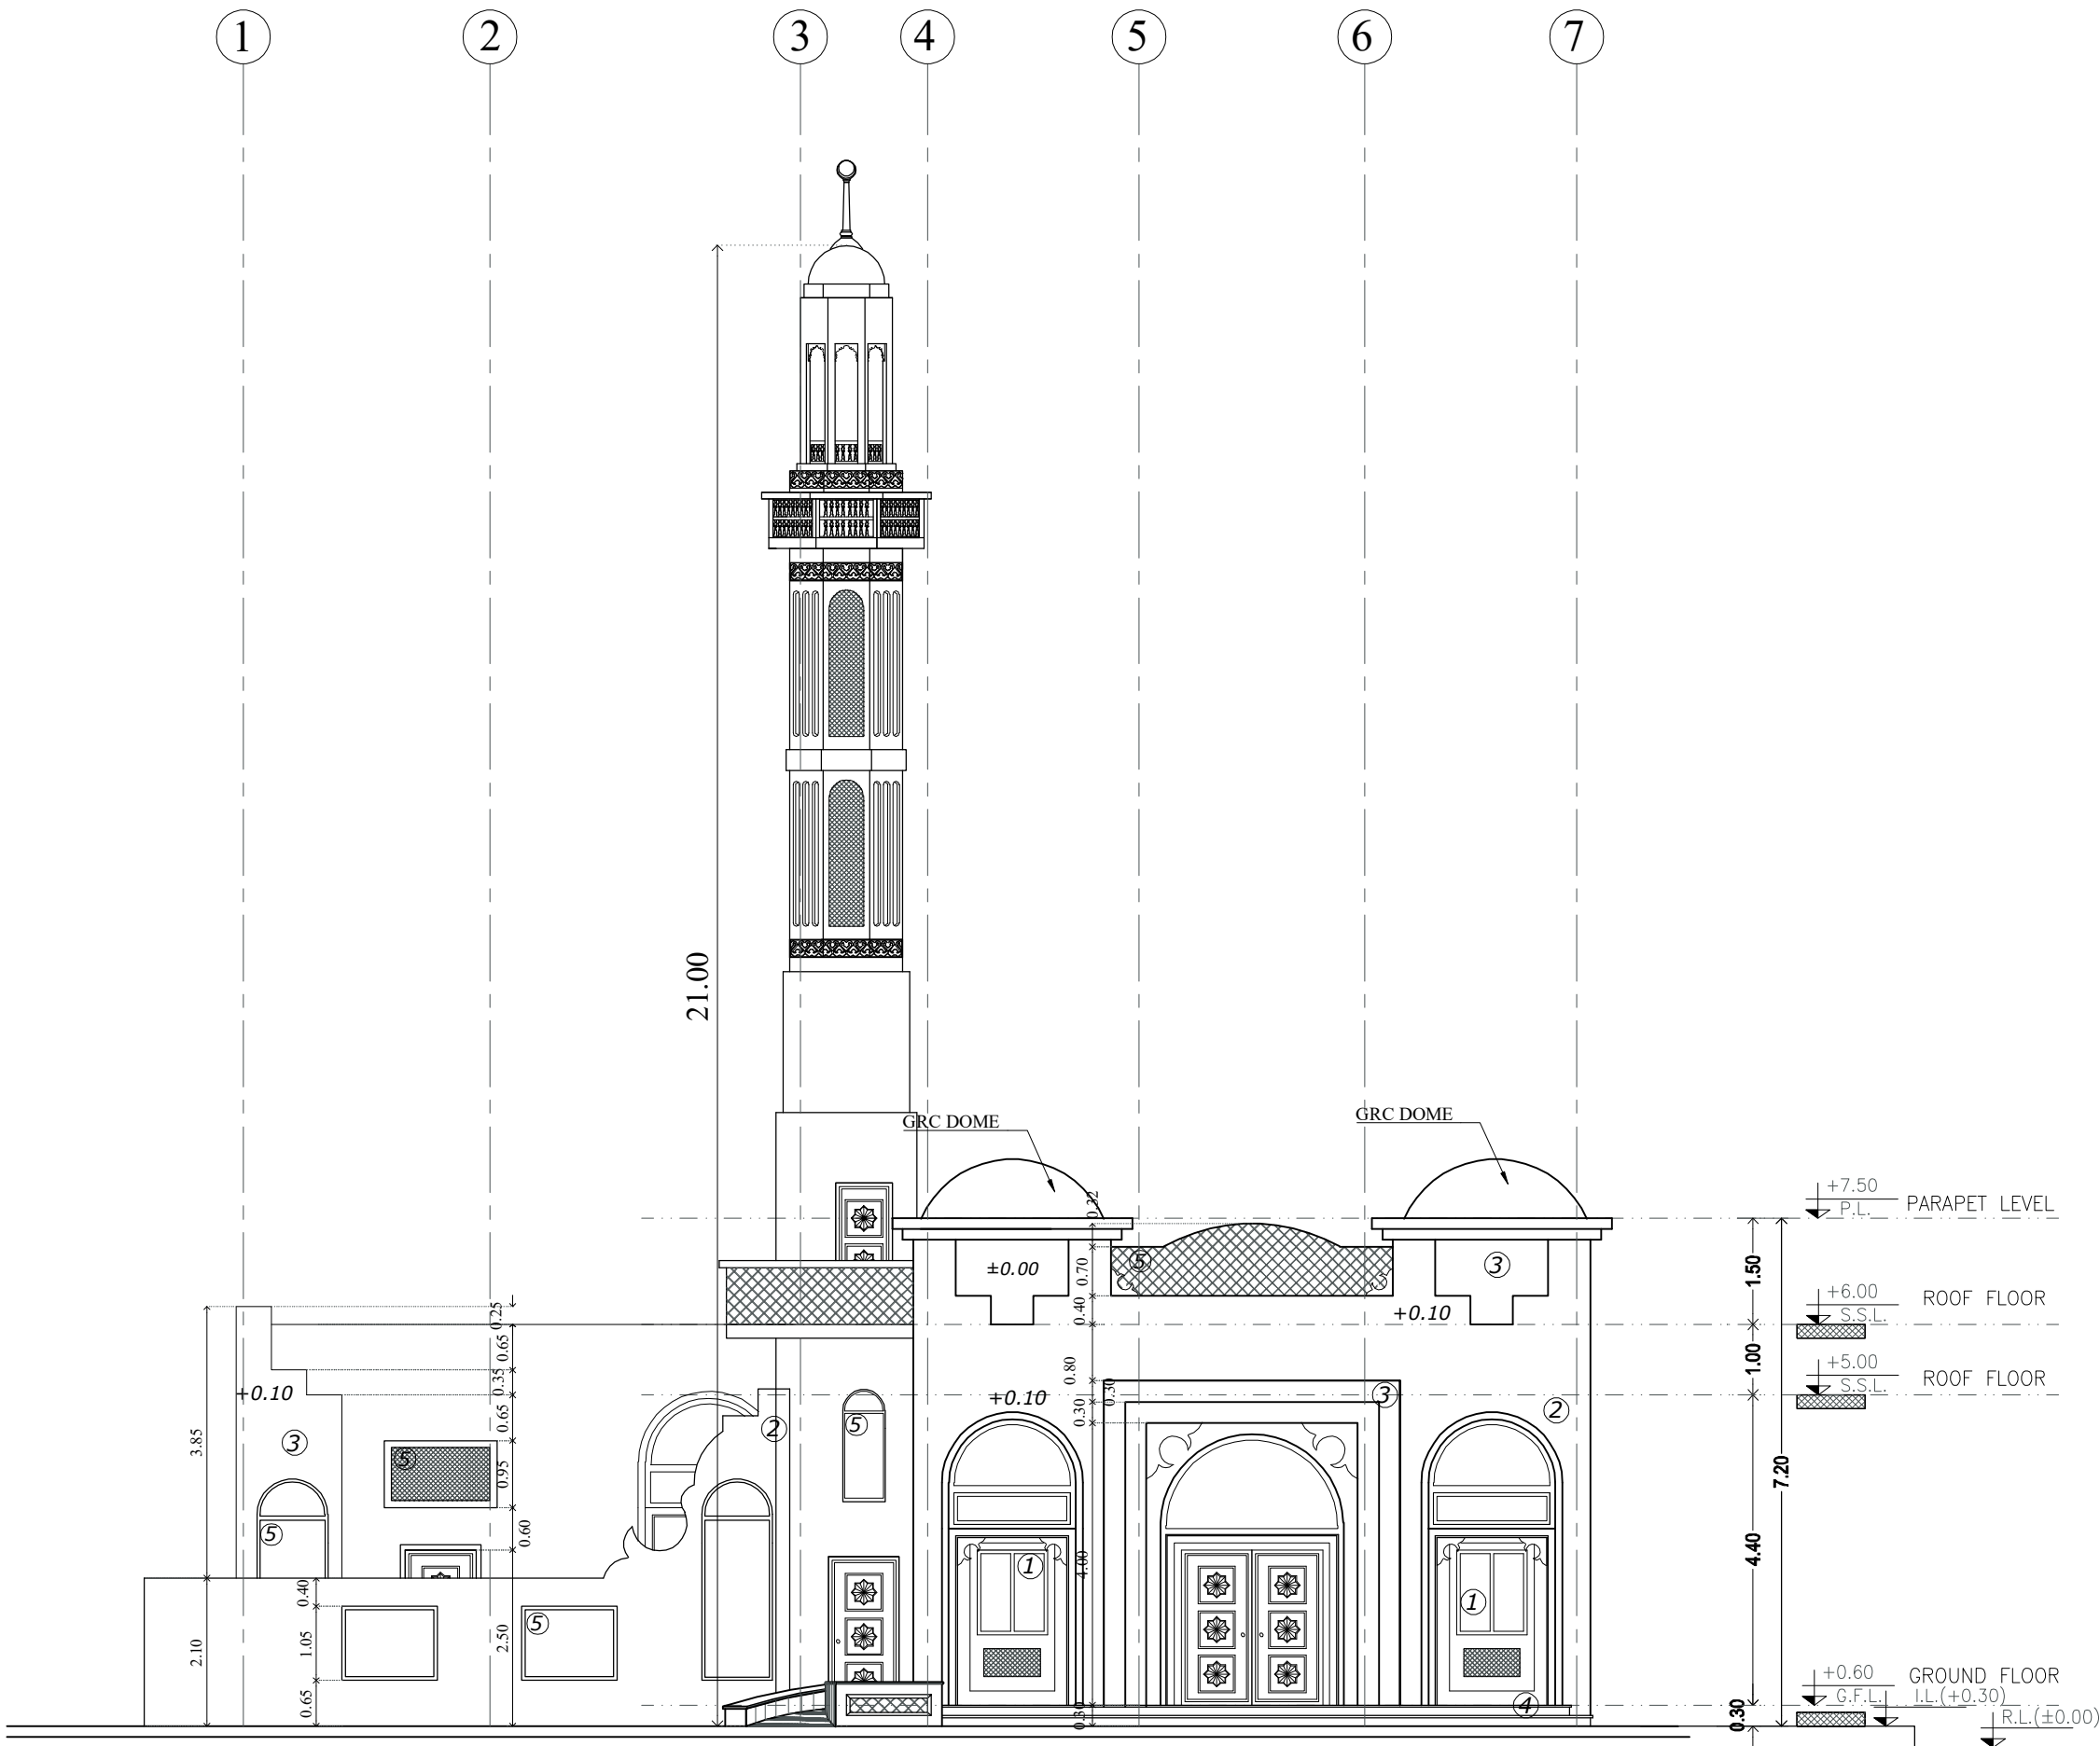

ELEVATION FINISHES

- 1- REFLECTIVE GLASS
- 2- GRAFFIO DECOR WHITE PAINT OR STONE CLADDING
- 3- GRAFFIO DECOR OFF WHITE PAINT OR STONE CLADDING
- 4- GRANITE FINISHING
- 5- G.R.C.

GENERAL NOTES:

1. IT IS NOT ALLOWED TO REPRODUCE THE SHEETS CONTENTS IN ANY FORM EXCEPT FOR THE PURPOSE FOR WHICH IT IS INTENDED.
2. THESE DRAWINGS ARE DIAGRAMMATIC AND SHALL NOT BE SCALED. ADDITIONAL DATA SHALL BE REQUESTED FROM THE CONSULTANCY THROUGH WRITTEN CLARIFICATION. VERIFY ALL EXISTING CONDITIONS AND DIMENSIONS BEFORE PROCEEDING WITH ANY PORTION OF ANY WORK.
3. NO CHANGES, MODIFICATIONS OR DEVIATIONS SHALL BE WRITTEN PERMISSION FROM **ALMASAH ENGINEERING CONSULTANTS**.
4. ALL WORK AS OUTLINED IN THESE DOCUMENTS, SHALL STRICTLY CONFORM TO ALL APPLICABLE CODES. IN THE EVENT OF A CONFLICT, THE MORE STRINGENT REQUIREMENT SHALL GOVERN AND BE MET.



SIA - SM-03



CONSULTANT STAMP



CLIENT: **GOVERNMENT OF SHARJAH - DEPARTMENT OF ISLAMIC AFFAIRS**


PROJECT: **(SIA - SM-03) PROPOSED MASJID + ABLUTION + IMAM HOUSE**

SHEET TITLE: **ELEVATION A & B**

ARCHITECT Arch. Mostafa Ramadan	TYPE ARCHITECTURE
STRUCTURAL Eng : Mohamed Gomaa	SHEET No. A -04
CHECKED BY Eng : Mohamed Attia	Location : Plot No :
SCALE 1:100	DATE February - 2022
Project No.	SIA - SM-03

ELEVATIONS - B

SCALE 1:100

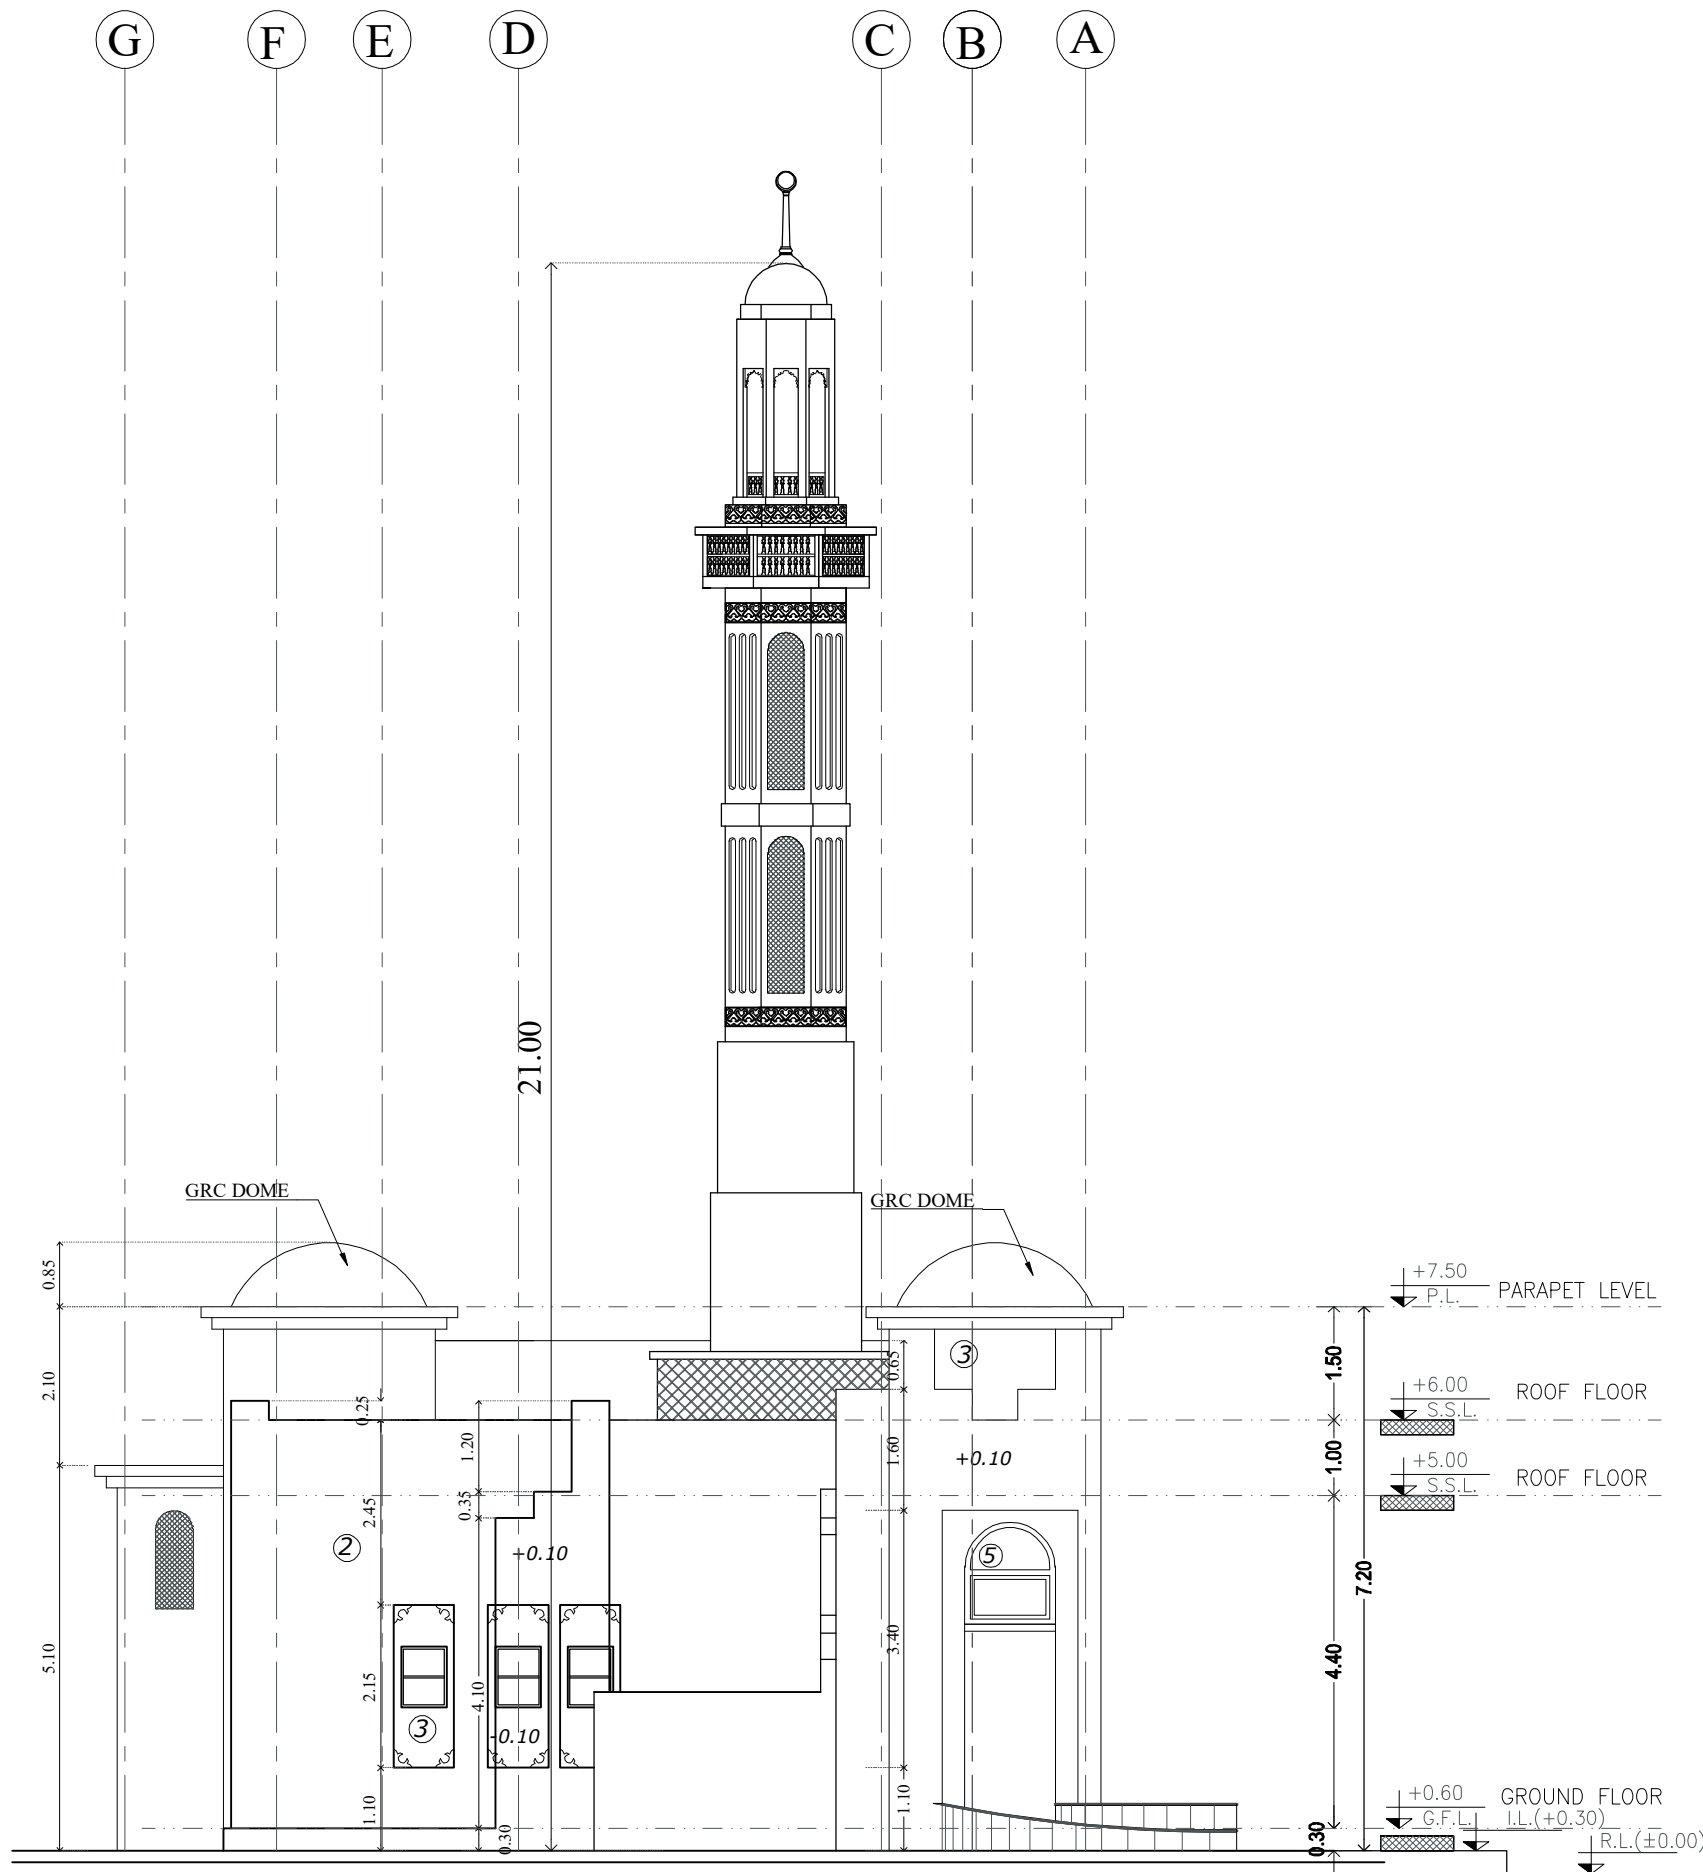

ELEVATION FINISHES

- 1- REFLECTIVE GLASS
- 2- GRAFFIO DECOR WHITE PAINT OR STONE CLADDING
- 3- GRAFFIO DECOR OFF WHITE PAINT OR STONE CLADDING WHITE PAINT OR STONE CLADDING
- 4- GRANITE FINISHING
- 5- G.R.C.

GENERAL NOTES:

1. IT IS NOT ALLOWED TO REPRODUCE THE SHEETS CONTENTS IN ANY FORM EXCEPT FOR THE PURPOSE FOR WHICH IT IS INTENDED.
2. THESE DRAWINGS ARE DIAGRAMMATIC AND SHALL NOT BE SCALED. ADDITIONAL DATA SHALL BE REQUESTED FROM THE CONSULTANCY THROUGH WRITTEN CLARIFICATION. VERIFY ALL EXISTING CONDITIONS AND DIMENSIONS BEFORE PROCEEDING WITH ANY PORTION OF ANY WORK.
3. NO CHANGES, MODIFICATIONS OR DEVIATIONS SHALL BE WRITTEN PERMISSION FROM **ALMASAH ENGINEERING CONSULTANTS**.
4. ALL WORK AS OUTLINED IN THESE DOCUMENTS, SHALL STRICTLY CONFORM TO ALL APPLICABLE CODES. IN THE EVENT OF A CONFLICT, THE MORE STRINGENT REQUIREMENT SHALL GOVERN AND BE MET.



SIA - SM-03



CONSULTANT STAMP



Sharjah ☎ 06 5 444 521 ☎ 06 5 444 523 📍 Office: 306, Al Fisal 2 Bldg., King Faisal St.


CLIENT: **GOVERNMENT OF SHARJAH -
DEPARTMENT OF ISLAMIC AFFAIRS**

PROJECT: **(SIA - SM-03)
PROPOSED MASJID + ABLUTION +
IMAM HOUSE**


SHEET TITLE: **ELEVATION A & B**

ARCHITECT Arch. Mostafa Ramadan	TYPE	ARCHITECTURE
STRUCTURAL Eng : Mohamed Gomaa	SHEET No.	A -05
CHECKED BY Eng : Mohamed Attia	Location :	
	Plot No :	
SCALE 1:100	DATE February - 2022	Project No.
		SIA - SM-03

SCALE 1:100

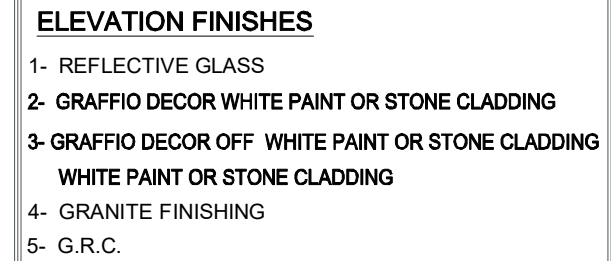

1. IT IS NOT ALLOWED TO REPRODUCE THE SHEETS CONTENTS IN ANY FORM EXCEPT FOR THE PURPOSE FOR WHICH IT IS INTENDED.
2. THESE DRAWINGS ARE DIAGRAMMATIC AND SHALL NOT BE SCALED. ADDITIONAL DATA SHALL BE REQUESTED FROM THE CONSULTANCY THROUGH WRITTEN CLARIFICATION. VERIFY ALL EXISTING CONDITIONS AND DIMENSIONS BEFORE PROCEEDING WITH ANY PORTION OF ANY WORK.
3. NO CHANGES, MODIFICATIONS OR DEVIATIONS SHALL BE WRITTEN PERMISSION FROM **ALMASAH ENGINEERING CONSULTANTS.**
4. ALL WORK AS OUTLINED IN THESE DOCUMENTS, SHALL STRICTLY CONFORM TO ALL APPLICABLE CODES. IN THE EVENT OF A CONFLICT, THE MORE STRINGENT REQUIREMENT SHALL GOVERN AND BE MET.

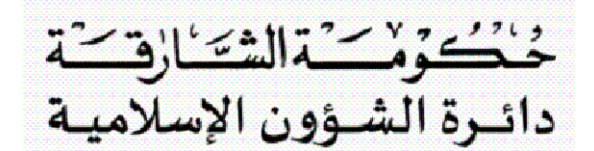

المحاسبة
للاستشارات الهندسية
AL-Masah
Engineering Consultant
Drawings Only




SHEET TITLE:

ELEVATION C & D

ARCHITECT Arch. Mostafa Ramadan		TYPE	ARCHITECTURE
STRUCTURAL Eng : Mohamed Gomaa		SHEET No.	A -06
CHECKED BY Eng : Mohamed Attia		Location :	
		Plot No :	
SCALE 1:100	DATE February - 2022	Project No.	SIA - SM-03

ELEVATIONS - D

SCALE 1:100

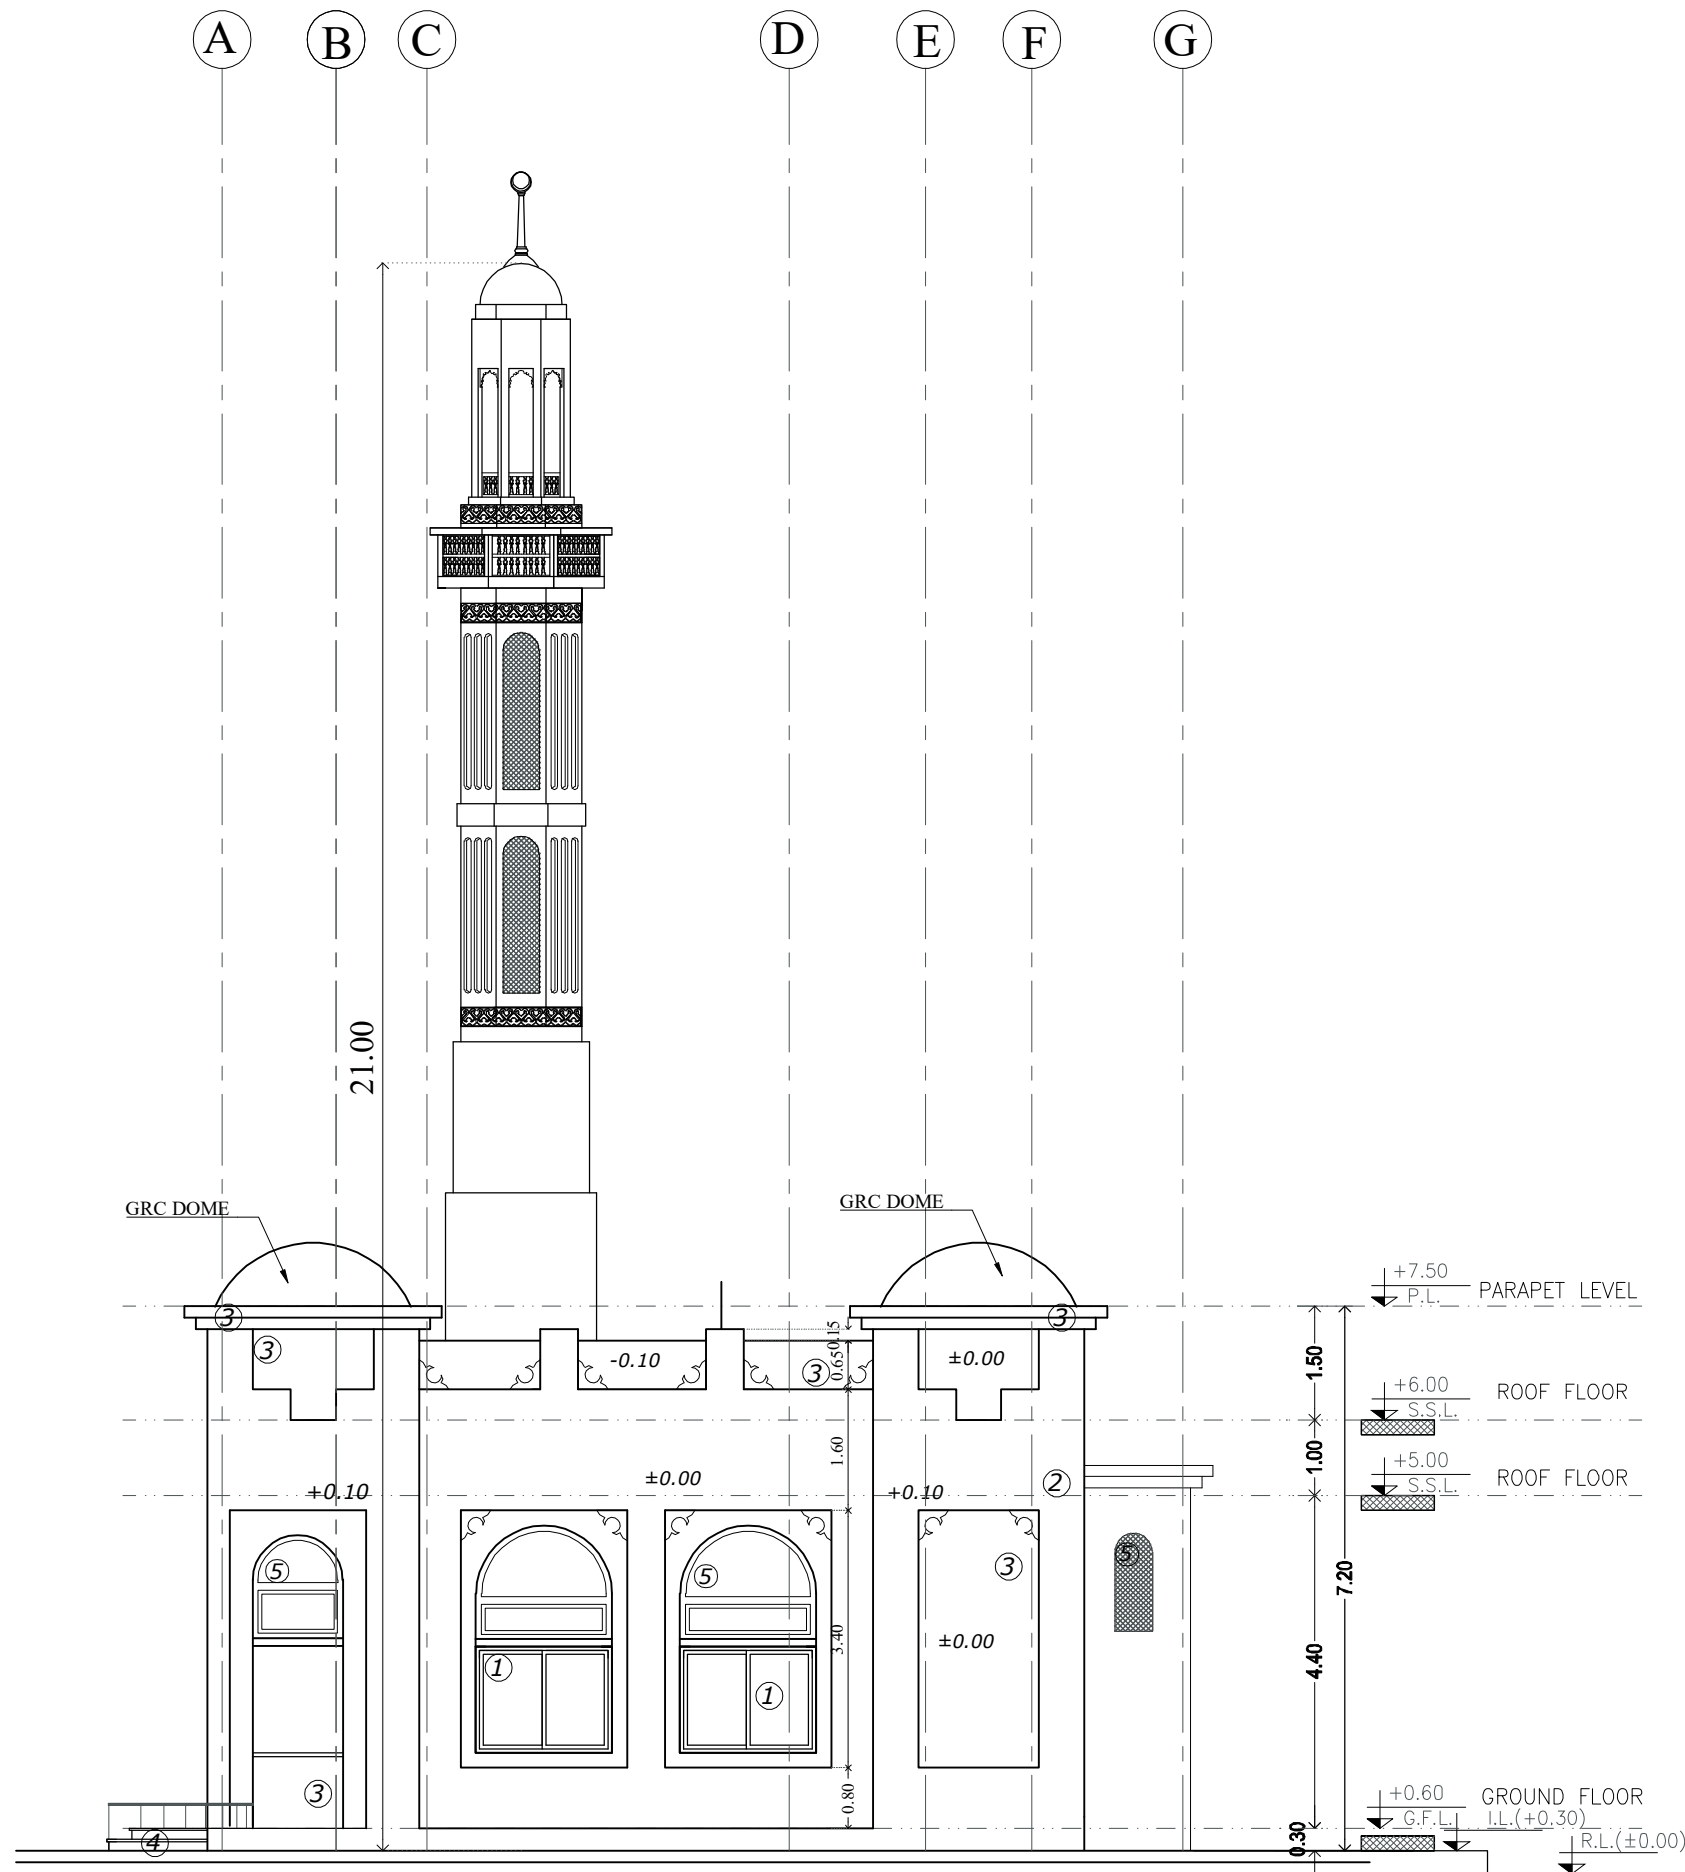

ELEVATION FINISHES

- 1- REFLECTIVE GLASS
- 2- GRAFFIO DECOR WHITE PAINT OR STONE CLADDING
- 3- GRAFFIO DECOR OFF WHITE PAINT OR STONE CLADDING WHITE PAINT OR STONE CLADDING
- 4- GRANITE FINISHING
- 5- G.R.C.

GENERAL NOTES:

1. IT IS NOT ALLOWED TO REPRODUCE THE SHEETS CONTENTS IN ANY FORM EXCEPT FOR THE PURPOSE FOR WHICH IT IS INTENDED.
2. THESE DRAWINGS ARE DIAGRAMMATIC AND SHALL NOT BE SCALED. ADDITIONAL DATA SHALL BE REQUESTED FROM THE CONSULTANCY THROUGH WRITTEN CLARIFICATION. VERIFY ALL EXISTING CONDITIONS AND DIMENSIONS BEFORE PROCEEDING WITH ANY PORTION OF ANY WORK.
3. NO CHANGES, MODIFICATIONS OR DEVIATIONS SHALL BE WRITTEN PERMISSION FROM **ALMASAH ENGINEERING CONSULTANTS**.
4. ALL WORK AS OUTLINED IN THESE DOCUMENTS, SHALL STRICTLY CONFORM TO ALL APPLICABLE CODES. IN THE EVENT OF A CONFLICT, THE MORE STRINGENT REQUIREMENT SHALL GOVERN AND BE MET.



SIA - SM-03



CONSULTANT STAMP




Sharjah ☎ 06 5 444 521 ☎ 06 5 444 523 ☎ Office: 306, Al Fisal 2 Bldg., King Faisal St.

CLIENT: **GOVERNMENT OF SHARJAH - DEPARTMENT OF ISLAMIC AFFAIRS**


PROJECT: **(SIA - SM-03) PROPOSED MASJID + ABLUTION + IMAM HOUSE**

SHEET TITLE: **ELEVATION C & D**

ARCHITECT Arch. Mostafa Ramadan	TYPE	ARCHITECTURE
STRUCTURAL Eng : Mohamed Gomaa	SHEET No.	A-07
CHECKED BY Eng : Mohamed Attia	Location :	
	Plot No :	
SCALE 1:100	DATE February - 2022	Project No.
		SIA - SM-03

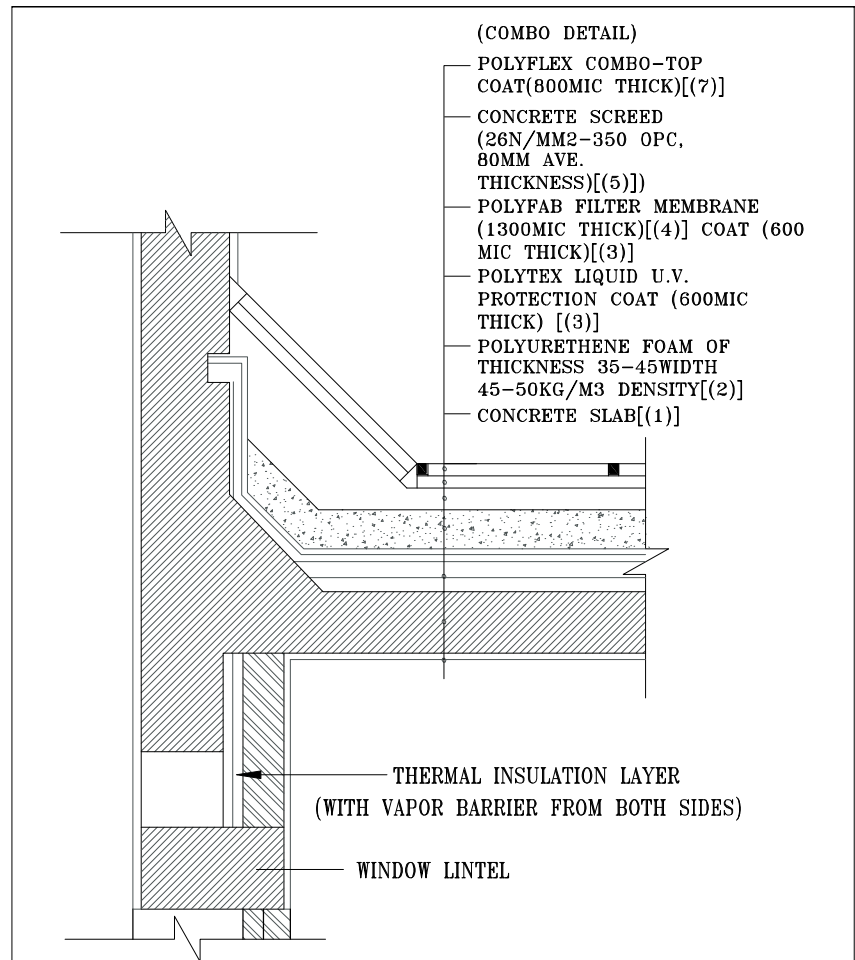


PARAPET & ROOF FINISHING DETAILS

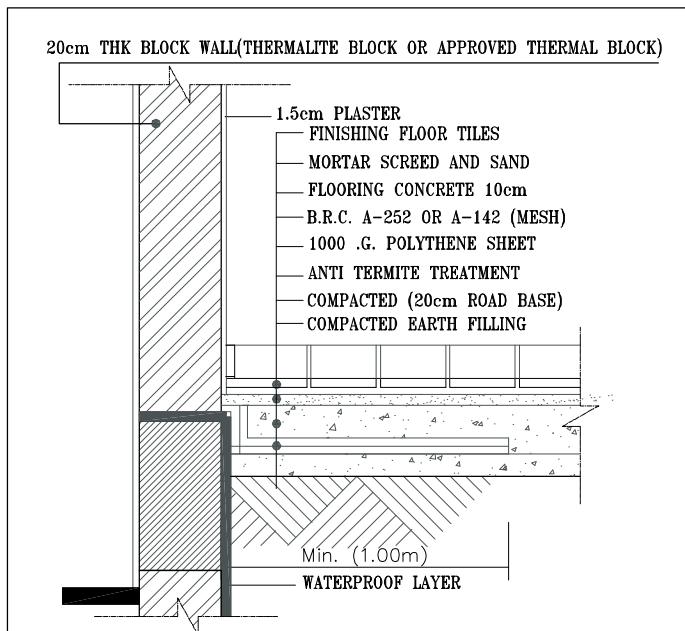

GROUND FLOOR DETAILS


* NOTES ::

- ALL EXTERNAL WALLS TO BE 20.cm THERMAL BLOCK.
- WINDOWS TO BE DOUBLE REFLECTIVE GLASS

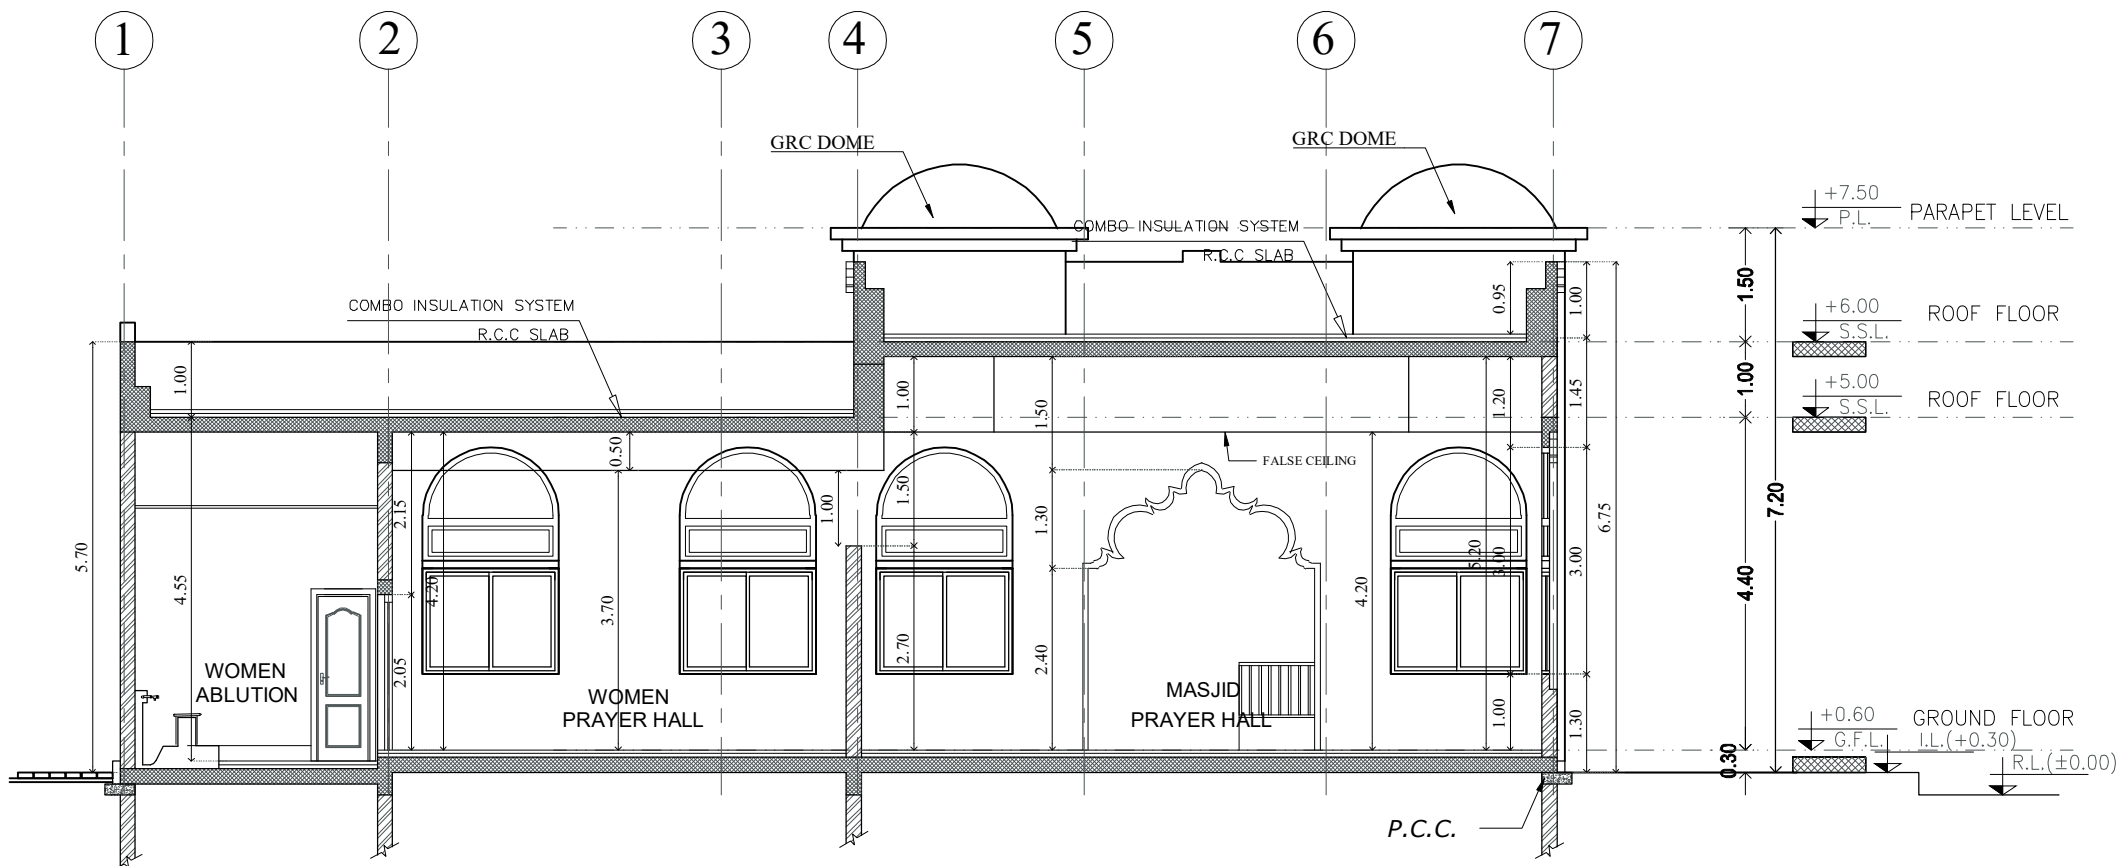

SECTION X - X

SCALE 1:100

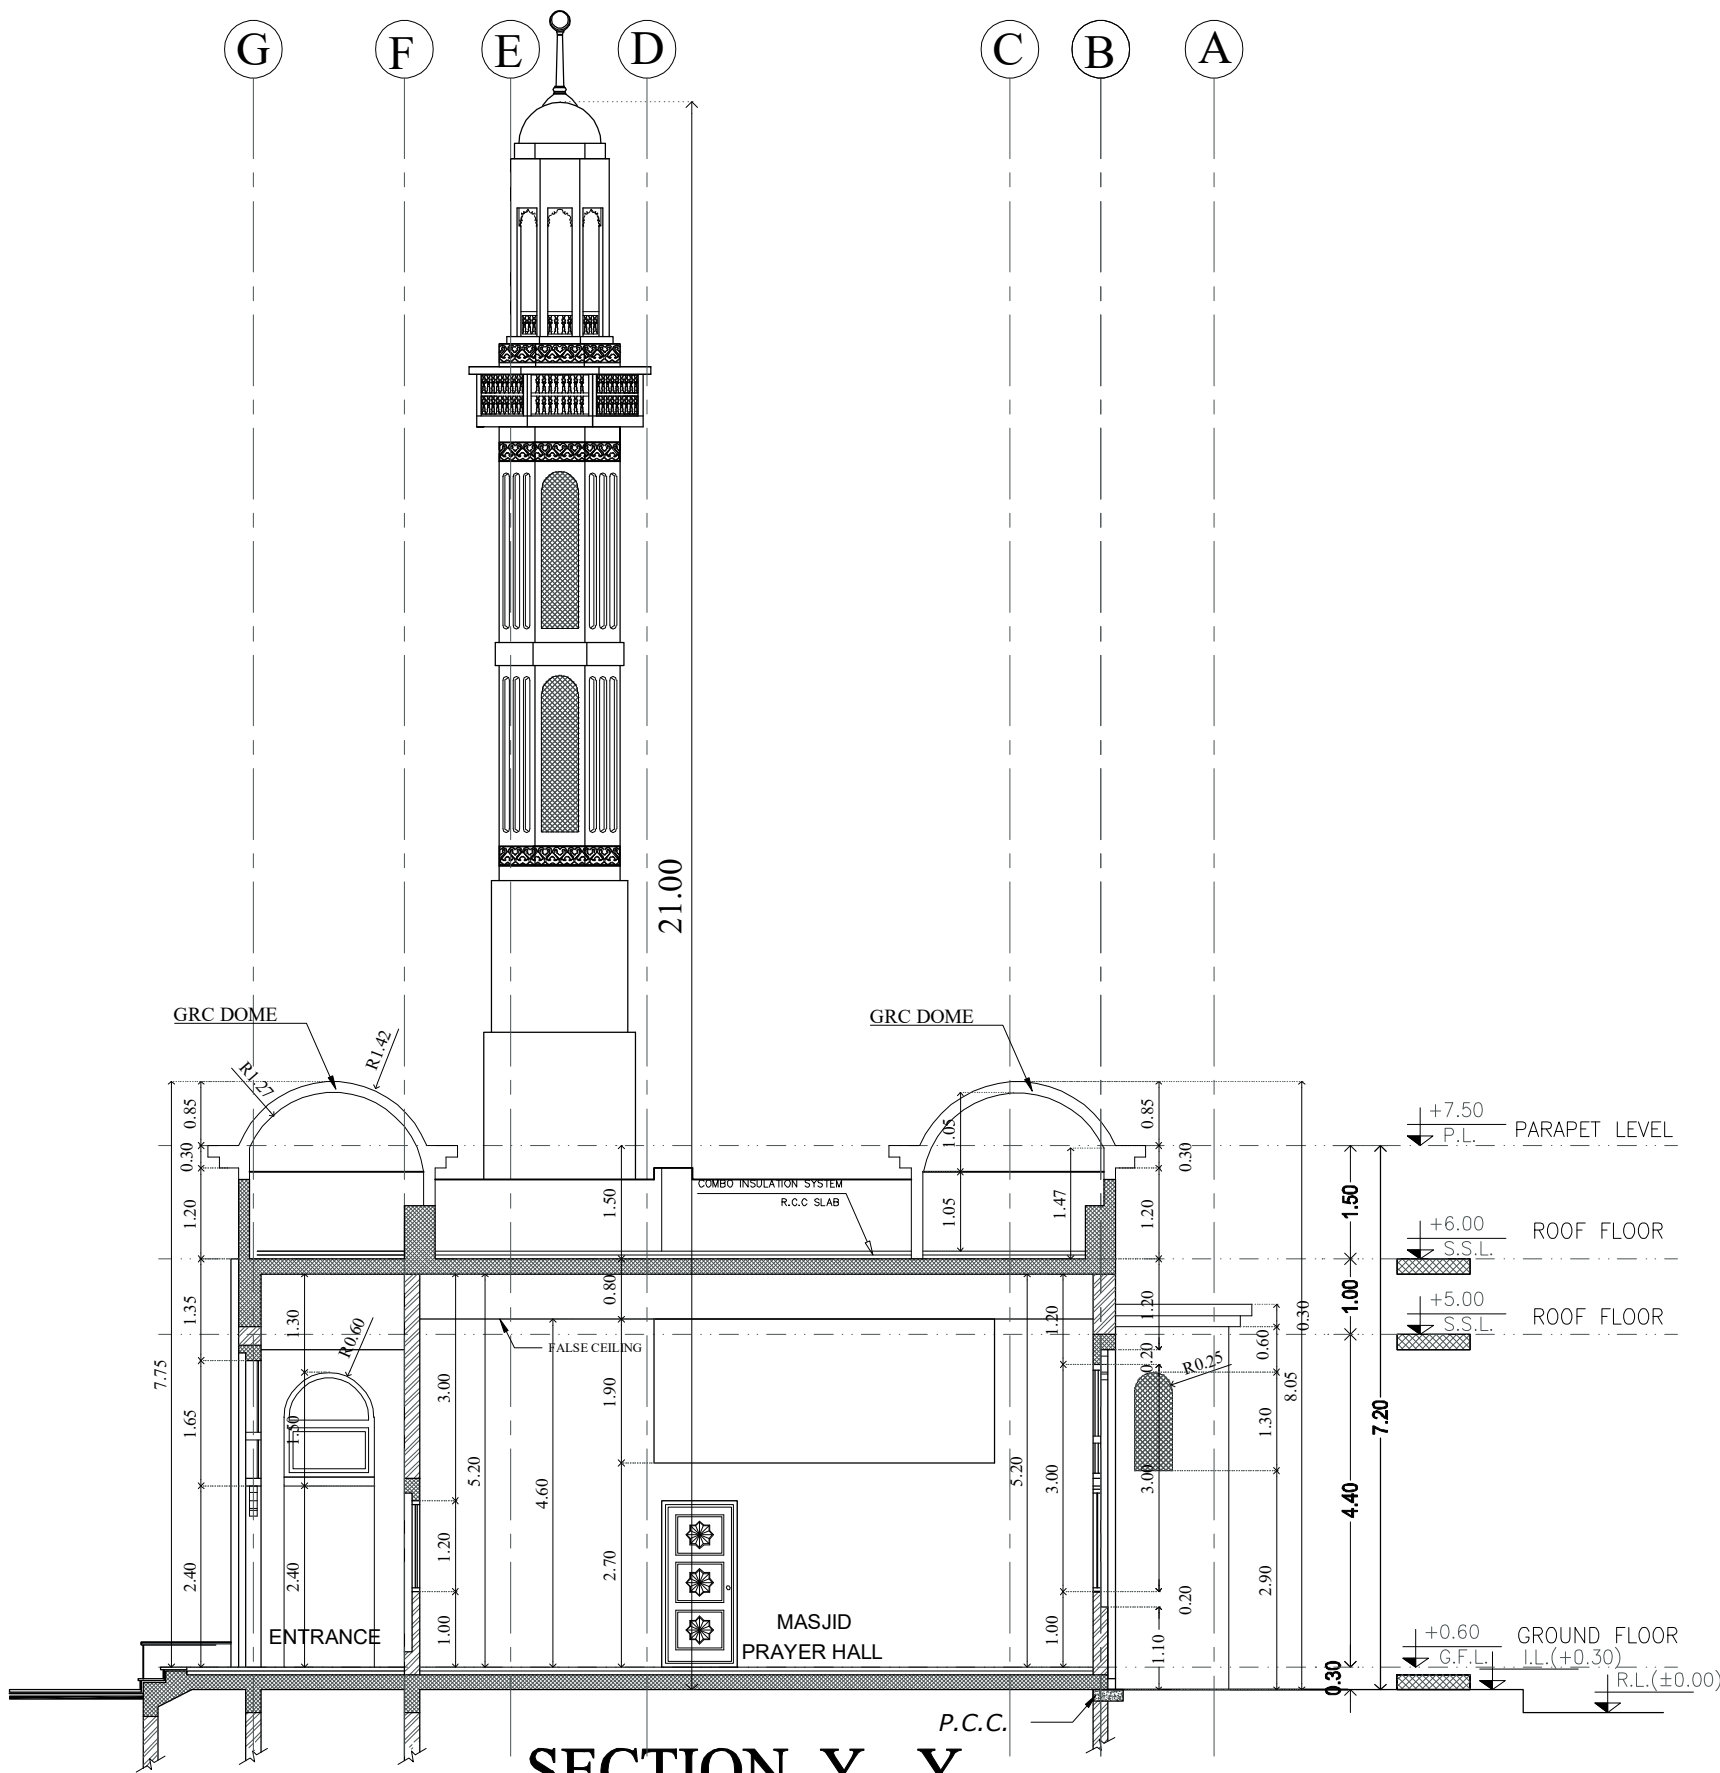

SECTION Y - Y

SCALE 1:100

GENERAL NOTES:

- IT IS NOT ALLOWED TO REPRODUCE THE SHEETS CONTENTS IN ANY FORM EXCEPT FOR THE PURPOSE FOR WHICH IT IS INTENDED.
- THESE DRAWINGS ARE DIAGRAMMATIC AND SHALL NOT BE SCALED. ADDITIONAL DATA SHALL BE REQUESTED FROM THE CONSULTANCY THROUGH WRITTEN CLARIFICATION. VERIFY ALL EXISTING CONDITIONS AND DIMENSIONS BEFORE PROCEEDING WITH ANY PORTION OF ANY WORK.
- NO CHANGES, MODIFICATIONS OR DEVIATIONS SHALL BE WRITTEN PERMISSION FROM **ALMASAH ENGINEERING CONSULTANTS**.
- ALL WORK AS OUTLINED IN THESE DOCUMENTS, SHALL STRICTLY CONFORM TO ALL APPLICABLE CODES. IN THE EVENT OF A CONFLICT, THE MORE STRINGENT REQUIREMENT SHALL GOVERN AND BE MET.



SIA - SM-03



حكومة الشارقة
دائرة الشؤون الإسلامية

CONSULTANT STAMP



CLIENT:

GOVERNMENT OF SHARJAH -
DEPARTMENT OF ISLAMIC AFFAIRS

PROJECT:

(SIA - SM-03)
PROPOSED MASJID + ABLUTION +
IMAM HOUSE

SHEET TITLE:

SECTION X-X & Y-Y

ARCHITECT

Arch. Mostafa Ramadan

TYPE

ARCHITECTURE

STRUCTURAL

Eng : Mohamed Gomaa

SHEET

No.

A-08

CHECKED BY

Eng : Mohamed Attia

Location :

Plot No :

SCALE

1:100


DATE

February - 2022


Project

No.

SIA - SM-03

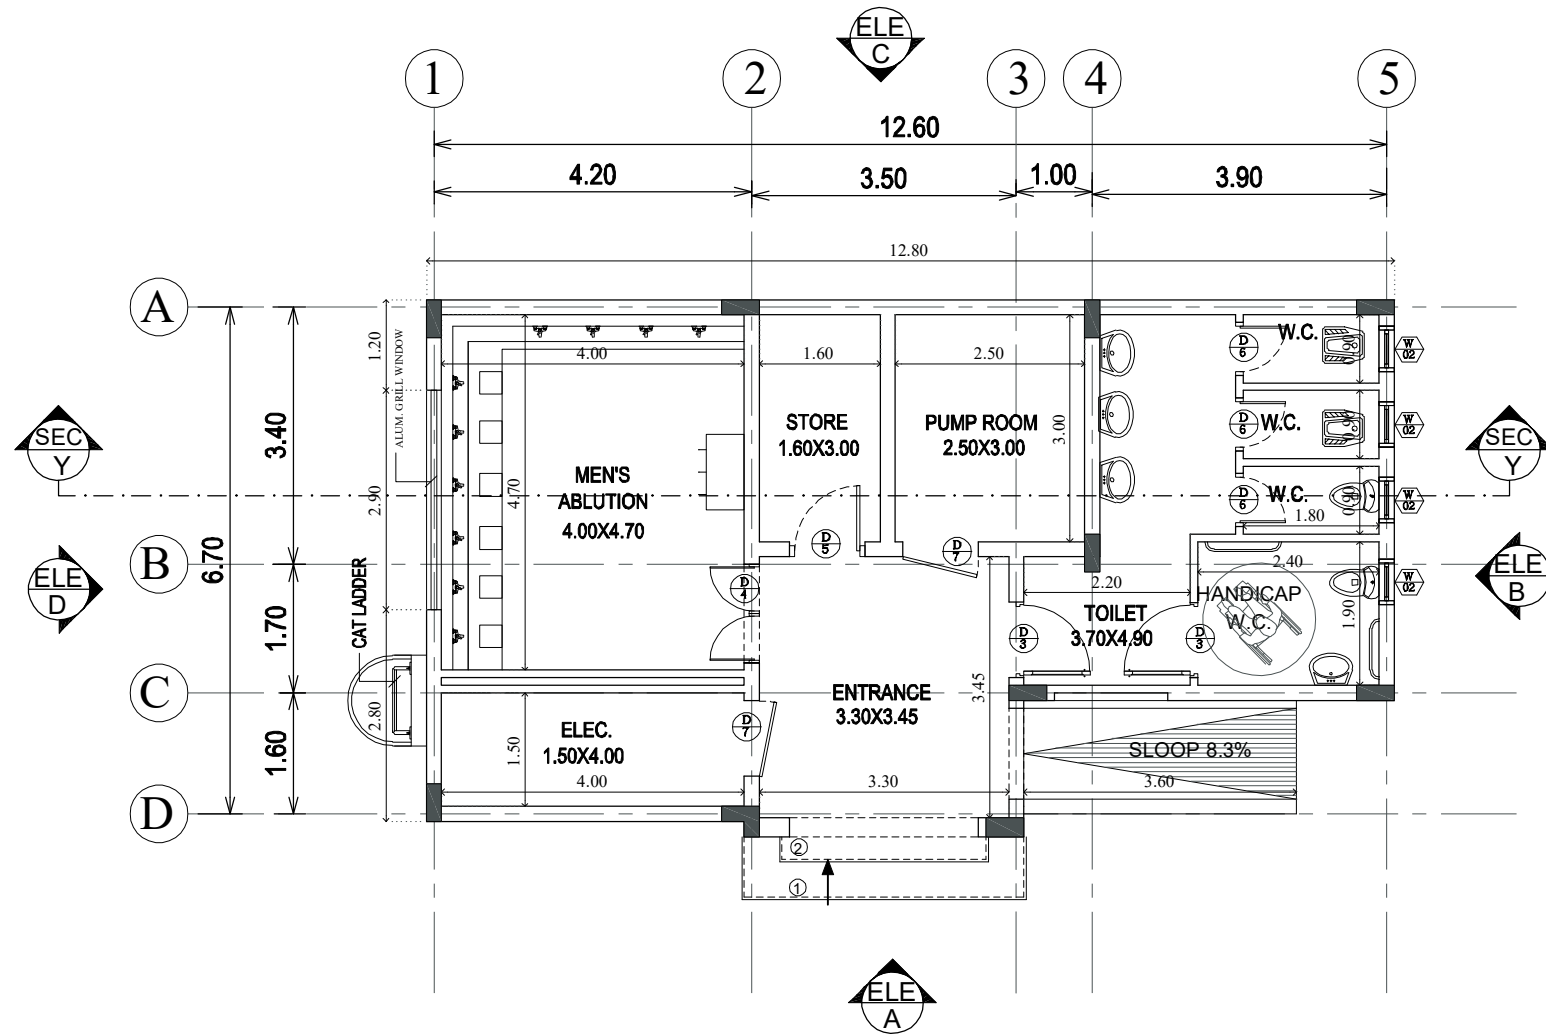

GROUND FLOOR PLAN
SCALE 1:100

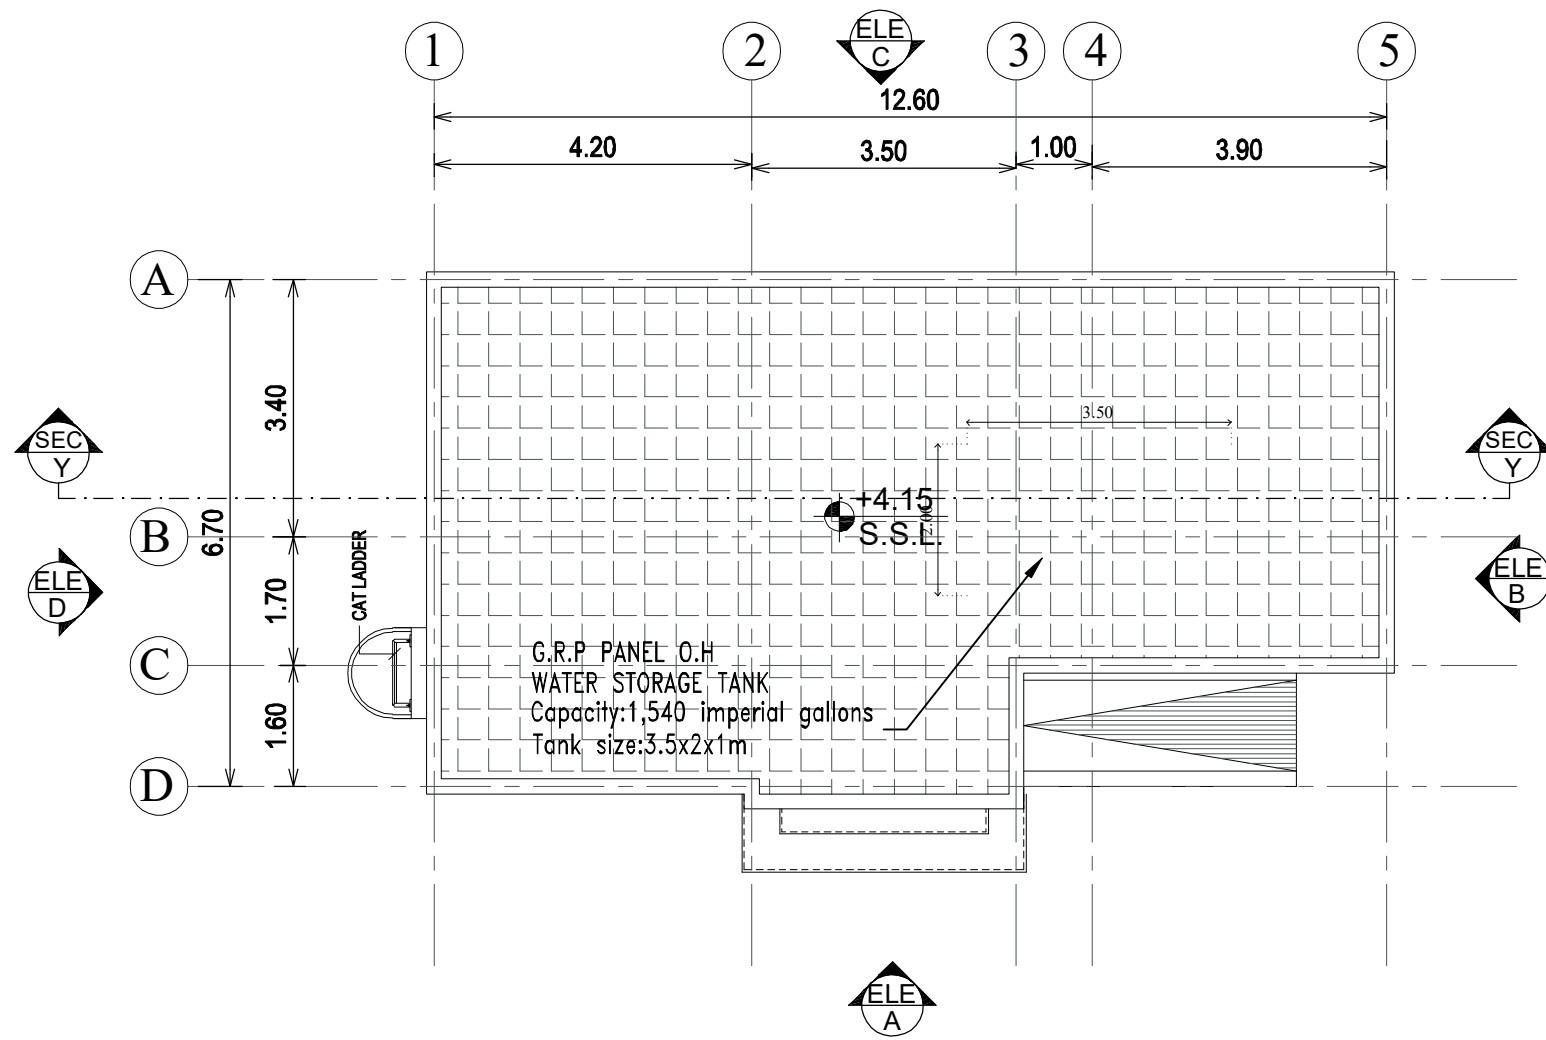

ROOF FLOOR PLAN
SCALE 1:100

GENERAL NOTES:


1. IT IS NOT ALLOWED TO REPRODUCE THE SHEETS CONTENTS IN ANY FORM EXCEPT FOR THE PURPOSE FOR WHICH IT IS INTENDED.
2. THESE DRAWINGS ARE DIAGRAMMATIC AND SHALL NOT BE SCALED. ADDITIONAL DATA SHALL BE REQUESTED FROM THE CONSULTANCY THROUGH WRITTEN CLARIFICATION. VERIFY ALL EXISTING CONDITIONS AND DIMENSIONS BEFORE PROCEEDING WITH ANY PORTION OF ANY WORK.
3. NO CHANGES, MODIFICATIONS OR DEVIATIONS SHALL BE WRITTEN PERMISSION FROM **ALMASAH ENGINEERING CONSULTANTS**.
4. ALL WORK AS OUTLINED IN THESE DOCUMENTS, SHALL STRICTLY CONFORM TO ALL APPLICABLE CODES. IN THE EVENT OF A CONFLICT, THE MORE STRINGENT REQUIREMENT SHALL GOVERN AND BE MET.




SIA - SM-03



حكومة الشارقة
دائرة الشؤون الإسلامية

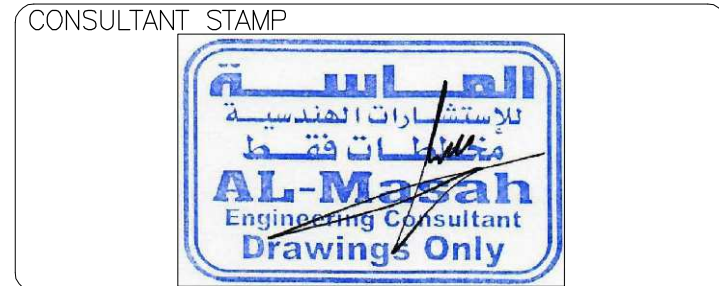


CLIENT: GOVERNMENT OF SHARJAH - DEPARTMENT OF ISLAMIC AFFAIRS			
PROJECT: (SIA - SM-03) PROPOSED MASJID + ABLUTION + IMAM HOUSE			
SHEET TITLE: ABLUTION GROUND & ROOF FLOOR PLANS			
ARCHITECT Arch. Mostafa Ramadan	TYPE	ARCHITECTURE	
STRUCTURAL Eng : Mohamed Gomaa	SHEET No.	A -09	
CHECKED BY Eng : Mohamed Attia	Location :		
	Plot No :		
SCALE 1:100	DATE February - 2022	Project No.	SIA - SM-03

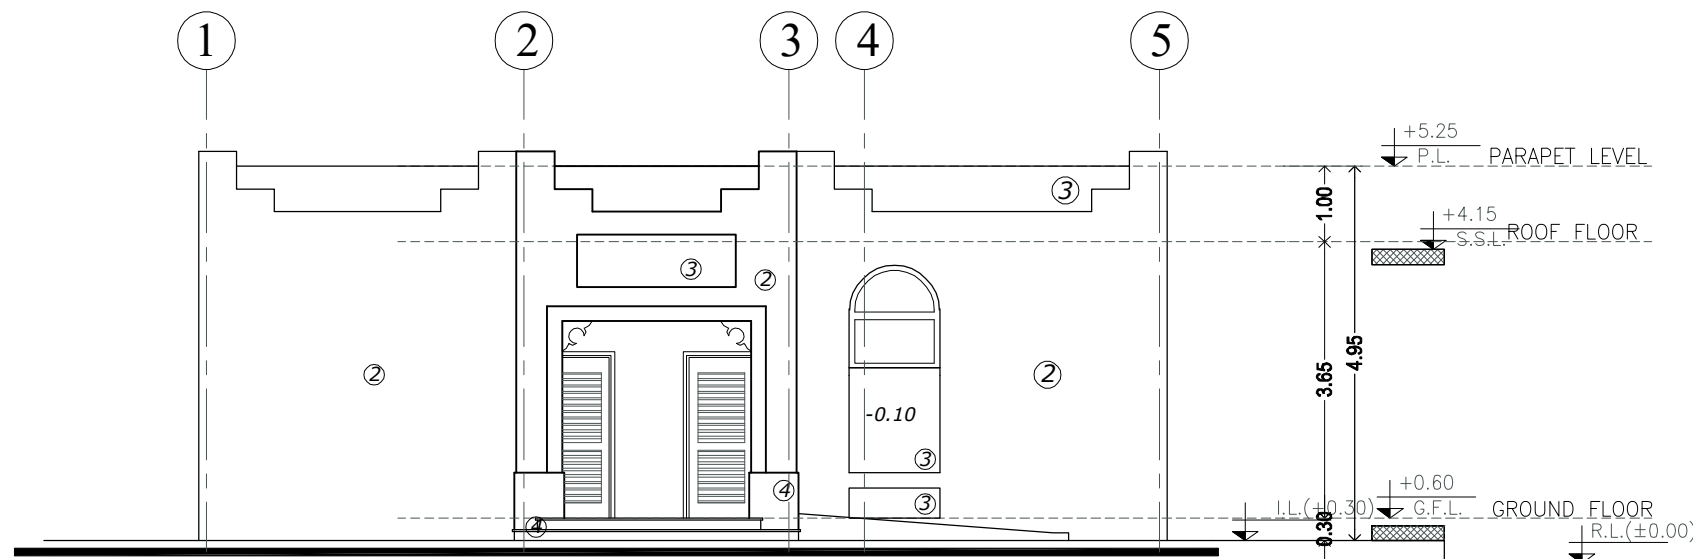


ELEVATION - A

SCALE 1:100

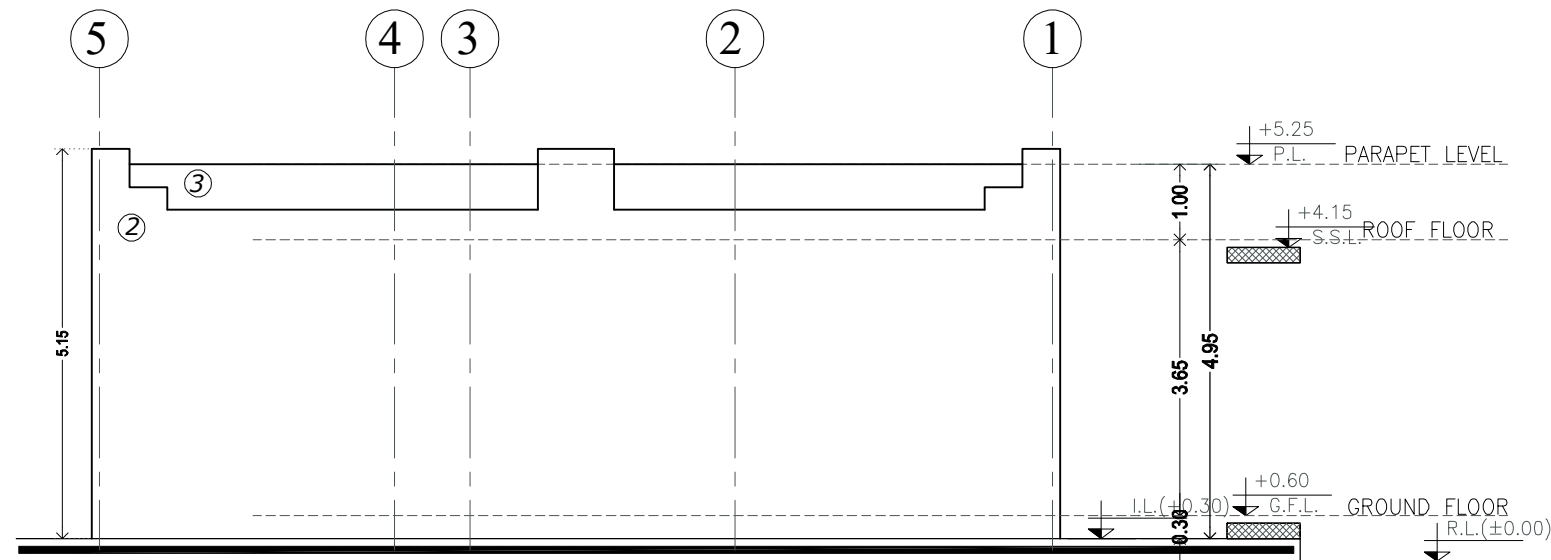


ELEVATION - C

SCALE 1:100

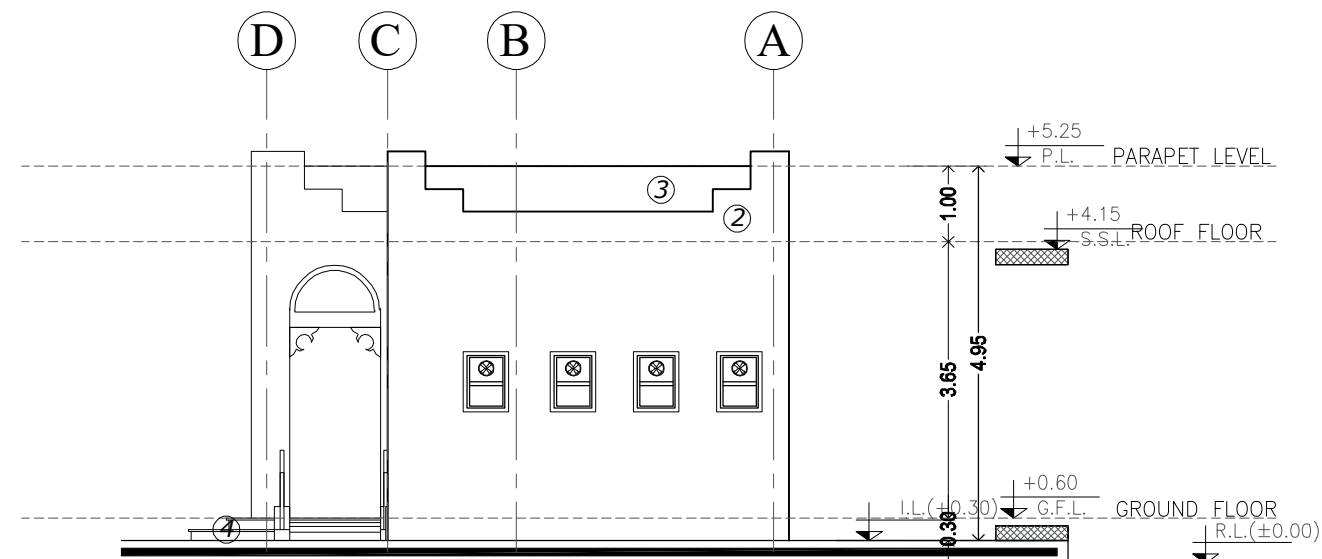


ELEVATION - B

SCALE 1:100

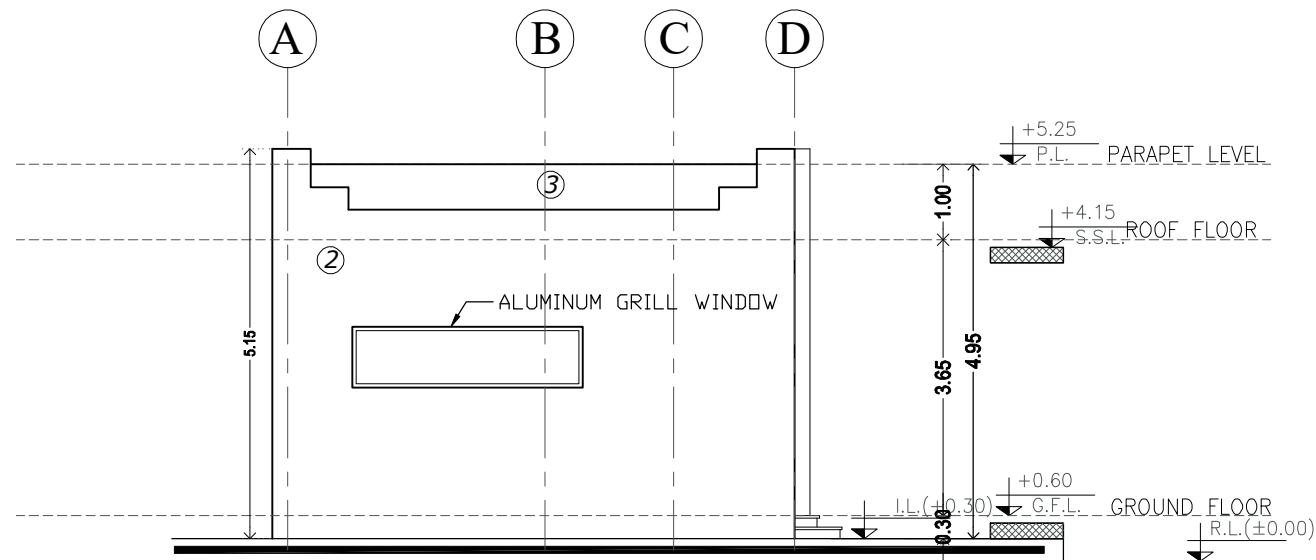


ELEVATION - D

SCALE 1:100

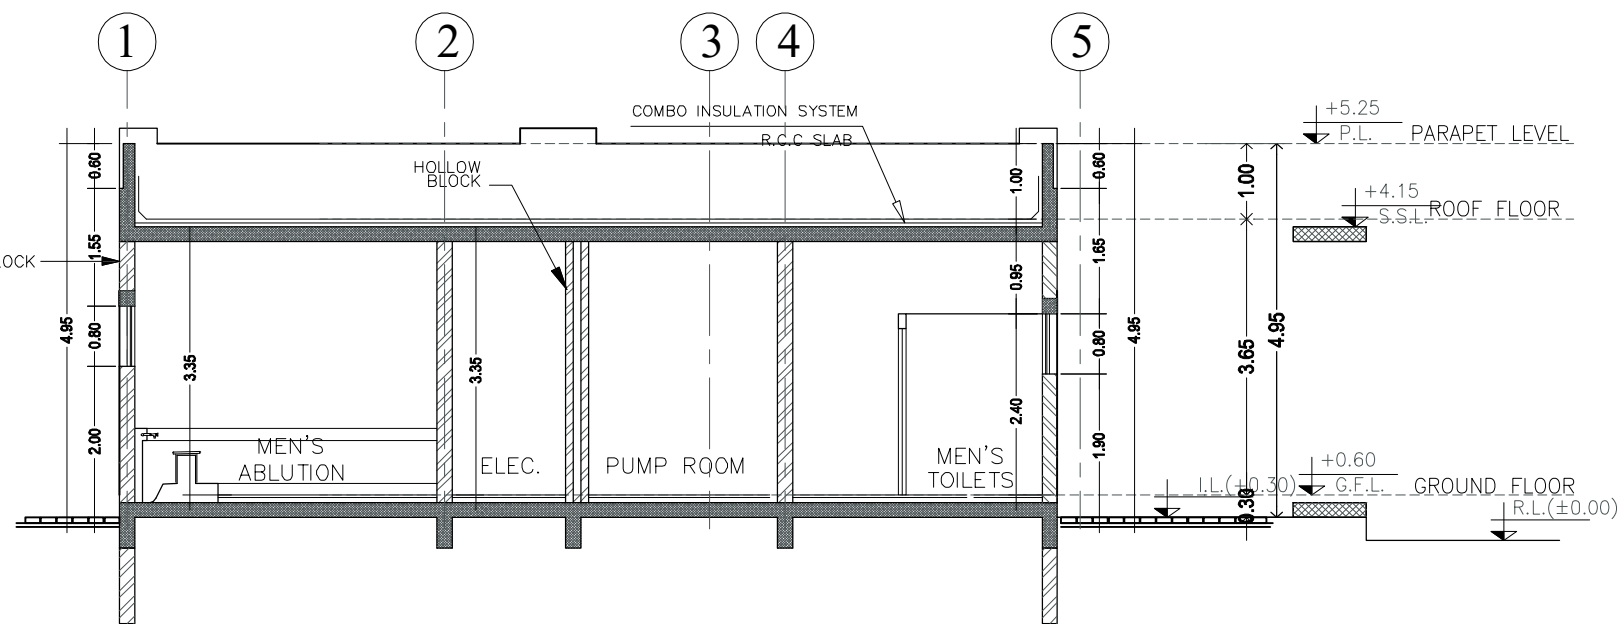


SECTION Z-Z

SCALE 1:100

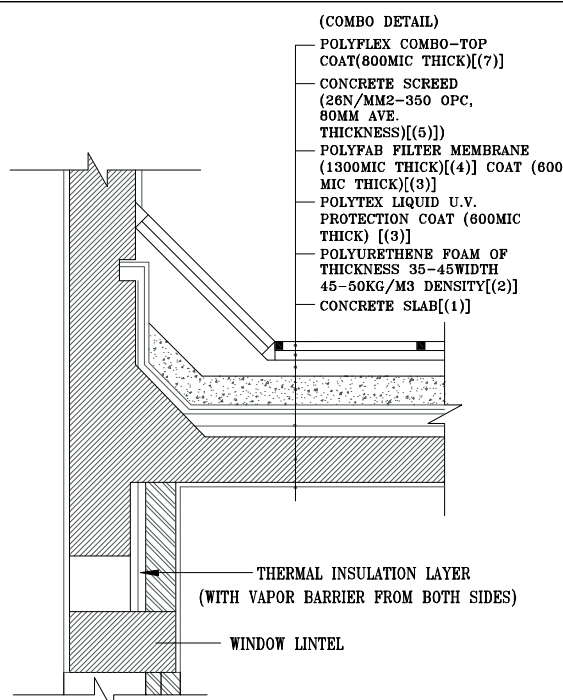

PARAPET & ROOF FINISHING DETAILS

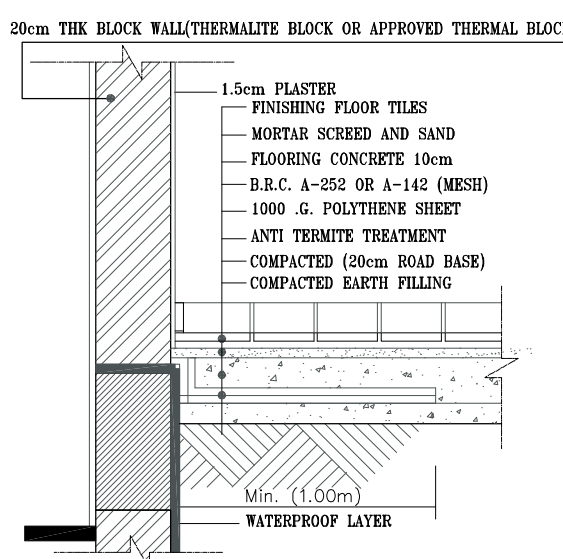

GROUND FLOOR DETAILS


ELEVATION FINISHES

- 1- REFLECTIVE GLASS
- 2- GRAFFIO DECOR WHITE PAINT OR STONE CLADDING
- 3- GRAFFIO DECOR OFF WHITE PAINT OR STONE CLADDING
- 4- GRANITE FINISHING
- 5- G.R.C.


ALL WINDOWS & BALCONY DOORS SHOULD BE EQUIPED WITH WINDOWS OPENING CONTROL DEVICE (W.O.C.D.) TO LIMITS THE OPENING LESS THAN 10 CM TO HAVE MAXIMUM OPENING LIMIT OF 10 CM TO HELP IN THE PREVENTION OF ACCIDENTAL FALLS FROM WINDOWS & BALCONIES BY CHILDREN AS PER SHARJAH MUNICIPALITY REGULATIONS.

* NOTES ::


- 1- ALL EXTERNAL WALLS TO BE 20.cm THERMAL BLOCK.
- 2- WINDOWS TO BE DOUBLE REFLECTIVE GLASS

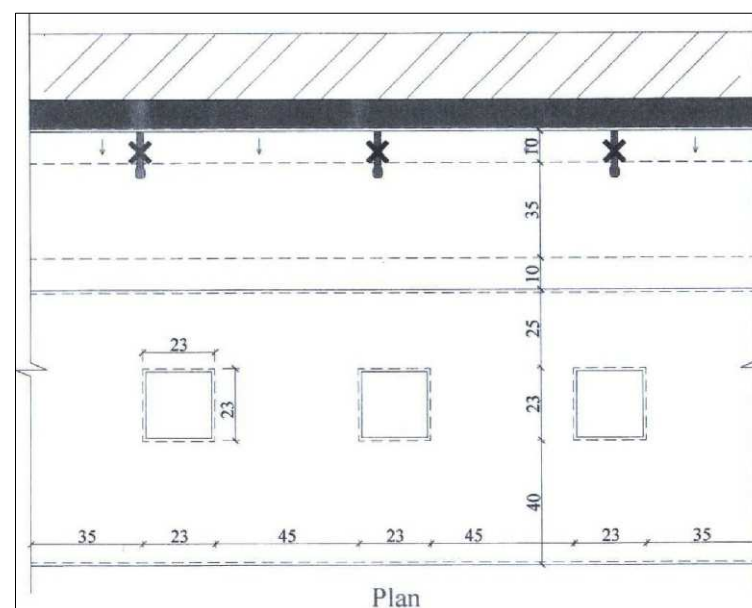


Plan

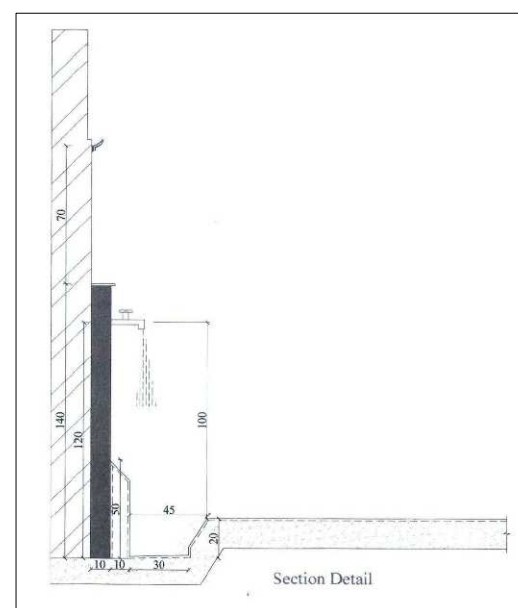

Section Detail

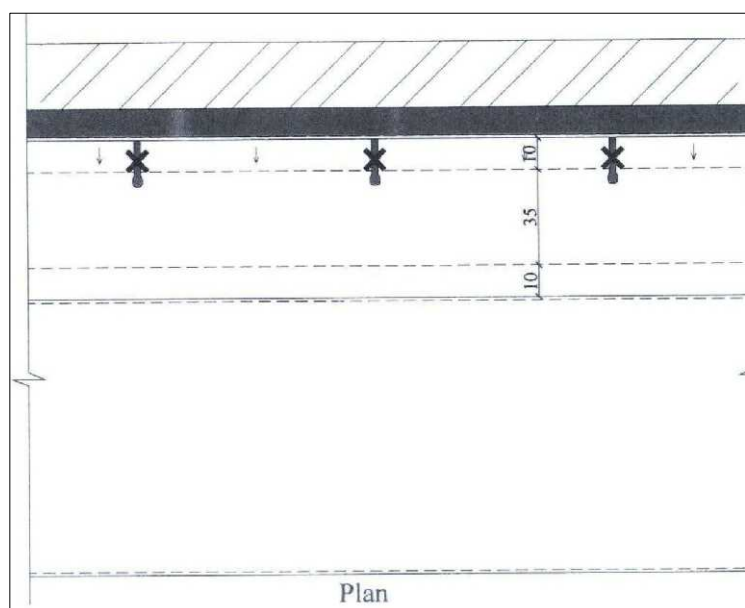

Plan

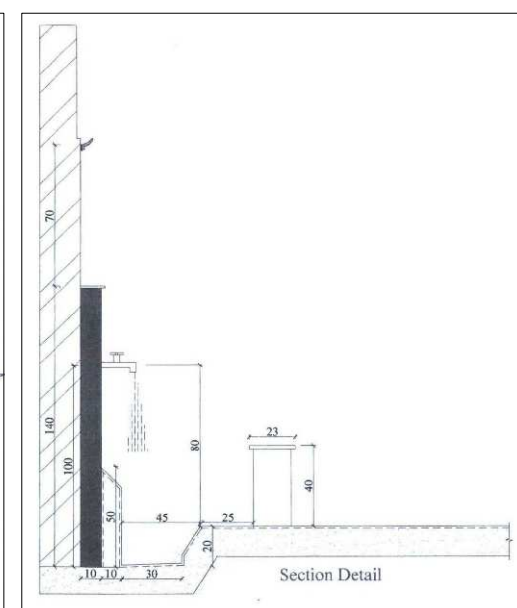

Section Detail

ABLUTION DETAIL

GENERAL NOTES:

- 1.IT IS NOT ALLOWED TO REPRODUCE THE SHEETS CONTENTS IN ANY FORM EXCEPT FOR THE PURPOSE FOR WHICH IT IS INTENDED.
2. THESE DRAWINGS ARE DIAGRAMMATIC AND SHALL NOT BE SCALED. ADDITIONAL DATA SHALL BE REQUESTED FROM THE CONSULTANCY THROUGH WRITTEN CLARIFICATION. VERIFY ALL EXISTING CONDITIONS AND DIMENSIONS BEFORE PROCEEDING WITH ANY PORTION OF ANY WORK.
3. NO CHANGES, MODIFICATIONS OR DEVIATIONS SHALL BE WRITTEN PERMISSION FROM **ALMASAH ENGINEERING CONSULTANTS**.
4. ALL WORK AS OUTLINED IN THESE DOCUMENTS, SHALL STRICTLY CONFORM TO ALL APPLICABLE CODES. IN THE EVENT OF A CONFLICT, THE MORE STRINGENT REQUIREMENT SHALL GOVERN AND BE MET.



SIA - SM-03



حكومة الشارقة
دائرة الشؤون الإسلامية

CONSULTANT STAMP



CLIENT:

GOVERNMENT OF SHARJAH -
DEPARTMENT OF ISLAMIC AFFAIRS


PROJECT:

(SIA - SM-03)
PROPOSED MASJID + ABLUTION +
IMAM HOUSE

SHEET TITLE:


ABLUTION
ELEVATIONS & SECTIONS

ARCHITECT Arch. Mostafa Ramadan	TYPE ARCHITECTURE
STRUCTURAL Eng : Mohamed Gomaa	SHEET No. A -10
CHECKED BY Eng : Mohamed Attia	Location : Plot No :
SCALE 1:100	DATE February - 2022
Project No.	SIA - SM-03

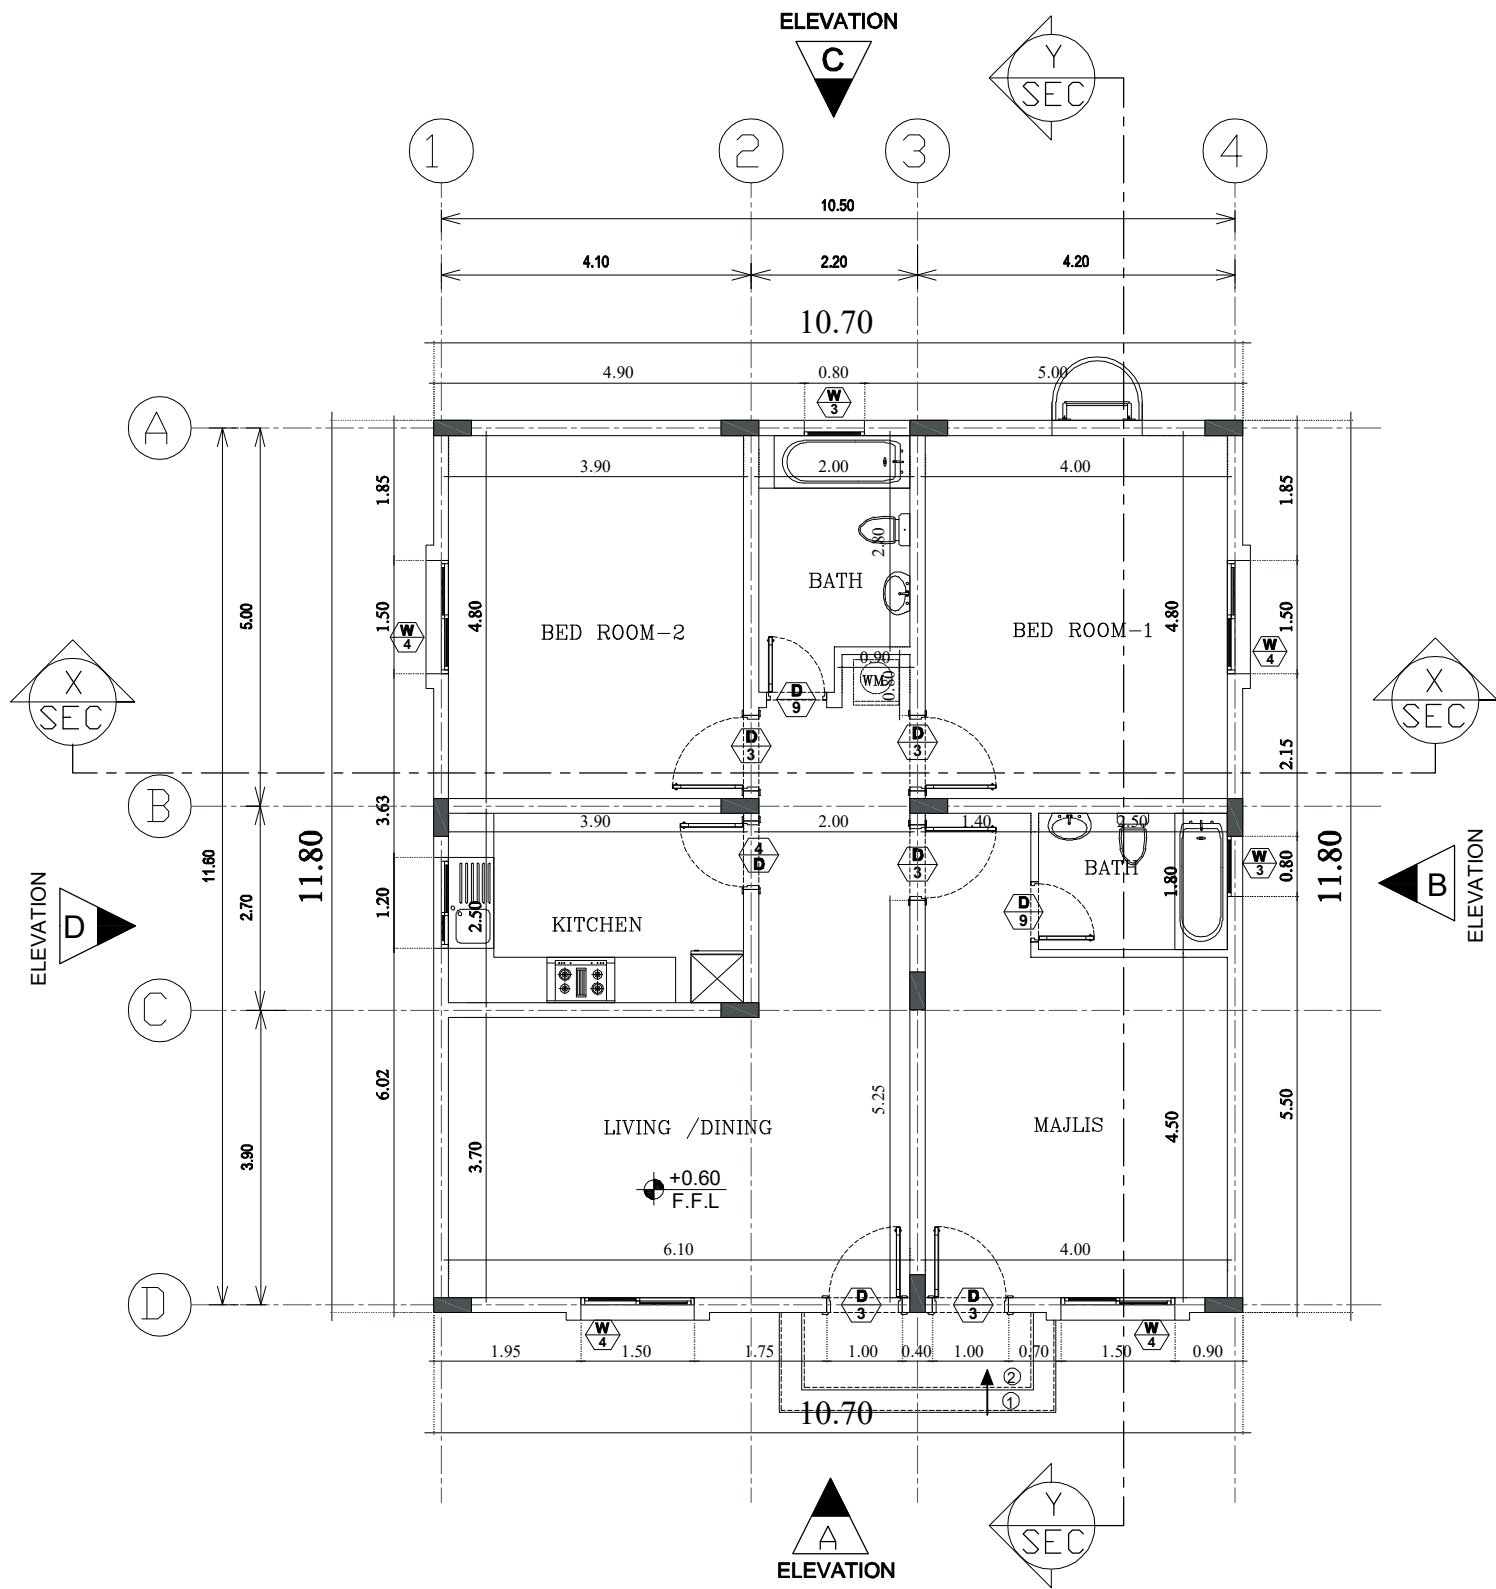

GROUND FLOOR PLAN

SCALE 1:100

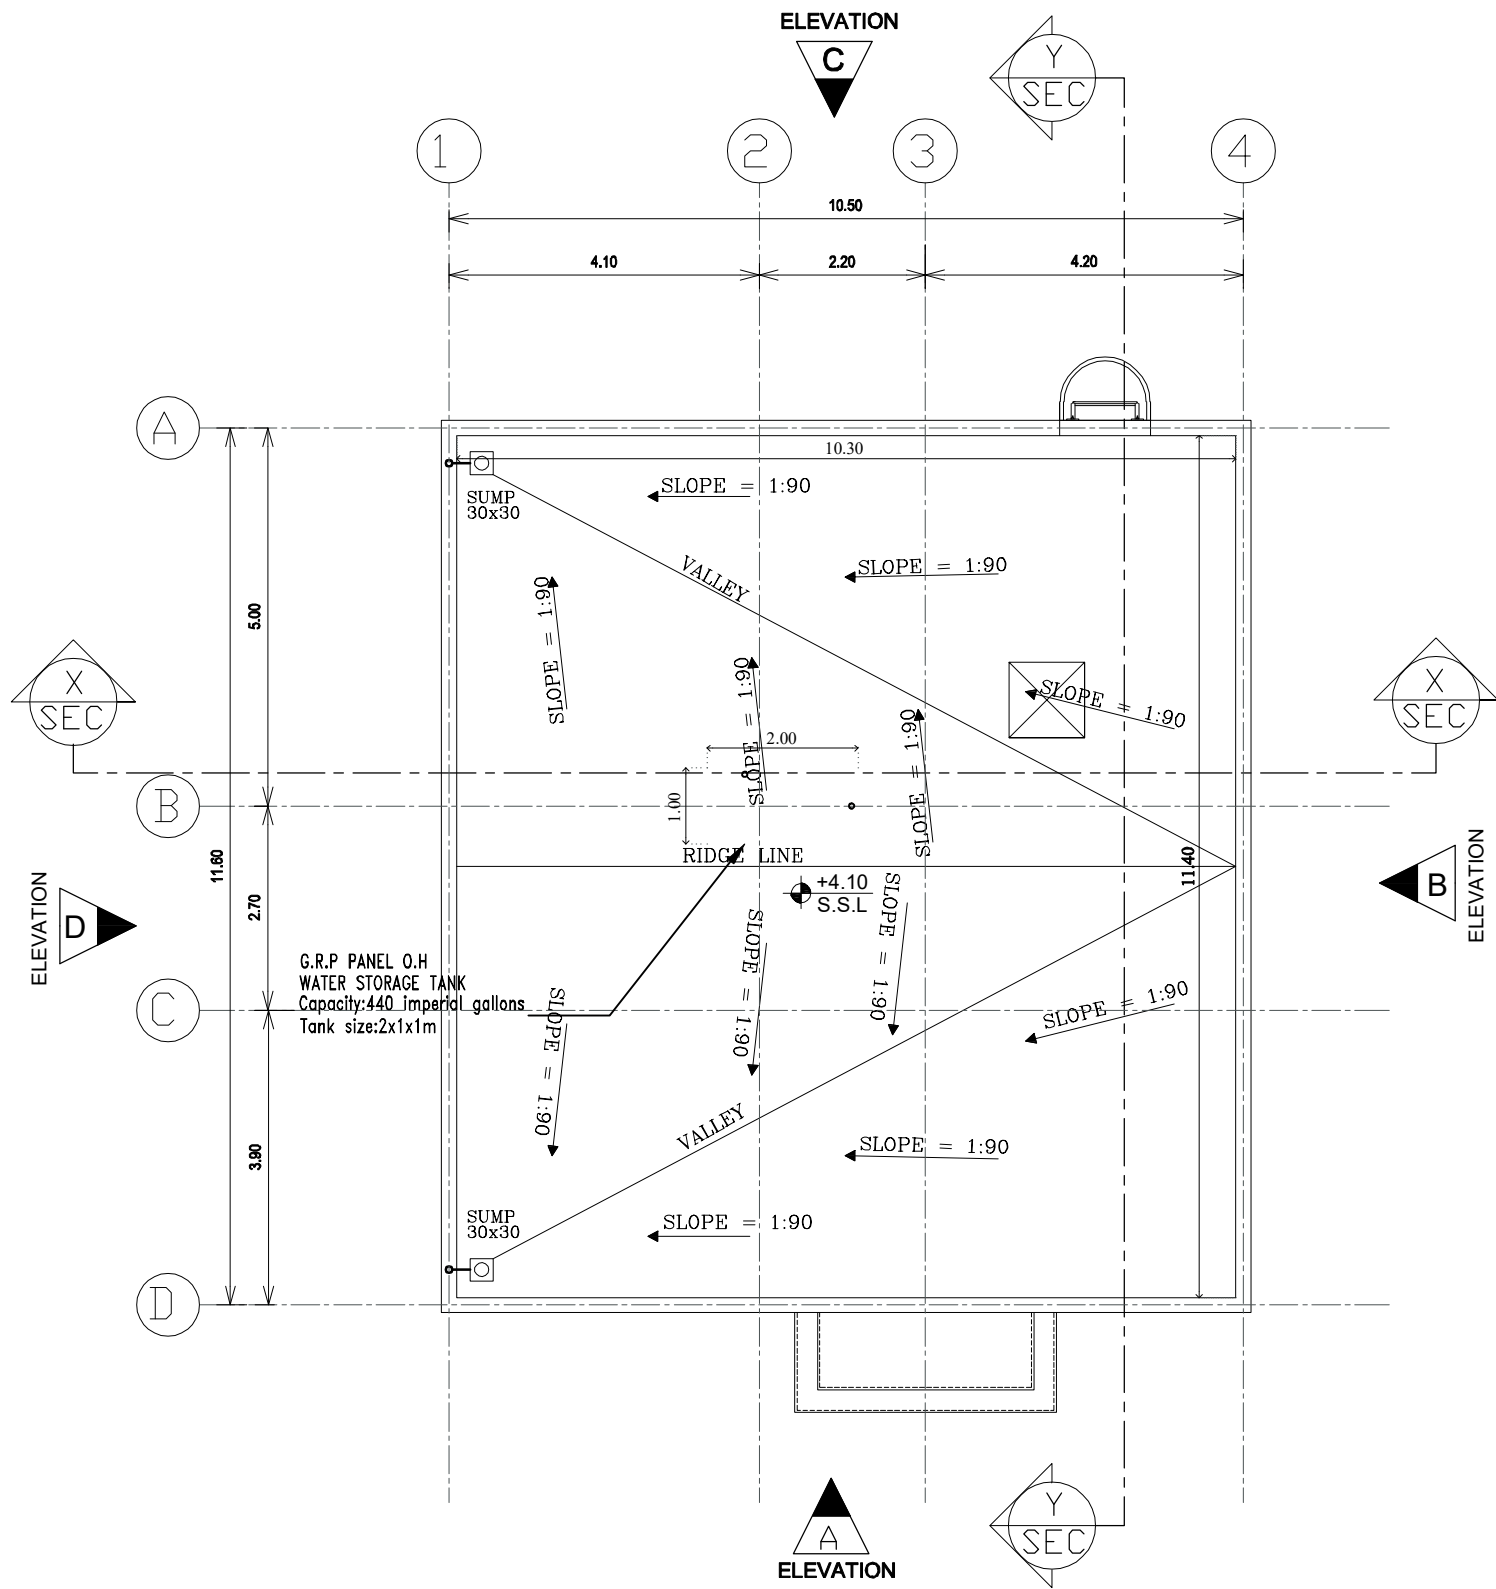

ROOF FLOOR PLAN

SCALE 1:100

GENERAL NOTES:

1. IT IS NOT ALLOWED TO REPRODUCE THE SHEETS CONTENTS IN ANY FORM EXCEPT FOR THE PURPOSE FOR WHICH IT IS INTENDED.
2. THESE DRAWINGS ARE DIAGRAMMATIC AND SHALL NOT BE SCALED. ADDITIONAL DATA SHALL BE REQUESTED FROM THE CONSULTANCY THROUGH WRITTEN CLARIFICATION. VERIFY ALL EXISTING CONDITIONS AND DIMENSIONS BEFORE PROCEEDING WITH ANY PORTION OF ANY WORK.
3. NO CHANGES, MODIFICATIONS OR DEVIATIONS SHALL BE WRITTEN PERMISSION FROM **ALMASAH ENGINEERING CONSULTANTS**.
4. ALL WORK AS OUTLINED IN THESE DOCUMENTS, SHALL STRICTLY CONFORM TO ALL APPLICABLE CODES. IN THE EVENT OF A CONFLICT, THE MORE STRINGENT REQUIREMENT SHALL GOVERN AND BE MET.




SIA - SM-03




CONSULTANT STAMP




CLIENT: GOVERNMENT OF SHARJAH - DEPARTMENT OF ISLAMIC AFFAIRS			
PROJECT: (SIA - SM-03) PROPOSED MASJID + ABLUTION + IMAM HOUSE			
SHEET TITLE: IMAM HOUSE GROUND & ROOF FLOOR PLANS			
ARCHITECT Arch. Mostafa Ramadan	TYPE	ARCHITECTURE	
STRUCTURAL Eng : Mohamed Gomaa	SHEET No.	A -11	
CHECKED BY Eng : Mohamed Attia	Location :		
	Plot No :		
SCALE 1:100	DATE February - 2022	Project No.	SIA - SM-03

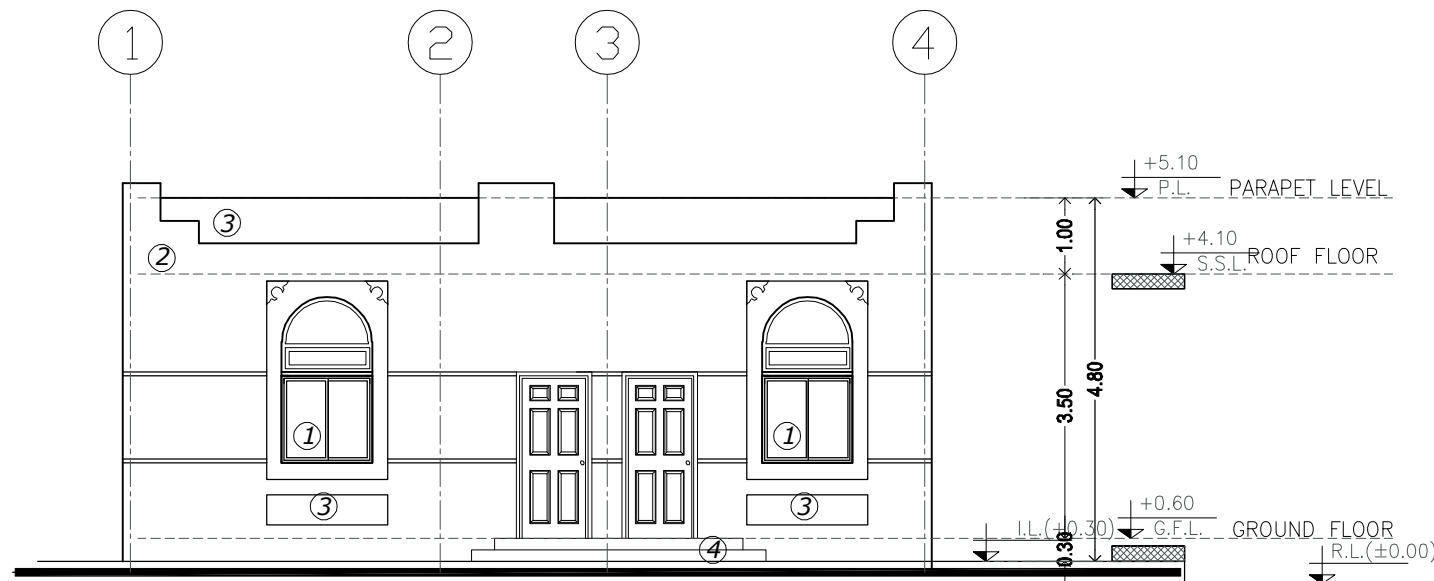


ELEVATION - A
SCALE 1:100

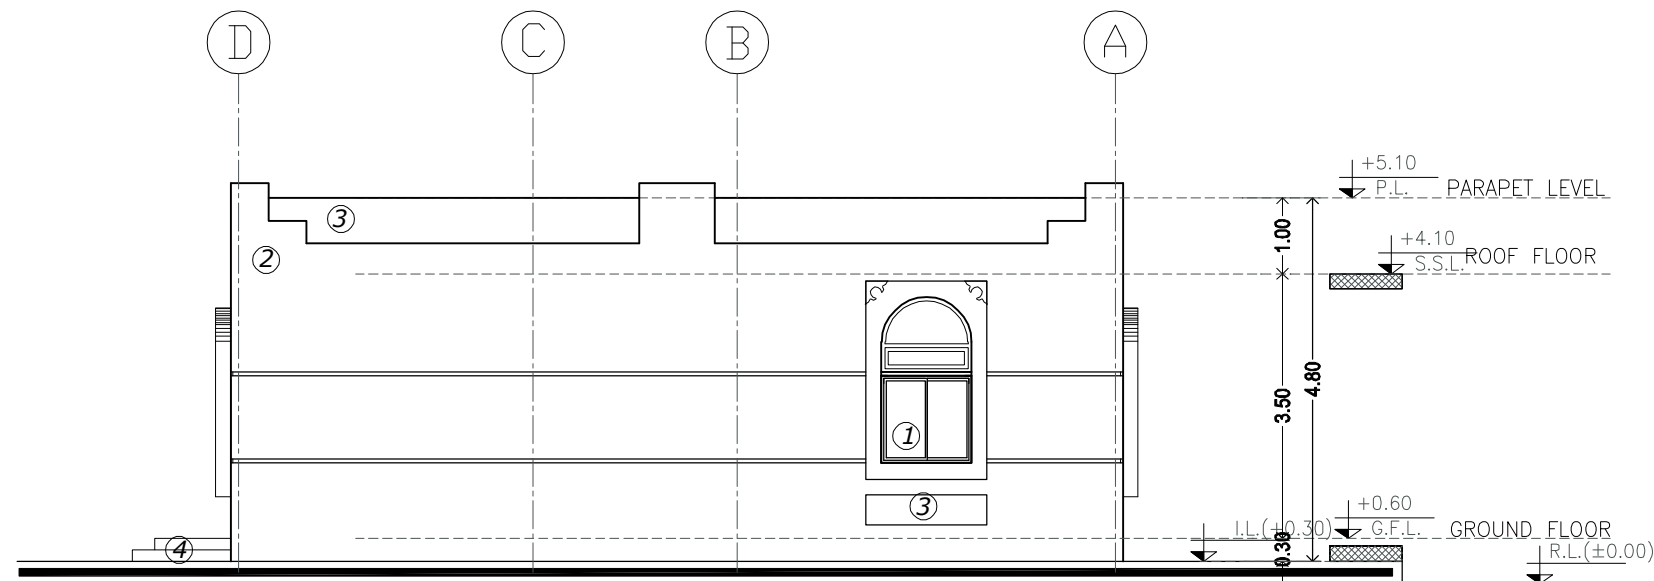


ELEVATION - B
SCALE 1:100

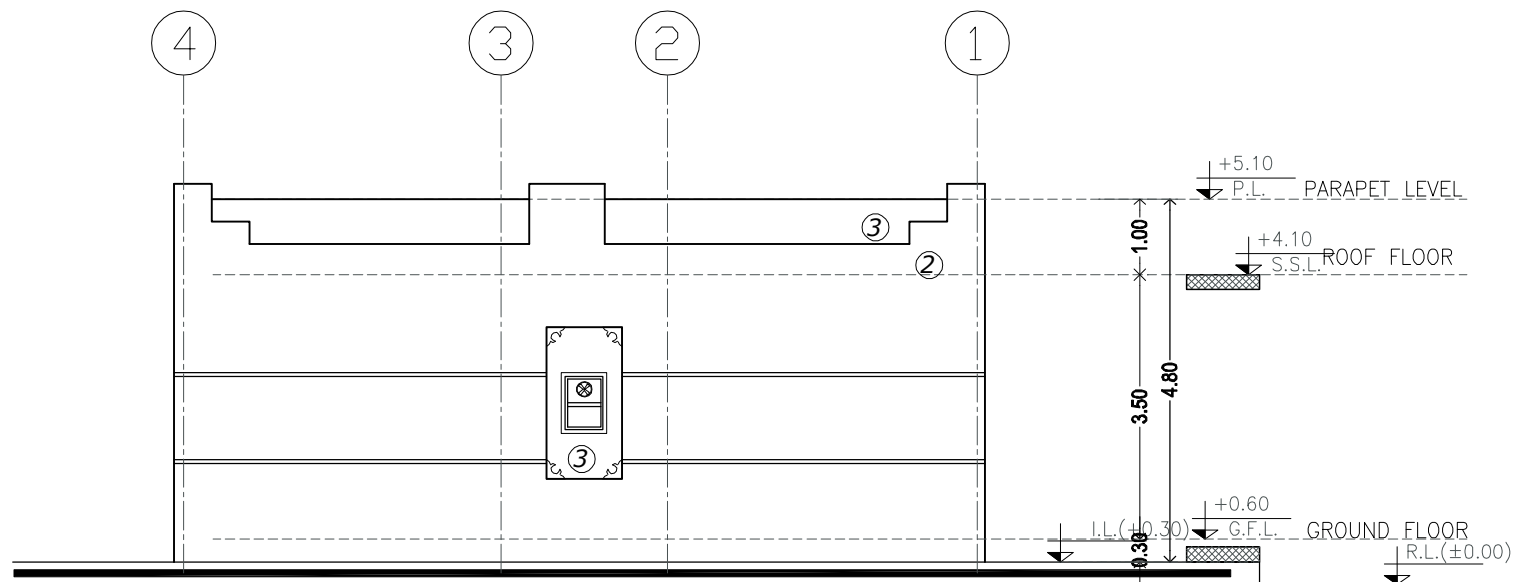


ELEVATION - C
SCALE 1:100

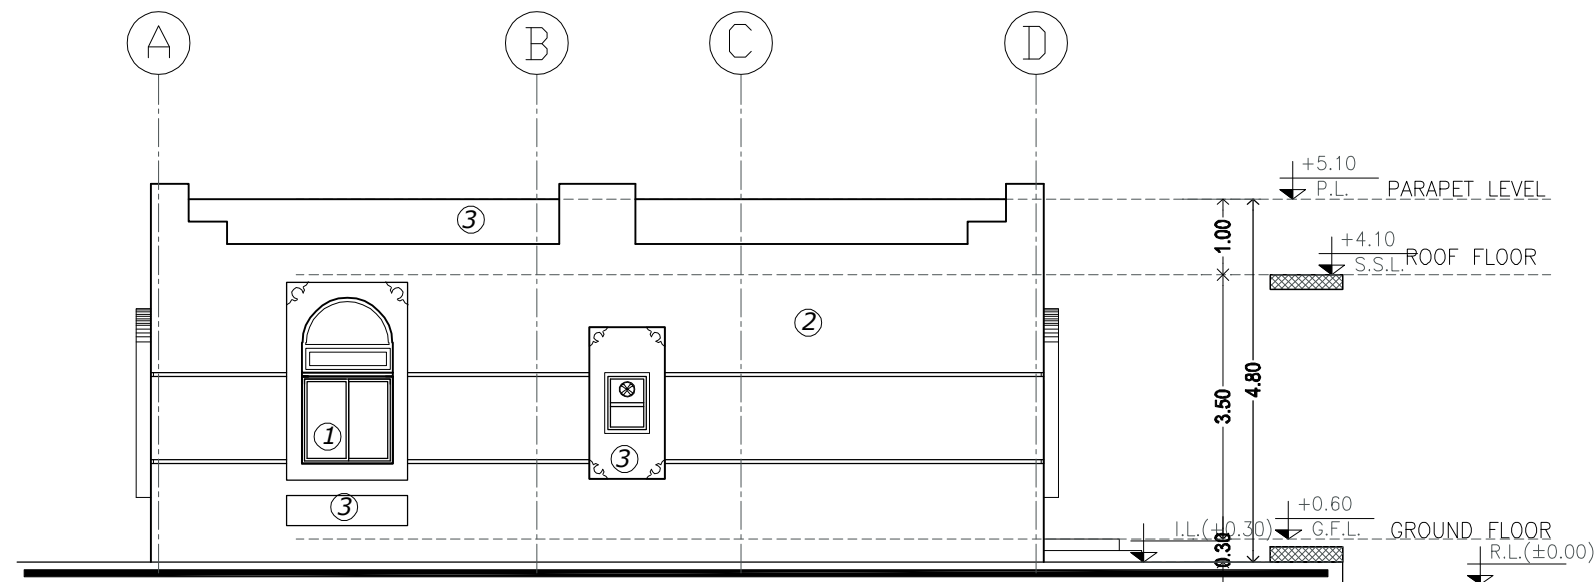



ELEVATION - D
SCALE 1:100

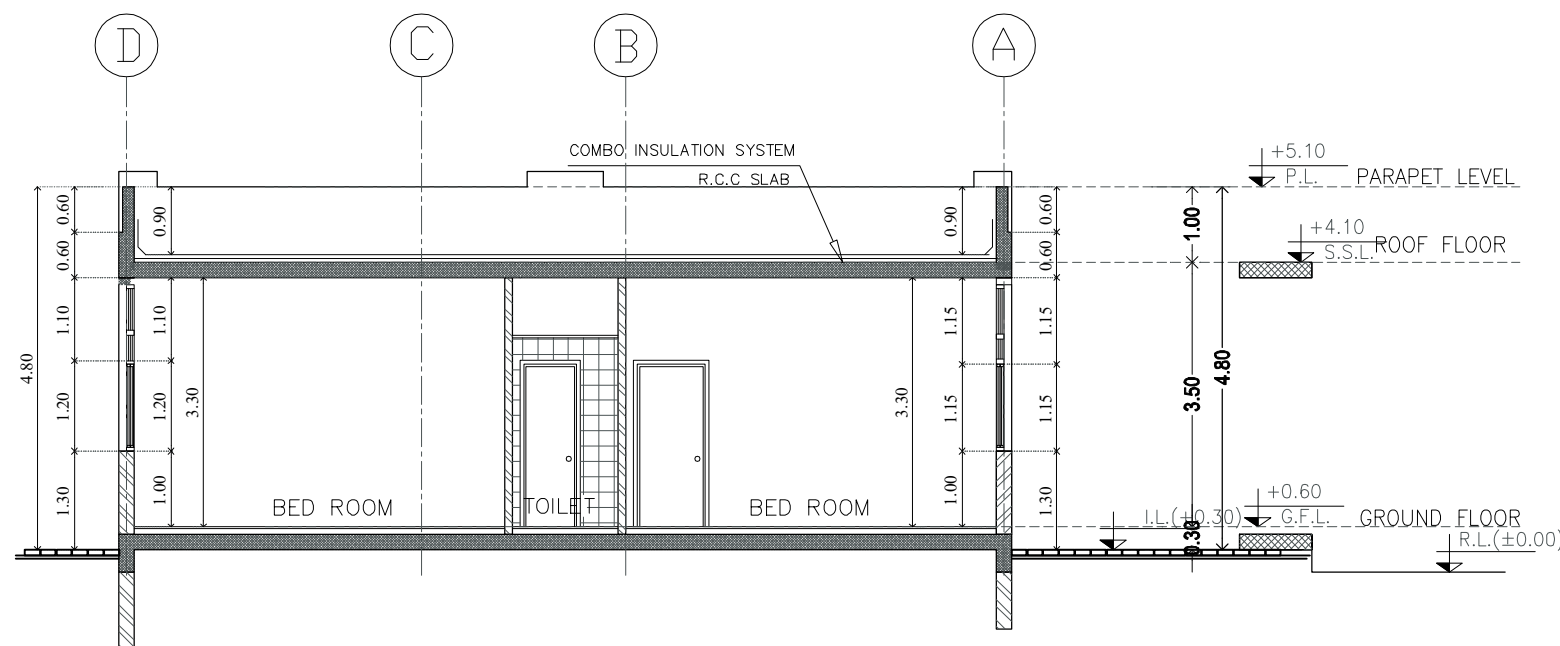

SECTION Y-Y
SCALE 1:100

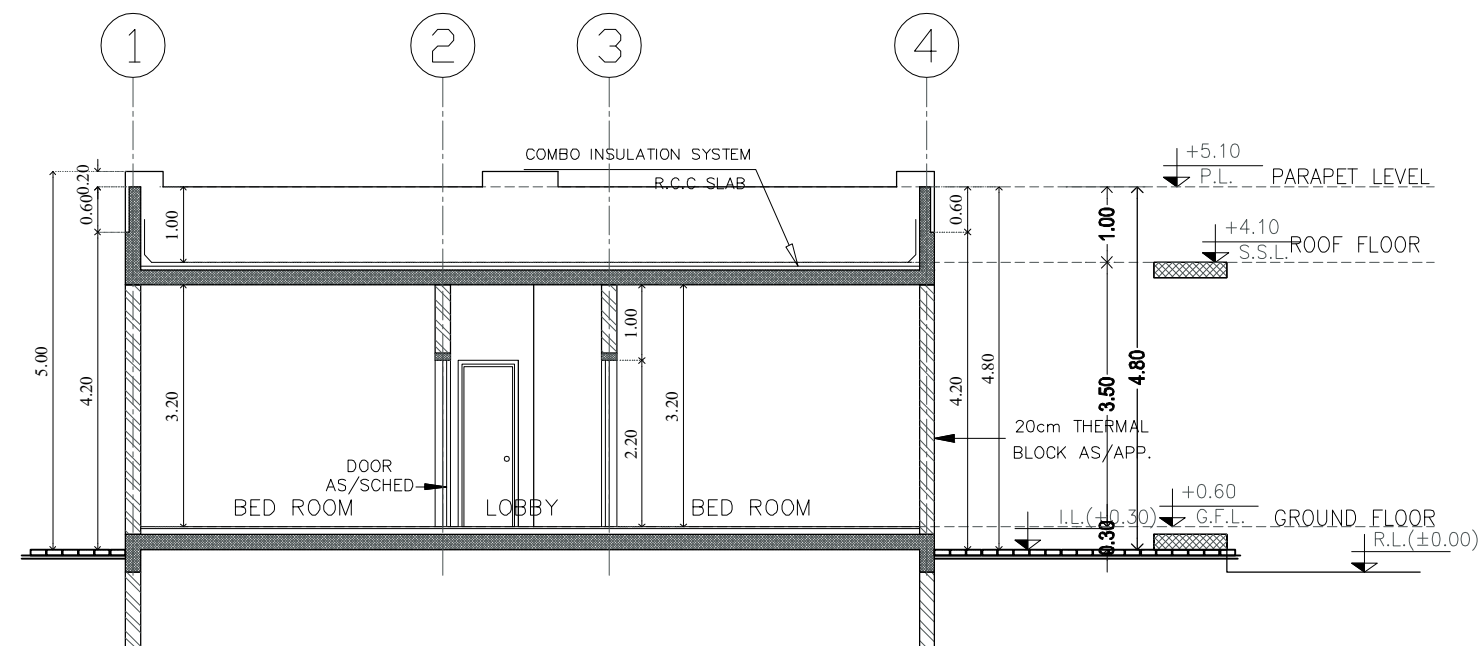

SECTION X-X
SCALE 1:100

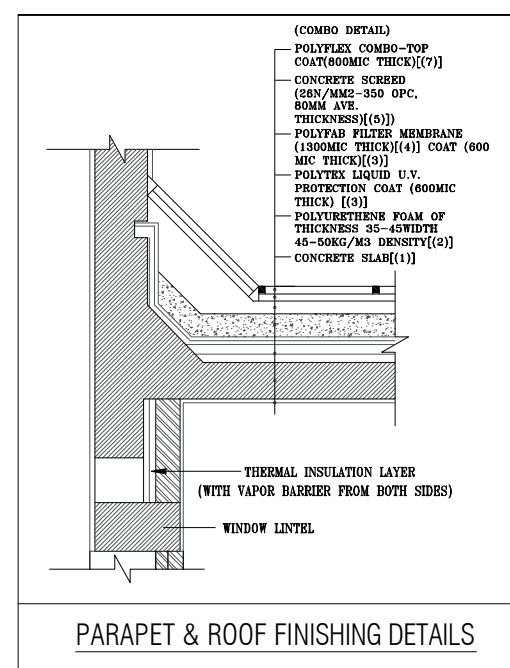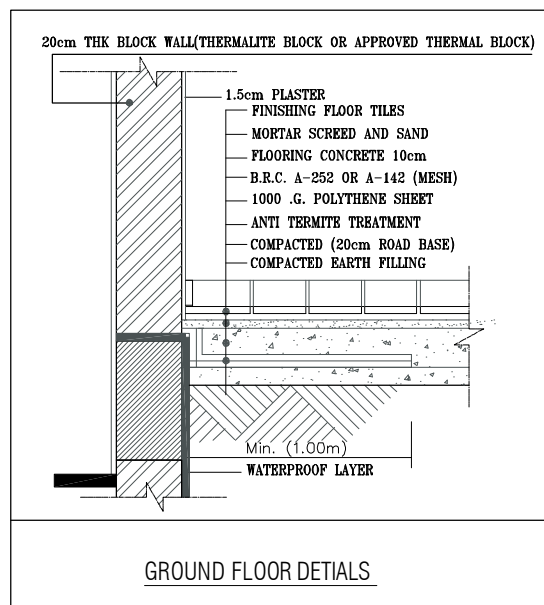

- ELEVATION FINISHES**
- 1- REFLECTIVE GLASS
 - 2- GRAFFIO DECOR WHITE PAINT OR STONE CLADDING
 - 3- GRAFFIO DECOR OFF WHITE PAINT OR STONE CLADDING
 - 4- GRANITE FINISHING
 - 5- G.R.C.

ALL WINDOWS & BALCONY DOORS SHOULD BE EQUIPED WITH WINDOWS OPENING CONTROL DEVICE (W.O.C.D.) TO LIMITS THE OPENING LESS THAN 10 CM TO HAVE MAXIMUM OPENING LIMIT OF 10 CM TO HELP IN THE PREVENTION OF ACCIDENTAL FALLS FROM WINDOWS & BALCONIES BY CHILDREN AS PER SHARJAH MUNICIPALITY REGULATIONS.

- * NOTES :**
- 1- ALL EXTERNAL WALLS TO BE 20.cm THERMAL BLOCK.
 - 2- WINDOWS TO BE DOUBLE REFLECTIVE GLASS


- GENERAL NOTES:**
1. IT IS NOT ALLOWED TO REPRODUCE THE SHEETS CONTENTS IN ANY FORM EXCEPT FOR THE PURPOSE FOR WHICH IT IS INTENDED.
 2. THESE DRAWINGS ARE DIAGRAMMATIC AND SHALL NOT BE SCALED. ADDITIONAL DATA SHALL BE REQUESTED FROM THE CONSULTANCY THROUGH WRITTEN CLARIFICATION. VERIFY ALL EXISTING CONDITIONS AND DIMENSIONS BEFORE PROCEEDING WITH ANY PORTION OF ANY WORK.
 3. NO CHANGES, MODIFICATIONS OR DEVIATIONS SHALL BE WRITTEN PERMISSION FROM **ALMASAH ENGINEERING CONSULTANTS**.
 4. ALL WORK AS OUTLINED IN THESE DOCUMENTS, SHALL STRICTLY CONFORM TO ALL APPLICABLE CODES. IN THE EVENT OF A CONFLICT, THE MORE STRINGENT REQUIREMENT SHALL GOVERN AND BE MET.




SIA - SM-03




حكومة الشارقة
دائرة الشؤون الإسلامية

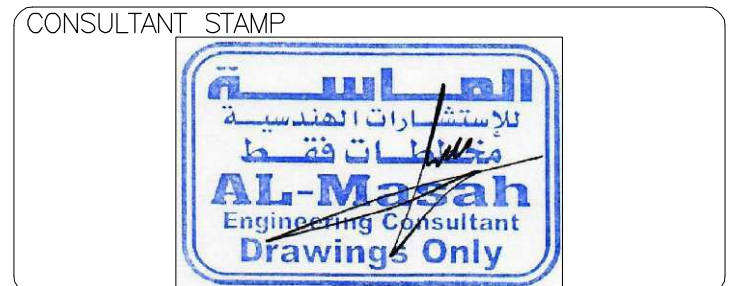


CLIENT: GOVERNMENT OF SHARJAH - DEPARTMENT OF ISLAMIC AFFAIRS		
PROJECT: (SIA - SM-03) PROPOSED MASJID + ABLUTION + IMAM HOUSE		
SHEET TITLE: IMAM HOUSE ELEVATIONS & SECTION		
ARCHITECT Arch. Mostafa Ramadan	TYPE	ARCHITECTURE
STRUCTURAL Eng : Mohamed Gomaa	SHEET No.	A -12
CHECKED BY Eng : Mohamed Attia	Location :	
SCALE 1:100	DATE February - 2022	Project No.
		SIA - SM-03

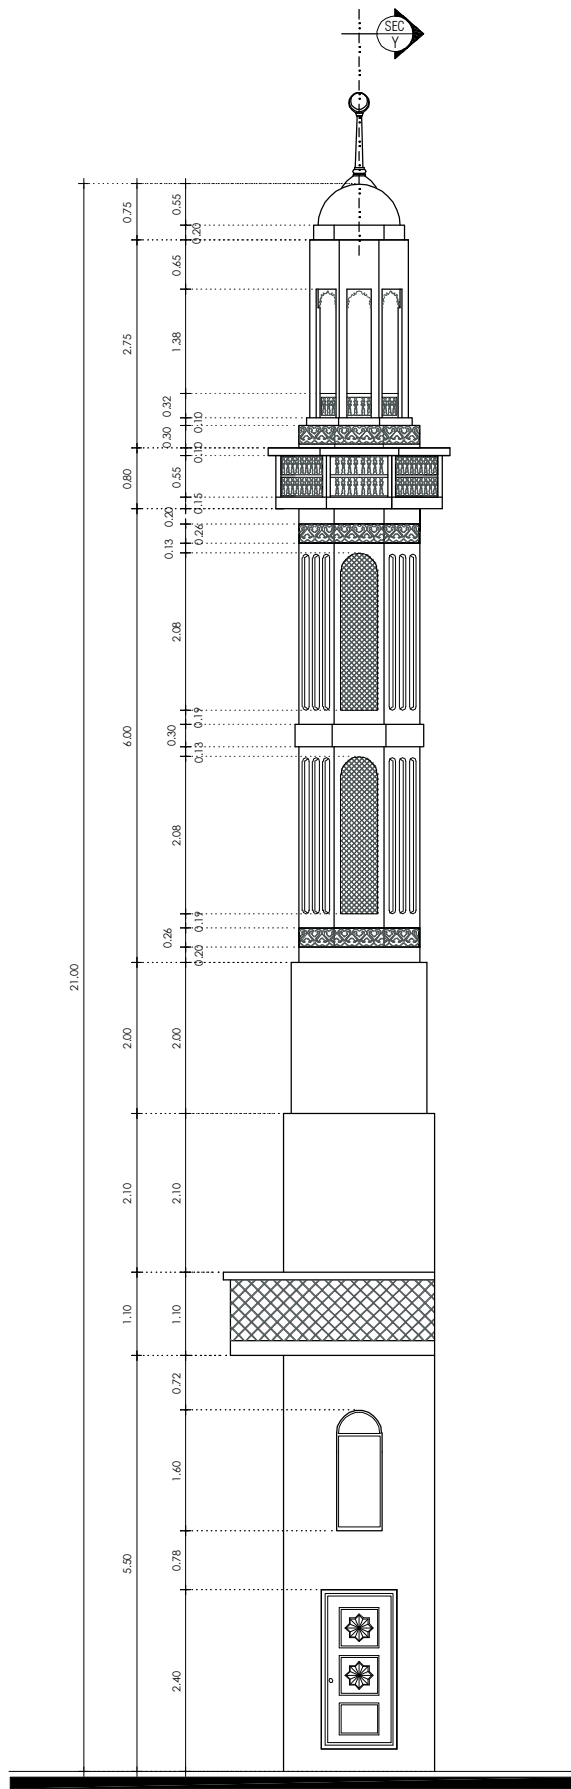


MANAR ELEVATION
(SCALE = 1 : 100)

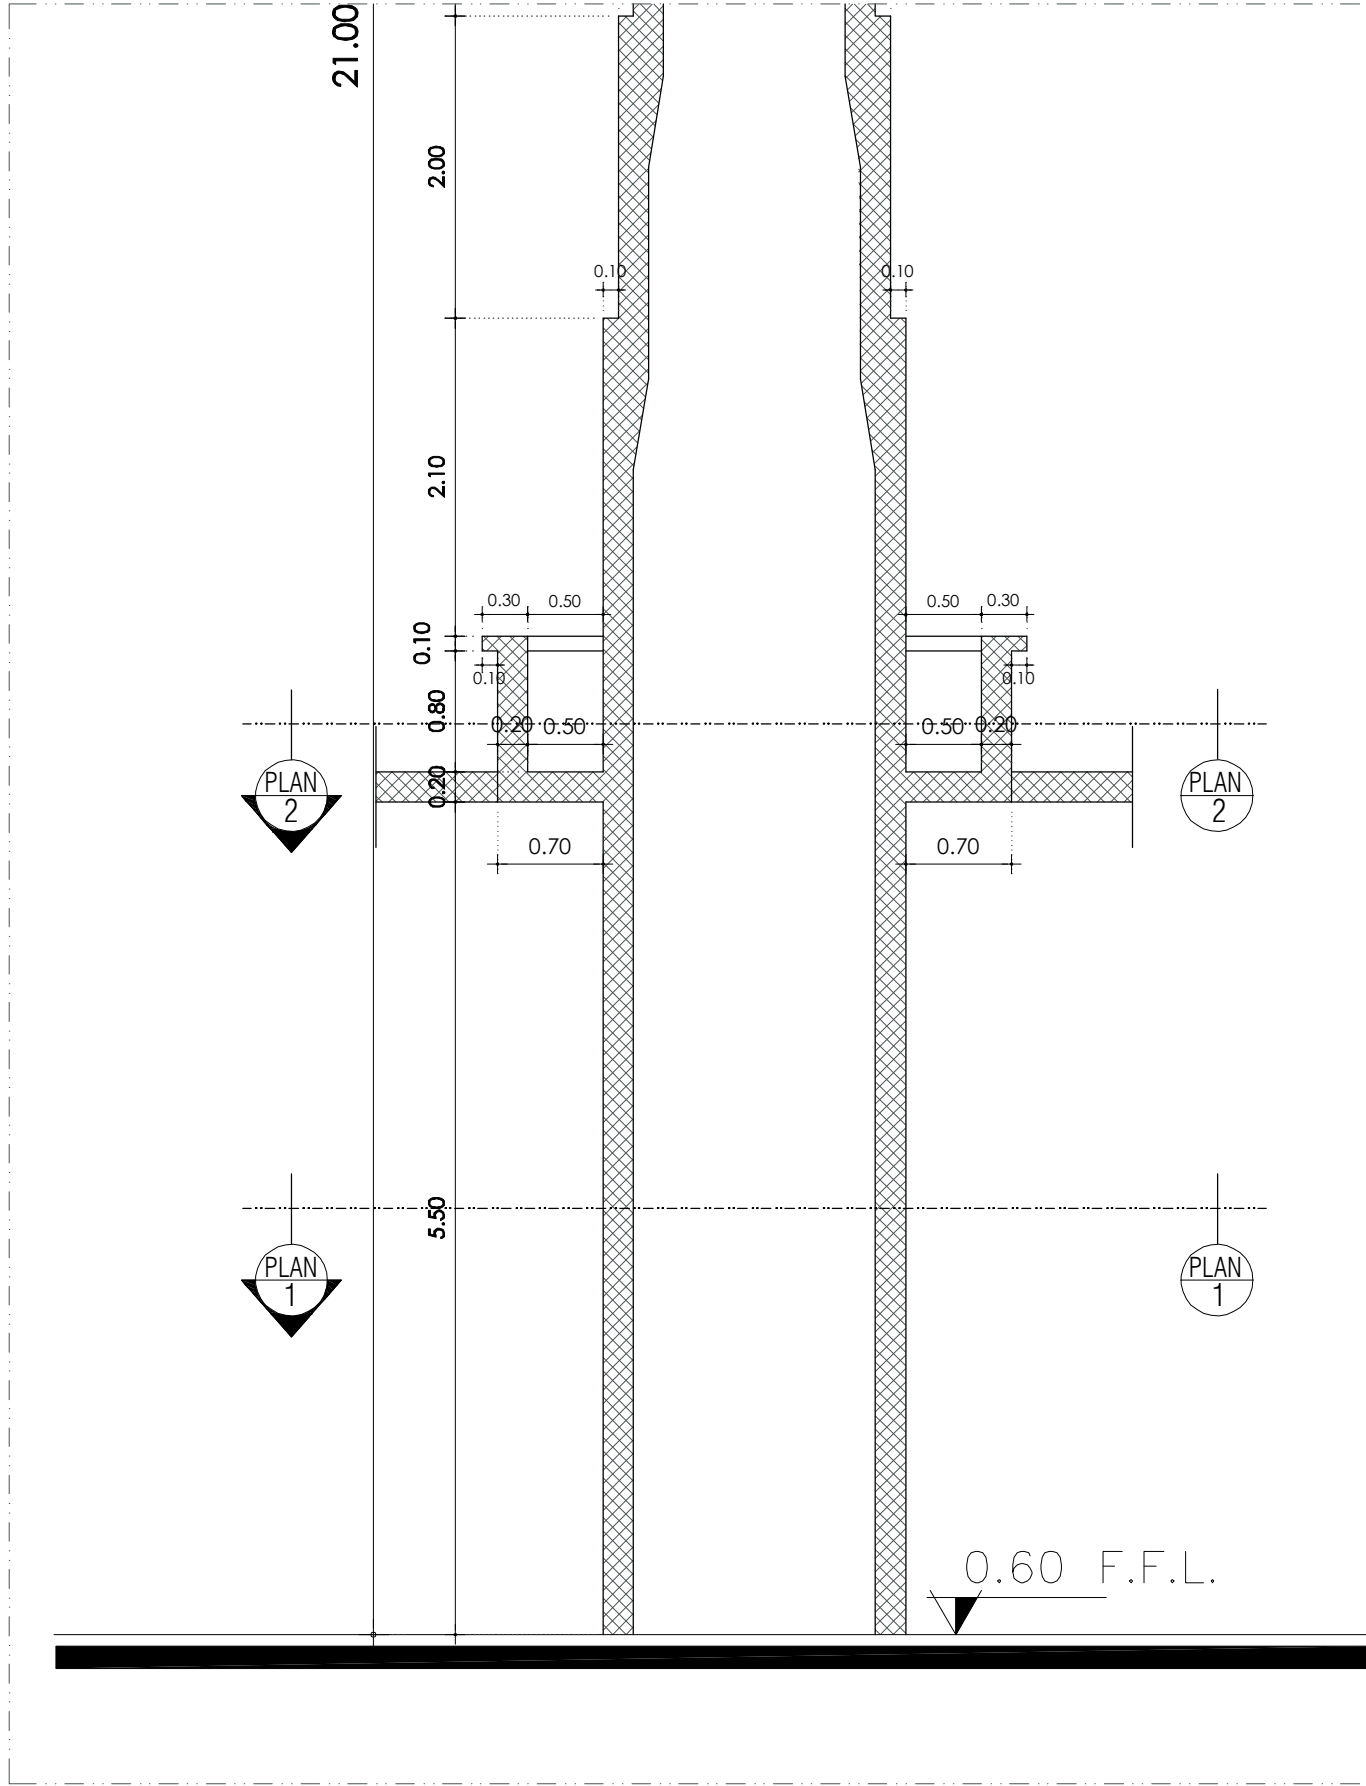


SECTION Y-Y
(SCALE = 1 : 50)

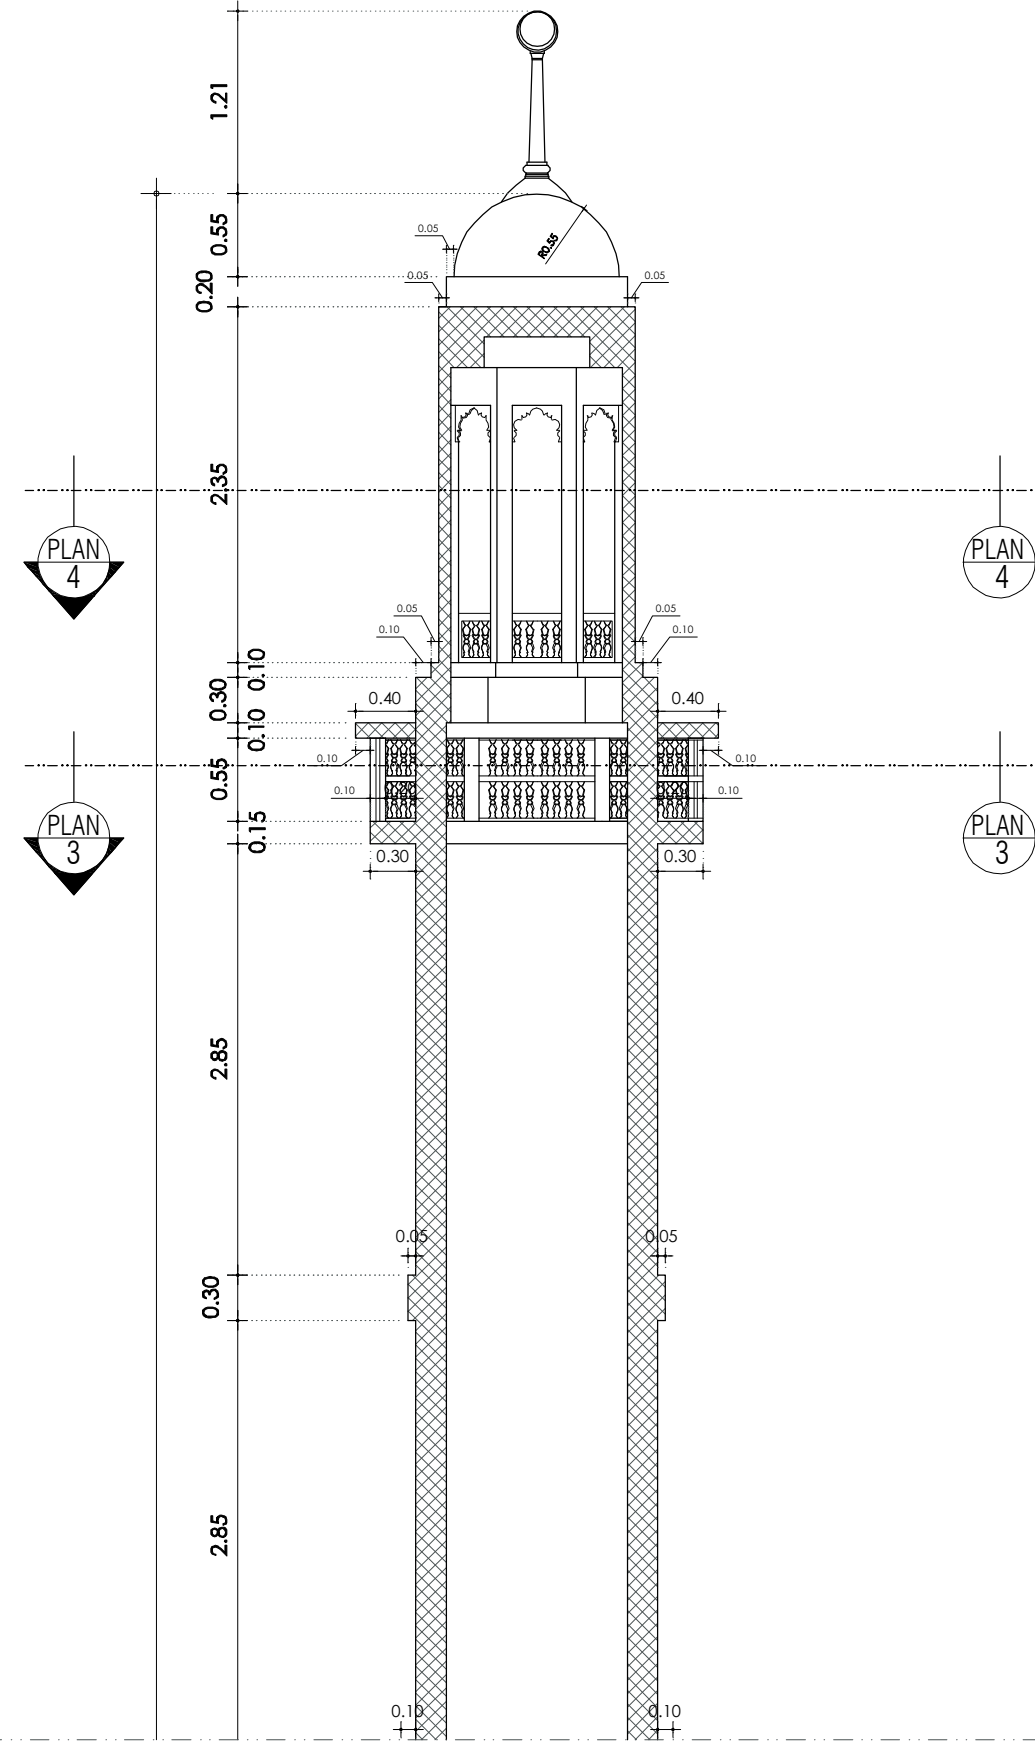


SECTION Y-Y
(SCALE = 1 : 50)

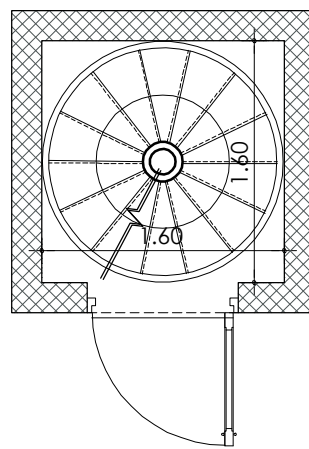


PLAN -1
(SCALE = 1 : 50)

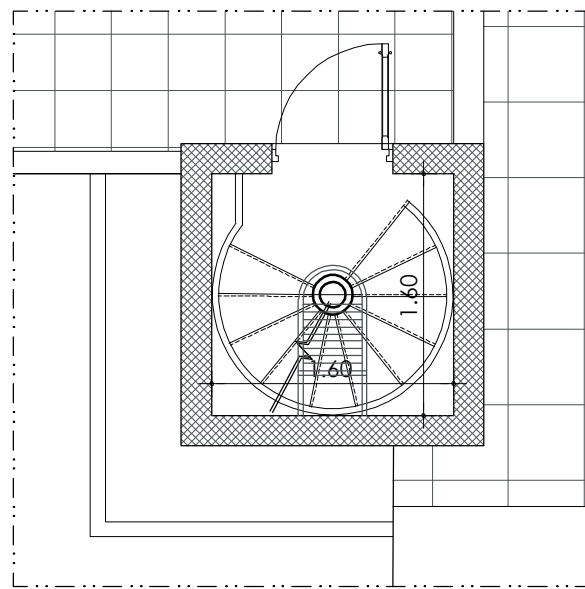

PLAN -2
(SCALE = 1 : 50)

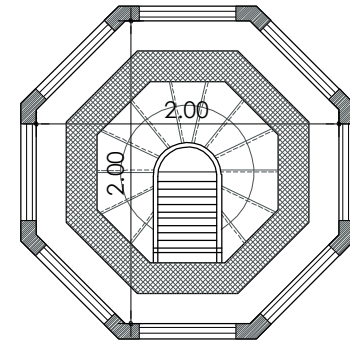

PLAN -3
(SCALE = 1 : 50)

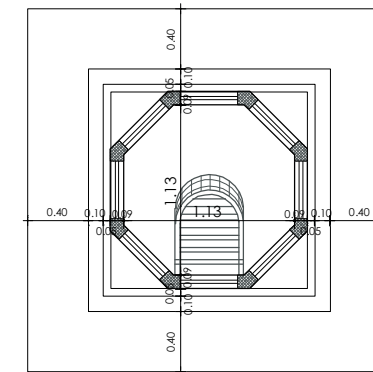

PLAN -4
(SCALE = 1 : 50)

GENERAL NOTES:

- 1.IT IS NOT ALLOWED TO REPRODUCE THE SHEETS CONTENTS IN ANY FORM EXCEPT FOR THE PURPOSE FOR WHICH IT IS INTENDED.
2. THESE DRAWINGS ARE DIAGRAMMATIC AND SHALL NOT BE SCALED. ADDITIONAL DATA SHALL BE REQUESTED FROM THE CONSULTANCY THROUGH WRITTEN CLARIFICATION. VERIFY ALL EXISTING CONDITIONS AND DIMENSIONS BEFORE PROCEEDING WITH ANY PORTION OF ANY WORK.
3. NO CHANGES, MODIFICATIONS OR DEVIATIONS SHALL BE WRITTEN PERMISSION FROM **ALMASAH ENGINEERING CONSULTANTS**.
4. ALL WORK AS OUTLINED IN THESE DOCUMENTS, SHALL STRICTLY CONFORM TO ALL APPLICABLE CODES. IN THE EVENT OF A CONFLICT, THE MORE STRINGENT REQUIREMENT SHALL GOVERN AND BE MET.

SIA - SM-03



حُكُومَةُ الشَّارِقَةِ
دائرة الشؤون الإسلامية

CONSULTANT STAMP



Sharjah ☎ 06 5 444 521 ☎ 06 5 444 523 📍 Office: 306, Al Fisal 2 Bldg., King Fisal St.

CLIENT:

GOVERNMENT OF SHARJAH -
DEPARTMENT OF ISLAMIC AFFAIRS









PROJECT:

(SIA - SM-03)
PROPOSED MASJID + ABLUTION +
IMAM HOUSE

SHEET TITLE:

MANAR DETAILS

ARCHITECT Arch. Mostafa Ramadan	TYPE ARCHITECTURE
STRUCTURAL Eng : Mohamed Gomaa	SHEET No. A -13
CHECKED BY Eng : Mohamed Attia	Location : Plot No :
SCALE 1:100	DATE February - 2022
Project No.	SIA - SM-03

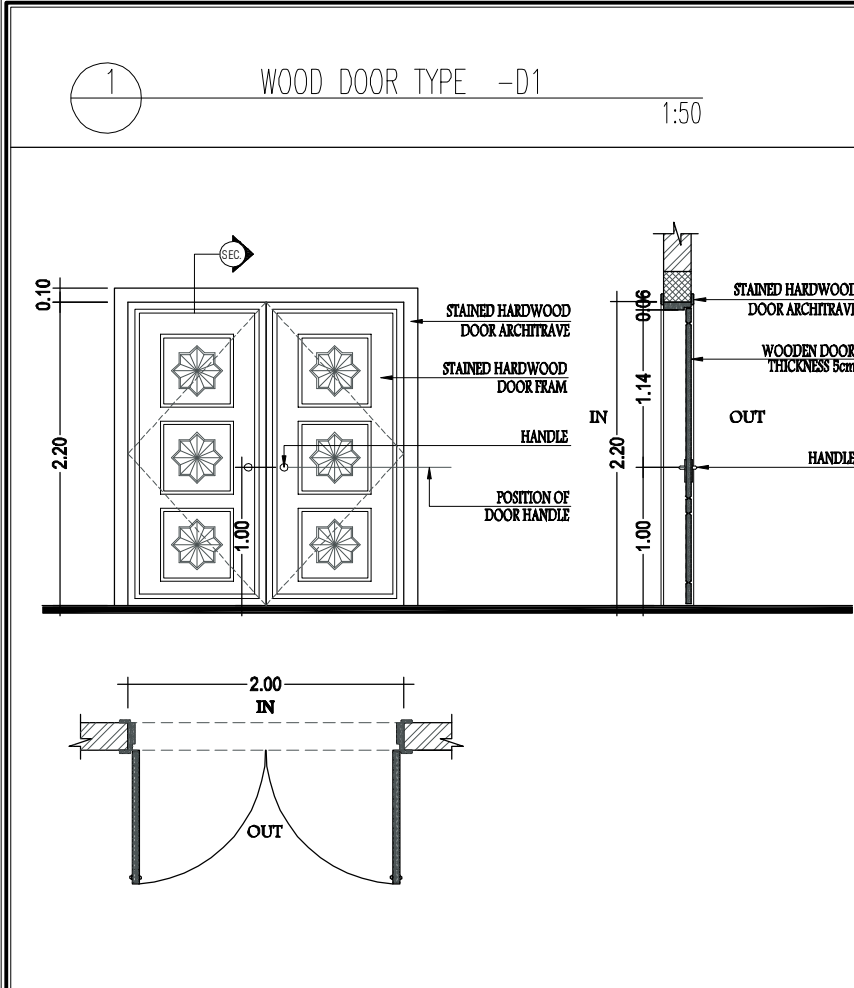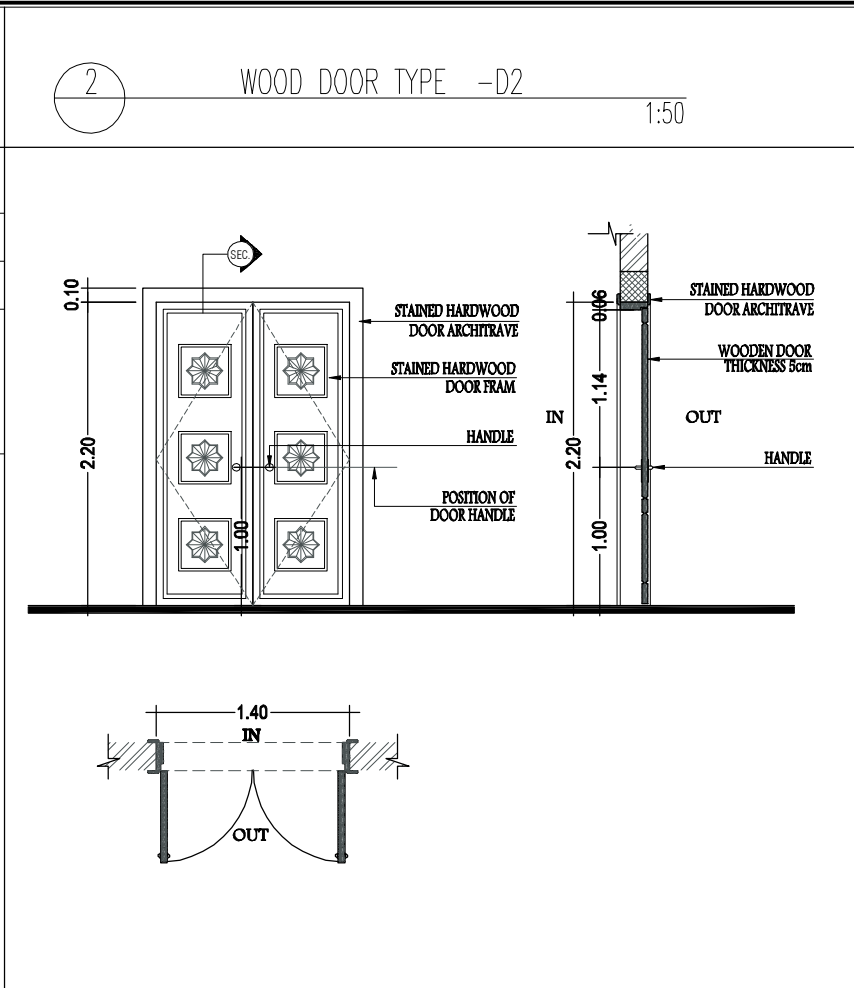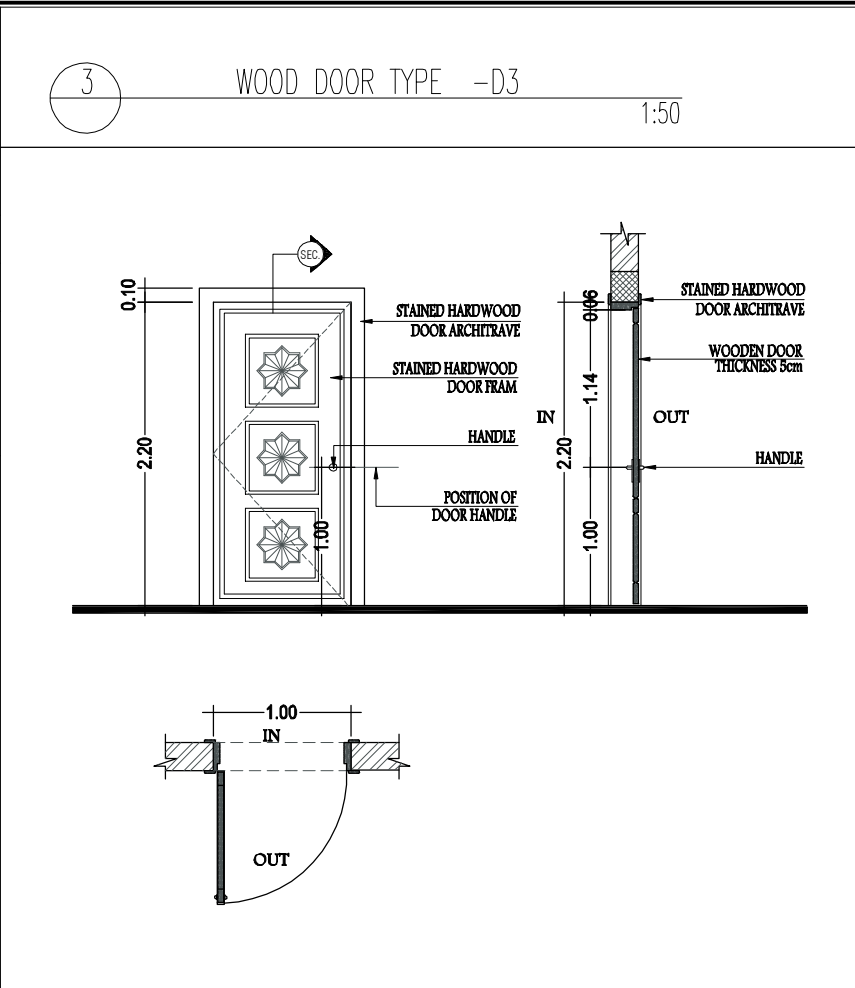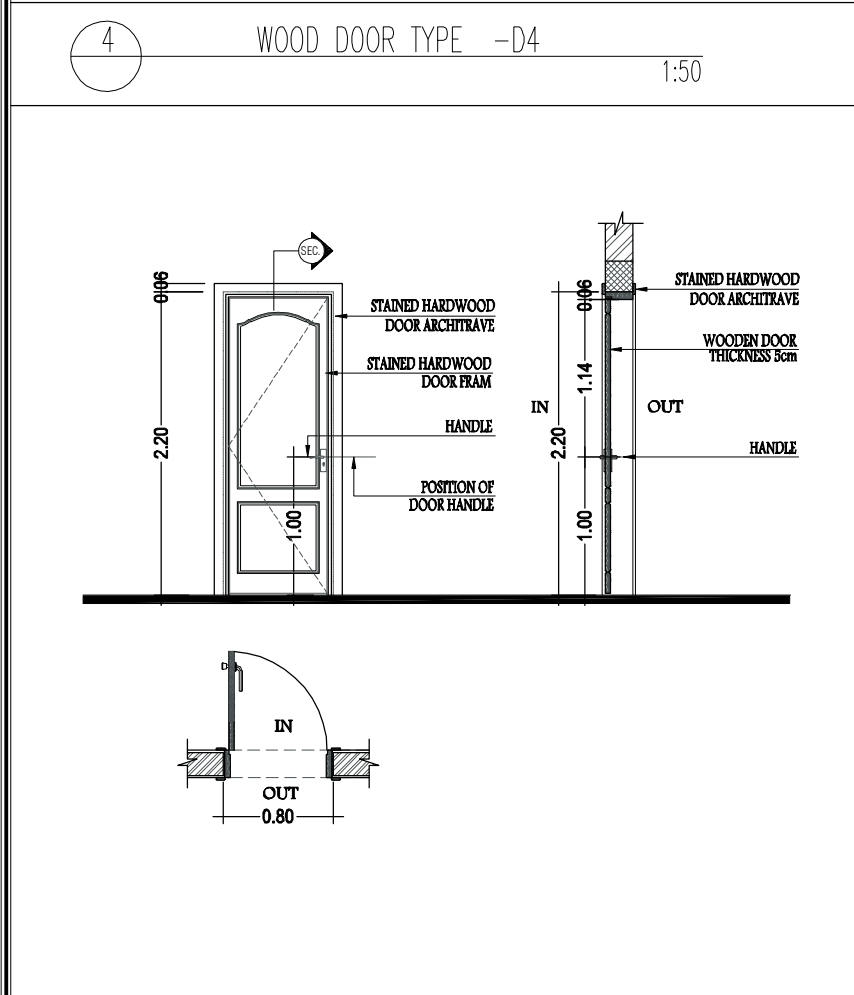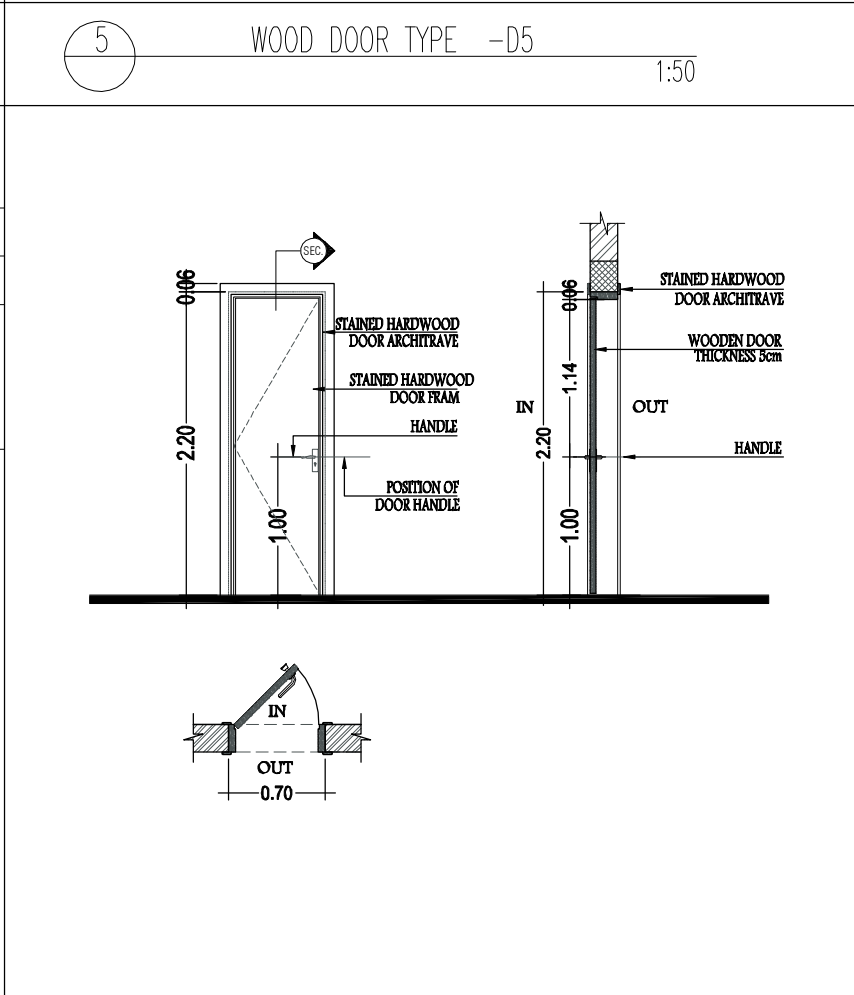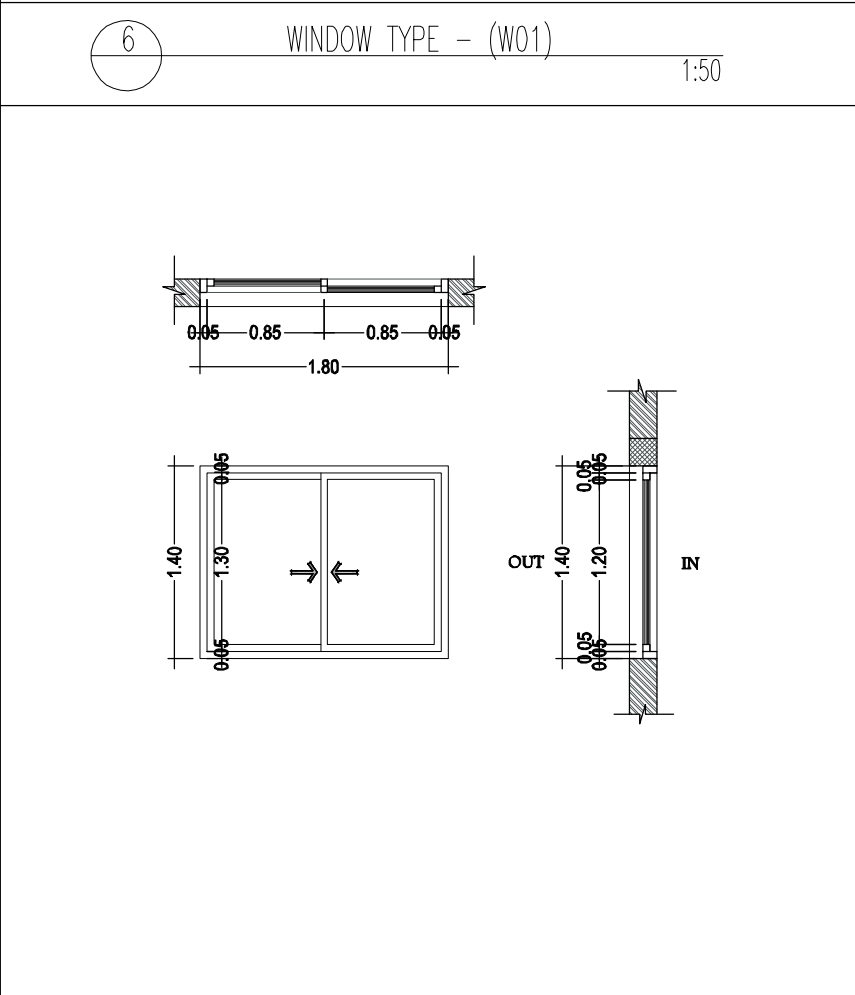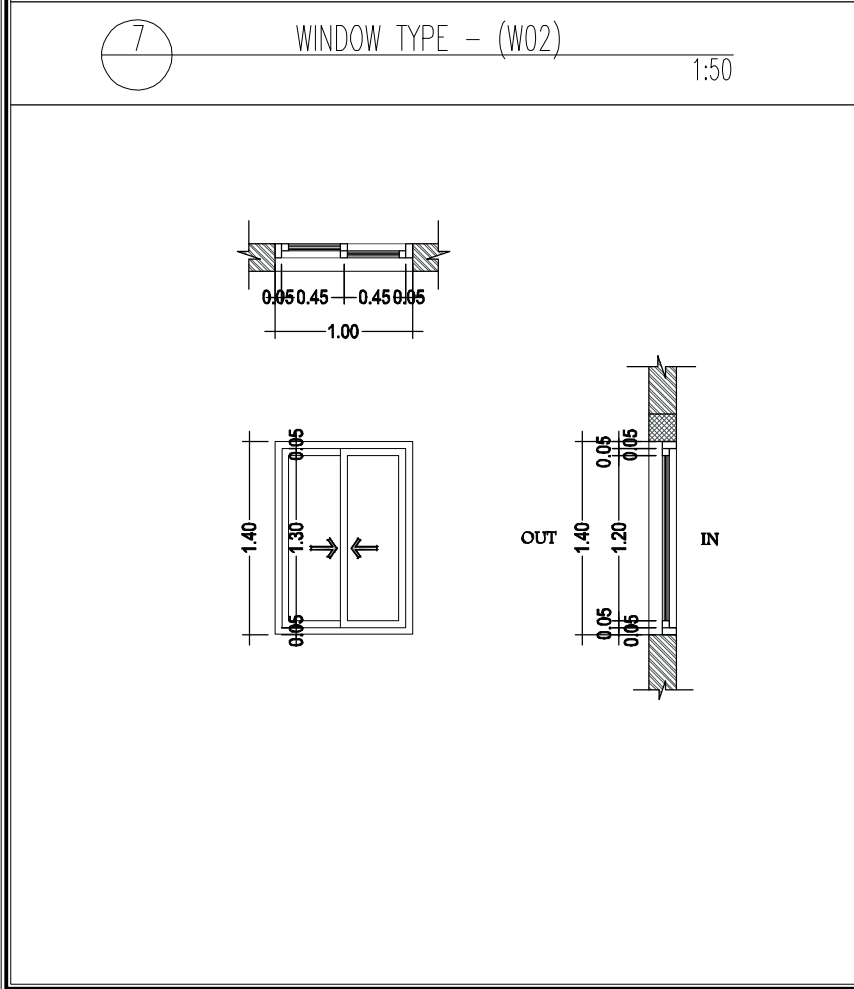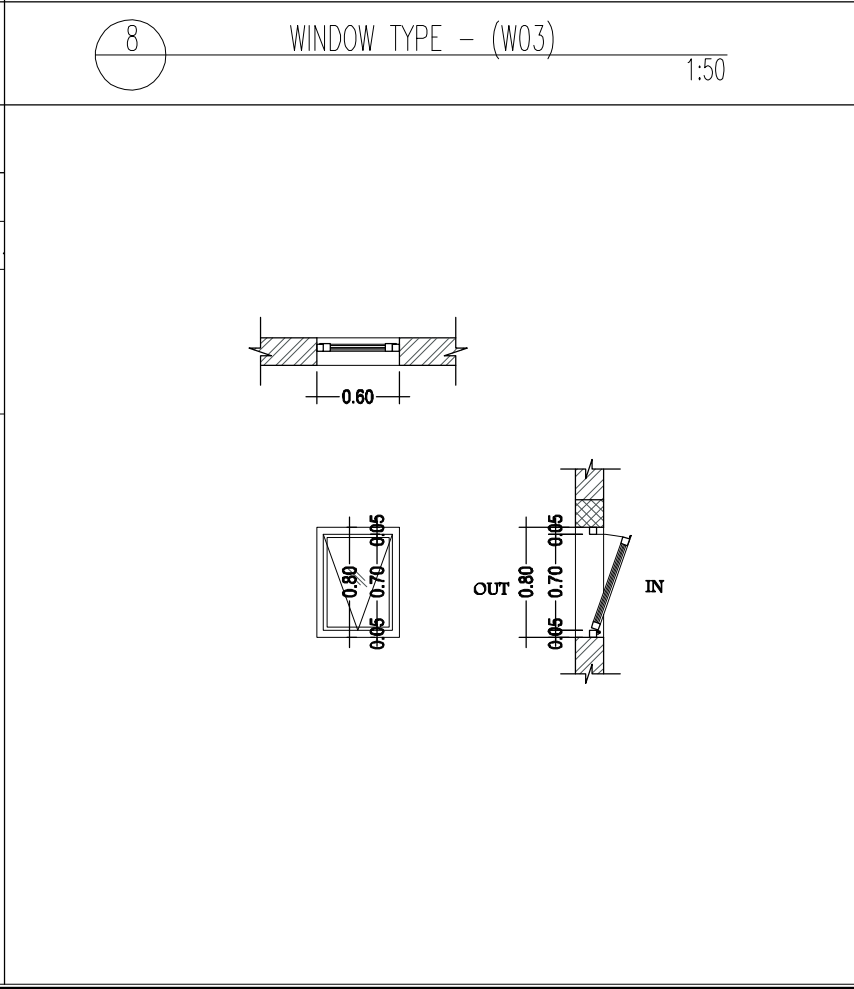1 WOOD DOOR TYPE -D1 1:50  DOOR TYPE D1 2.00m. X 2.20 m. LOCATION: ENTRANCE DESCRIPTION: DOUBLE PANEL WOODEN HINGED DOOR (2.00m. X 2.20 m.) FRAME: 0.05X0.20/0.05X0.10M SOLID MERANTI WOOD FRAME WITH SOLID MERANTI WOOD DECORATIVE ARCHITRAVE ON BOTH SIDES FINISH: POLYURETHANE LACQUER FINISH.	2 WOOD DOOR TYPE -D2 1:50  DOOR TYPE D2 1.40m. X 2.20 m. LOCATION: WOMEN ENTRANCE DESCRIPTION: DOUBLE PANEL WOODEN DOOR (1.40m. X 2.20 m.) FRAME: 0.05X0.20/0.05X0.10M SOLID MERANTI WOOD FRAME WITH SOLID MERANTI WOOD DECORATIVE ARCHITRAVE ON BOTH SIDES FINISH: POLYURETHANE LACQUER FINISH.	3 WOOD DOOR TYPE -D3 1:50  DOOR TYPE D3 1.00m. X 2.20 m. LOCATION: WOMEN ABLUTION MAAZANA DESCRIPTION: DOUBLE PANEL WOODEN DOOR (1.00m. X 2.20 m.) FRAME: 0.05X0.20/0.05X0.10M SOLID MERANTI WOOD FRAME WITH SOLID MERANTI WOOD DECORATIVE ARCHITRAVE ON BOTH SIDES FINISH: POLYURETHANE LACQUER FINISH.
4 WOOD DOOR TYPE -D4 1:50  DOOR TYPE D4 0.80m. X 2.20 m. LOCATION: TOILET OUTER DOOR DESCRIPTION: SINGLE PANEL WOODEN HINGED DOOR (0.80m. X 2.20 m.) FRAME: 0.05X0.20/0.05X0.10M SOLID MERANTI WOOD FRAME WITH SOLID MERANTI WOOD DECORATIVE ARCHITRAVE ON BOTH SIDES FINISH: POLYURETHANE LACQUER FINISH.	5 WOOD DOOR TYPE -D5 1:50  DOOR TYPE D5 0.70m. X 2.20 m. LOCATION: W.C DESCRIPTION: SINGLE PANEL WOODEN HINGED DOOR (0.70m. X 2.20 m.) FRAME: 0.05X0.20/0.05X0.10M SOLID MERANTI WOOD FRAME WITH SOLID MERANTI WOOD DECORATIVE ARCHITRAVE ON BOTH SIDES FINISH: POLYURETHANE LACQUER FINISH.	6 WINDOW TYPE - (W01) 1:50  WINDOW TYPE W1 SIZE: 1.80m. X 1.40 m. LOCATION: WOMEN PRAYER HALL MASJID DESCRIPTION : SLIDING ALUMINUM WINDOW (1.80M X 1.40M) SECTIONS: ALL ALUMINIUM SECTIONS FROM EL GHARER FOR GLAZING WORKS WILL BE DOUBLE GLAZED. INNER PANEL CLEAR FLOAT FINISH : ALL SECTIONS ARE POLYESTER POWDER COATED AT FACTORY
7 WINDOW TYPE - (W02) 1:50  WINDOW TYPE W02 SIZE: 1.00m. X 1.40 m LOCATION: MASJID DESCRIPTION : SLIDING ALUMINUM WINDOW (1.00M X 1.40M) SECTIONS: ALL ALUMINIUM SECTIONS FROM EL GHARER FOR GLAZING WORKS WILL BE DOUBLE GLAZED. INNER PANEL CLEAR FLOAT FINISH : ALL SECTIONS ARE POLYESTER POWDER COATED AT FACTORY	8 WINDOW TYPE - (W03) 1:50  WINDOW TYPE W03 SIZE: 0.80m. X 0.60m. LOCATION: TOILET DESCRIPTION : PIVOTED WINDOW WITH DOUBLE GLAZED (0.80m X 0.60m) SECTIONS: ALL ALUMINIUM SECTIONS FROM EL GHARER FOR GLAZING WORKS WILL BE DOUBLE GLAZED. INNER PANEL CLEAR FLOAT FINISH : ALL SECTIONS ARE POLYESTER POWDER COATED AT FACTORY	

GENERAL NOTES:

1.IT IS NOT ALLOWED TO REPRODUCE THE SHEETS CONTENTS IN ANY FORM EXCEPT FOR THE PURPOSE FOR WHICH IT IS INTENDED.

2. THESE DRAWINGS ARE DIAGRAMMATIC AND SHALL NOT BE SCALED. ADDITIONAL DATA SHALL BE REQUESTED FROM THE CONSULTANCY THROUGH WRITTEN CLARIFICATION. VERIFY ALL EXISTING CONDITIONS AND DIMENSIONS BEFORE PROCEEDING WITH ANY PORTION OF ANY WORK.

3. NO CHANGES, MODIFICATIONS OR DEVIATIONS SHALL BE WRITTEN PERMISSION FROM ALMASAH ENGINEERING CONSULTANTS.

4. ALL WORK AS OUTLINED IN THESE DOCUMENTS, SHALL STRICTLY CONFORM TO ALL APPLICABLE CODES. IN THE EVENT OF A CONFLICT, THE MORE STRINGENT REQUIREMENT SHALL GOVERN AND BE MET.

SIA - SM-03



CONSULTANT STAMP





Sharjah ☎ 06 5 444 521 ☎ 06 5 444 523 📍 Office: 306, Al Fisal 2 Bldg., King Faisal St.

CLIENT:

GOVERNMENT OF SHARJAH -
DEPARTMENT OF ISLAMIC AFFAIRS

PROJECT:







(SIA - SM-03)
PROPOSED MASJID + ABLUTION +
IMAM HOUSE

SHEET TITLE:

MASJID
DOOR & WINDOW DETAILS

ARCHITECT	TYPE	ARCHITECTURE
Arch. Mostafa Ramadan		
STRUCTURAL	SHEET No.	A -14
Eng : Mohamed Gomaa		
CHECKED BY	Location :	
Eng : Mohamed Attia	Plot No :	
SCALE 1:100	DATE February - 2022	Project No. SIA - SM-03

© ALL COPYRIGHTS IS RESERVED

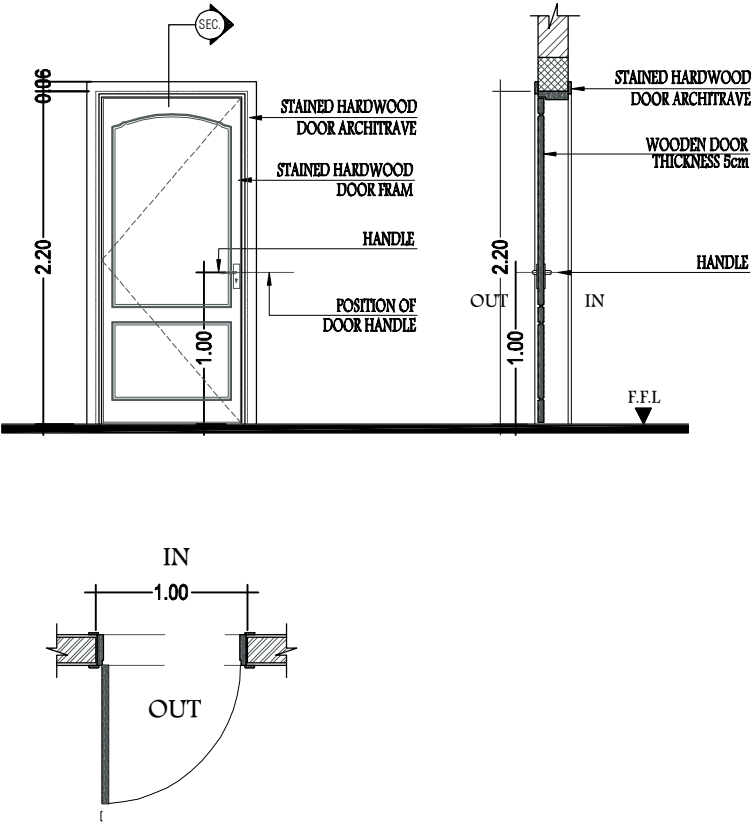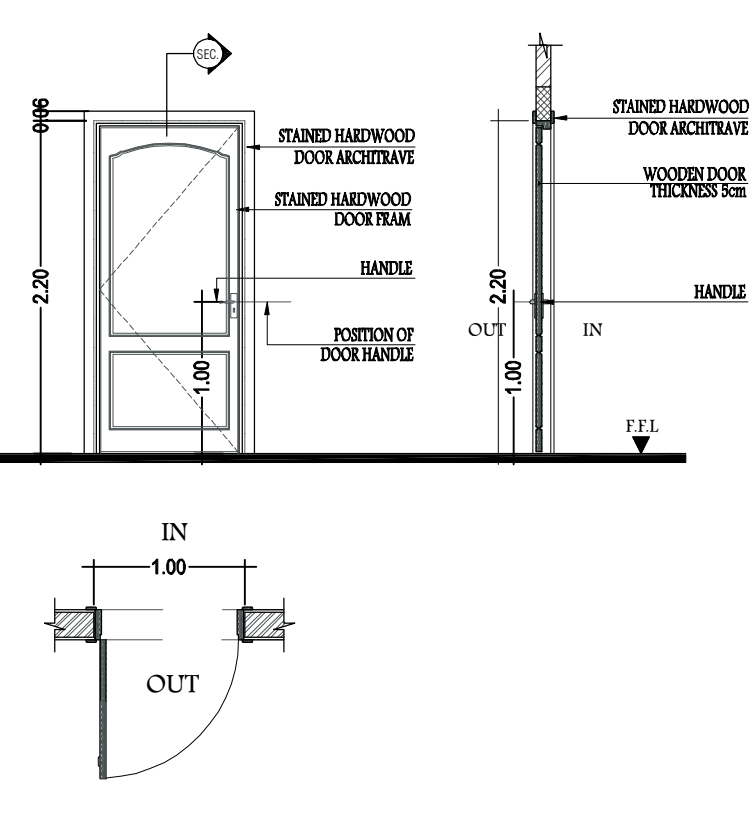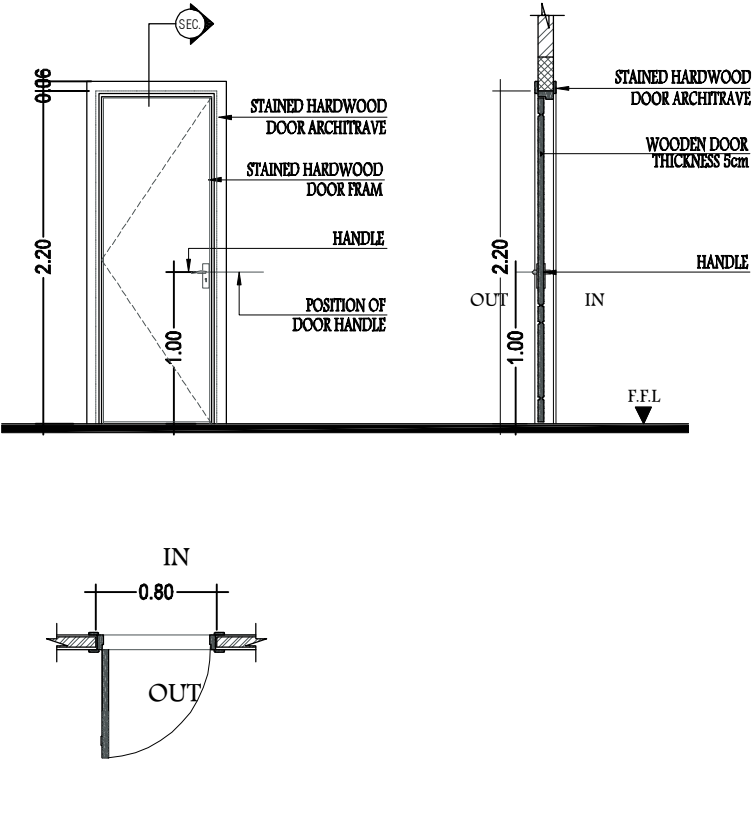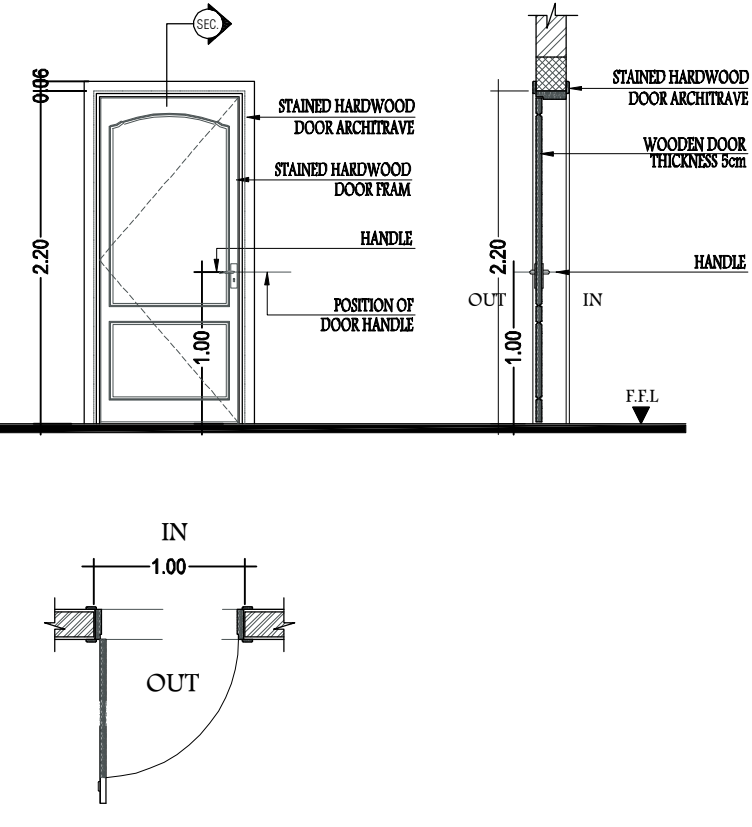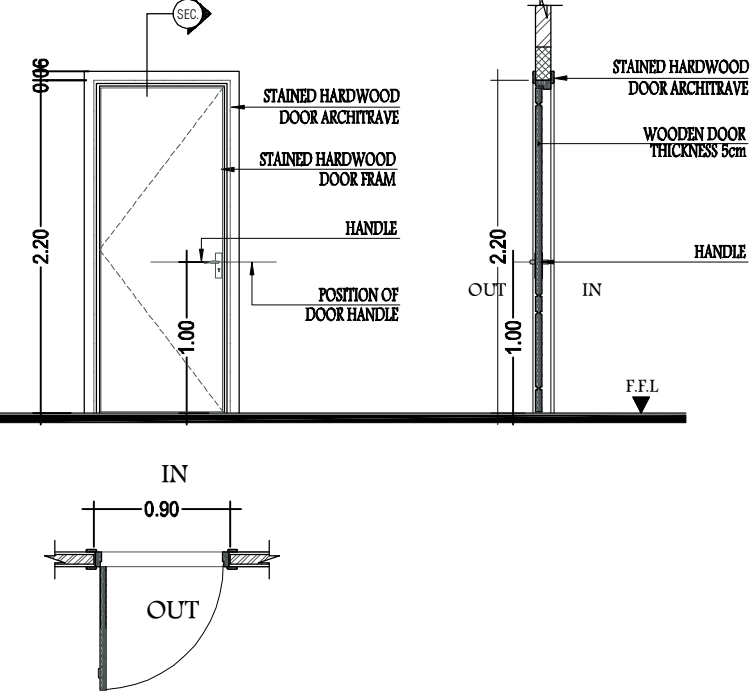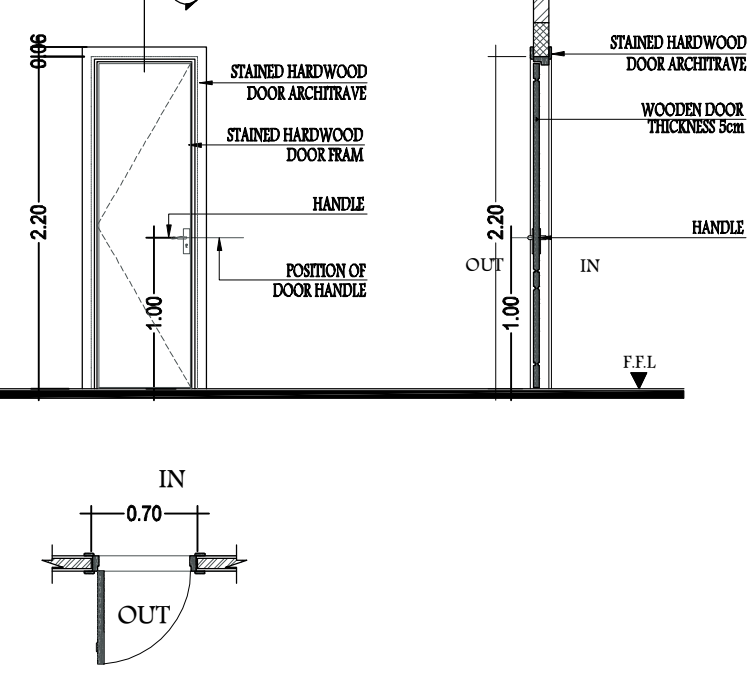1 WOODEN DOOR TYPE -D01 1:50 	DOOR TYPE D12 SIZE: 1.00m. X 2.20 m. LOCATION: ENTRANCE-MAJLIS DESCRIPTION: SINGLE PANEL WOODEN HINGED DOOR (1.00m. X 2.20 m.) FRAME: 0.05X0.20/0.05X0.10M SOLID MERANTI WOOD FRAME WITH SOLID MERANTI WOOD DECORATIVE ARCHITRAVE ON BOTH SIDES FINISH: POLYURETHANE LACQUER FINISH.	2 WOODEN DOOR TYPE -D02 1:50 	DOOR TYPE D12 SIZE: 1.00m. X 2.20 m. LOCATION: BEDROOM-MAJLIS DESCRIPTION: SINGLE PANEL WOODEN HINGED DOOR (1.00m. X 2.20 m.) FRAME: 0.05X0.20/0.05X0.10M SOLID MERANTI WOOD FRAME WITH SOLID MERANTI WOOD DECORATIVE ARCHITRAVE ON BOTH SIDES FINISH: POLYURETHANE LACQUER FINISH.
3 WOODEN DOOR TYPE -D03 1:50 	DOOR TYPE D06 SIZE: 0.70m. X 2.20 m. LOCATION: BATHROOM KITCHEN DESCRIPTION: SINGLE PANEL WOODEN HINGED DOOR (0.70m. X 2.20 m.) FRAME: 0.05X0.20/0.05X0.10M SOLID MERANTI WOOD FRAME WITH SOLID MERANTI WOOD DECORATIVE ARCHITRAVE ON BOTH SIDES FINISH: POLYURETHANE LACQUER FINISH.	4 WOODEN DOOR TYPE -D04 1:50 	DOOR TYPE D12 SIZE: 1.00m. X 2.20 m. LOCATION: W.C MEN'S ABLUTION DESCRIPTION: SINGLE PANEL WOODEN HINGED DOOR (1.00m. X 2.20 m.) FRAME: 0.05X0.20/0.05X0.10M SOLID MERANTI WOOD FRAME WITH SOLID MERANTI WOOD DECORATIVE ARCHITRAVE ON BOTH SIDES FINISH: POLYURETHANE LACQUER FINISH.
5 WOODEN DOOR TYPE -D05 1:50 	DOOR TYPE D06 SIZE: 0.90m. X 2.20 m. LOCATION: HANDICAPPED TOILET DESCRIPTION: SINGLE PANEL WOODEN HINGED DOOR (0.90m. X 2.20 m.) FRAME: 0.05X0.20/0.05X0.10M SOLID MERANTI WOOD FRAME WITH SOLID MERANTI WOOD DECORATIVE ARCHITRAVE ON BOTH SIDES FINISH: POLYURETHANE LACQUER FINISH.	6 WOODEN DOOR TYPE -D06 1:50 	DOOR TYPE D06 SIZE: 0.70m. X 2.20 m. LOCATION: TOILETS PARTITION DESCRIPTION: SINGLE PANEL WOODEN HINGED DOOR (0.70m. X 2.20 m.) FRAME: 0.05X0.20/0.05X0.10M SOLID MERANTI WOOD FRAME WITH SOLID MERANTI WOOD DECORATIVE ARCHITRAVE ON BOTH SIDES FINISH: POLYURETHANE LACQUER FINISH.

GENERAL NOTES:

1.IT IS NOT ALLOWED TO REPRODUCE THE SHEETS CONTENTS IN ANY FORM EXCEPT FOR THE PURPOSE FOR WHICH IT IS INTENDED.

2. THESE DRAWINGS ARE DIAGRAMMATIC AND SHALL NOT BE SCALED. ADDITIONAL DATA SHALL BE REQUESTED FROM THE CONSULTANCY THROUGH WRITTEN CLARIFICATION. VERIFY ALL EXISTING CONDITIONS AND DIMENSIONS BEFORE PROCEEDING WITH ANY PORTION OF ANY WORK.

3. NO CHANGES, MODIFICATIONS OR DEVIATIONS SHALL BE WRITTEN PERMISSION FROM ALMASAH ENGINEERING CONSULTANTS.

4. ALL WORK AS OUTLINED IN THESE DOCUMENTS, SHALL STRICTLY CONFORM TO ALL APPLICABLE CODES. IN THE EVENT OF A CONFLICT, THE MORE STRINGENT REQUIREMENT SHALL GOVERN AND BE MET.

SIA - SM-03



CONSULTANT STAMP





Sharjah 06 5 444 521 06 5 444 523 Office: 306, Al Fisal 2 Bldg., King Fisal St.

CLIENT:

GOVERNMENT OF SHARJAH -
DEPARTMENT OF ISLAMIC AFFAIRS

PROJECT:




(SIA - SM-03)
PROPOSED MASJID + ABLUTION +
IMAM HOUSE

SHEET TITLE:

IMAM & ABLUTION
DOOR & WINDOW DETAILS -1

ARCHITECT	TYPE	ARCHITECTURE
Arch. Mostafa Ramadan		
STRUCTURAL	SHEET	A -15
Eng : Mohamed Gomaa	No.	
CHECKED BY	Location :	
Eng : Mohamed Attia	Plot No :	
SCALE	DATE	Project
1:100	February - 2022	No. SIA - SM-03

© ALL COPYRIGHTS IS RESERVED

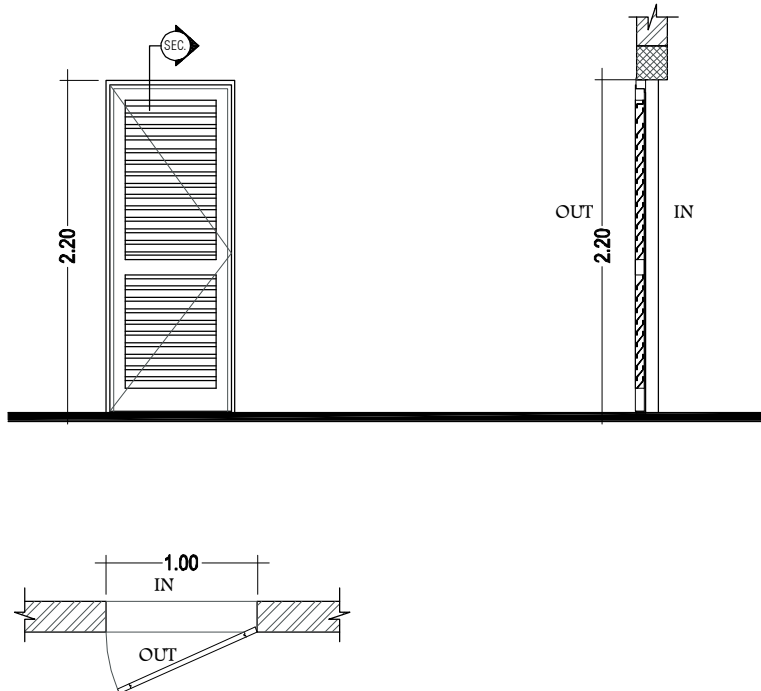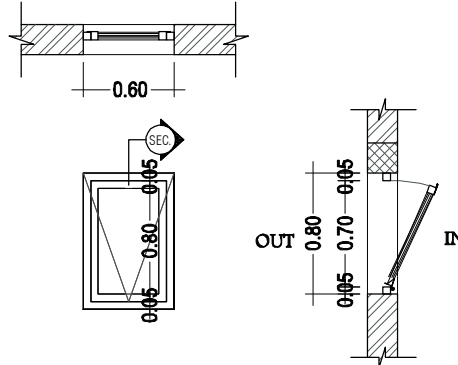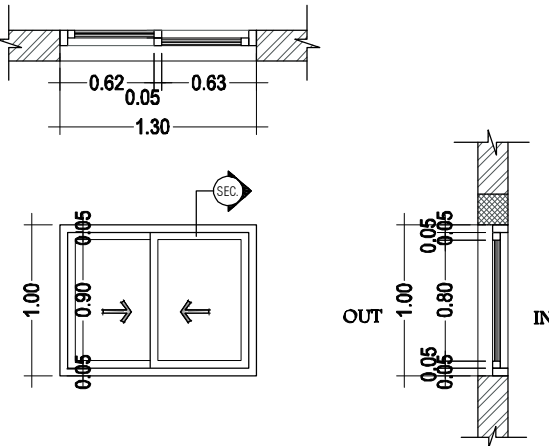7ALUMINUM DOOR TYPE -D071:50		8WINDOW TYPE -W011:50	
			
	DOOR TYPE D07		WINDOW TYPE W01
	SIZE: 1.00 m. X 2.20 m.		SIZE: 1.20 m. X 1.20 m.
	LOCATION: PUMB & ELEC. ROOM		LOCATION: BEDROOM MAJLIS KITCHEN
	DESCRIPTION : ALL ALUMINIUM SECTIONS WILL BE FROM EL GHARER FRAME: ALL SECTIONS WILL BE POLYESTER POWDER COATED AT FACTORY BY ELECTRO STATIC SPRAYING TO A MINIMUM THICKNESS OF 60 MICRONS FINISH: THE DOOR WILL BE ACCORDING TO CIVIL DEFENCE SPECIFICATION		DESCRIPTION : SLIDING ALUMINUM WINDOW (1.20M X 1.20M) SECTIONS: ALL ALUMINIUM SECTIONS WILL BE FROM EL GHARER FOR GLAZING WORKS WILL BE DOUBLE GLAZED. INNER PANEL CLEAR FLOAT FINISH : ALL SECTIONS WILL BE POLYESTER POWDER COATED AT FACTORY
9WINDOW TYPE -W021:50		10WINDOW TYPE -W031:50	
			
	WINDOW TYPE W03		WINDOW TYPE W01
	SIZE: 0.60 m. X 0.80 m.		SIZE: 1.50 m. X 1.00 m.
	LOCATION: BATHROOM		LOCATION: TOILET
	DESCRIPTION : PIVOTED WINDOW WITH DOUBLE GLAZED (0.60m X 0.80m) SECTIONS: ALL ALUMINIUM SECTIONS WILL BE FROM EL GHARER FOR GLAZING WORKS WILL BE DOUBLE GLAZED. INNER PANEL CLEAR FLOAT FINISH : ALL SECTIONS WILL BE POLYESTER POWDER COATED AT FACTORY		DESCRIPTION : SLIDING ALUMINUM WINDOW (1.50M X 1.00M) SECTIONS: ALL ALUMINIUM SECTIONS WILL BE FROM EL GHARER FOR GLAZING WORKS WILL BE DOUBLE GLAZED. INNER PANEL CLEAR FLOAT FINISH : ALL SECTIONS WILL BE POLYESTER POWDER COATED AT FACTORY
11WINDOW TYPE -W041:50			
			
	WINDOW TYPE W01		
	SIZE: 1.30 m. X 1.00 m.		
	LOCATION: ABLUTION		
	DESCRIPTION : SLIDING ALUMINUM WINDOW (1.30M X 1.00M) SECTIONS: ALL ALUMINIUM SECTIONS WILL BE FROM EL GHARER FOR GLAZING WORKS WILL BE DOUBLE GLAZED. INNER PANEL CLEAR FLOAT FINISH : ALL SECTIONS WILL BE POLYESTER POWDER COATED AT FACTORY		

GENERAL NOTES:
1.IT IS NOT ALLOWED TO REPRODUCE THE SHEETS CONTENTS IN ANY FORM EXCEPT FOR THE PURPOSE FOR WHICH IT IS INTENDED.
2. THESE DRAWINGS ARE DIAGRAMMATIC AND SHALL NOT BE SCALED. ADDITIONAL DATA SHALL BE REQUESTED FROM THE CONSULTANCY THROUGH WRITTEN CLARIFICATION. VERIFY ALL EXISTING CONDITIONS AND DIMENSIONS BEFORE PROCEEDING WITH ANY PORTION OF ANY WORK.
3. NO CHANGES, MODIFICATIONS OR DEVIATIONS SHALL BE WRITTEN PERMISSION FROM **ALMASAH ENGINEERING CONSULTANTS**.
4. ALL WORK AS OUTLINED IN THESE DOCUMENTS, SHALL STRICTLY CONFORM TO ALL APPLICABLE CODES. IN THE EVENT OF A CONFLICT, THE MORE STRINGENT REQUIREMENT SHALL GOVERN AND BE MET.


SIA - SM-03



حُكُومَةُ الشَّارِقَة
دائرة الشؤون الإسلامية

CONSULTANT STAMP



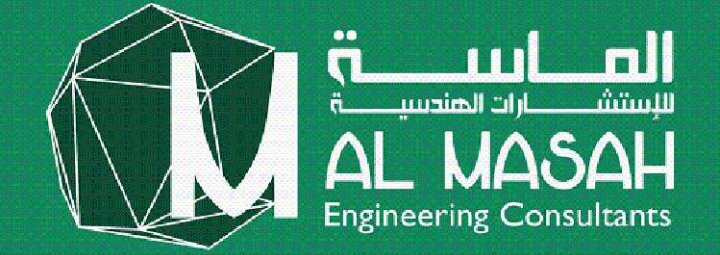

Sharjah 06 5 444 521 06 5 444 523 Office: 306, Al Fisal 2 Bldg., King Faisal St.


CLIENT:
**GOVERNMENT OF SHARJAH -
DEPARTMENT OF ISLAMIC AFFAIRS**

PROJECT:
**(SIA - SM-03)
PROPOSED MASJID + ABLUTION +
IMAM HOUSE**


SHEET TITLE:
**IMAM & ABLUTION
DOOR & WINDOW DETAILS -2**

ARCHITECT Arch. Mostafa Ramadan	TYPE	ARCHITECTURE
STRUCTURAL Eng : Mohamed Gomaa	SHEET No.	A -16
CHECKED BY Eng : Mohamed Attia	Location :	
SCALE 1:100	DATE February - 2022	Plot No :
	Project No.	SIA - SM-03

© ALL COPYRIGHTS IS RESERVED

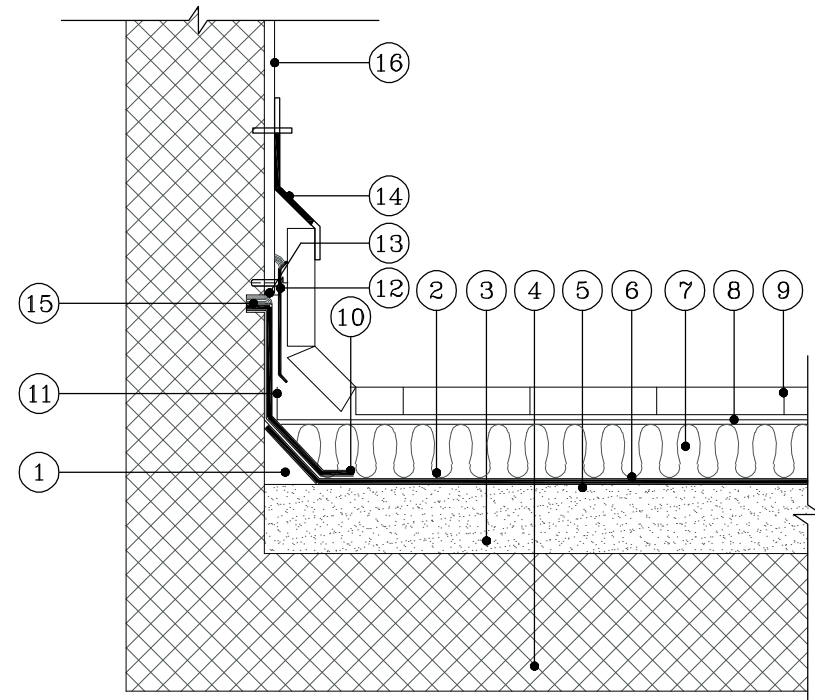


- ① ANGLE FILLET AT CORNERS
- ② SKIRTING MEMBRANE STARTED FROM 150MM FROM HORIZONTAL MEMBRANE
- ③ ROOF SLAB
- ④ LIGHT WEIGHT FOAM CONCRETE TO SLOPE MIN 50 MM @ OUTLET AND AVG 100MM THICK
- ⑤ BITUMINOUS PRIMER
- ⑥ COMPOSITE 4MM THICK W/P MEMBRANE TORCHWELDED WITH 10CMS SIDE 15& CMS END LAPS
- ⑦ 50MM THICK EXTRUDED. POLYSTYRENE BOARD DENSITY 35KG|M , 2LOOSE LAID
- ⑧ GEOTEXTILE FILTER LAYER
- ⑨ 300X300X40 MOSAIC TILES.
- ⑩ SKIRTING MEMBRANE
- ⑪ FILTER LAYER EXTENDED TO PROTECT MEMBRANE FROM GRAVEL
- ⑫ 1MM THICK POWDER COATED ALUMINIUM FLASHING, FIXED WITH FISHER NAILS AND TOPPED WITH SUPERFLEX - POLYURETHANE SEALANT
- ⑬ PLASTER STOPPER
- ⑭ 1mm THICK ALUMINUM FLASHING
- ⑮ WATERPROOF PLASTER
- ⑯ 20x 20GROOVE FOR MEMBRANE TERMINATION AND FILLED WITH MASTIC SEALANT CUT AT 350MM ABOVE CONCRETE DECK SLAB

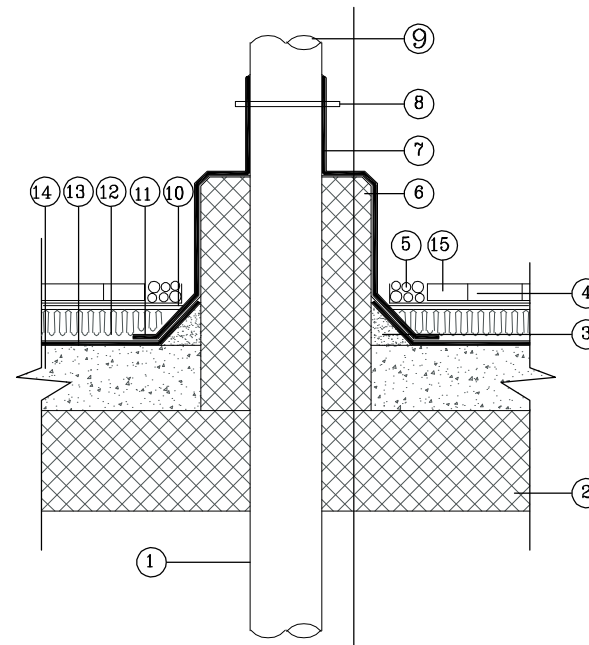

- ① PIPE PENETRATION
- ② ROOF SLAB
- ③ 50x50 ANGLE FILLET
- ④ ROOF CONT'N AS BEFORE
- ⑤ GRAVEL FILLING AT CORNER
- ⑥ CONCRETE PACKING AROUND PIPE
- ⑦ FOR EXPOSED APPLICATION AS FLASHING MEMBRANE COVERING THE CONCRETE UPSTAND
- ⑧ CLIP
- ⑨ SEALANT TO COVER THE OPENING
- ⑩ SEPERATION LAYER
- ⑪ ONE LAYER COMPOSITE 4MM THICK W/P MEMBRANE
- ⑫ 50MM THICK POLYSTYRENE 35.00, KG/M 3DENSITY BOARDS LOOSE LAID
- ⑬ PRIMER
- ⑭ LIGHT WEIGHT FOAMCONCRETE TO SLOPE
- ⑮ MARBLE MOSAIC TILES LOOSELY LAID


TYPICAL WATERPROOFING DETAILS AT SOUTH PARAPET

TYPICAL WATER PROOFING DETAILS FOR PIPE PENETRATION

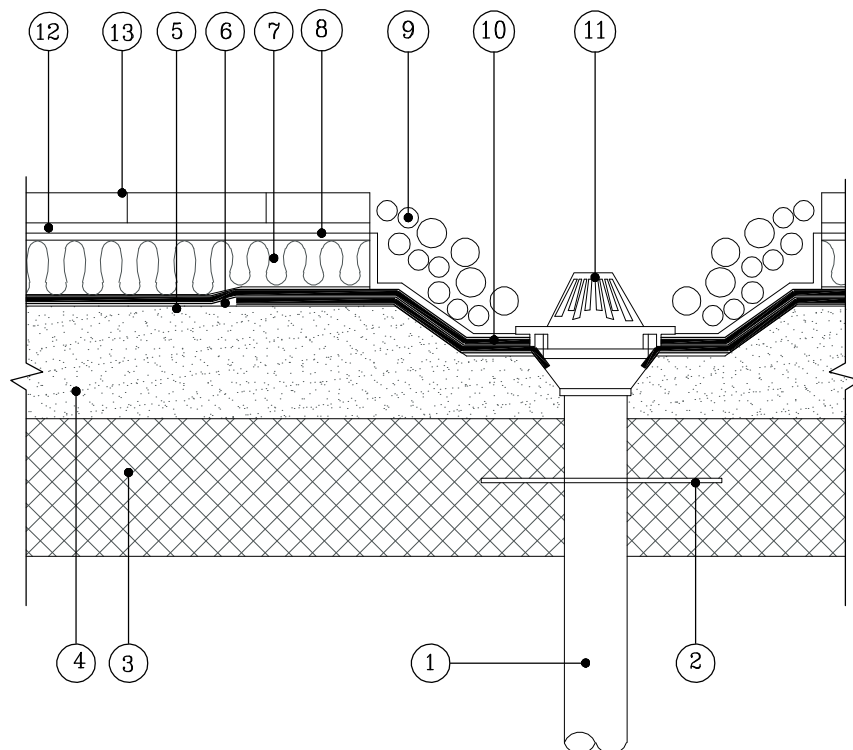


- ① PVC PIPE
- ② PUDDLE FLANGE
- ③ ROOF SLAB
- ④ LIGHT WEIGHT FOAM CONCRETE TO SLOPE MIN 50 MM @ OUTLET AND AVG 100MM THICK
- ⑤ BITUMINOUS PRIMER
- ⑥ 4MM THICK W/P MEMBRANE
- ⑦ 50MM THICK EXTRUDED POLYSTYRENE BOARD DENSITY 35KG|M2
- ⑧ GEOTEXTILE FILTER LAYER
- ⑨ GRAVEL AROUND OUTLET FOR MINIMUM 350mm WIDE
- ⑩ ADDITIONAL MEMBRANE STRIP DRESSED INTO THE OUTLET
- ⑪ RAIN OUTLET AS PER SPEC'S
- ⑫ FILTER LAYER EXTENDED TO PROTECT MEMBRANE
- ⑬ MARBLE MOSAIC TILE.

TYPICAL RAIN WATER OUTLET DRESSING DETAILS

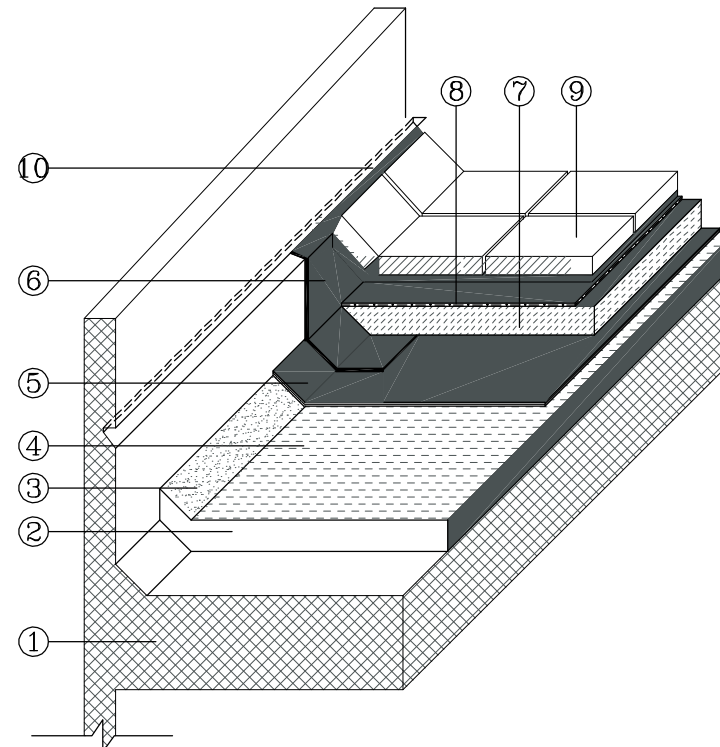


- ① RCC. SLAB
- ② 7.5cm THERMAL INSULATION LAYER
- ③ ANGLE FILLET, SAND, CEMENT
- ④ COLD PRIMER
- ⑤ 4mm MEMBRANE "ISOFLEX 200" HP.
- ⑥ 4mm MEMBRANE " ISOFLEX " SKIRTING 200 HP.
- ⑦ HEAT INSULATION BOARD
- ⑧ FILTER " EDILFON " 150gm/sq.M.
- ⑨ 30x30cm. SIKKA TILES ON MORTAR BED IN MAXI 3. x3m. BAYS WITH AND INCLUDING THE MOVEMENT JOINTS COMPRISING.
- ⑩ 1"x1" GROOVE WITH MASTIC SEALANT

TYPICAL ROOF WATERPROOFING & INSULATION DETAIL WITH GROOVE SYSTEM

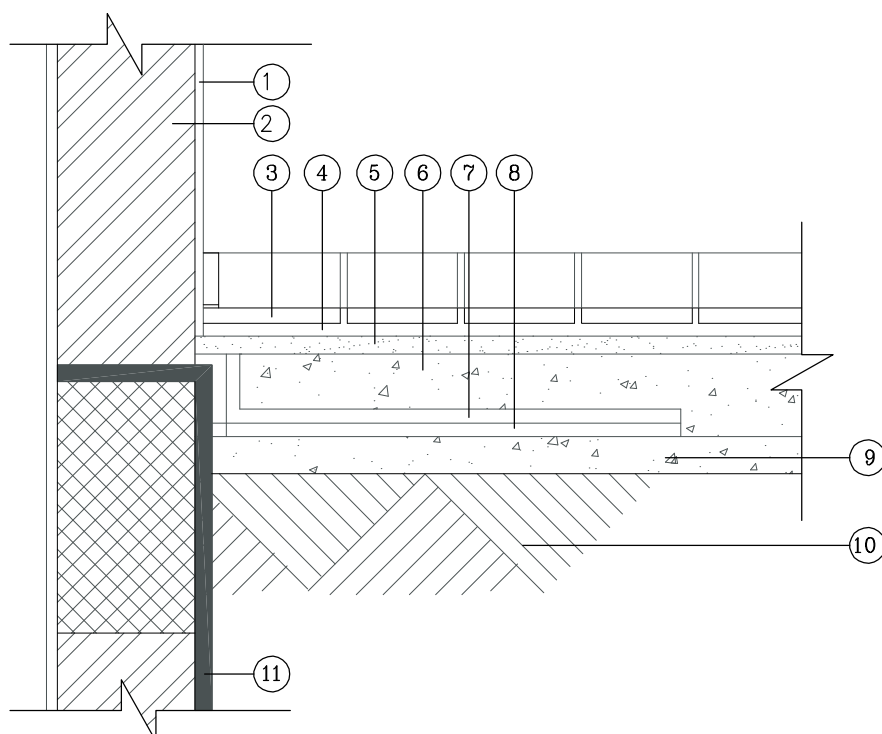

- ① 1.5cm PLASTER
- ② 20cm THK BLOCK WALL(THERMALITE BLOCK OR APPROVED THERMAL BLOCK)
- ③ FINISHING FLOOR TILES
- ④ MORTAR SCREED AND SAND
- ⑤ FLOORING CONCRETE 10cm
- ⑥ B.R.C. A-252 OR A-142 (MESH)
- ⑦ 1000 .G. POLYTHENE SHEET
- ⑧ ANTI TERMITE TREATMENT
- ⑨ COMPACTED (20cm ROAD BASE)
- ⑩ COMPACTED EARTH FILLING
- ⑪ WATERPROOF LAYER

GROUND FLOOR DETIALS

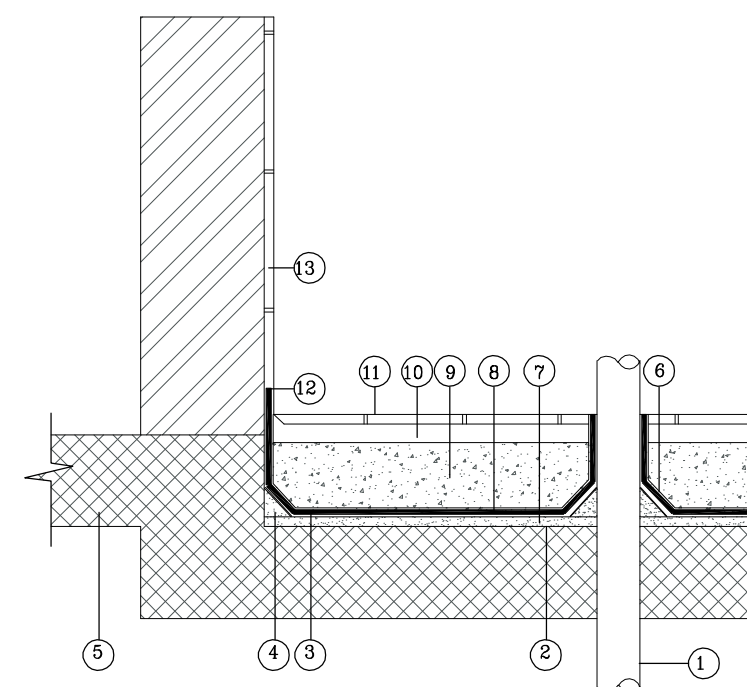

- ① DRAIN PIPE
- ② SLAB SURFACE SMOOTH FINISHED
- ③ ROOFAB
- ④ 50X50 mm CEMENT SAND ANGLE FILLET
- ⑤ CONCRETE SLAB
- ⑥ POLYESTER REINFORCEMENT AROUND PIPE B/N TWO COAT
- ⑦ TWO COATS 1.5(MM THK) OF ROOFTEX COLD APPLIED POLYURETHENE WATERPROOFING MEMBRANE
- ⑧ POLYETHENE PROTECTION LAYER
- ⑨ PROTECTION SCREED/ MORTAR FILLING IF REQ.
- ⑩ BEDDING MORTAR AS SPECIFIED
- ⑪ CERAMIC FLOOR TILES AS SPECIFIED
- ⑫ ROOFTEX COATING EXTENDED MINIMUM 50MM HIGH ABOVE F.F.L.
- ⑬ CERAMIC WALL TILES AS SPECIFIED

TYPICAL WATERPROOFING DETAILS TO TOILETS, UTILITIES AND OTHER INTERNAL WET AREAS

GENERAL NOTES:

- 1.IT IS NOT ALLOWED TO REPRODUCE THE SHEETS CONTENTS IN ANY FORM EXCEPT FOR THE PURPOSE FOR WHICH IT IS INTENDED.
2. THESE DRAWINGS ARE DIAGRAMMATIC AND SHALL NOT BE SCALED. ADDITIONAL DATA SHALL BE REQUESTED FROM THE CONSULTANCY THROUGH WRITTEN CLARIFICATION. VERIFY ALL EXISTING CONDITIONS AND DIMENSIONS BEFORE PROCEEDING WITH ANY PORTION OF ANY WORK.
3. NO CHANGES, MODIFICATIONS OR DEVIATIONS SHALL BE WRITTEN PERMISSION FROM ALMASAH ENGINEERING CONSULTANTS.
4. ALL WORK AS OUTLINED IN THESE DOCUMENTS, SHALL STRICTLY CONFORM TO ALL APPLICABLE CODES. IN THE EVENT OF A CONFLICT, THE MORE STRINGENT REQUIREMENT SHALL GOVERN AND BE MET.

SIA - SM-03



حُكُومَةُ الشَّارِقَةِ
دائرة الشؤون الإسلامية

CONSULTANT STAMP



CLIENT:

GOVERNMENT OF SHARJAH -
DEPARTMENT OF ISLAMIC AFFAIRS

PROJECT:

(SIA - SM-03)
PROPOSED MASJID + ABLUTION +
IMAM HOUSE

SHEET TITLE:

MASJID, IMAM & ABLUTION
GENERAL DETAILS

ARCHITECT Arch. Mostafa Ramadan	TYPE ARCHITECTURE
STRUCTURAL Eng : Mohamed Gomaa	SHEET No. A -17
CHECKED BY Eng : Mohamed Attia	Location : Plot No :
SCALE 1:100	DATE February - 2022
Project No.	SIA - SM-03

	LOCATION	FLOOR												WALLS														CEILING					REMARKS
MASJID		30X60X2 CM THICK NATURAL MARBLE WITH 10 CM HIGH SIMILAR SKIRTING.	30X60X2 CM THICK NATURAL GRANITE WITH 10 CM HIGH SIMILAR SKIRTING TO APPROVAL.	20X20X2 CM THICK MARBLE MOSAIC TILES WITH 7.5 CM HIGH CERAMIC TILES SKIRTING TO APPROVAL.	NON-SLIP CERAMIC TILES TO APPROVAL	SMOOTH SCREED FINISH TO APPROVAL.	FLOOR HARDENER OVER P.C.C TO APPROVAL	3 CM THICK MARBLE/ GRANITE TREADS&2 CM THICK SIMILAR RISER WITH APPROVED NON SLIP NOSING.	MARBLE MOSAIC (5 CM TREADS&2 CM RISER) TO APPROVAL WITH APPROVED NON SLIP NOSING.	MEDIUM DUTY 30X30X3 CM PRECAST CONC. PAVING TILES LAID TO SLOP AS DIRECTED.	MEDIUM DUTY INTERLOCK PAVING 6.0 CM IN TWO COLOURS ON COMPACTED SAND BASE LAID TO SLOPE.	P.V.C TILES TO APPROVAL	PARQUET FLOORING TILES TO APPROVAL	4 COATS OF ACRYLIC BASED EXTERNAL TYPE PAINT MULTITILE OR EQUIVALENT TO APPROVAL.	4 COATS OF EPOXY BASED EXTERNAL TYPE PAINT MULTITILE OR EQUIVALENT TO APPROVAL	3 COATS OF EMULSION PAINT (VINYL SILK)	JORDANIAN STONE CLADDING TO APPROVAL.	MARBLE CLADDING TO APPROVAL.	GRANITE CLADDING TO APPROVAL.	TYROLEAN (WHITE)	GLAZED CERAMIC TILES TO APPROVAL (UP TO FULL HT. OR 10 CMS ABOVE FALSE CEILING LEVEL.	DECORATIVE PRECAST CONC. BALUSTRADING FINISHED WITH SMOOTH EPOXY PAINT TO APPROVAL.	DECORATIVE TEAK WOOD/RED MERANTI BALUSTRADING TO APPROVAL FOR STAIRCASE	COLOURED POWDER COATED ALUMINIUM RAILING TO APPROVAL	DECORATIVE CAST ALUMINIUM RAILING TO APPROVAL	COLOURED POWDER COATED ALUMINIUM RAILING WITH TOUGHENED GLASS TO APPROVAL.	NON TOXIC EPOXY PAINT TO APPROVAL.	3 COATS OF EMULSION PAINT (VINYL SILK) TO APPROVAL.	3 COATS OF EXTERNAL TYPE EMULSION PAINT (FENOTEX OR EQUIVALENT) TO APPROVAL.	DECORATIVE GYPSUM BOARD FALSE CEILING TO APPROVAL (PAINT FINISH)	PROPRIETARY MAKE EXPOSED GRID SYSTEM(60X60 CM) SUSPENDED FALSE CEILING MOISTURE PROOF AIR TIGHT WITH ACCESS PANEL AT MIN. 8' HT. IN BATHS.	CONCEALED GRID SYSTEM (60X60 CM) SUSPENDED FALSE CEILING, MOISTURE PROOF AIR TIGHT WITH ACCESS PANEL.	
REF-No		F1	F2	F3	F4	F5	F6	F7	F8	F9	F10	F11	F12	W1	W2	W3	W4	W5	W6	W7	W8	W9	W10	W11	W12	W13	W14	C1	C2	C3	C4	C5	
GROUND FLOOR PLAN																																	
G-1	MAIN ENTRANCE		●															●												●			
G-2	MASJID	●														●		●										●					
G-3	WOMEN PRAYER HALL	●														●		●										●					
G-4	TOILETS				●																●									●			
G-5	WOMEN ABLUTION				●																●									●			
G-6	OUTER CORRIDOR	●														●																	
ROOF FLOOR																																	
R-1										●																							
R-2										●																							
R-3										●																							

- GENERAL NOTES:**
- 1.IT IS NOT ALLOWED TO REPRODUCE THE SHEETS CONTENTS IN ANY FORM EXCEPT FOR THE PURPOSE FOR WHICH IT IS INTENDED.
 2. THESE DRAWINGS ARE DIAGRAMMATIC AND SHALL NOT BE SCALED. ADDITIONAL DATA SHALL BE REQUESTED FROM THE CONSULTANCY THROUGH WRITTEN CLARIFICATION. VERIFY ALL EXISTING CONDITIONS AND DIMENSIONS BEFORE PROCEEDING WITH ANY PORTION OF ANY WORK.
 3. NO CHANGES, MODIFICATIONS OR DEVIATIONS SHALL BE WRITTEN PERMISSION FROM **ALMASAH ENGINEERING CONSULTANTS**.
 4. ALL WORK AS OUTLINED IN THESE DOCUMENTS, SHALL STRICTLY CONFORM TO ALL APPLICABLE CODES. IN THE EVENT OF A CONFLICT, THE MORE STRINGENT REQUIREMENT SHALL GOVERN AND BE MET.

SIA - SM-03



حُكُومَةُ الشَّارِقَةِ
دائرة الشؤون الإسلامية

CONSULTANT STAMP





Sharjah ☎ 06 5 444 521 ☎ 06 5 444 523 📍 Office: 306, Al Fisal 2 Bldg., King Fisal St.

CLIENT: **GOVERNMENT OF SHARJAH - DEPARTMENT OF ISLAMIC AFFAIRS**

PROJECT: **(SIA - SM-03)
PROPOSED MASJID + ABLUTION + IMAM HOUSE**

SHEET TITLE: **MASJID
FINISHING MATERIALS**

ARCHITECT Arch. Mostafa Ramadan	TYPE	ARCHITECTURE
STRUCTURAL Eng : Mohamed Gomaa	SHEET No.	A -18
CHECKED BY Eng : Mohamed Attia	Location :	
	Plot No :	
SCALE 1:100	DATE February - 2022	Project No. SIA - SM-03


	LOCATION	FLOOR												WALLS												CEILING					REMARKS				
IMAM HOUSE																																			
	REF-No		F1	F2	F3	F4	F5	F6	F7	F8	F9	F10	F11	F12	W1	W2	W3	W4	W5	W6	W7	W8	W9	W10	W11	W12	W13	W14	C1	C2	C3	C4	C5		
	GROUND FLOOR																																		
	G-1	ENTRANCE	●												●																●				
	G-2	HALL	●												●																●				
	G-3	MAJLIS	●												●																●				
	G-4	BEDROOM				●									●																●				
	G-5	BEDROOM				●									●																●				
	G-6	TOILET				●																●										●			
	G-7	BATHROOM				●																●										●			
	G-8	KITCHEN				●																●										●			
	ROOF FLOOR																																		
	R-1	ROOF									●																								
		LOCATION	FLOOR												WALLS												CEILING					REMARKS			
ABLUTION																																			
	REF-No		F1	F2	F3	F4	F5	F6	F7	F8	F9	F10	F11	F12	W1	W2	W3	W4	W5	W6	W7	W8	W9	W10	W11	W12	W13	W14	C1	C2	C3	C4	C5		
	GROUND FLOOR																																		
	G-1	ENTRANCE	●												●																	●			
	G-2	MEN ABLUTION				●																●										●			
	G-3	TOILET				●																●										●			
	G-4	PUMP. ROOM				●											●												●						
	G-5	ELEC. ROOM				●											●												●						
	ROOF FLOOR																																		
	R-1	ROOF									●																								

- GENERAL NOTES:**
- 1.IT IS NOT ALLOWED TO REPRODUCE THE SHEETS CONTENTS IN ANY FORM EXCEPT FOR THE PURPOSE FOR WHICH IT IS INTENDED.
 2. THESE DRAWINGS ARE DIAGRAMMATIC AND SHALL NOT BE SCALED. ADDITIONAL DATA SHALL BE REQUESTED FROM THE CONSULTANCY THROUGH WRITTEN CLARIFICATION. VERIFY ALL EXISTING CONDITIONS AND DIMENSIONS BEFORE PROCEEDING WITH ANY PORTION OF ANY WORK.
 3. NO CHANGES, MODIFICATIONS OR DEVIATIONS SHALL BE WRITTEN PERMISSION FROM **ALMASAH ENGINEERING CONSULTANTS**.
 4. ALL WORK AS OUTLINED IN THESE DOCUMENTS, SHALL STRICTLY CONFORM TO ALL APPLICABLE CODES. IN THE EVENT OF A CONFLICT, THE MORE STRINGENT REQUIREMENT SHALL GOVERN AND BE MET.

SIA - SM-03



CONSULTANT STAMP

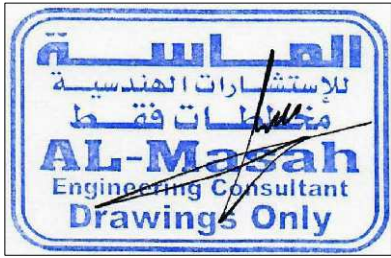

CLIENT: **GOVERNMENT OF SHARJAH - DEPARTMENT OF ISLAMIC AFFAIRS**

PROJECT: **(SIA - SM-03) PROPOSED MASJID + ABLUTION + IMAM HOUSE**

SHEET TITLE: **IMAM & ABLUTION FINISHING MATERIALS**

ARCHITECT Arch. Mostafa Ramadan	TYPE	ARCHITECTURE
------------------------------------	------	--------------

STRUCTURAL Eng : Mohamed Gomaa	SHEET No.	A -19
-----------------------------------	-----------	-------

CHECKED BY Eng : Mohamed Attia	Location :	
	Plot No :	

SCALE 1:100	DATE February - 2022	Project No.	SIA - SM-03
----------------	-------------------------	-------------	-------------