



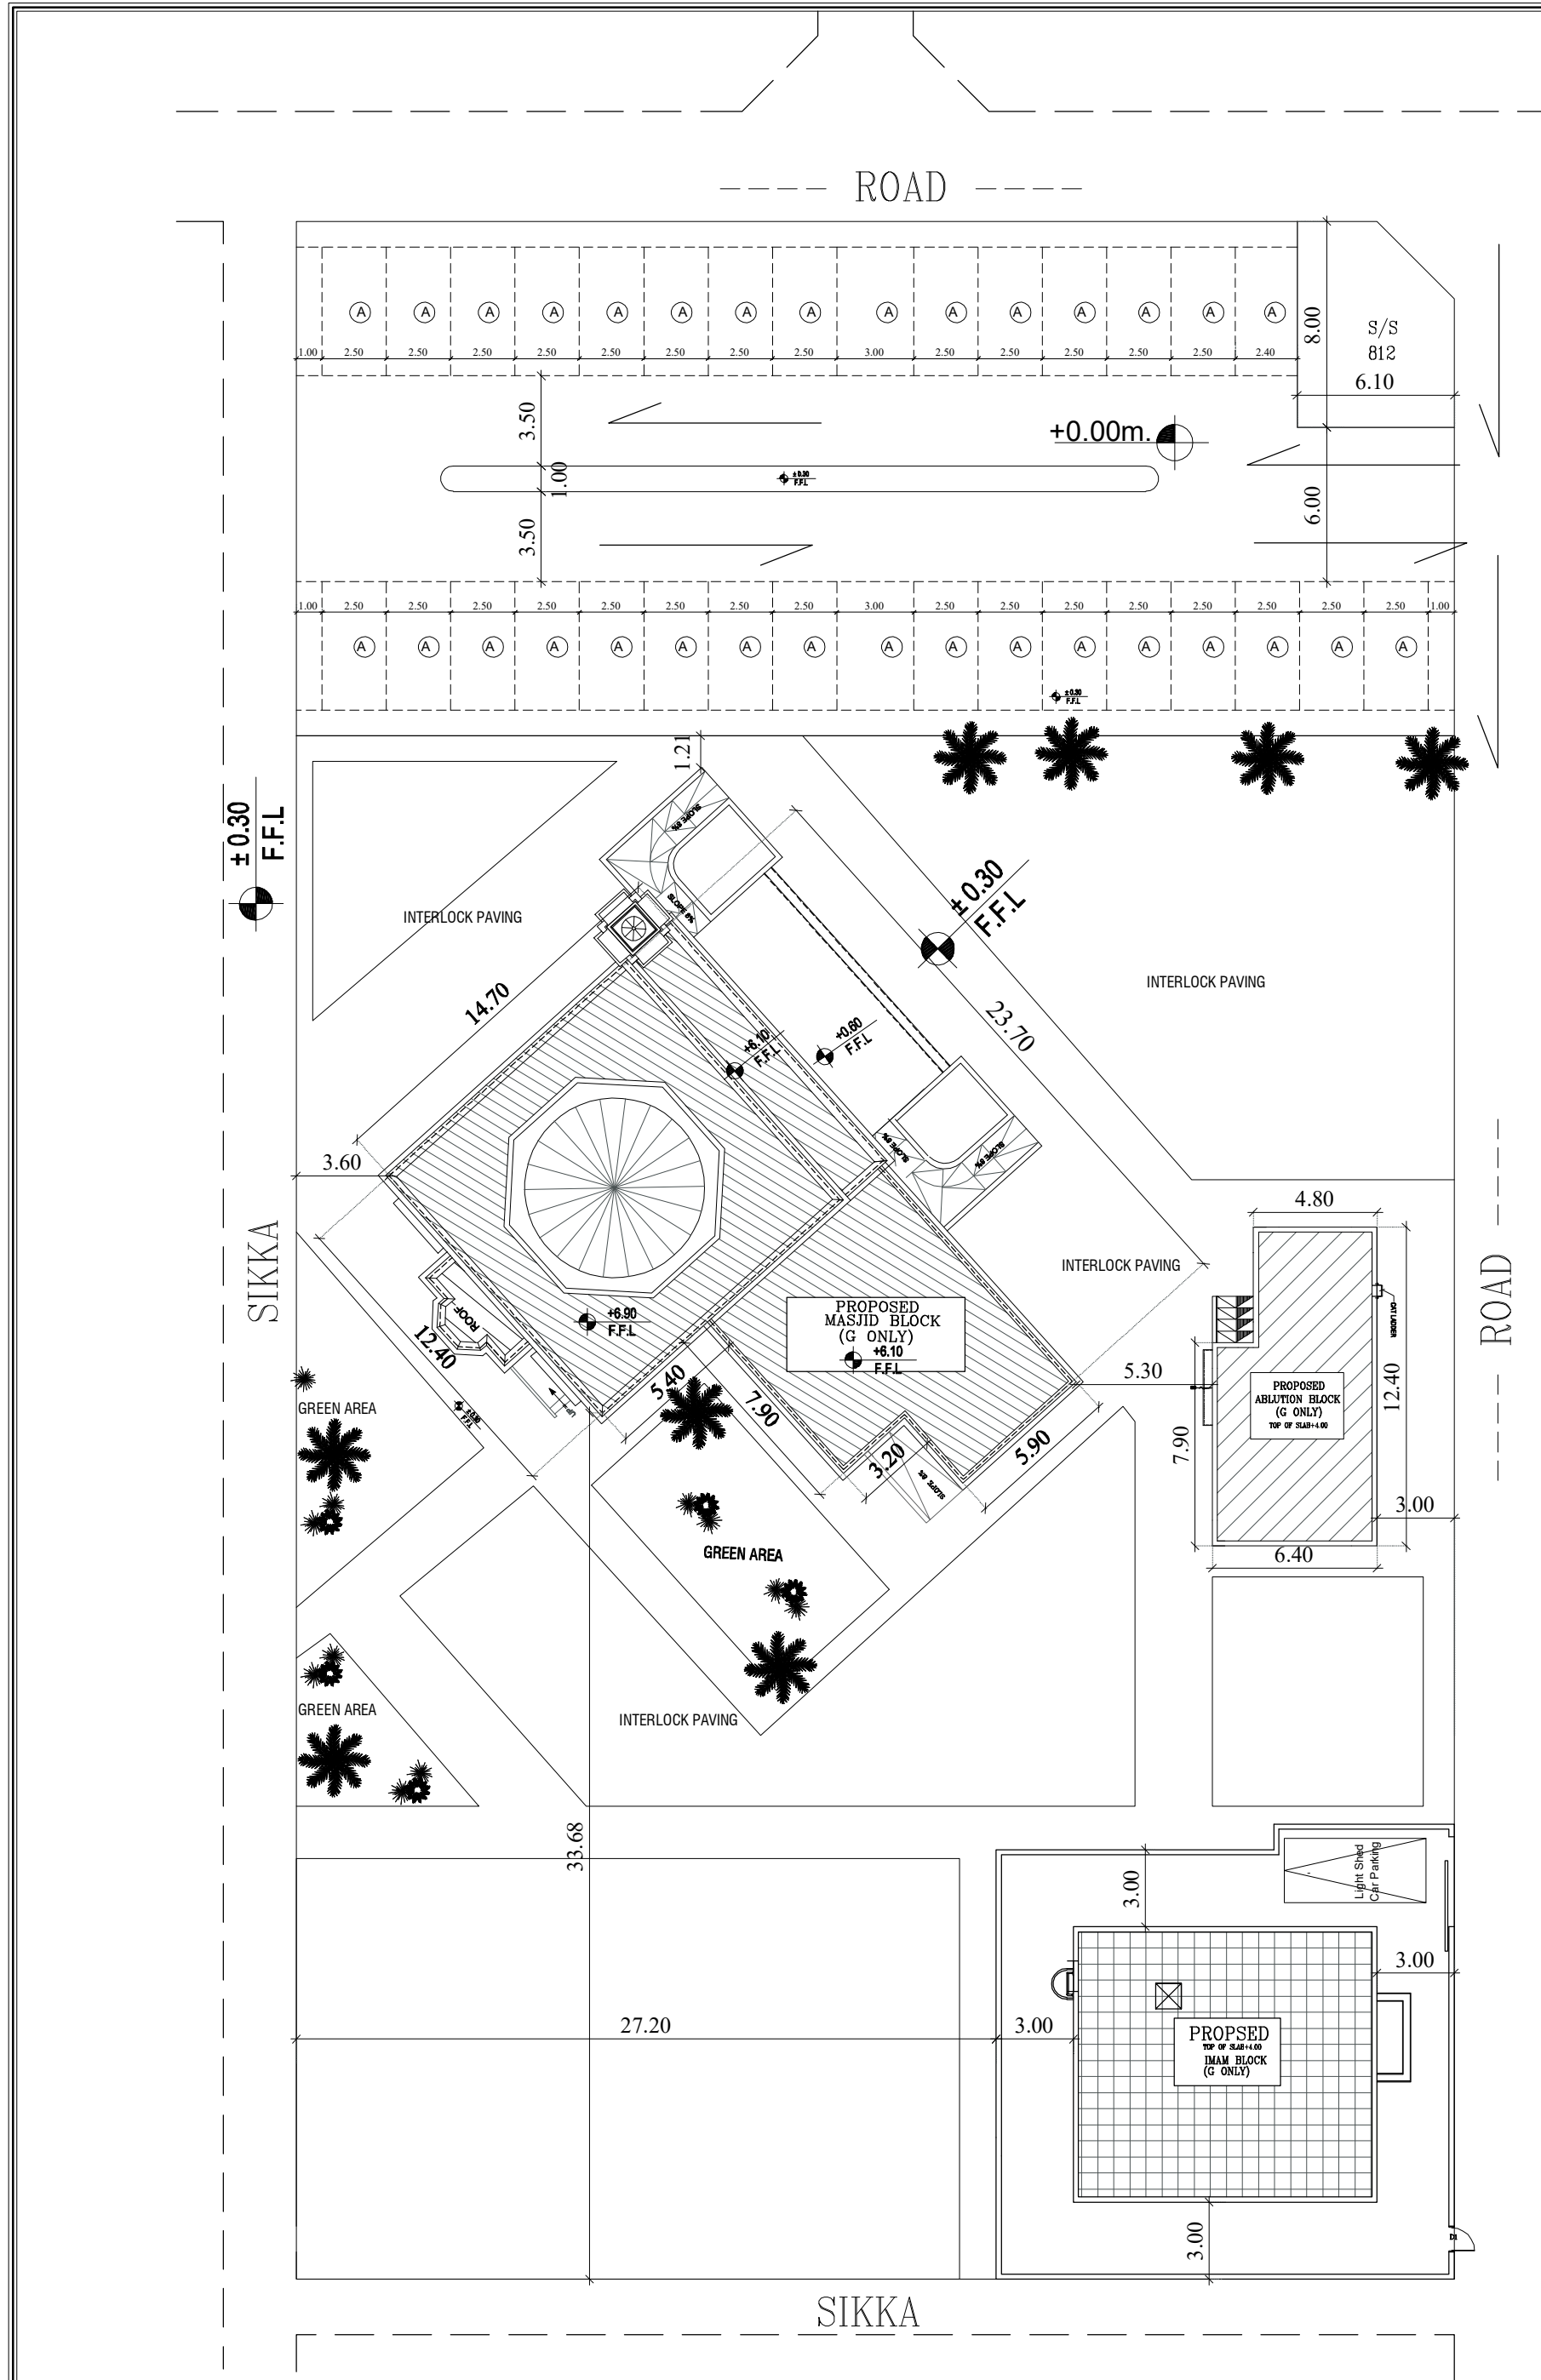

1
SETTING OUT PLAN
SCALE :

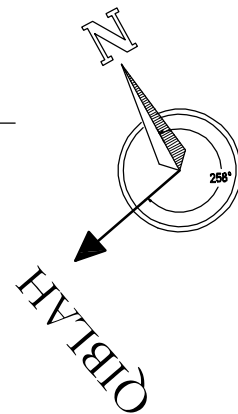

GOVERNMENT OF SHARJAH
Department Of Islamic Affairs

حكومة الشارقة
دائرة الشؤون الإسلامية

التاريخ: 16 نوالقعدة 1442هـ
الموافق: 27 يونيو 2021
المرجع: بيراهد / 934

الموقع: سعادة / ثابت سالم عبيد الطريفي
مدير عام بلدية مدينة الشارقة

السلام عليكم ورحمة الله وبركاته، وبعد:

الموضوع / مخططات المساجد مسابقة الاعتماد

تهديكم الدائرة أطيب تحياتها وتمنياتها لكم بدوام التوفيق والسداد، هذا وبالإشارة إلي الموضوع أعلاه يرجى التكرم بالإيعاز إلي جهة الاختصاص لديكم باعتماد مخططات النماذج التالية:

اسم النموذج	م
SIA - SM-01	1
SIA - SM-02	2
SIA - SM-03	3
SIA - SM-04	4
SIA - SM-05	5
SIA - SM-06	6

وحيث أن هذه النماذج سيتم إستخدامها بشكل متكرر في مشاريع دائرة الشؤون الإسلامية بالإمارة، يرجى التقاضل بإعفاء مكتب / الماسة للاستشارات الهندسية من رسوم اعتماد المخططات، مع تسليمة المخططات الأصلية المعتمدة من قبلكم، شاكرين لكم لحسن تعاونكم معنا.

لزيد من الاستفسار يرجى الاتصال على :

المهندس / محمد عطية ، هاتف رقم 0558049138 - الماسة للاستشارات الهندسية.
المهندس / عبدالله أبو بكر الياسي ، هاتف رقم 0551736666 - دائرة الشؤون الإسلامية
وتفضلوا بقبول فائق الاحترام والتقدير،،،

عبدالله خليفة يعرف السبوسي
رئيس الدائرة

info@sia.gov.ae | Islamic_affairs | Fax: +971 6 5381101 | Tel: +971 8 5055888
www.sia.gov.ae | 066 1688 292 | P.O. Box: 1087 | ح.ب. 1087 | الرقم المجاني: 800 17



Built Up Area Schedule			
S.NO	FLOOR DETAILS	AREA	
		SQ.M	SQ.FT
1	Masjid Area	282.10	3035.45
2	Ablution Block Area	80.48	865.96
3	Imam House Area	126.26	1358.56
Total Built Up Area		488.84	5259.97

GENERAL NOTES:

- IT IS NOT ALLOWED TO REPRODUCE THE SHEETS CONTENTS IN ANY FORM EXCEPT FOR THE PURPOSE FOR WHICH IT IS INTENDED.
- THESE DRAWINGS ARE DIAGRAMMATIC AND SHALL NOT BE SCALED. ADDITIONAL DATA SHALL BE REQUESTED FROM THE CONSULTANCY THROUGH WRITTEN CLARIFICATION. VERIFY ALL EXISTING CONDITIONS AND DIMENSIONS BEFORE PROCEEDING WITH ANY PORTION OF ANY WORK.
- NO CHANGES, MODIFICATIONS OR DEVIATIONS SHALL BE WRITTEN PERMISSION FROM **ALMASAH ENGINEERING CONSULTANTS**.
- ALL WORK AS OUTLINED IN THESE DOCUMENTS, SHALL STRICTLY CONFORM TO ALL APPLICABLE CODES. IN THE EVENT OF A CONFLICT, THE MORE STRINGENT REQUIREMENT SHALL GOVERN AND BE MET.

قطاع الهندسة و المبانى
إدارة تراخيص البناء

15/06/2022
موقع عام معتمد
General Site Approved
التوقيع

SIA - SM-06

حكومة الشارقة
دائرة الشؤون الإسلامية

CONSULTANT STAMP

الماسة
للإستشارات الهندسية
مخططات فقط
AL-MASAH
Engineering Consultant
Drawings Only

الماسة
للإستشارات الهندسية
AL MASAH
Engineering Consultants
Sharjah ☎ 06 5 444 521 ☎ 06 5 444 523 Office: 306, Al Fisal 2 Bldg., King Faisal St.

CLIENT: **GOVERNMENT OF SHARJAH - DEPARTMENT OF ISLAMIC AFFAIRS**

PROJECT: **(SIA - SM-06) PROPOSED MASJID + ABLUTION + IMAM HOUSE**

SHEET TITLE: **SETTING OUT PLAN**

ARCHITECT Arch. Mostafa Ramadan	TYPE	ARCHITECTURE
STRUCTURAL Eng : Mohamed Gomaa	SHEET No.	A-01
CHECKED BY Eng : Mohamed Attia	Location :	
SCALE 1:100	DATE November - 2021	Project No.

© ALL COPYRIGHTS IS RESERVED

GENERAL NOTES:

1. IT IS NOT ALLOWED TO REPRODUCE THE SHEETS CONTENTS IN ANY FORM EXCEPT FOR THE PURPOSE FOR WHICH IT IS INTENDED.
2. THESE DRAWINGS ARE DIAGRAMMATIC AND SHALL NOT BE SCALED. ADDITIONAL DATA SHALL BE REQUESTED FROM THE CONSULTANCY THROUGH WRITTEN CLARIFICATION. VERIFY ALL EXISTING CONDITIONS AND DIMENSIONS BEFORE PROCEEDING WITH ANY PORTION OF ANY WORK.
3. NO CHANGES, MODIFICATIONS OR DEVIATIONS SHALL BE WRITTEN PERMISSION FROM **ALMASAH ENGINEERING CONSULTANTS**.
4. ALL WORK AS OUTLINED IN THESE DOCUMENTS, SHALL STRICTLY CONFORM TO ALL APPLICABLE CODES. IN THE EVENT OF A CONFLICT, THE MORE STRINGENT REQUIREMENT SHALL GOVERN AND BE MET.



SIA - SM-06

حكومة الشارقة
دائرة الشؤون الإسلامية

CONSULTANT STAMP



CLIENT:

GOVERNMENT OF SHARJAH -
DEPARTMENT OF ISLAMIC AFFAIRS

PROJECT:


(SIA - SM-06)
PROPOSED MASJID + ABLUTION +
IMAM HOUSE

SHEET TITLE:

MASJID GROUND FLOOR PLAN

ARCHITECT Arch. Mostafa Ramadan	TYPE ARCHITECTURE
STRUCTURAL Eng : Mohamed Gomaa	SHEET No. A- 02
CHECKED BY Eng : Mohamed Attia	Location : Plot No :
SCALE 1:100	DATE November - 2021
Project No.	


© ALL COPYRIGHTS IS RESERVED

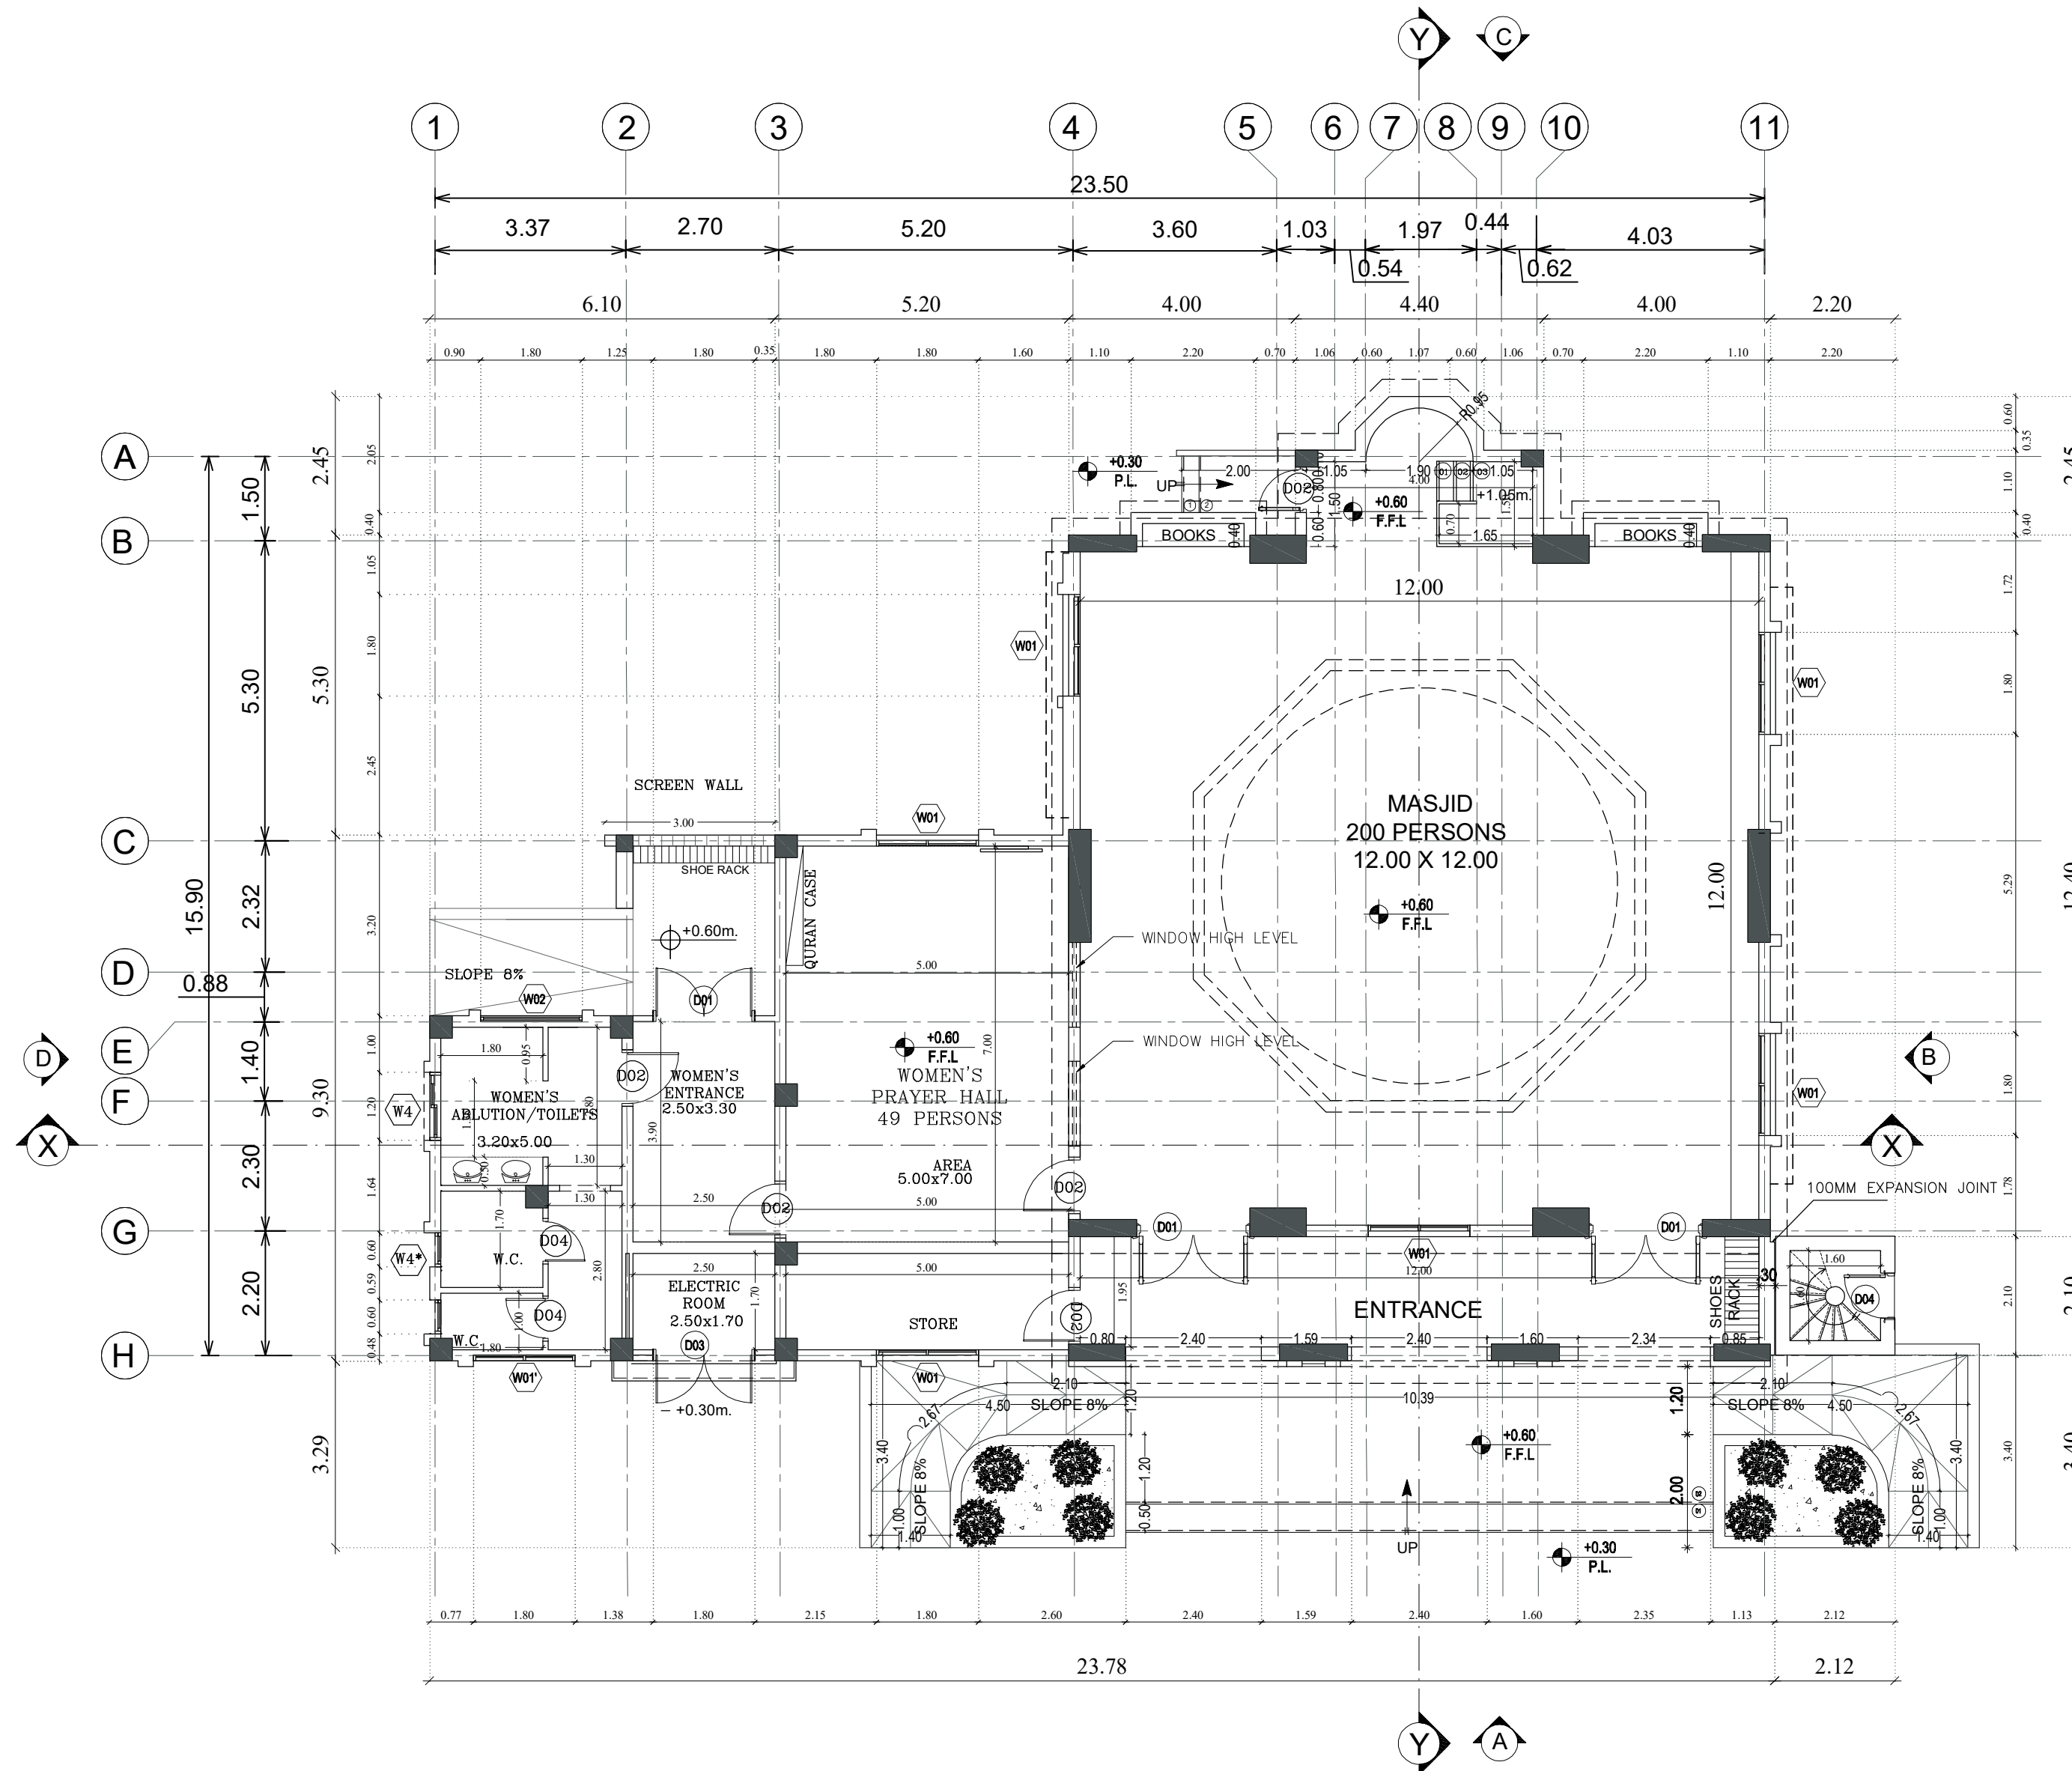

1

MASJID GROUND FLOOR PLAN

SCALE :

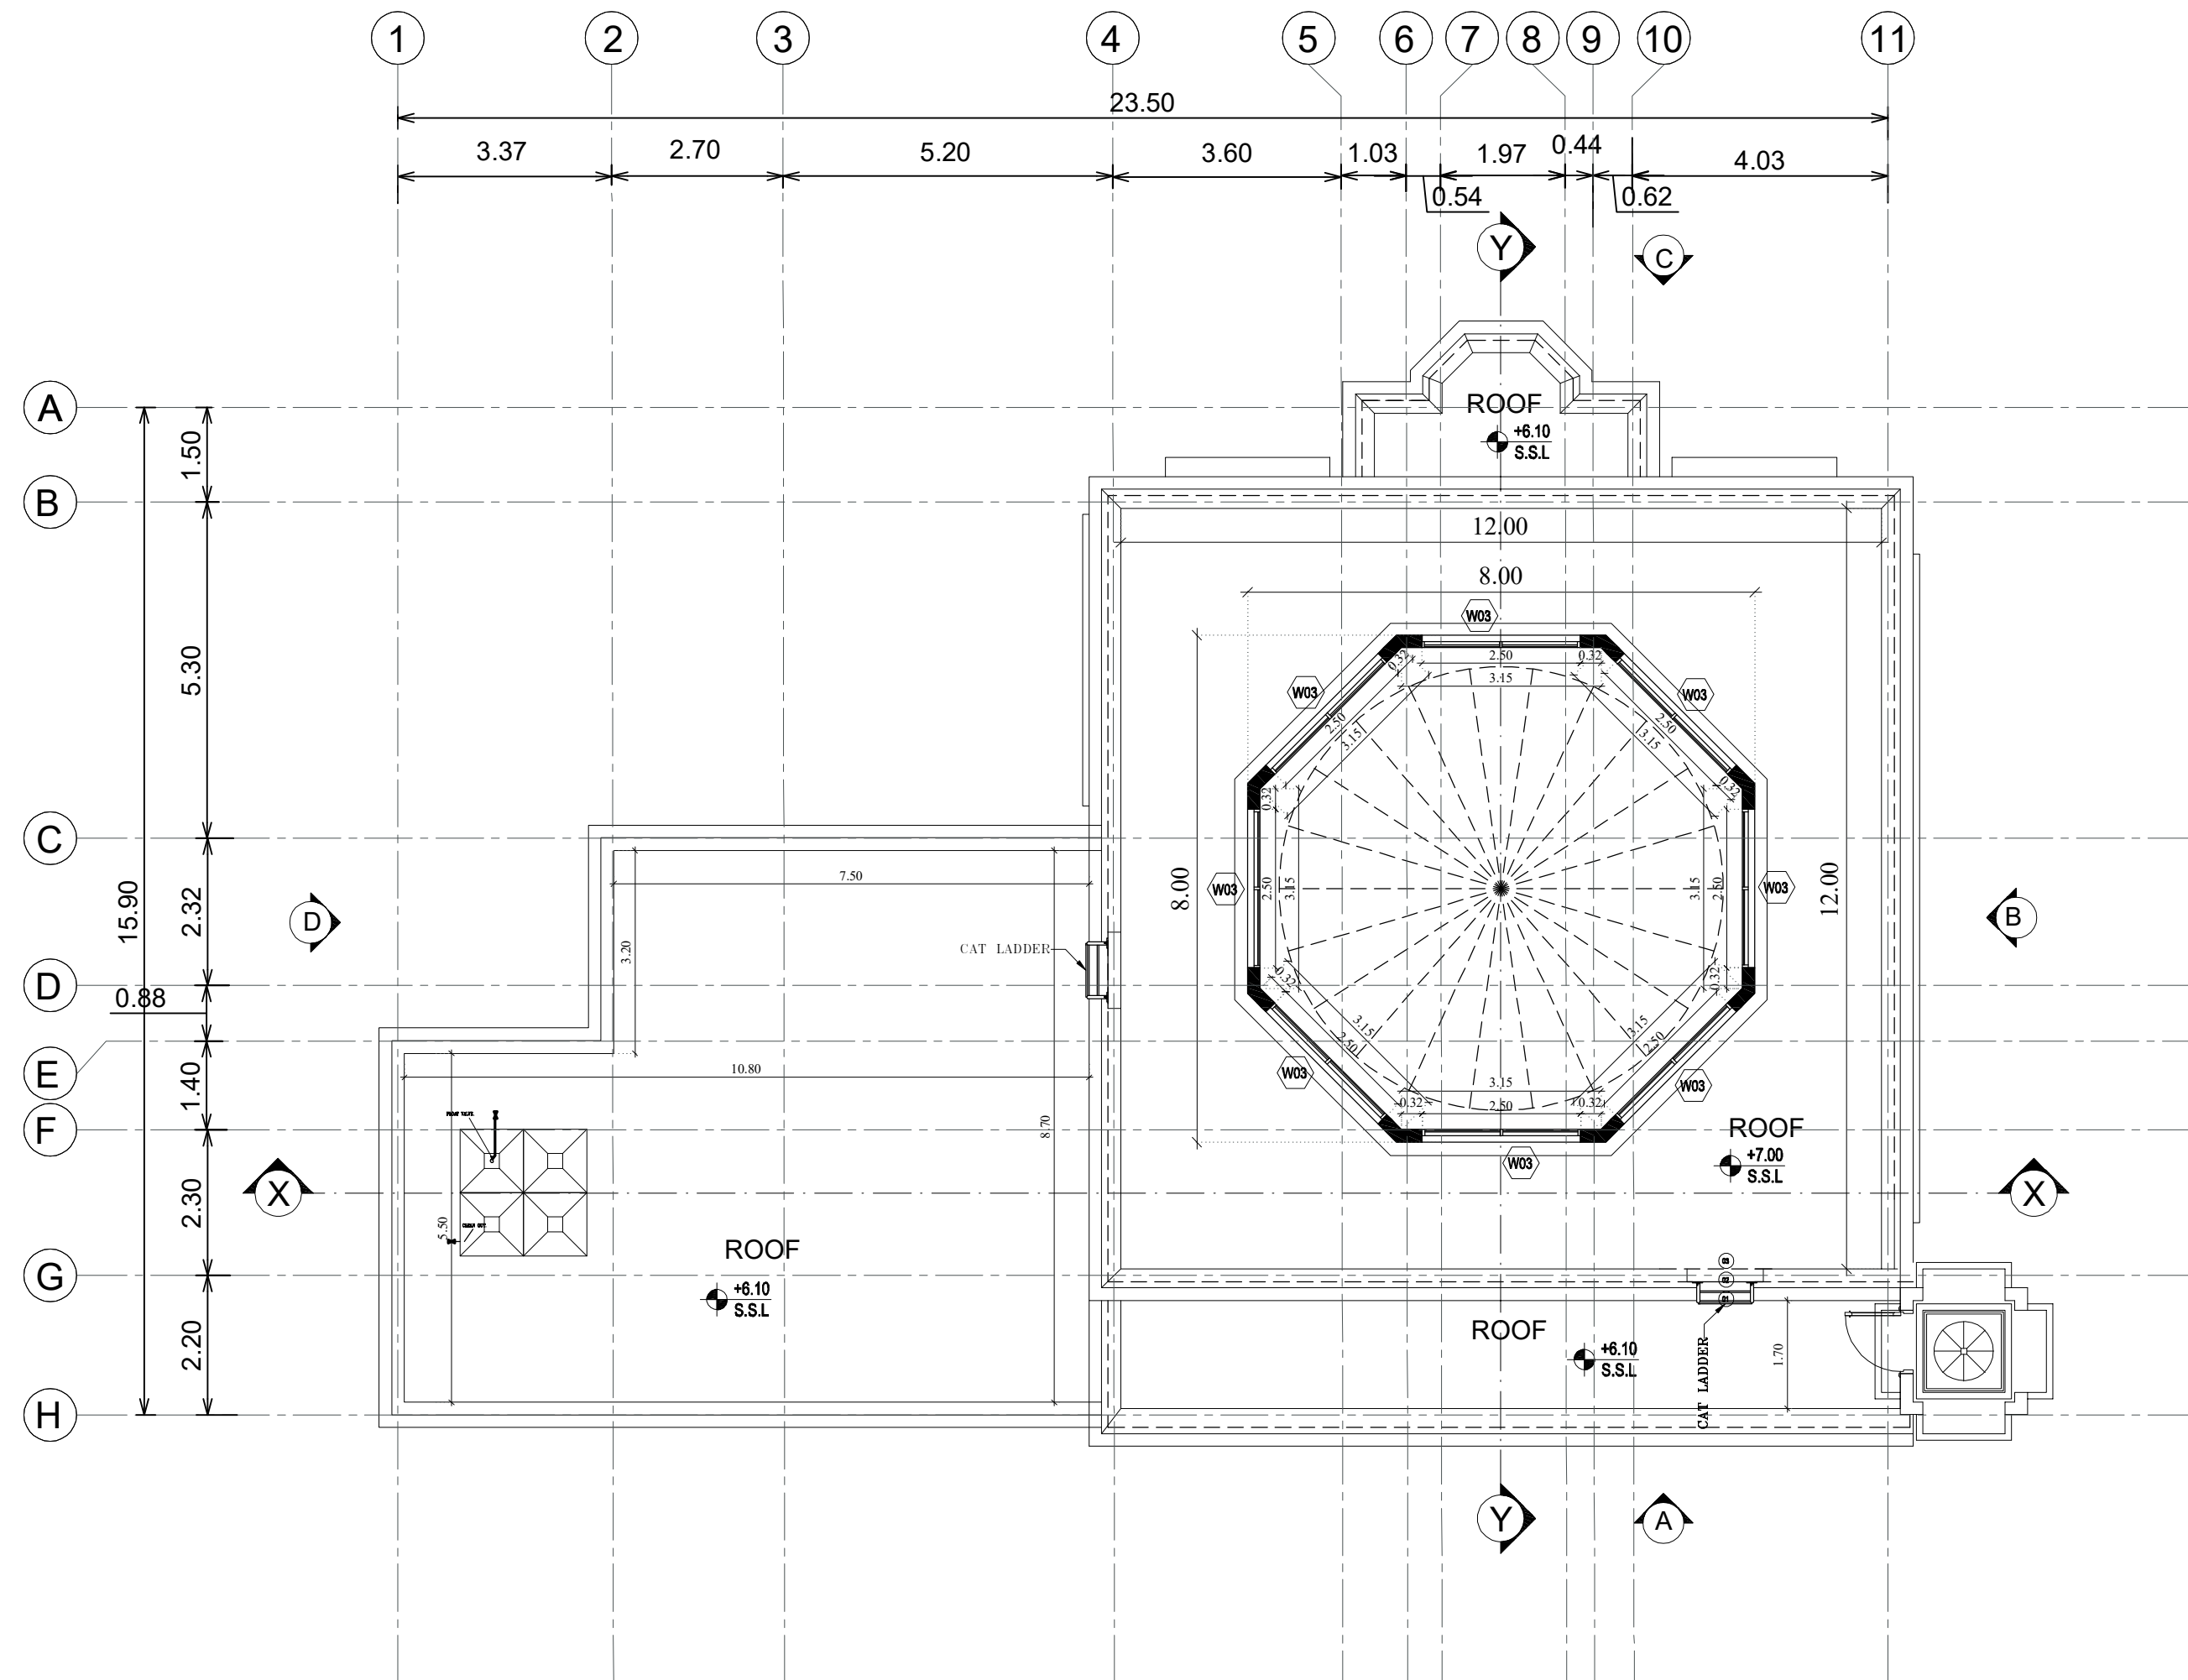

1
MASJID ROOF PLAN
SCALE :


- GENERAL NOTES:**
1. IT IS NOT ALLOWED TO REPRODUCE THE SHEETS CONTENTS IN ANY FORM EXCEPT FOR THE PURPOSE FOR WHICH IT IS INTENDED.
 2. THESE DRAWINGS ARE DIAGRAMMATIC AND SHALL NOT BE SCALED. ADDITIONAL DATA SHALL BE REQUESTED FROM THE CONSULTANCY THROUGH WRITTEN CLARIFICATION. VERIFY ALL EXISTING CONDITIONS AND DIMENSIONS BEFORE PROCEEDING WITH ANY PORTION OF ANY WORK.
 3. NO CHANGES, MODIFICATIONS OR DEVIATIONS SHALL BE WRITTEN PERMISSION FROM **ALMASAH ENGINEERING CONSULTANTS**.
 4. ALL WORK AS OUTLINED IN THESE DOCUMENTS, SHALL STRICTLY CONFORM TO ALL APPLICABLE CODES. IN THE EVENT OF A CONFLICT, THE MORE STRINGENT REQUIREMENT SHALL GOVERN AND BE MET.



SIA - SM-06



CLIENT: GOVERNMENT OF SHARJAH - DEPARTMENT OF ISLAMIC AFFAIRS		
PROJECT: (SIA - SM-06) PROPOSED MASJID + ABLUTION + IMAM HOUSE		
SHEET TITLE: MASJID ROOF PLAN		
ARCHITECT Arch. Mostafa Ramadan	TYPE	ARCHITECTURE
STRUCTURAL Eng : Mohamed Gomaa	SHEET No.	A- 03
CHECKED BY Eng : Mohamed Attia	Location :	
SCALE 1:100	DATE November - 2021	Project No.

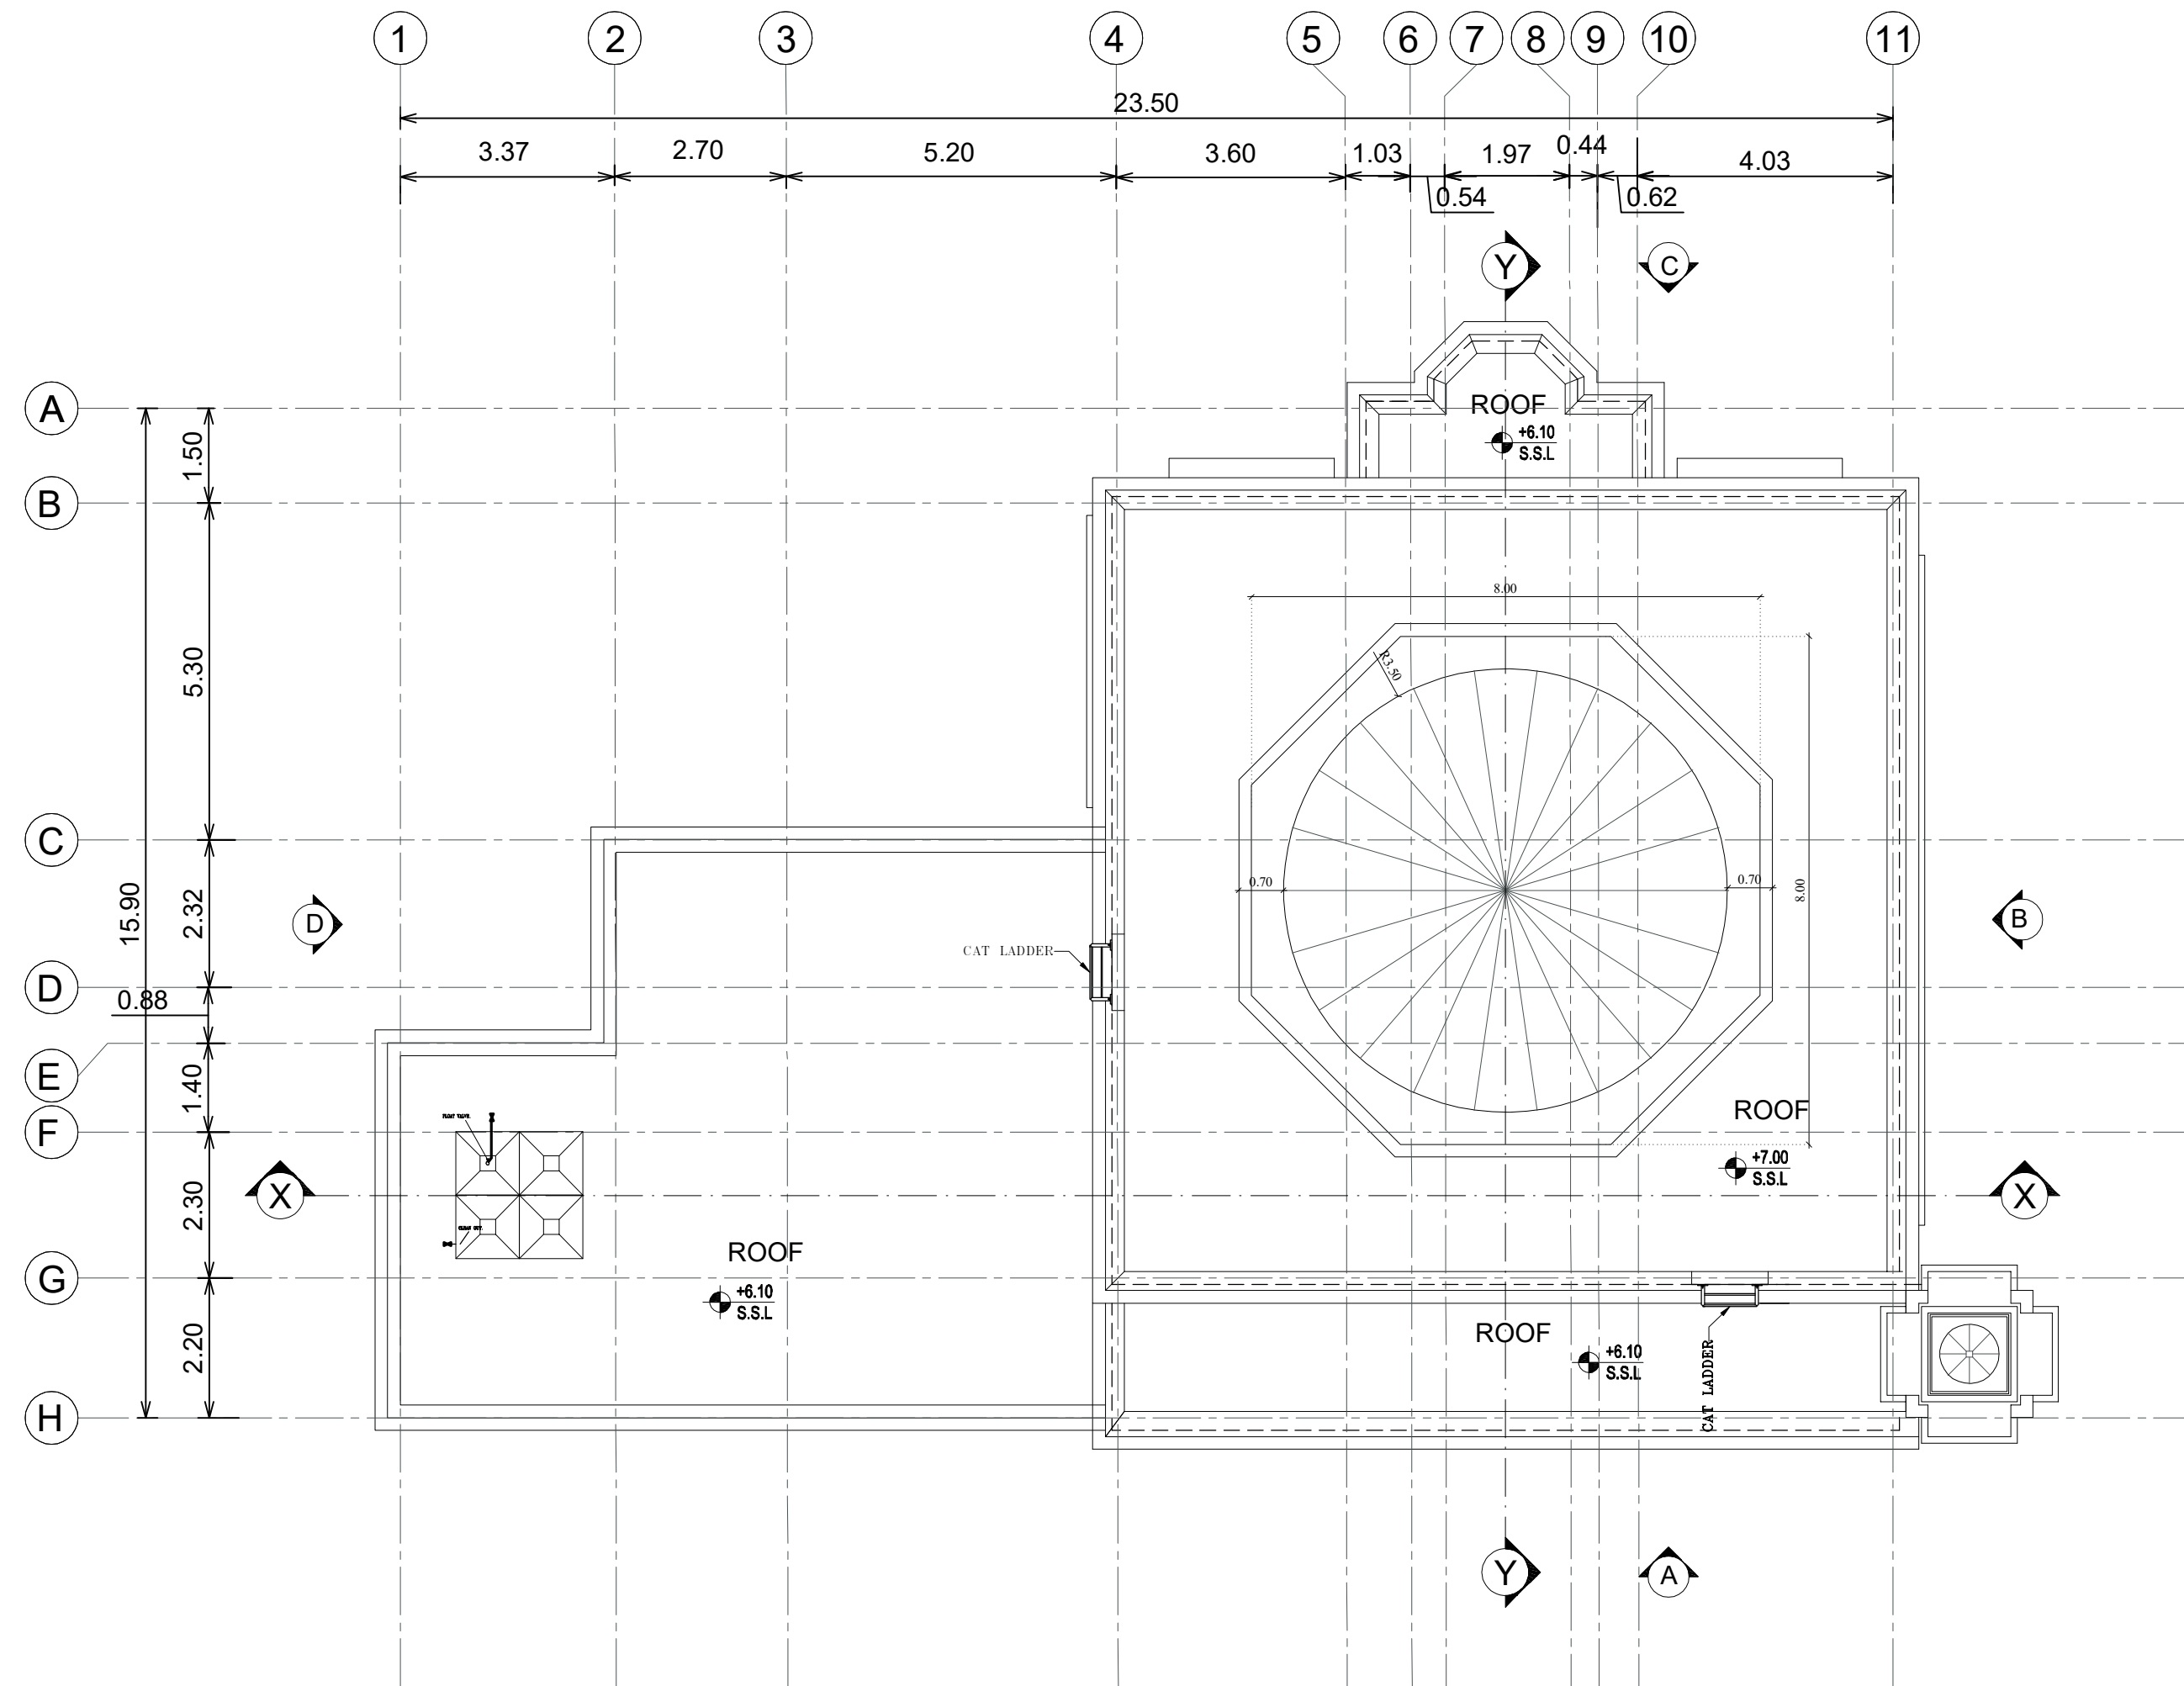

MASJID TOP ROOF PLAN

SCALE :

GENERAL NOTES:

1. IT IS NOT ALLOWED TO REPRODUCE THE SHEETS CONTENTS IN ANY FORM EXCEPT FOR THE PURPOSE FOR WHICH IT IS INTENDED.
2. THESE DRAWINGS ARE DIAGRAMMATIC AND SHALL NOT BE SCALED. ADDITIONAL DATA SHALL BE REQUESTED FROM THE CONSULTANCY THROUGH WRITTEN CLARIFICATION. VERIFY ALL EXISTING CONDITIONS AND DIMENSIONS BEFORE PROCEEDING WITH ANY PORTION OF ANY WORK.
3. NO CHANGES, MODIFICATIONS OR DEVIATIONS SHALL BE WRITTEN PERMISSION FROM **ALMASAH ENGINEERING CONSULTANTS**.
4. ALL WORK AS OUTLINED IN THESE DOCUMENTS, SHALL STRICTLY CONFORM TO ALL APPLICABLE CODES. IN THE EVENT OF A CONFLICT, THE MORE STRINGENT REQUIREMENT SHALL GOVERN AND BE MET.



SIA - SM-06



حُكُومَةُ الشَّارِجَةِ
دائرة الشؤون الإسلامية

CONSULTANT STAMP



CLIENT: **GOVERNMENT OF SHARJAH - DEPARTMENT OF ISLAMIC AFFAIRS**

PROJECT: **(SIA - SM-06) PROPOSED MASJID + ABLUTION + IMAM HOUSE**

SHEET TITLE: **MASJID TOP ROOF PLAN**

ARCHITECT Arch. Mostafa Ramadan	TYPE ARCHITECTURE
STRUCTURAL Eng : Mohamed Gomaa	SHEET No. A- 04
CHECKED BY Eng : Mohamed Attia	Location : Plot No :
SCALE 1:100	DATE November - 2021
	Project No.

ELEVATION FINISHES

- 1- REFLECTIVE GLASS
- 2- GRAFFIO DECOR WHITE PAINT OR STONE CLADDING
- 3- GRAFFIO DECOR OFF WHITE PAINT OR STONE CLADDING
- 4- GRANITE FINISHING
- 5- G.R.C.

ALL WINDOWS & BALCONY DOORS SHOULD BE EQUIPPED WITH WINDOWS OPENING CONTROL DEVICE (W.O.C.D.) TO LIMITS THE OPENING LESS THAN 10 CM TO HAVE MAXIMUM OPENING LIMIT OF 10 CM TO HELP IN THE PREVENTION OF ACCIDENTAL FALLS FROM WINDOWS & BALCONIES BY CHILDREN AS PER SHARJAH MUNICIPALITY REGULATIONS.

GENERAL NOTES:

- 1.IT IS NOT ALLOWED TO REPRODUCE THE SHEETS CONTENTS IN ANY FORM EXCEPT FOR THE PURPOSE FOR WHICH IT IS INTENDED.
2. THESE DRAWINGS ARE DIAGRAMMATIC AND SHALL NOT BE SCALED. ADDITIONAL DATA SHALL BE REQUESTED FROM THE CONSULTANCY THROUGH WRITTEN CLARIFICATION. VERIFY ALL EXISTING CONDITIONS AND DIMENSIONS BEFORE PROCEEDING WITH ANY PORTION OF ANY WORK.
3. NO CHANGES, MODIFICATIONS OR DEVIATIONS SHALL BE WRITTEN PERMISSION FROM **ALMASAH ENGINEERING CONSULTANTS**.
4. ALL WORK AS OUTLINED IN THESE DOCUMENTS, SHALL STRICTLY CONFORM TO ALL APPLICABLE CODES. IN THE EVENT OF A CONFLICT, THE MORE STRINGENT REQUIREMENT SHALL GOVERN AND BE MET.



SIA - SM-06



CONSULTANT STAMP



CLIENT:

GOVERNMENT OF SHARJAH -
DEPARTMENT OF ISLAMIC AFFAIRS

PROJECT:

(SIA - SM-06)
PROPOSED MASJID + ABLUTION +
IMAM HOUSE

SHEET TITLE:

MASJID ELEVATIONS A & B

ARCHITECT Arch. Mostafa Ramadan	TYPE ARCHITECTURE	
STRUCTURAL Eng : Mohamed Gomaa	SHEET No.	A- 05
CHECKED BY Eng : Mohamed Attia	Location :	
SCALE 1:100	Plot No :	
DATE November - 2021	Project No.	

© ALL COPYRIGHTS IS RESERVED

- ELEVATION FINISHES**
- 1- REFLECTIVE GLASS
 - 2- GRAFFIO DECOR WHITE PAINT OR STONE CLADDING
 - 3- GRAFFIO DECOR OFF WHITE PAINT OR STONE CLADDING
 - 4- GRANITE FINISHING
 - 5- G.R.C.

ALL WINDOWS & BALCONY DOORS SHOULD BE EQUIPED WITH WINDOWS OPENING CONTROL DEVICE (W.O.C.D.) TO LIMITS THE OPENING LESS THAN 10 CM TO HAVE MAXIMUM OPENING LIMIT OF 10 CM TO HELP IN THE PREVENTION OF ACCIDENTAL FALLS FROM WINDOWS & BALCONIES BY CHILDREN AS PER SHARJAH MUNICIPALITY REGULATIONS.

GENERAL NOTES:

- 1.IT IS NOT ALLOWED TO REPRODUCE THE SHEETS CONTENTS IN ANY FORM EXCEPT FOR THE PURPOSE FOR WHICH IT IS INTENDED.
2. THESE DRAWINGS ARE DIAGRAMMATIC AND SHALL NOT BE SCALED. ADDITIONAL DATA SHALL BE REQUESTED FROM THE CONSULTANCY THROUGH WRITTEN CLARIFICATION. VERIFY ALL EXISTING CONDITIONS AND DIMENSIONS BEFORE PROCEEDING WITH ANY PORTION OF ANY WORK.
3. NO CHANGES, MODIFICATIONS OR DEVIATIONS SHALL BE WRITTEN PERMISSION FROM **ALMASAH ENGINEERING CONSULTANTS**.
4. ALL WORK AS OUTLINED IN THESE DOCUMENTS, SHALL STRICTLY CONFORM TO ALL APPLICABLE CODES. IN THE EVENT OF A CONFLICT, THE MORE STRINGENT REQUIREMENT SHALL GOVERN AND BE MET.



SIA - SM-06



CONSULTANT STAMP






CLIENT: **GOVERNMENT OF SHARJAH - DEPARTMENT OF ISLAMIC AFFAIRS**

PROJECT: **(SIA - SM-06) PROPOSED MASJID + ABLUTION + IMAM HOUSE**

SHEET TITLE: **MASJID ELEVATIONS C & D**


ARCHITECT Arch. Mostafa Ramadan	TYPE ARCHITECTURE	
STRUCTURAL Eng : Mohamed Gomaa	SHEET No.	A- 06
CHECKED BY Eng : Mohamed Attia	Location :	
SCALE 1:100	Plot No :	
DATE November - 2021	Project No.	

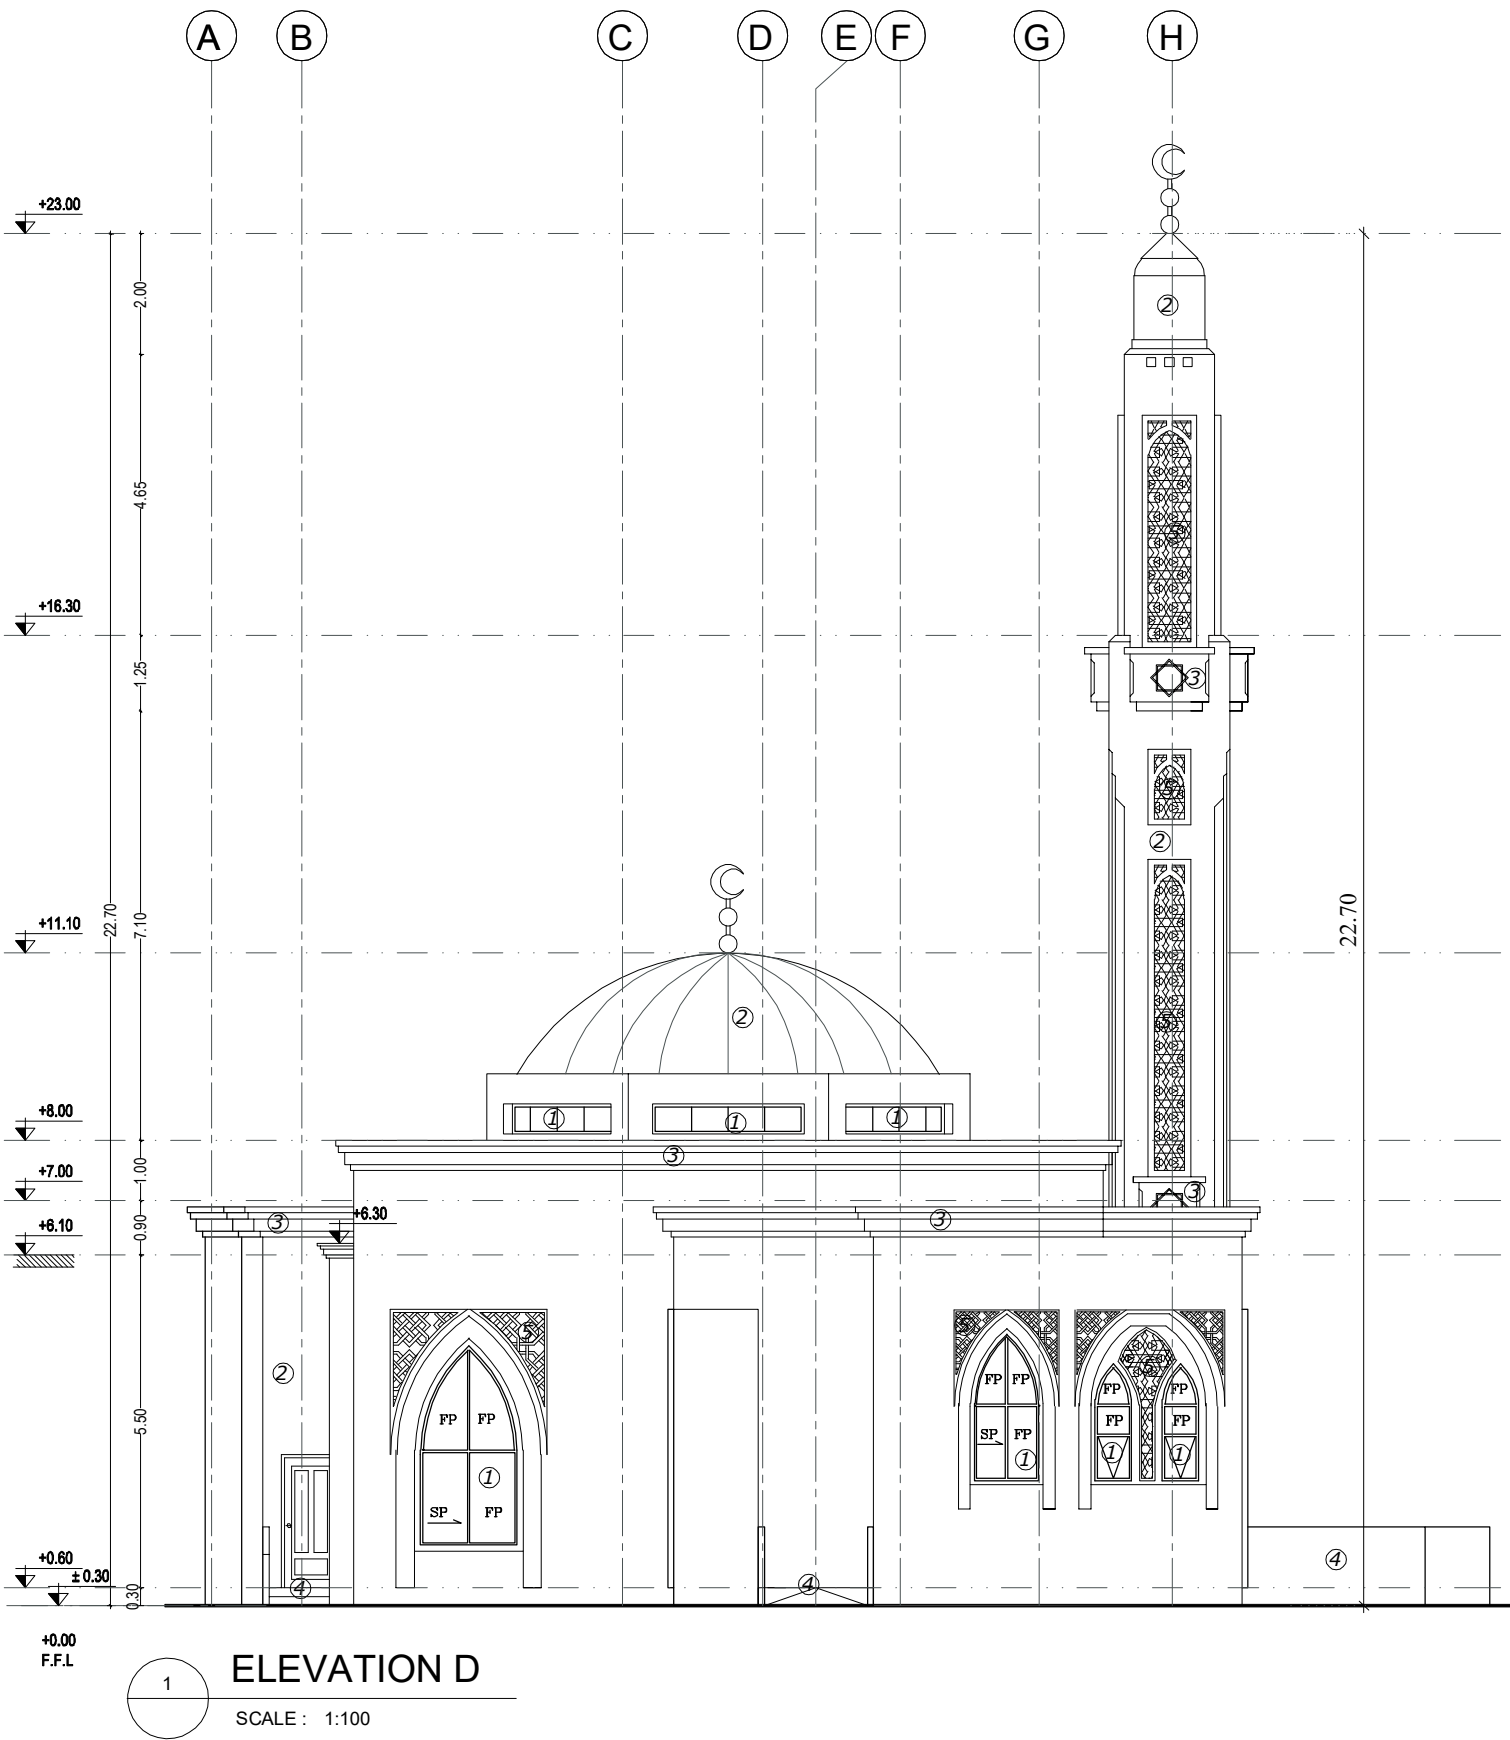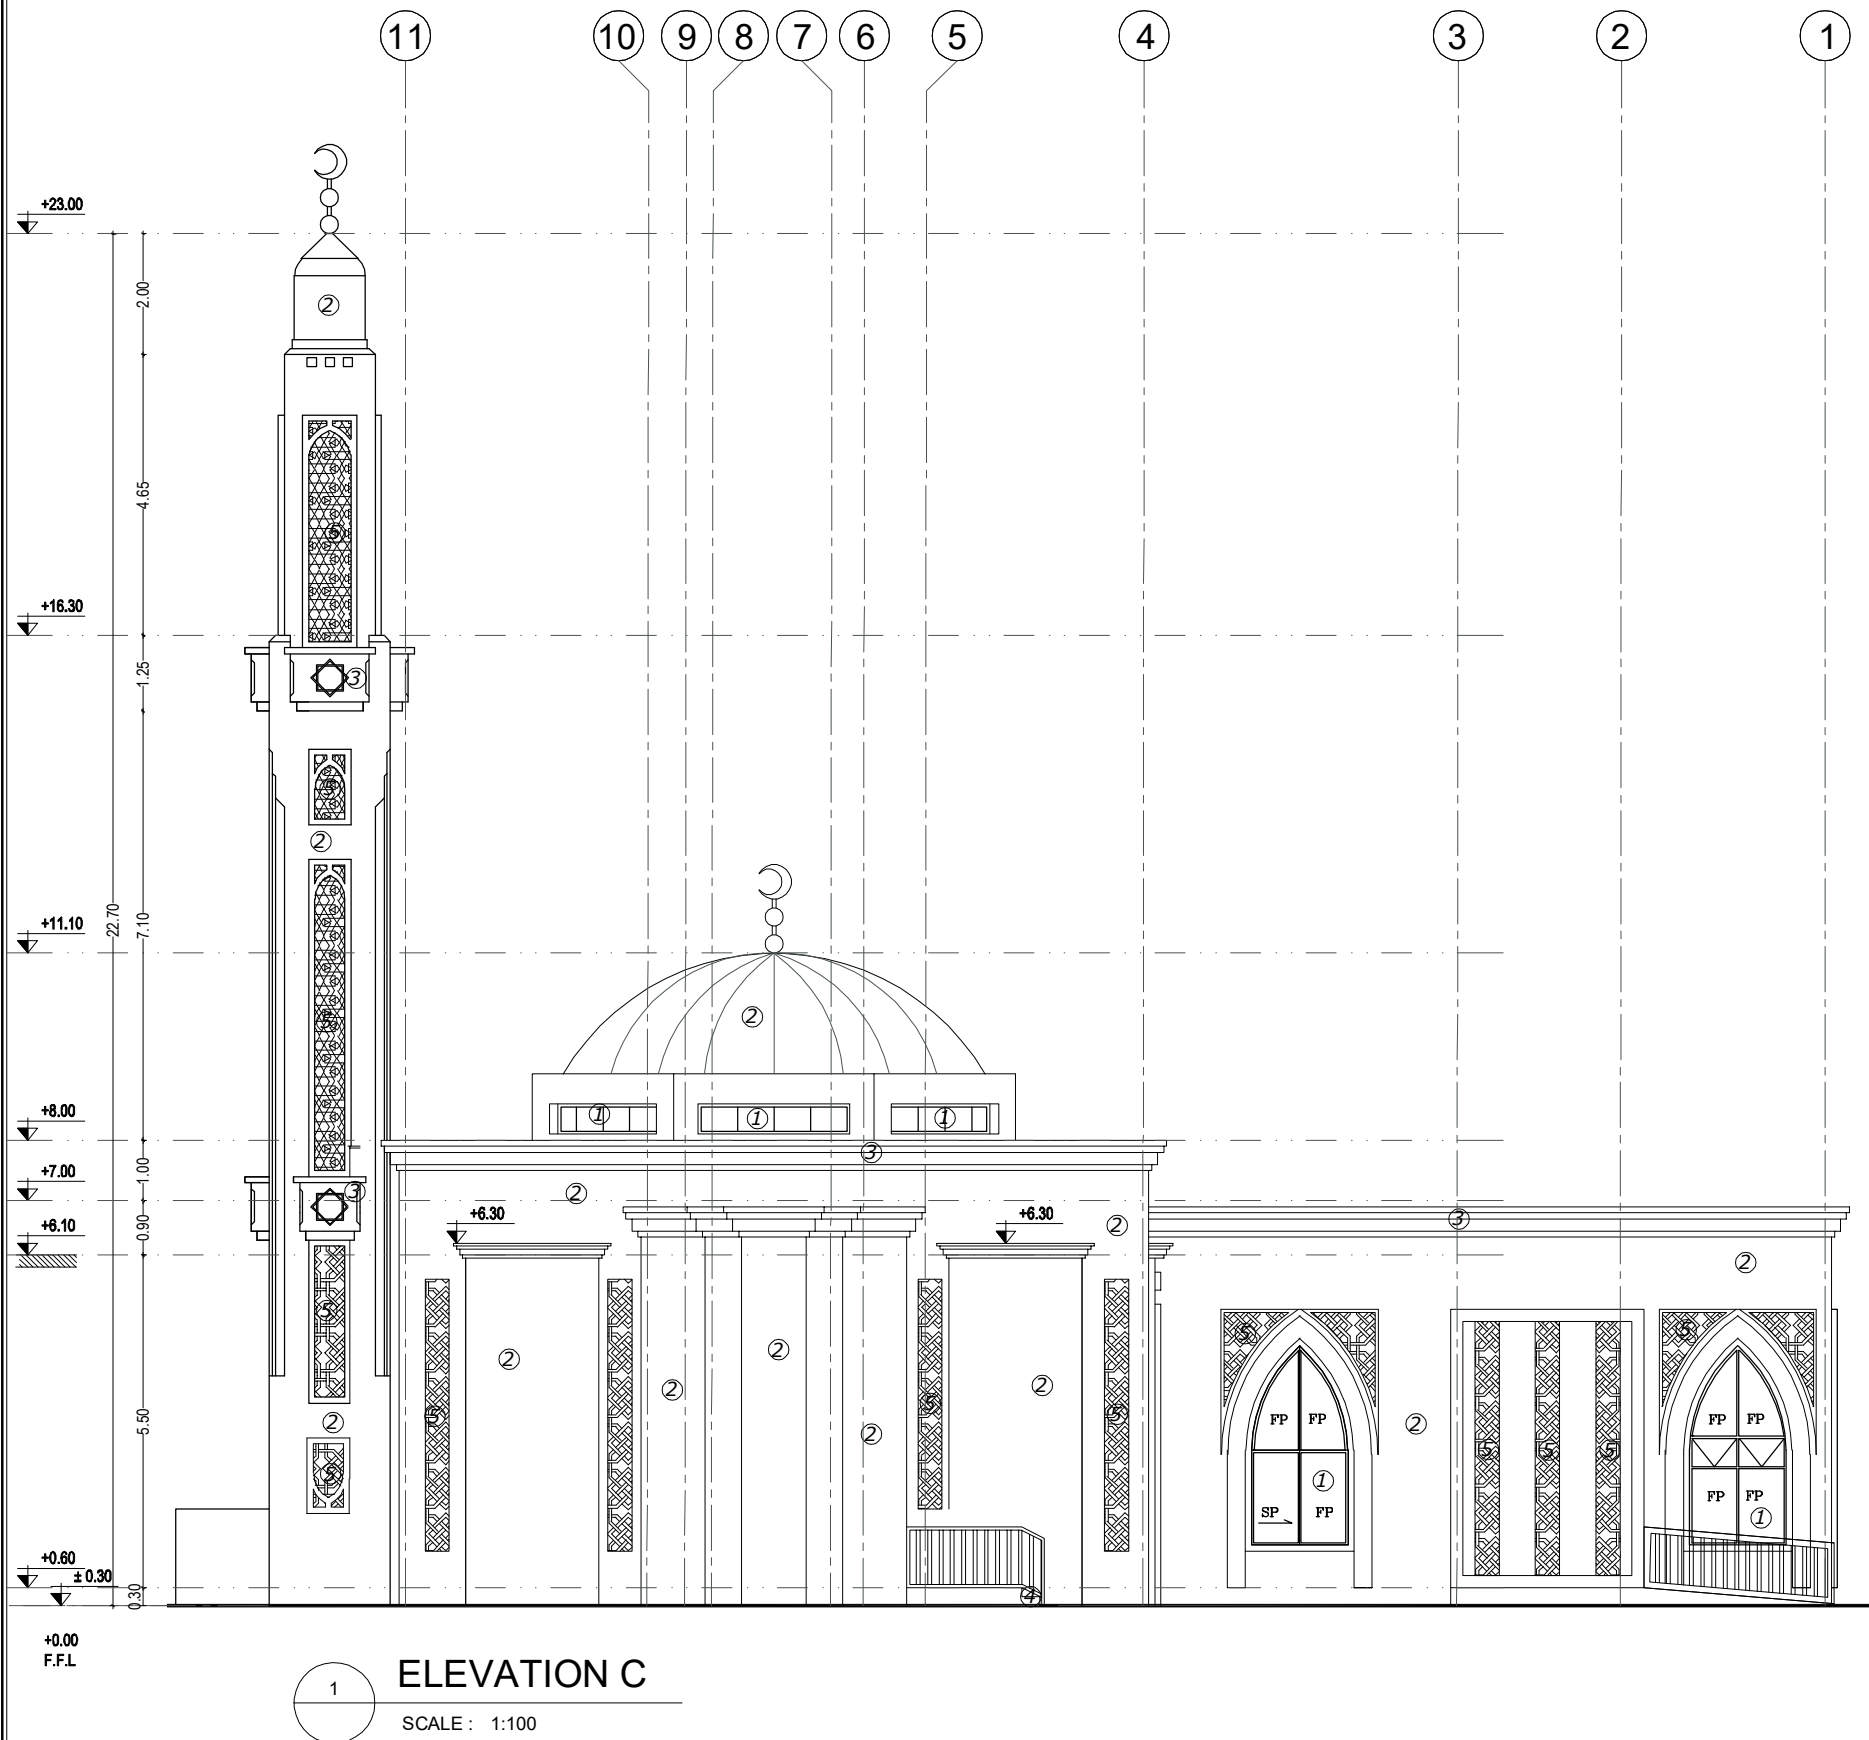

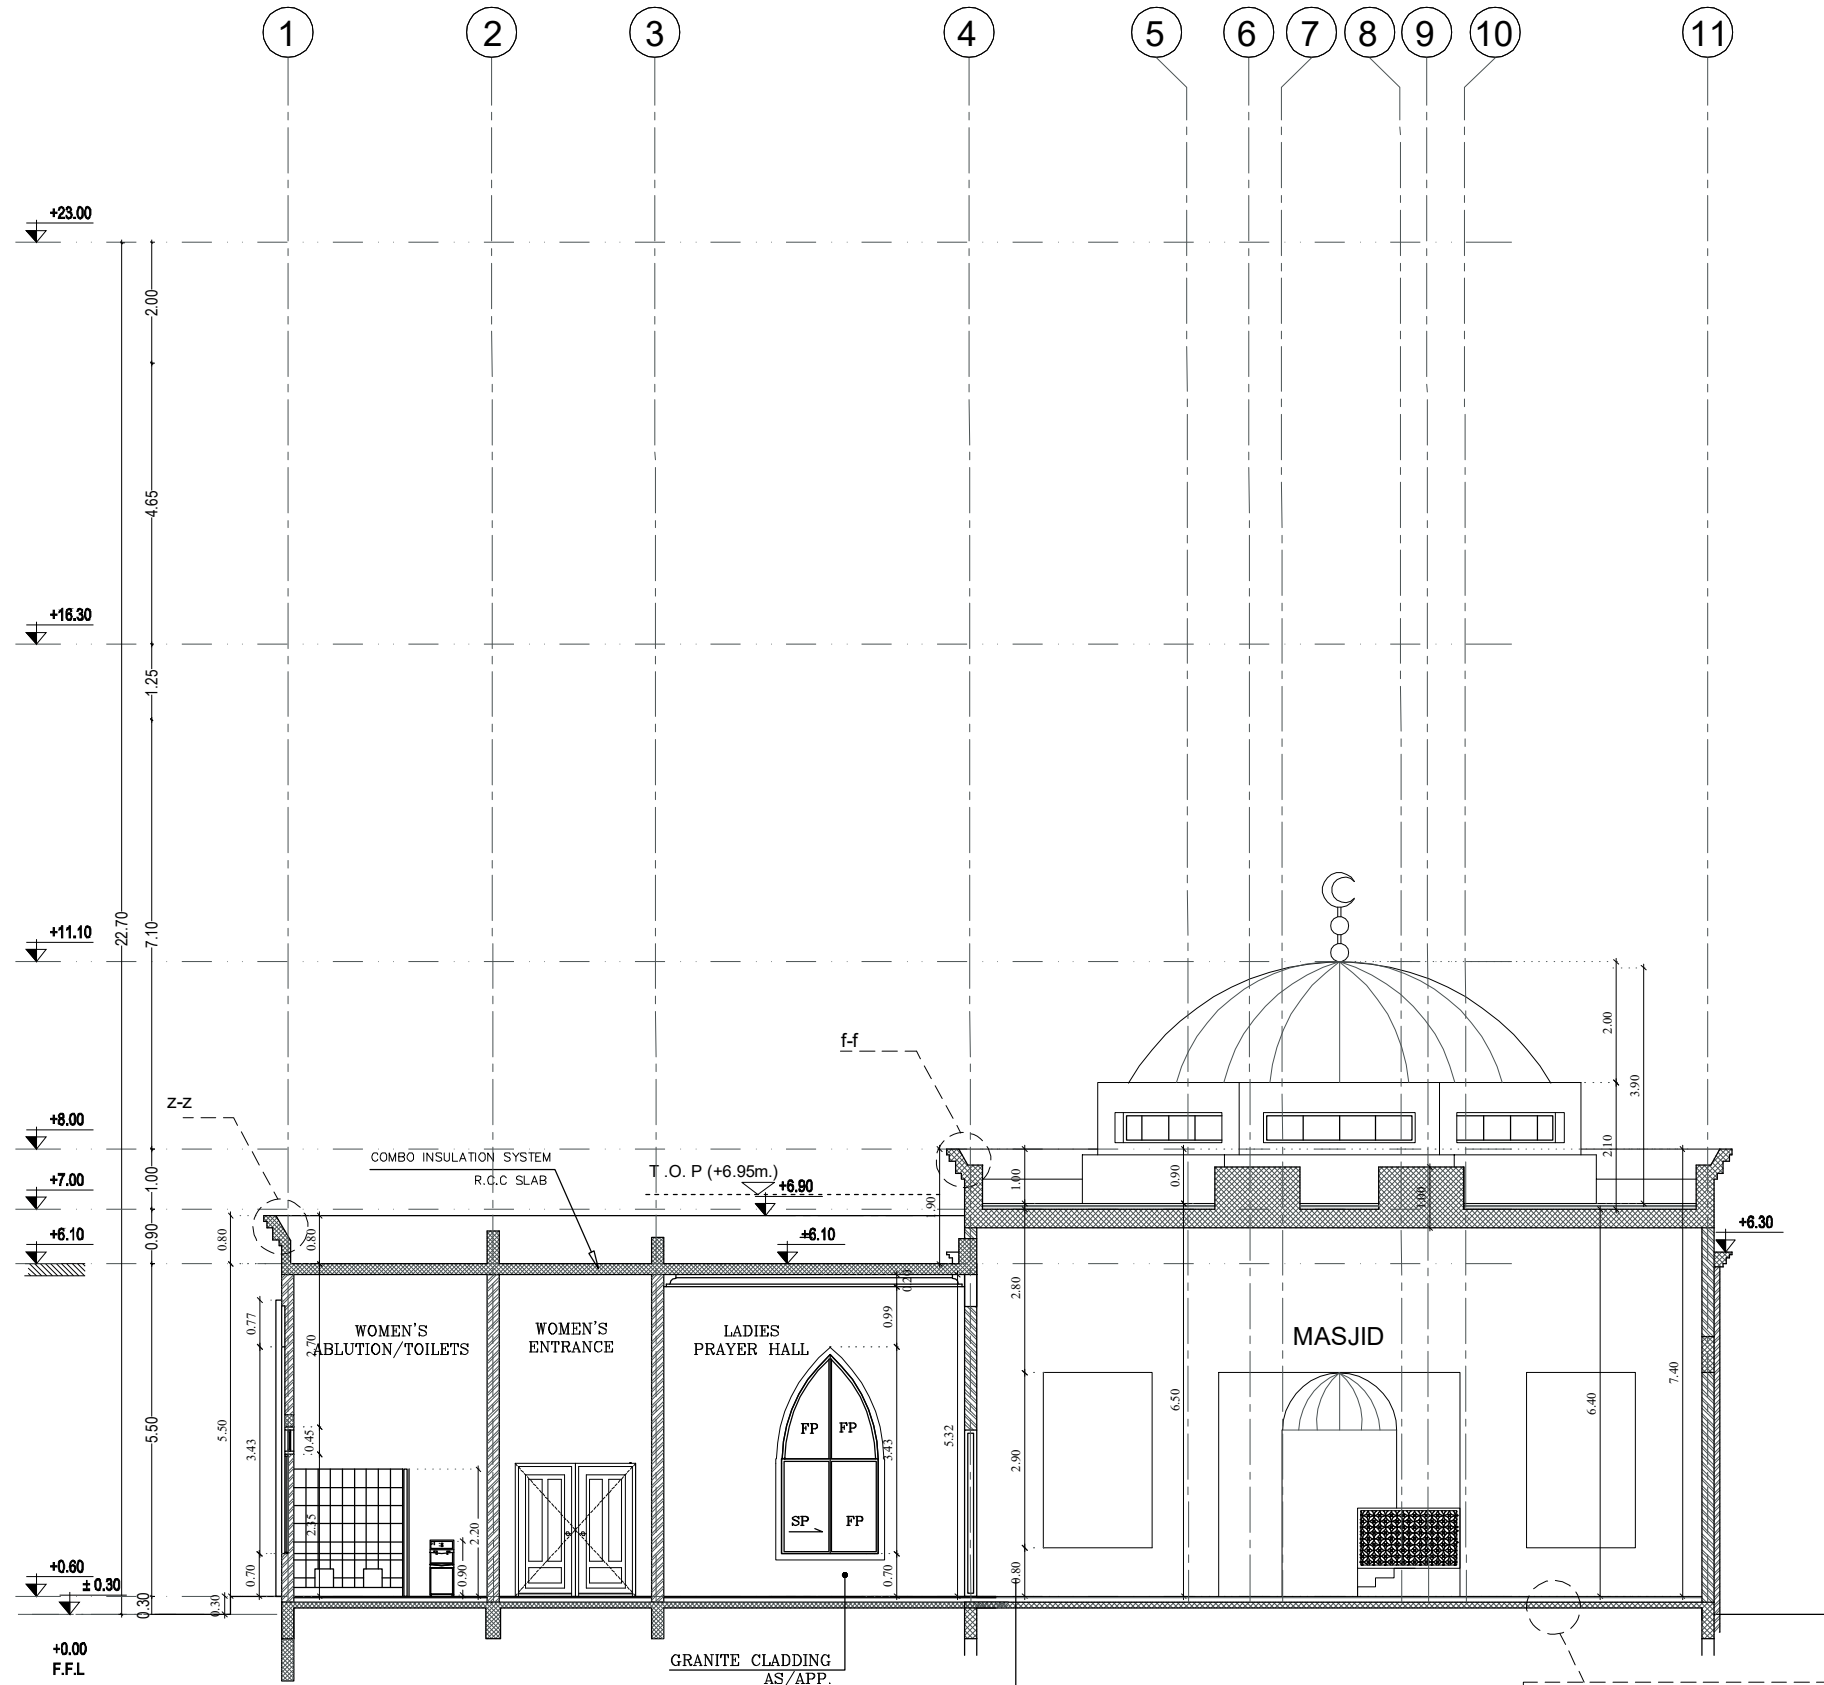


MASJID SECTION X-X

SCALE : 1:125

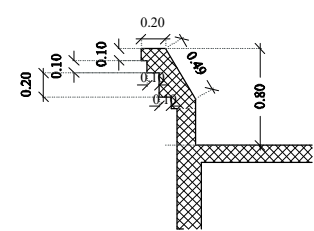

TYPICAL PARAPET DETAIL z-z

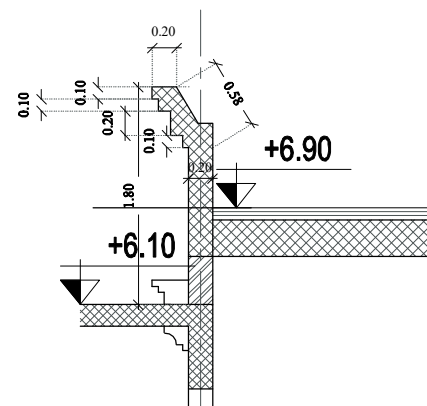


TYPICAL PARAPET DETAIL f-f

TYPICAL PARAPET DETAIL
SCALE = 1:20

SUBKHA FILLING IN LAYERS.
MARBLE SKIRTING ALL AROUND
AS PER SPECIFICATION
MORTAR SCREED AND SAND FLOORING CONCRETE
10 cm THICK B.R.C FLOORING WITH
ANTI - TERMITE


- SKIRTING AS PER SCHEDULE
- TILES AS PER SCHEDULE
- MORTAR
- 10cm THICK CONCRETE,
WITH 8mm MESH STEEL 150mm C/C
- 1000 GAUGE POLYTHENE SHEET
- ANTI TERMITE TREATMENT
- COMPACTED AND TESTED FILLING LAYER

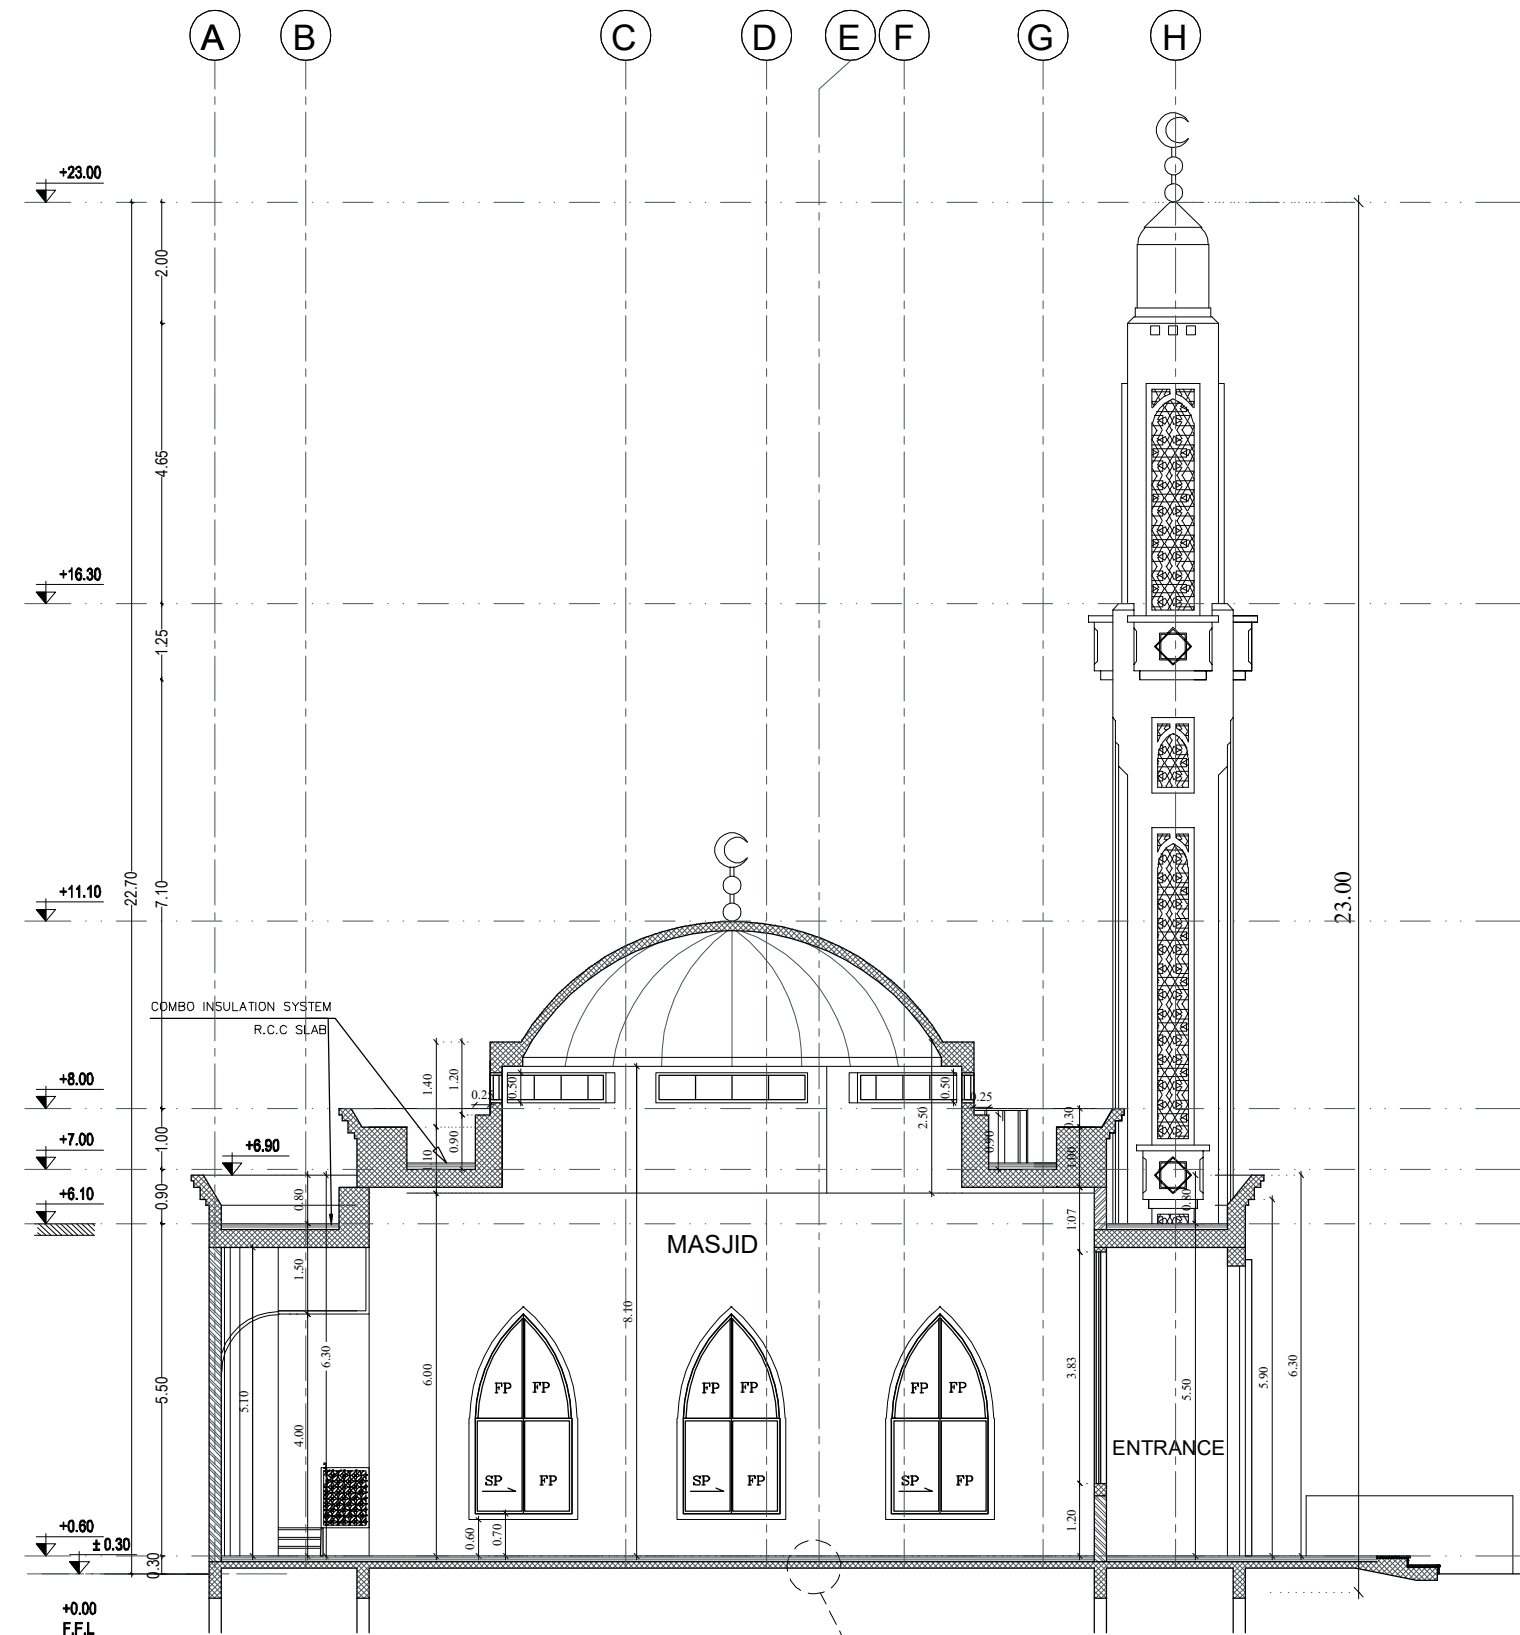

MASJID SECTION Y-Y

SCALE : 1:125

- SKIRTING AS PER SCHEDULE
- TILES AS PER SCHEDULE
- MORTAR
- 10cm THICK CONCRETE,
WITH 8mm MESH STEEL 150mm C/C
- 1000 GAUGE POLYTHENE SHEET
- ANTI TERMITE TREATMENT
- COMPACTED AND TESTED FILLING LAYER

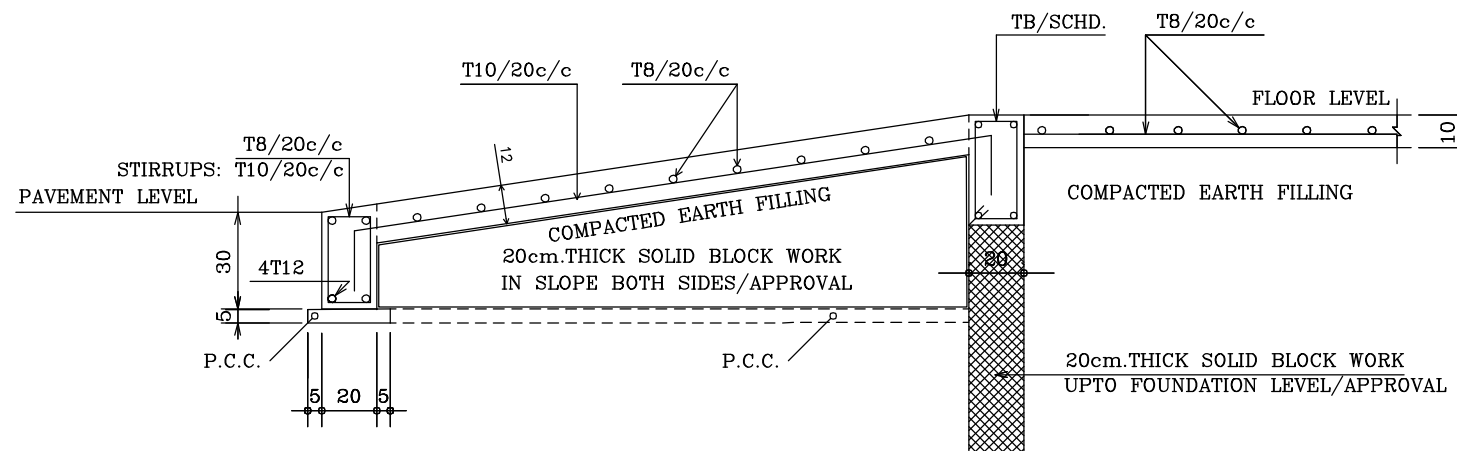

RAMP DETAIL

- * NOTES :-**
- 1- ALL EXTERNAL WALLS TO BE 20.cm THERMAL BLOCK.
 - 2- WINDOWS TO BE DOUBLE REFLECTIVE GLASS

GENERAL NOTES:

- 1.IT IS NOT ALLOWED TO REPRODUCE THE SHEETS CONTENTS IN ANY FORM EXCEPT FOR THE PURPOSE FOR WHICH IT IS INTENDED.
2. THESE DRAWINGS ARE DIAGRAMMATIC AND SHALL NOT BE SCALED. ADDITIONAL DATA SHALL BE REQUESTED FROM THE CONSULTANCY THROUGH WRITTEN CLARIFICATION. VERIFY ALL EXISTING CONDITIONS AND DIMENSIONS BEFORE PROCEEDING WITH ANY PORTION OF ANY WORK.
3. NO CHANGES, MODIFICATIONS OR DEVIATIONS SHALL BE WRITTEN PERMISSION FROM **ALMASAH ENGINEERING CONSULTANTS**.
4. ALL WORK AS OUTLINED IN THESE DOCUMENTS, SHALL STRICTLY CONFORM TO ALL APPLICABLE CODES. IN THE EVENT OF A CONFLICT, THE MORE STRINGENT REQUIREMENT SHALL GOVERN AND BE MET.



SIA - SM-06



حكومة الشارقة
دائرة الشؤون الإسلامية

CONSULTANT STAMP



CLIENT:

**GOVERNMENT OF SHARJAH -
DEPARTMENT OF ISLAMIC AFFAIRS**


PROJECT:

**(SIA - SM-06)
PROPOSED MASJID + ABLUTION +
IMAM HOUSE**


SHEET TITLE:

SECTIONS X-X & Y-Y





ARCHITECT Arch. Mostafa Ramadan	TYPE ARCHITECTURE
STRUCTURAL Eng : Mohamed Gomaa	SHEET No. A- 07
CHECKED BY Eng : Mohamed Attia	Location : Plot No : Project No :
SCALE 1:100	DATE November - 2021

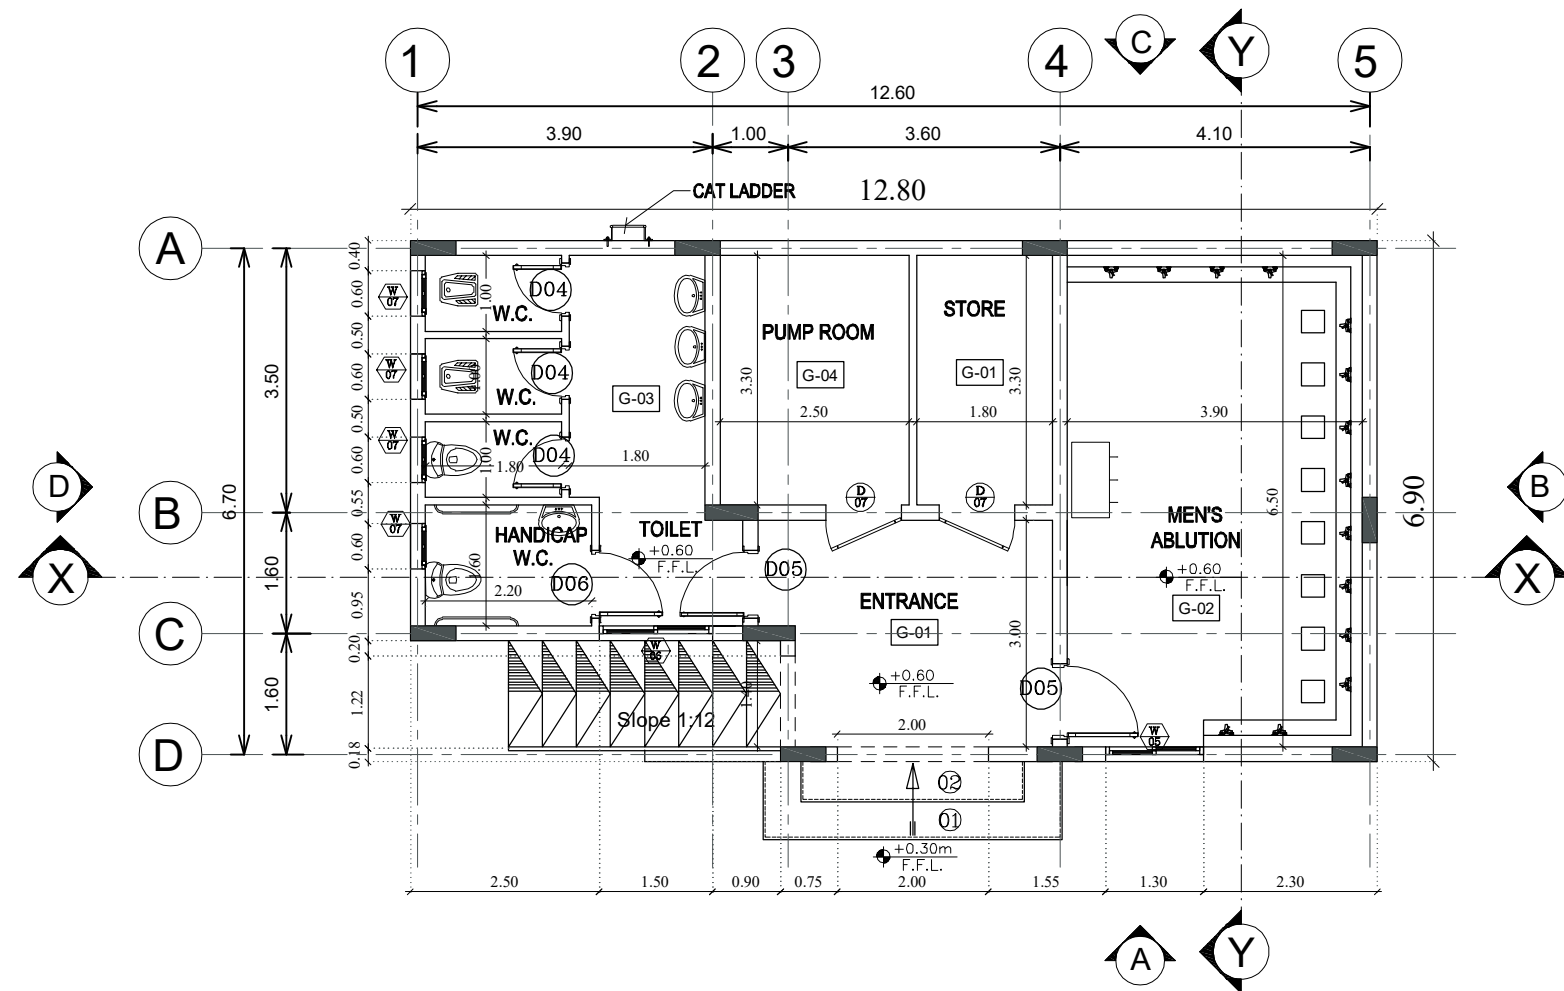

1 ABLUTION BLOCK GROUND FLOOR PLAN
SCALE : 1:100

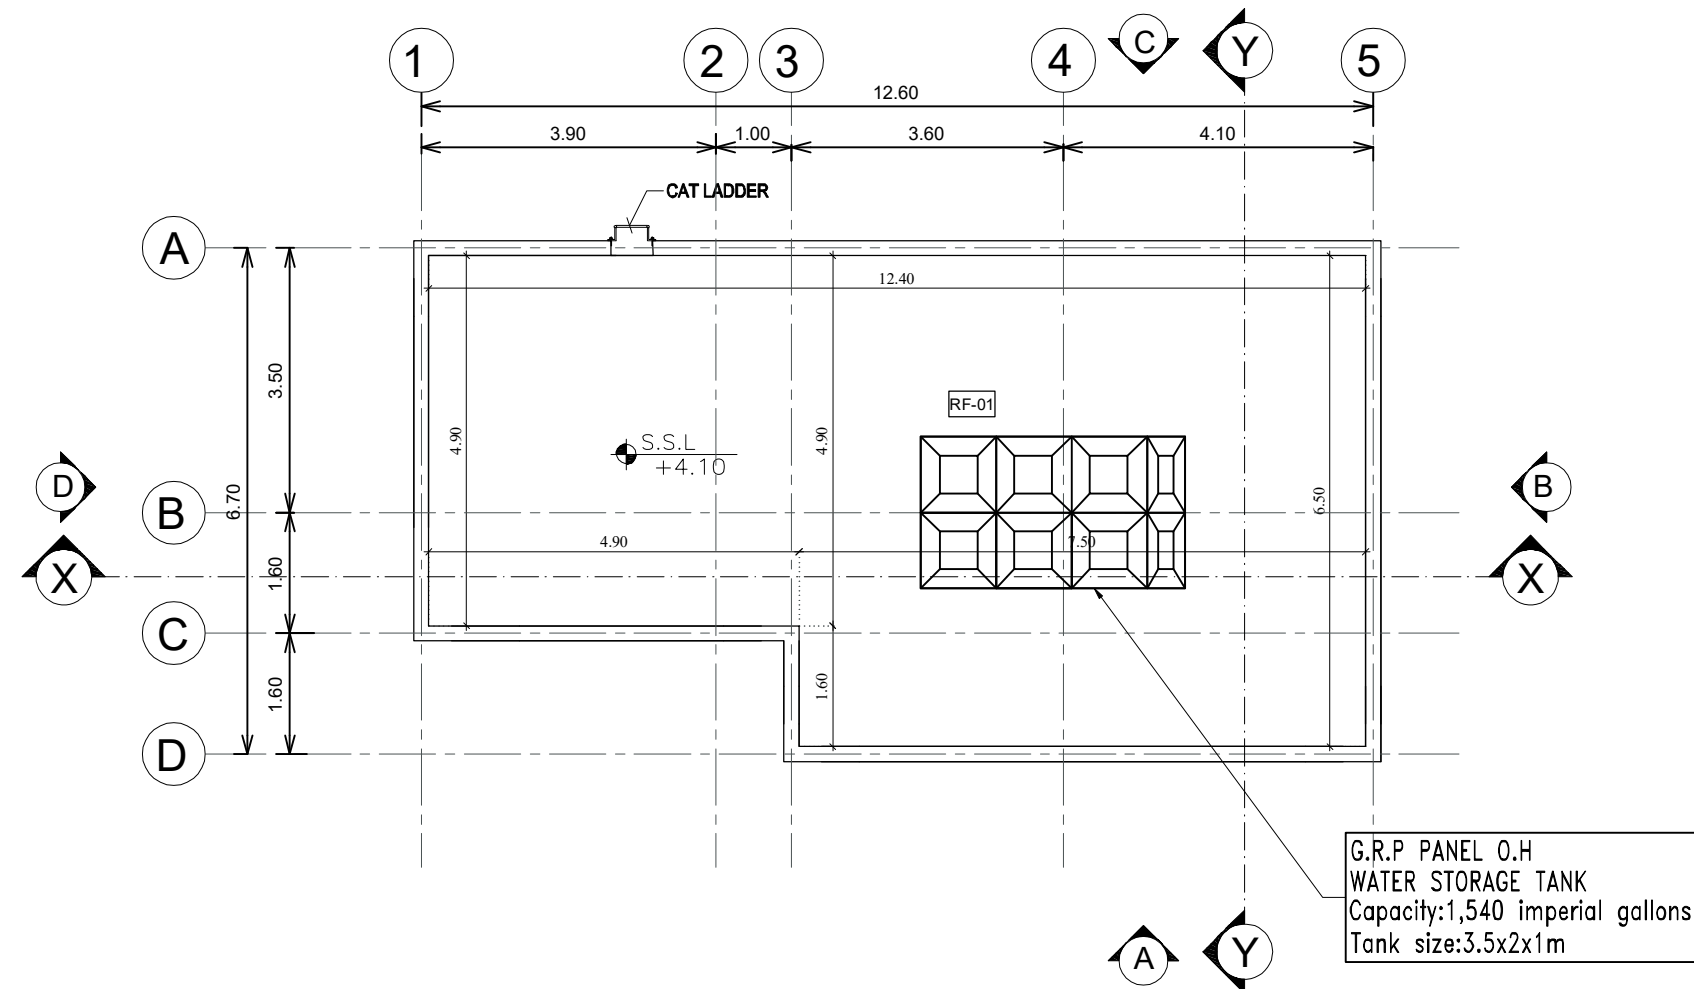

1 ABLUTION BLOCK ROOF PLAN
SCALE : 1:100

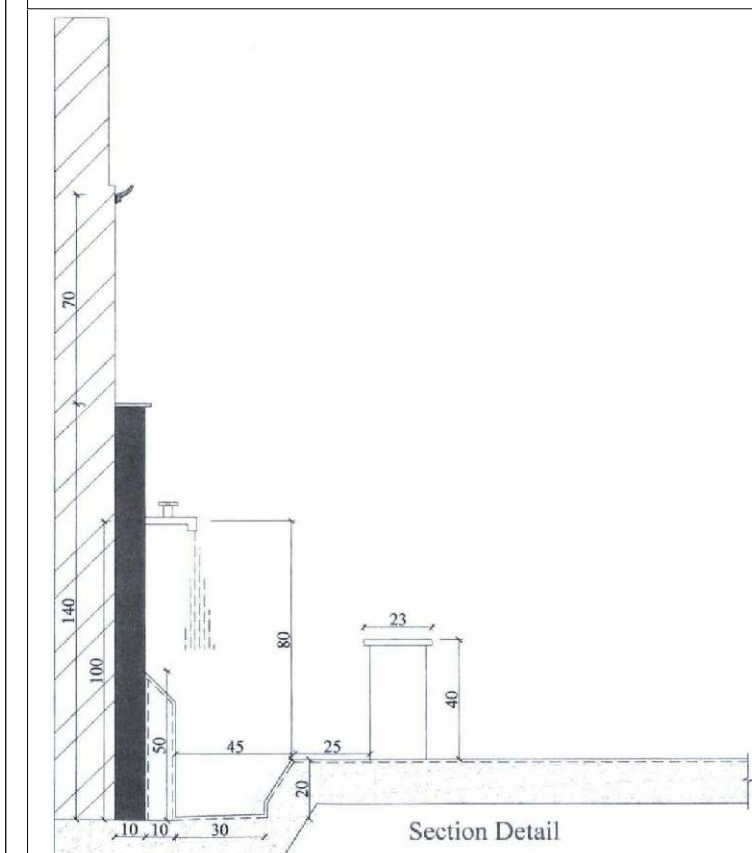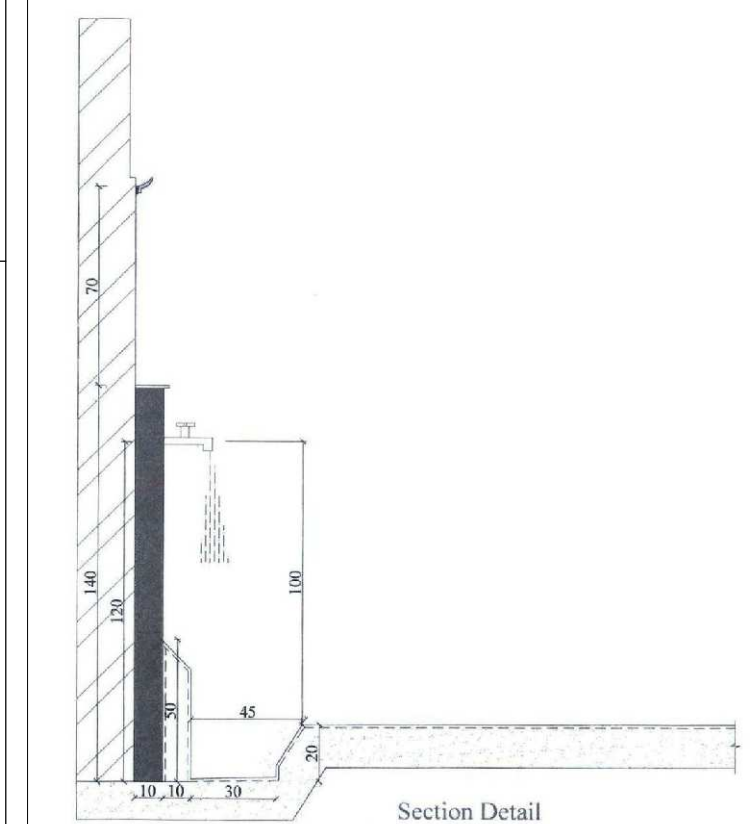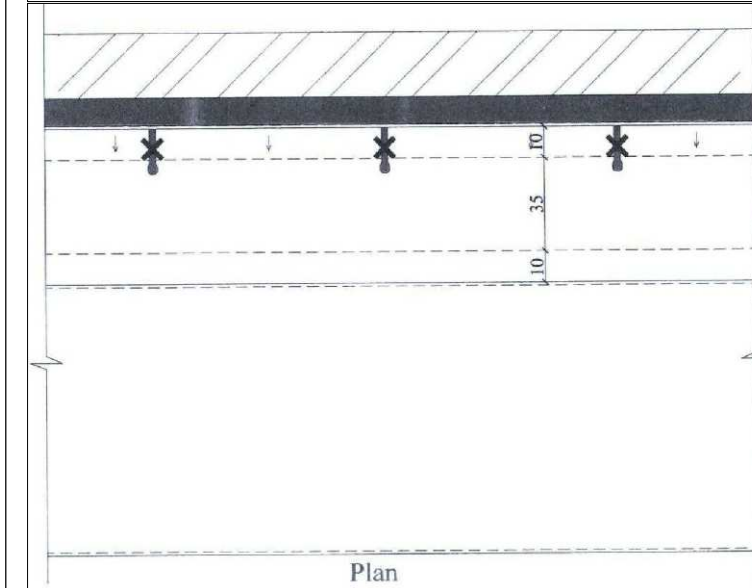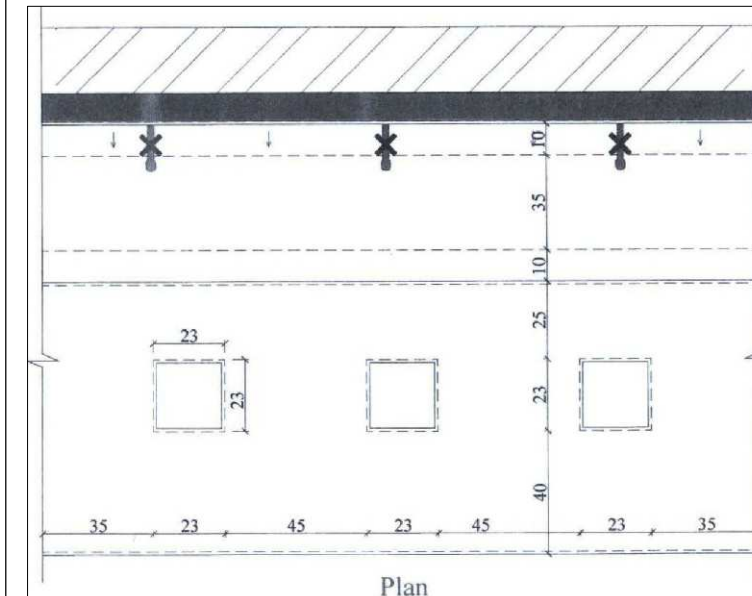

- GENERAL NOTES:**
1. IT IS NOT ALLOWED TO REPRODUCE THE SHEETS CONTENTS IN ANY FORM EXCEPT FOR THE PURPOSE FOR WHICH IT IS INTENDED.
 2. THESE DRAWINGS ARE DIAGRAMMATIC AND SHALL NOT BE SCALED. ADDITIONAL DATA SHALL BE REQUESTED FROM THE CONSULTANCY THROUGH WRITTEN CLARIFICATION. VERIFY ALL EXISTING CONDITIONS AND DIMENSIONS BEFORE PROCEEDING WITH ANY PORTION OF ANY WORK.
 3. NO CHANGES, MODIFICATIONS OR DEVIATIONS SHALL BE WRITTEN PERMISSION FROM **ALMASAH ENGINEERING CONSULTANTS**.
 4. ALL WORK AS OUTLINED IN THESE DOCUMENTS, SHALL STRICTLY CONFORM TO ALL APPLICABLE CODES. IN THE EVENT OF A CONFLICT, THE MORE STRINGENT REQUIREMENT SHALL GOVERN AND BE MET.



SIA - SM-06



حُكُومَةُ الشَّارِجَةِ
دائرة الشؤون الإسلامية

CONSULTANT STAMP




CLIENT: **GOVERNMENT OF SHARJAH -
DEPARTMENT OF ISLAMIC AFFAIRS**

PROJECT: **(SIA - SM-06)
PROPOSED MASJID + ABLUTION +
IMAM HOUSE**


SHEET TITLE: **ABLUTION
GROUND & ROOF FLOOR PLANS**

ARCHITECT Arch. Mostafa Ramadan	TYPE ARCHITECTURE	
STRUCTURAL Eng : Mohamed Gomaa	SHEET No.	A - 08
CHECKED BY Eng : Mohamed Attia	Location :	
SCALE 1:100	DATE November - 2021	Project No.

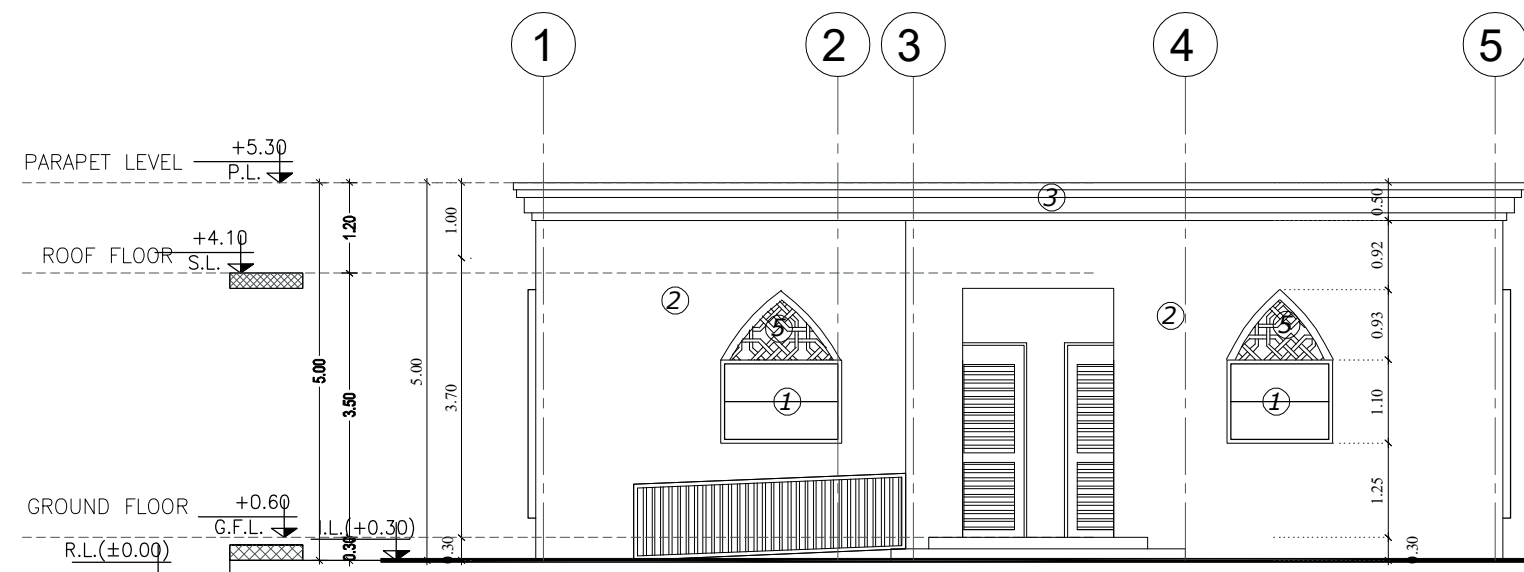

1 ABLUTION BLOCK ELEVATION A

SCALE : 1:100

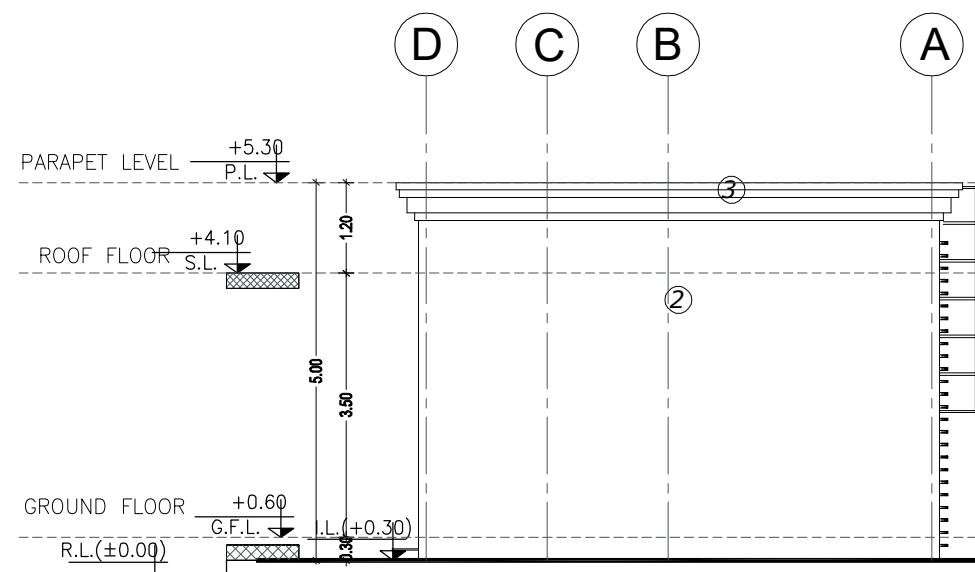


1 ABLUTION BLOCK ELEVATION B

SCALE : 1:100

ELEVATION FINISHES


- 1- REFLECTIVE GLASS
- 2- GRAFFIO DECOR WHITE PAINT OR STONE CLADDING
- 3- GRAFFIO DECOR OFF WHITE PAINT OR STONE CLADDING
- 4- GRANITE FINISHING
- 5- G.R.C.

ALL WINDOWS & BALCONY DOORS SHOULD BE EQUIPED WITH WINDOWS OPENING CONTROL DEVICE (W.O.C.D.) TO LIMITS THE OPENING LESS THAN 10 CM TO HAVE MAXIMUM OPENING LIMIT OF 10 CM TO HELP IN THE PREVENTION OF ACCIDENTAL FALLS FROM WINDOWS & BALCONIES BY CHILDREN AS PER SHARJAH MUNICIPALITY REGULATIONS.

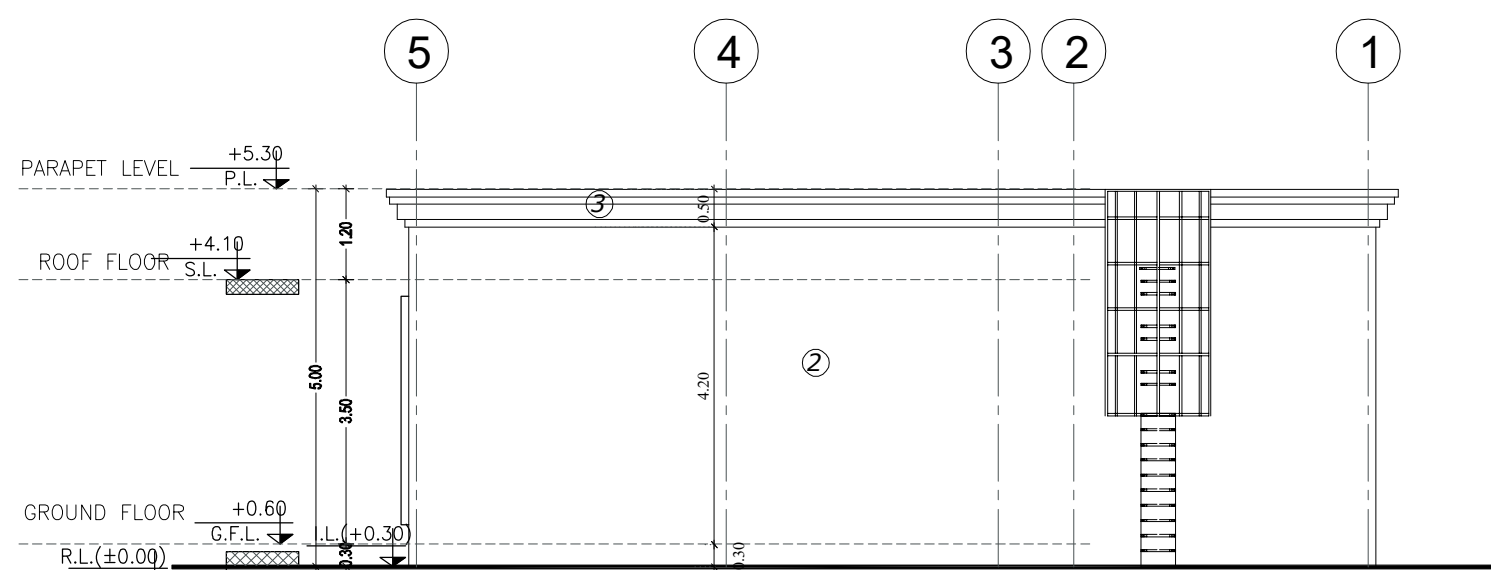


1 ABLUTION BLOCK ELEVATION C

SCALE : 1:100

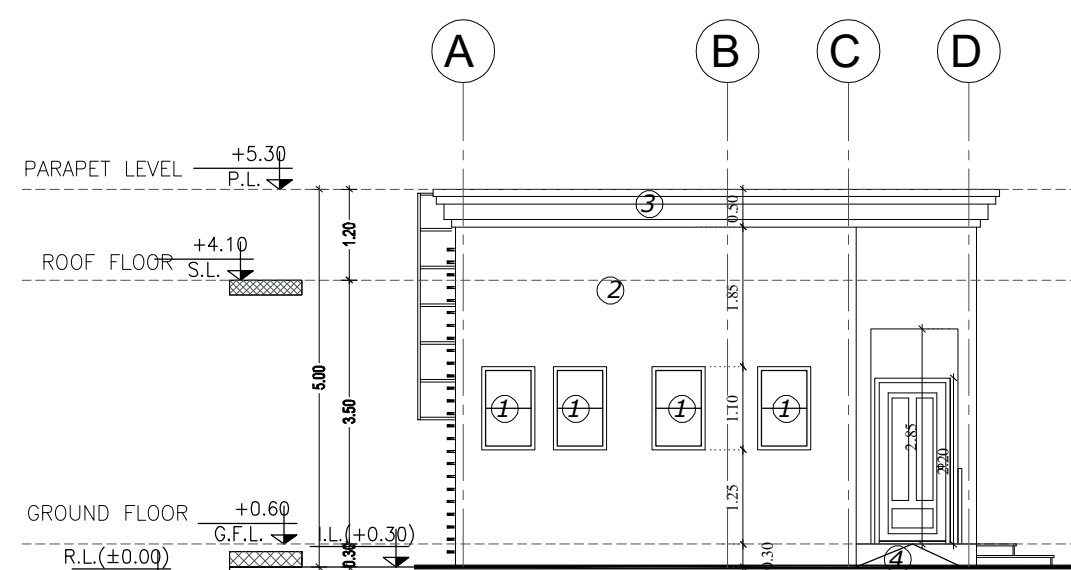

1 ABLUTION BLOCK ELEVATION D


SCALE : 1:100

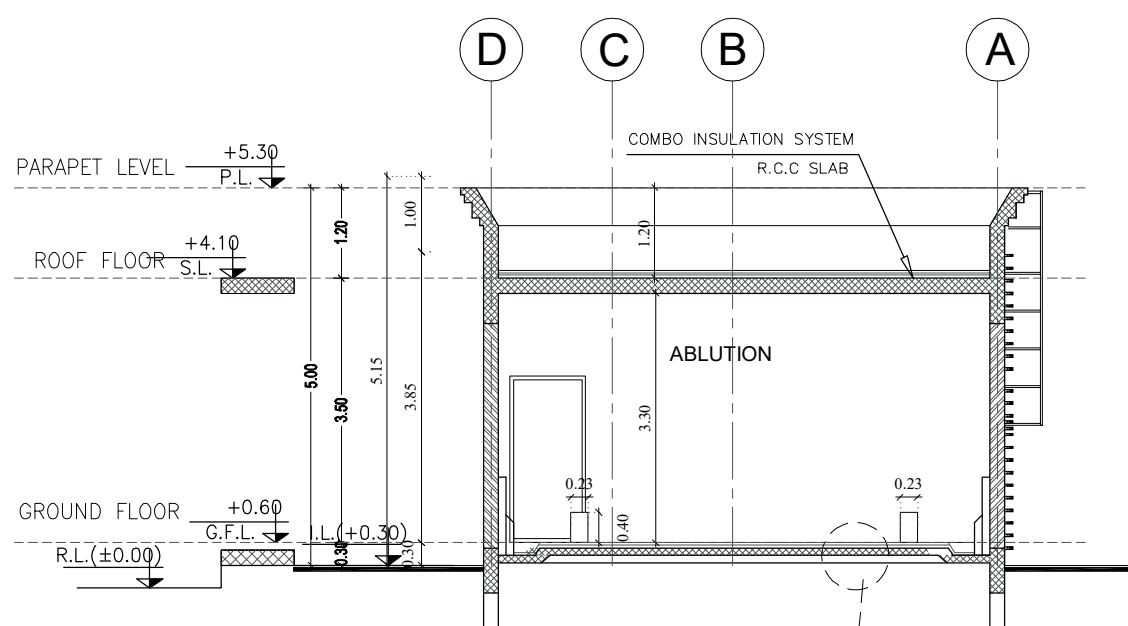

1 ABLUTION BLOCK SECTION Y-Y

SCALE : 1:100

- SKIRTING AS PER SCHEDULE
- TILES AS PER SCHEDULE
- MORTAR
- 10cm THICK CONCRETE, WITH 8mm MESH STEEL 150mm C/C
- 1000 GAUGE POLYTHENE SHEET
- ANTI TERMITE TREATMENT
- COMPACTED AND TESTED FILLING LAYER

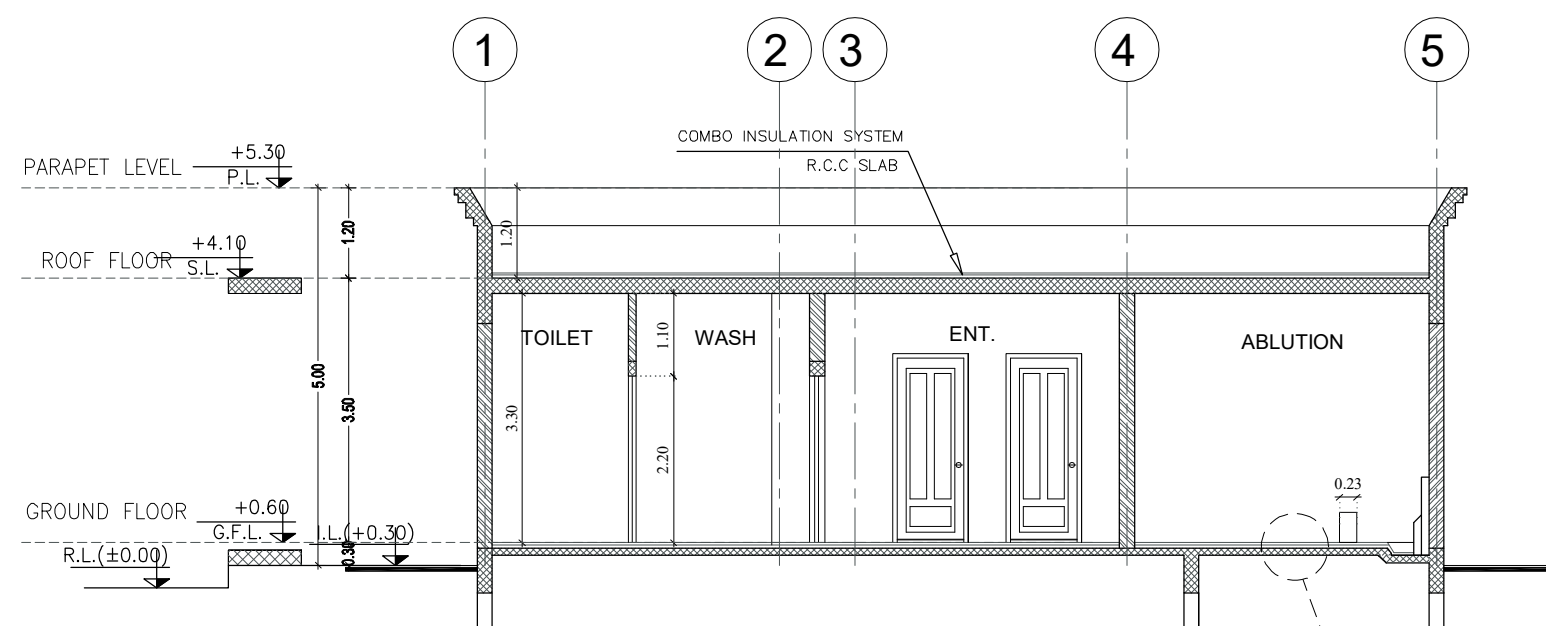

1 ABLUTION BLOCK SECTION X-X

SCALE : 1:100

- SKIRTING AS PER SCHEDULE
- TILES AS PER SCHEDULE
- MORTAR
- 10cm THICK CONCRETE, WITH 8mm MESH STEEL 150mm C/C
- 1000 GAUGE POLYTHENE SHEET
- ANTI TERMITE TREATMENT
- COMPACTED AND TESTED FILLING LAYER

GENERAL NOTES:

- 1.IT IS NOT ALLOWED TO REPRODUCE THE SHEETS CONTENTS IN ANY FORM EXCEPT FOR THE PURPOSE FOR WHICH IT IS INTENDED.
2. THESE DRAWINGS ARE DIAGRAMMATIC AND SHALL NOT BE SCALED. ADDITIONAL DATA SHALL BE REQUESTED FROM THE CONSULTANCY THROUGH WRITTEN CLARIFICATION. VERIFY ALL EXISTING CONDITIONS AND DIMENSIONS BEFORE PROCEEDING WITH ANY PORTION OF ANY WORK.
3. NO CHANGES, MODIFICATIONS OR DEVIATIONS SHALL BE WRITTEN PERMISSION FROM **ALMASAH ENGINEERING CONSULTANTS**.
4. ALL WORK AS OUTLINED IN THESE DOCUMENTS, SHALL STRICTLY CONFORM TO ALL APPLICABLE CODES. IN THE EVENT OF A CONFLICT, THE MORE STRINGENT REQUIREMENT SHALL GOVERN AND BE MET.



SIA - SM-06



حكومة الشارقة
دائرة الشؤون الإسلامية

CONSULTANT STAMP



Sharjah ☎ 06 5 444 521 ☎ 06 5 444 523 Office: 306, Al Fisal 2 Bldg., King Fisal St.

CLIENT:

GOVERNMENT OF SHARJAH -
DEPARTMENT OF ISLAMIC AFFAIRS


PROJECT:

(SIA - SM-06)
PROPOSED MASJID + ABLUTION +
IMAM HOUSE

SHEET TITLE:


ABLUTION
ELEVATIONS & SECTIONS

ARCHITECT Arch. Mostafa Ramadan	TYPE ARCHITECTURE
STRUCTURAL Eng : Mohamed Gomaa	SHEET No. A - 09
CHECKED BY Eng : Mohamed Attia	Location : Plot No :
SCALE 1:100	DATE November - 2021
	Project No.

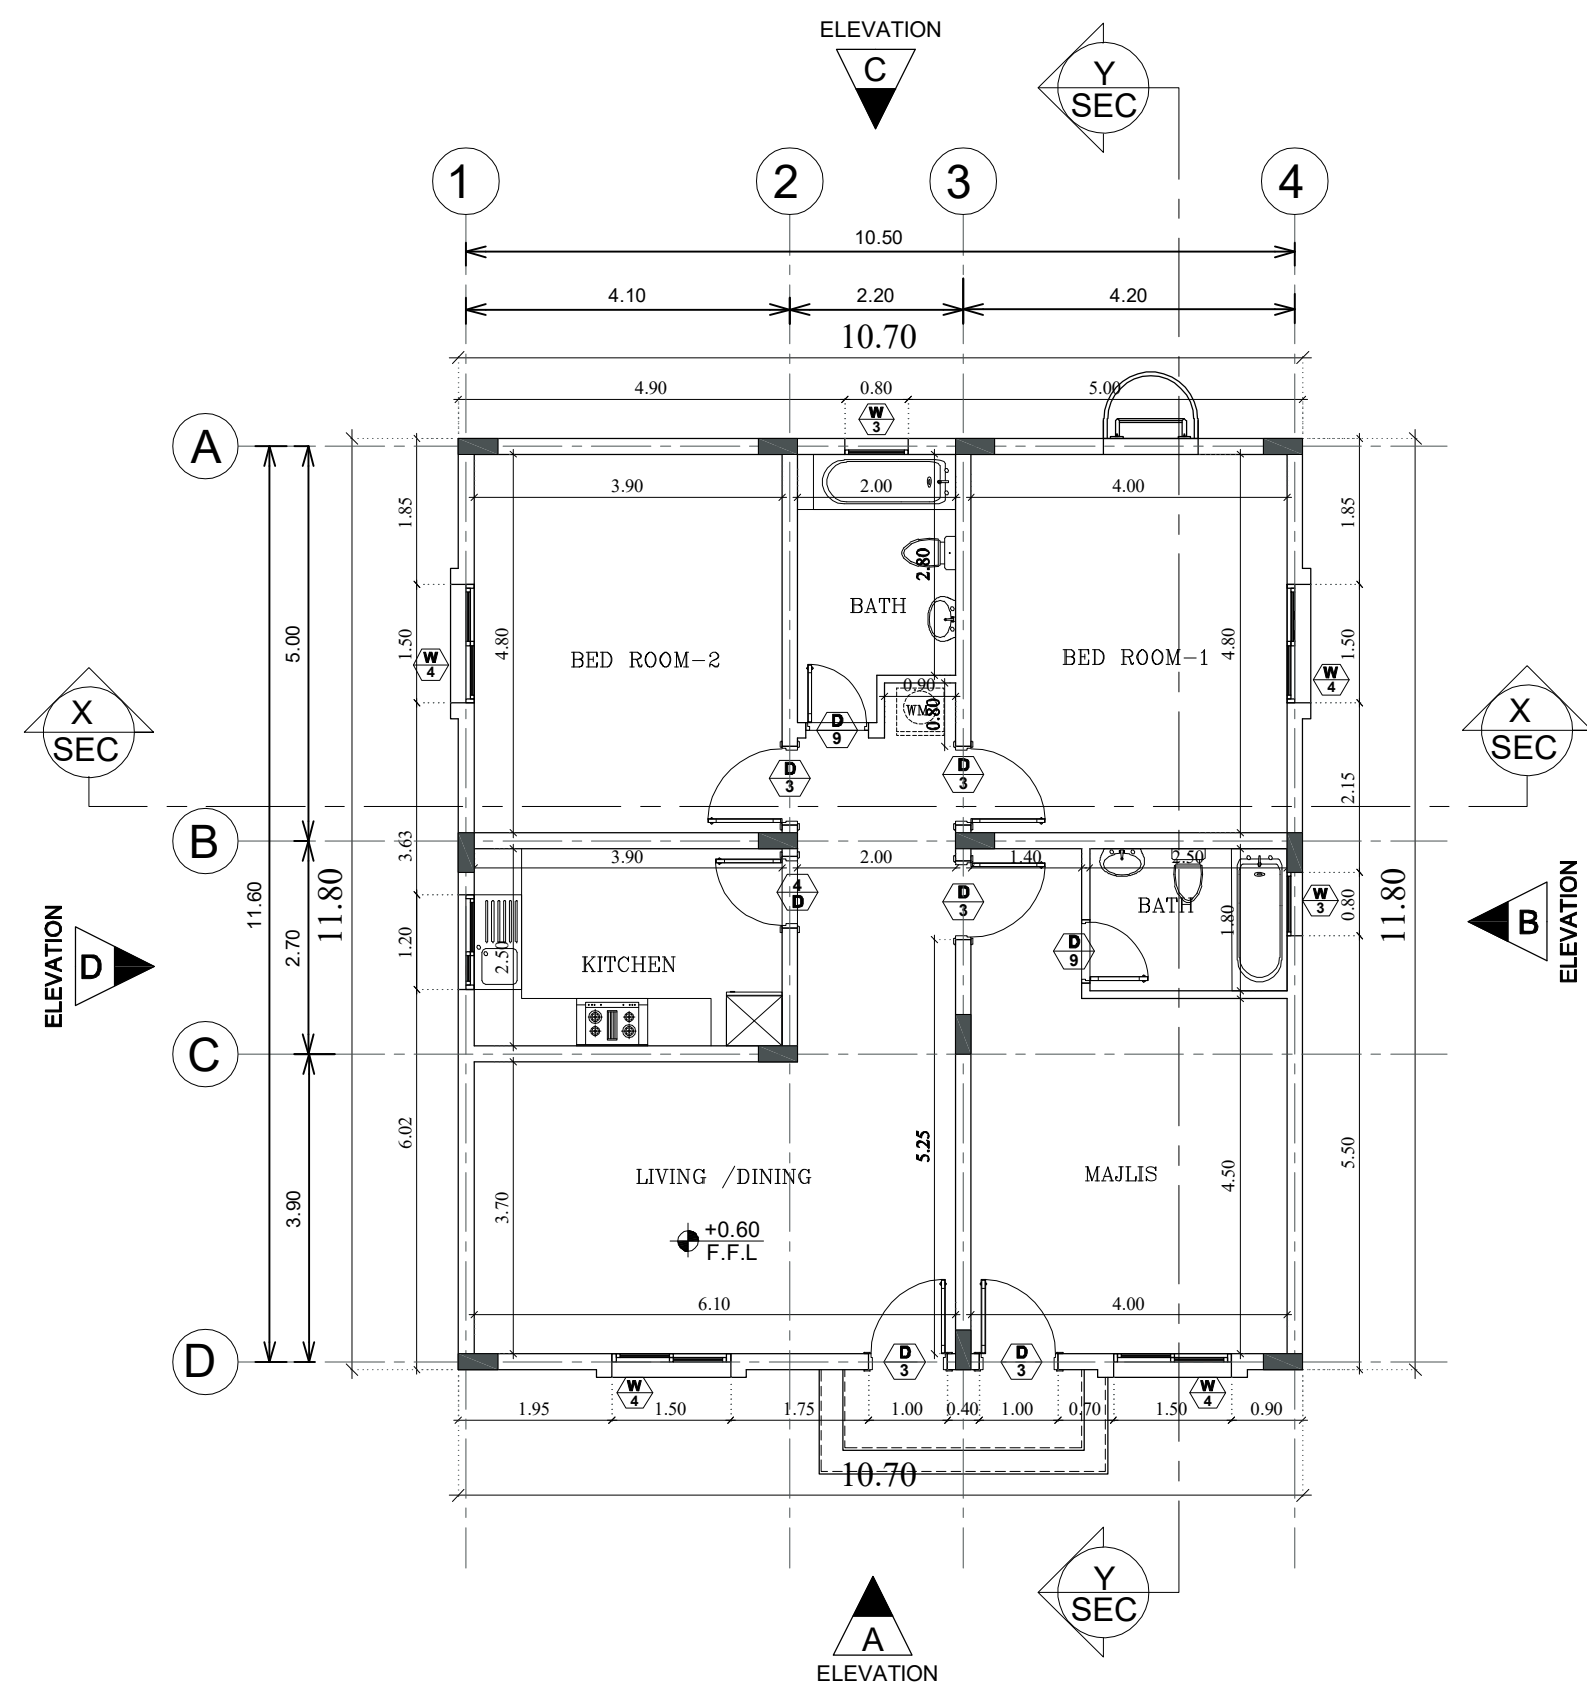

GROUND FLOOR PLAN

(SCALE = 1 : 100)

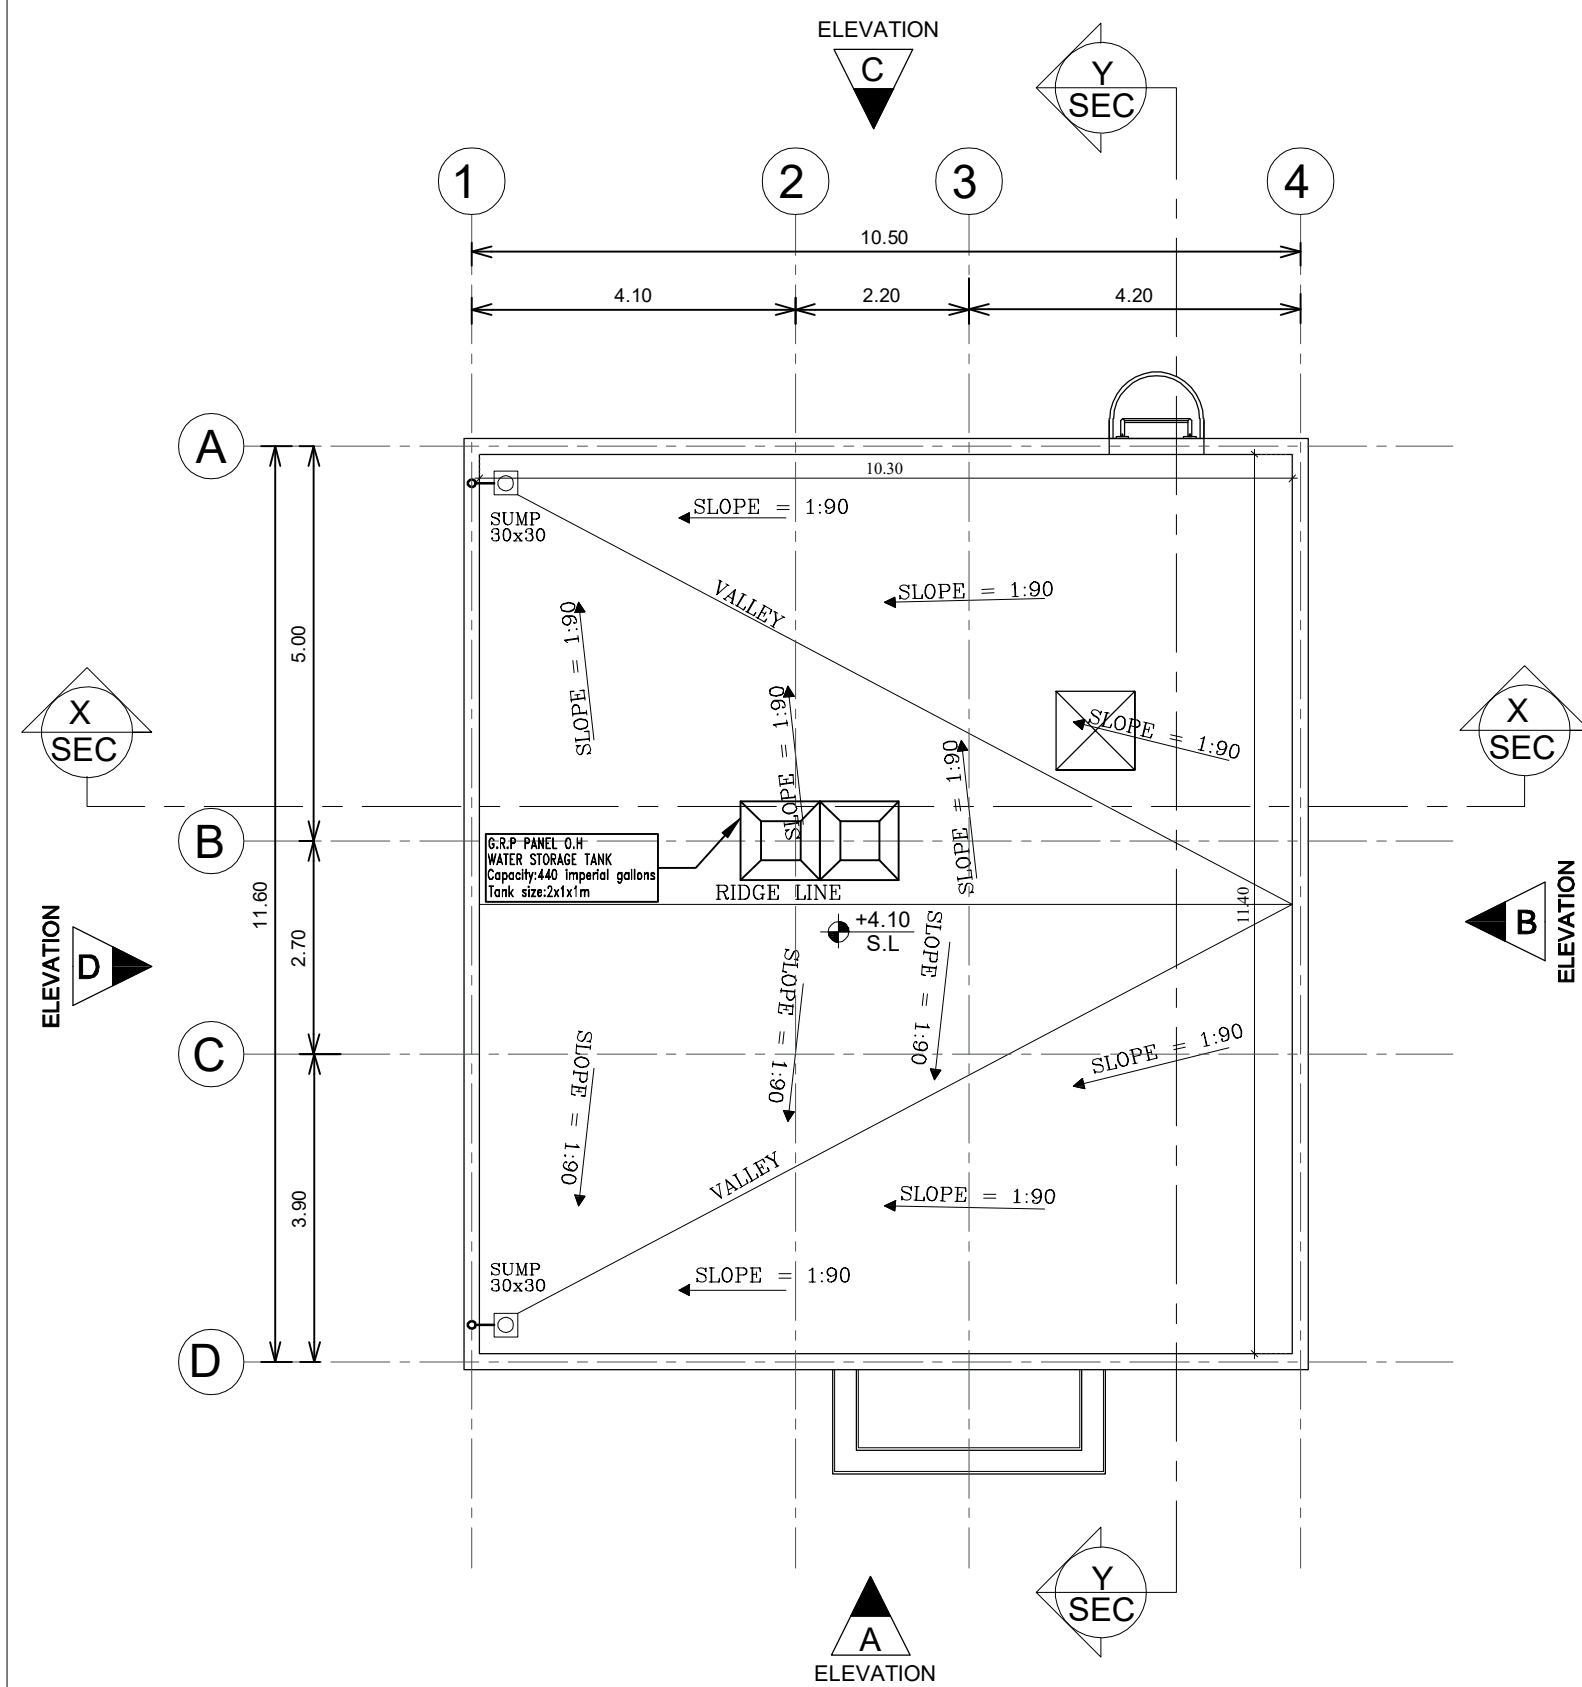

ROOF FLOOR PLAN

(SCALE = 1 : 100)

GENERAL NOTES:

1. IT IS NOT ALLOWED TO REPRODUCE THE SHEETS CONTENTS IN ANY FORM EXCEPT FOR THE PURPOSE FOR WHICH IT IS INTENDED.
2. THESE DRAWINGS ARE DIAGRAMMATIC AND SHALL NOT BE SCALED. ADDITIONAL DATA SHALL BE REQUESTED FROM THE CONSULTANCY THROUGH WRITTEN CLARIFICATION. VERIFY ALL EXISTING CONDITIONS AND DIMENSIONS BEFORE PROCEEDING WITH ANY PORTION OF ANY WORK.
3. NO CHANGES, MODIFICATIONS OR DEVIATIONS SHALL BE WRITTEN PERMISSION FROM **ALMASAH ENGINEERING CONSULTANTS**.
4. ALL WORK AS OUTLINED IN THESE DOCUMENTS, SHALL STRICTLY CONFORM TO ALL APPLICABLE CODES. IN THE EVENT OF A CONFLICT, THE MORE STRINGENT REQUIREMENT SHALL GOVERN AND BE MET.



SIA - MS-06



حكومة الشارقة
دائرة الشؤون الإسلامية

CONSULTANT STAMP



Sharjah ☎ 06 5 444 521 ☎ 06 5 444 523 📍 Office: 306, Al Fisal 2 Bldg., King Fisal St.

CLIENT:

GOVERNMENT OF SHARJAH -
DEPARTMENT OF ISLAMIC AFFAIRS

PROJECT:

(SIA - MS-06)
PROPOSED MASJID + ABLUTION +
IMAM HOUSE

SHEET TITLE:

IMAM HOUSE
GROUND & ROOF FLOOR PLAN

ARCHITECT

Arch. Mostafa Ramadan

TYPE

ARCHITECTURE

STRUCTURAL

Eng : Mohamed Goma

SHEET

No.

A - 10

CHECKED BY

Eng : Mohamed Attia

Location :

Plot No :

SCALE


1:100

DATE


July - 2021

Project

No.

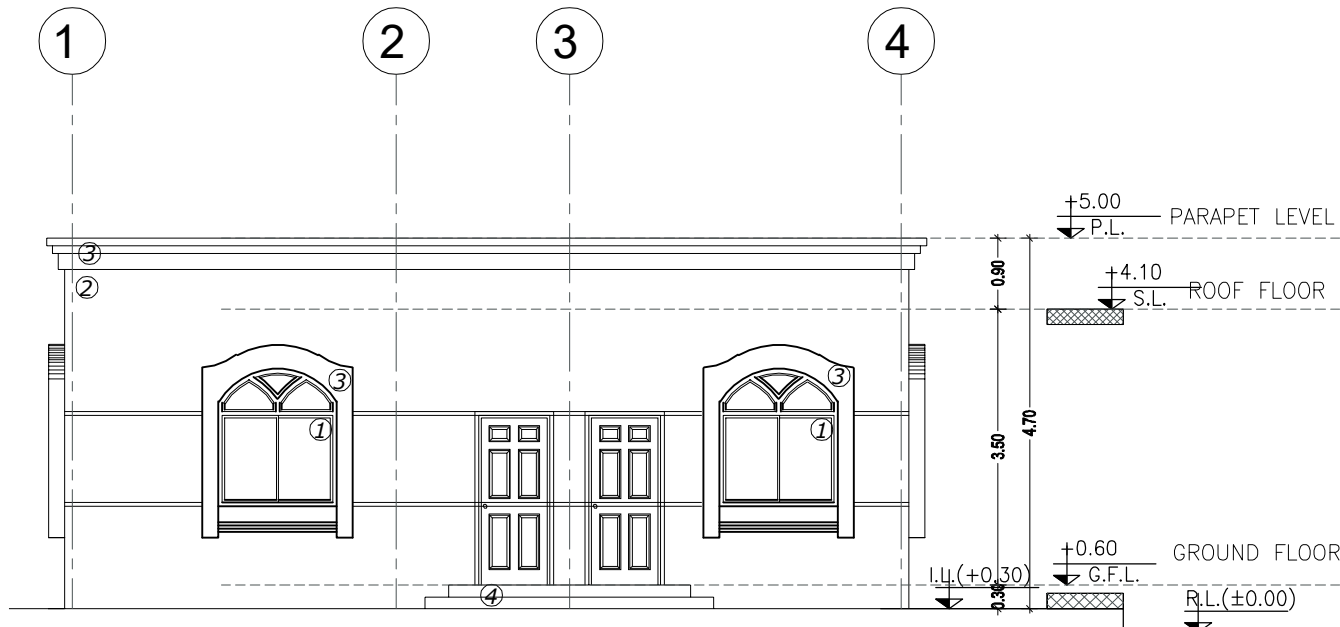

ELEVATION -A
(SCALE = 1 : 100)

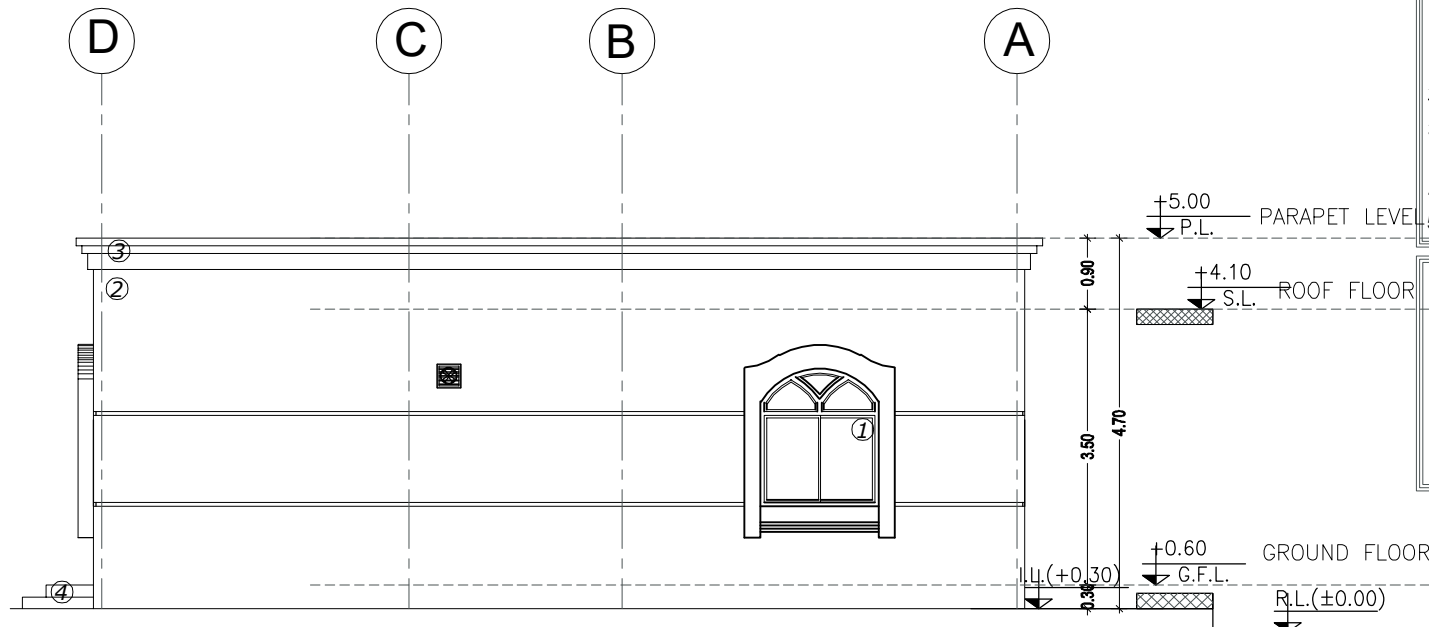


ELEVATION -B
(SCALE = 1 : 100)

ELEVATION FINISHES


- 1- REFLECTIVE GLASS
- 2- GRAFFIO DECOR WHITE PAINT OR STONE CLADDING
- 3- GRAFFIO DECOR OFF WHITE PAINT OR STONE CLADDING
- 4- GRANITE FINISHING
- 5- G.R.C.

ALL WINDOWS & BALCONY DOORS SHOULD BE EQUIPED WITH WINDOWS OPENING CONTROL DEVICE (W.O.C.D.) TO LIMITS THE OPENING LESS THAN 10 CM TO HAVE MAXIMUM OPENING LIMIT OF 10 CM TO HELP IN THE PREVENTION OF ACCIDENTAL FALLS FROM WINDOWS & BALCONIES BY CHILDREN AS PER SHARJAH MUNICIPALITY REGULATIONS.

- GENERAL NOTES:**
- 1.IT IS NOT ALLOWED TO REPRODUCE THE SHEETS CONTENTS IN ANY FORM EXCEPT FOR THE PURPOSE FOR WHICH IT IS INTENDED.
 2. THESE DRAWINGS ARE DIAGRAMMATIC AND SHALL NOT BE SCALED. ADDITIONAL DATA SHALL BE REQUESTED FROM THE CONSULTANCY THROUGH WRITTEN CLARIFICATION. VERIFY ALL EXISTING CONDITIONS AND DIMENSIONS BEFORE PROCEEDING WITH ANY PORTION OF ANY WORK.
 3. NO CHANGES, MODIFICATIONS OR DEVIATIONS SHALL BE WRITTEN PERMISSION FROM **ALMASAH ENGINEERING CONSULTANTS**.
 4. ALL WORK AS OUTLINED IN THESE DOCUMENTS, SHALL STRICTLY CONFORM TO ALL APPLICABLE CODES. IN THE EVENT OF A CONFLICT, THE MORE STRINGENT REQUIREMENT SHALL GOVERN AND BE MET.


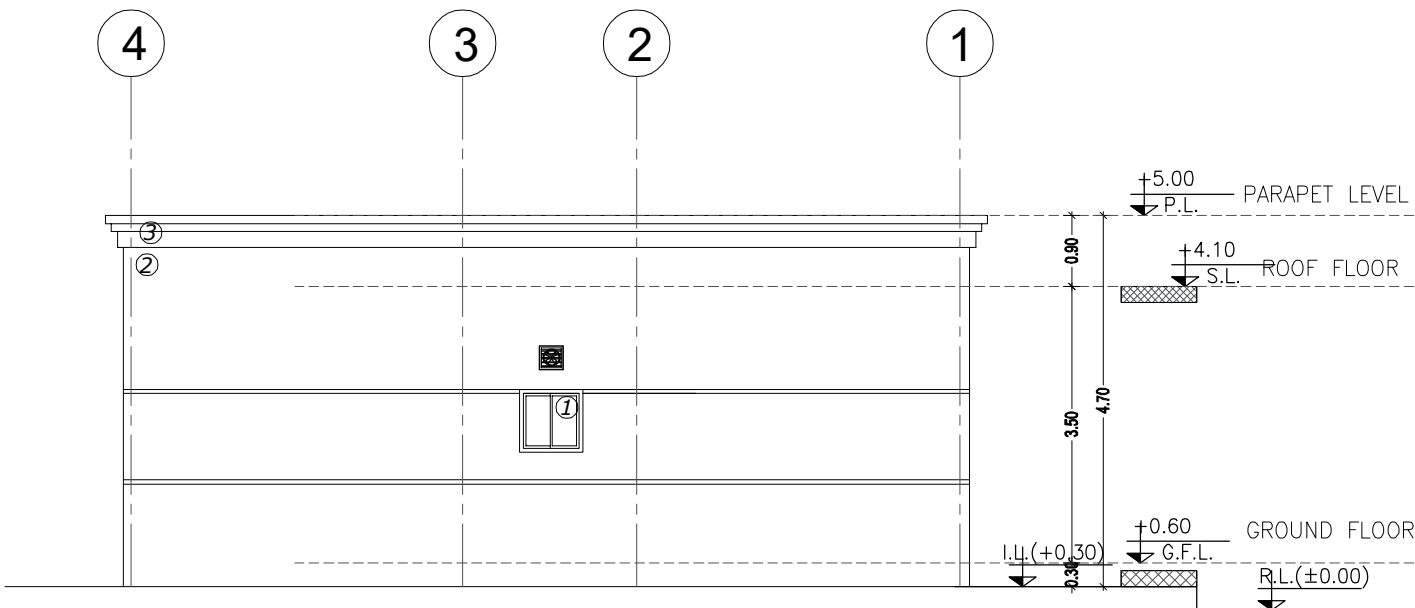


ELEVATION -C
(SCALE = 1 : 100)

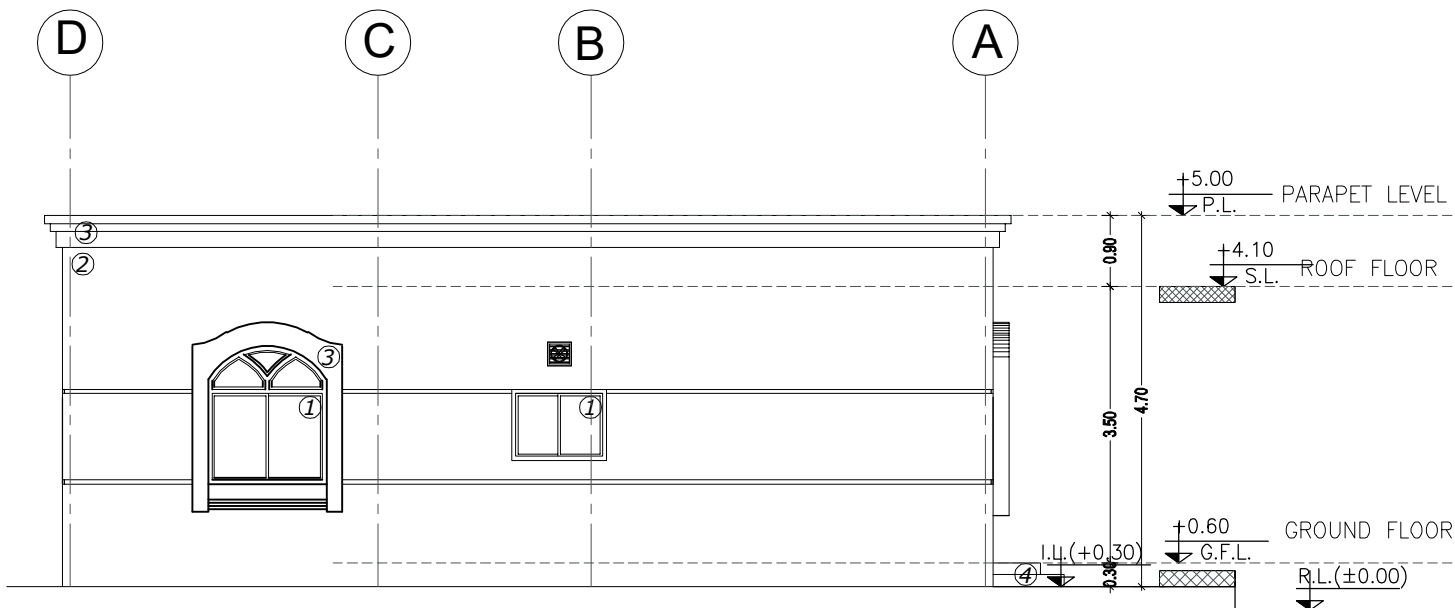


ELEVATION -D
(SCALE = 1 : 100)

- * NOTES :**
- 1- ALL EXTERNAL WALLS TO BE 20.cm THERMAL BLOCK.
 - 2- WINDOWS TO BE DOUBLE REFLECTIVE GLASS

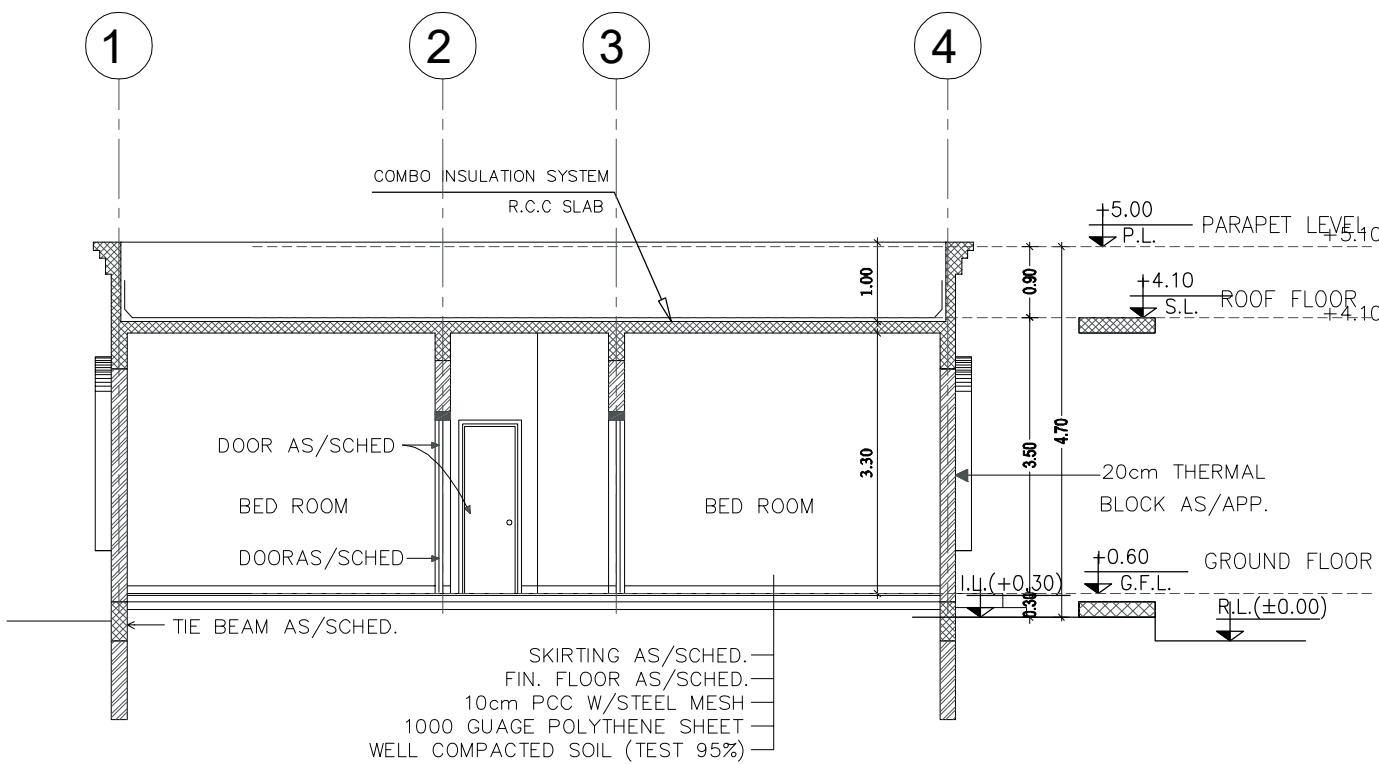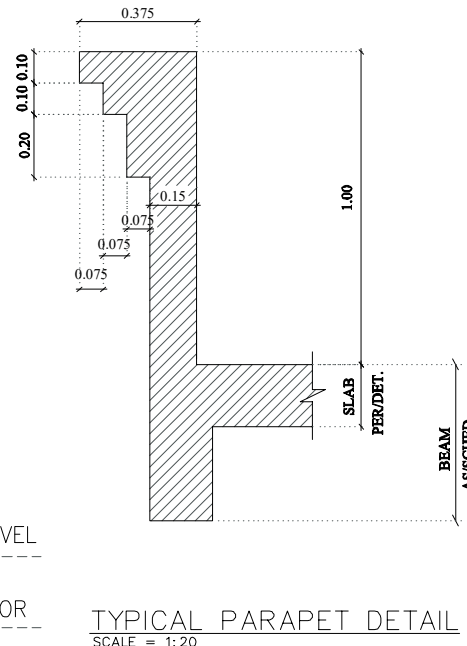

SECTION X-X
(SCALE = 1 : 100)

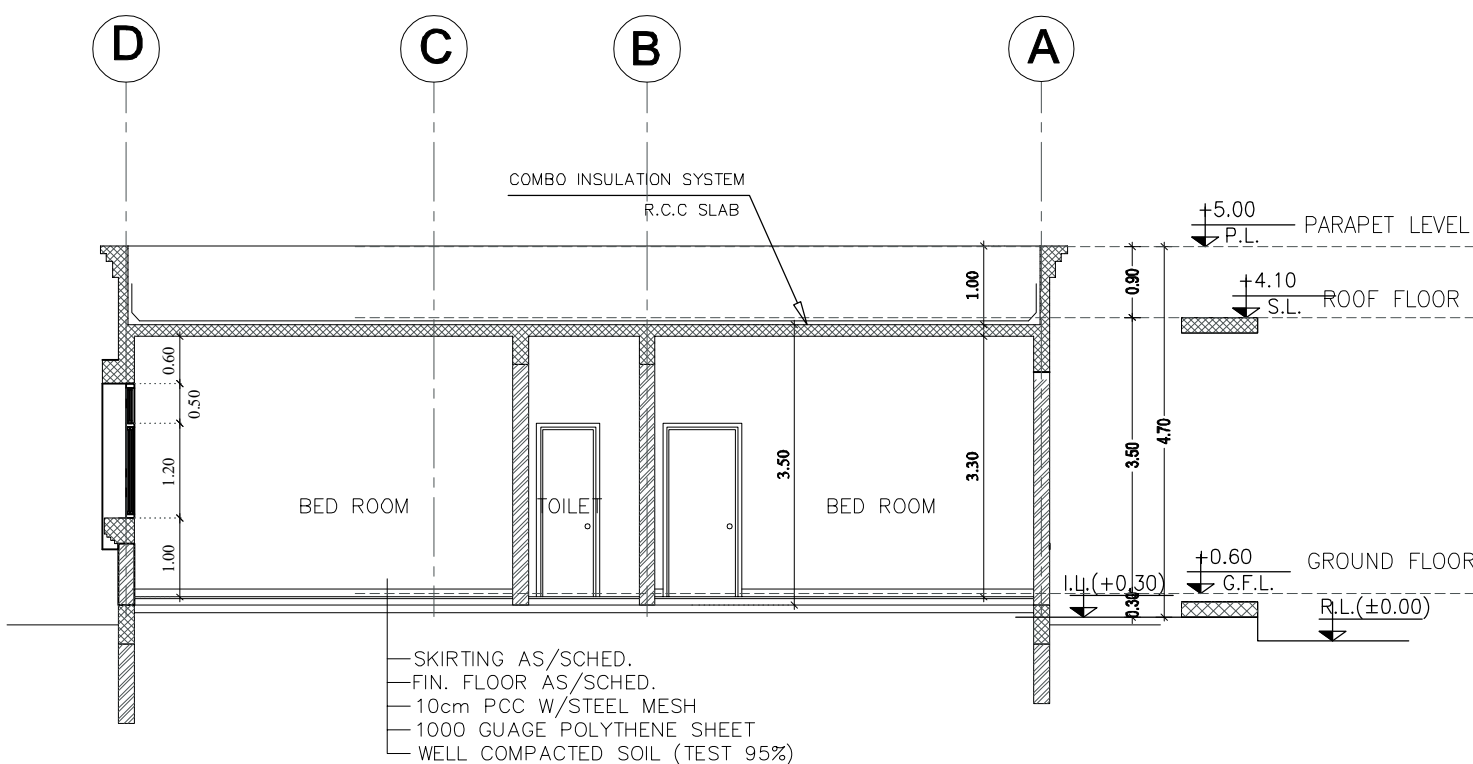

SECTION Y-Y
(SCALE = 1 : 100)

SIA - MS-06



حُكُومَةُ الشَّارِقَةِ
دائرة الشؤون الإسلامية

CONSULTANT STAMP




CLIENT: **GOVERNMENT OF SHARJAH -
DEPARTMENT OF ISLAMIC AFFAIRS**


PROJECT: **(SIA - MS-06)
PROPOSED MASJID + ABLUTION +
IMAM HOUSE**

SHEET TITLE: **IMAM HOUSE
ELEVATIONS & SECTION**


ARCHITECT Arch. Mostafa Ramadan	TYPE ARCHITECTURE
STRUCTURAL Eng : Mohamed Gomaa	SHEET No. A - 11
CHECKED BY Eng : Mohamed Attia	Location : Plot No :
SCALE 1:100	DATE July - 2021
	Project No.

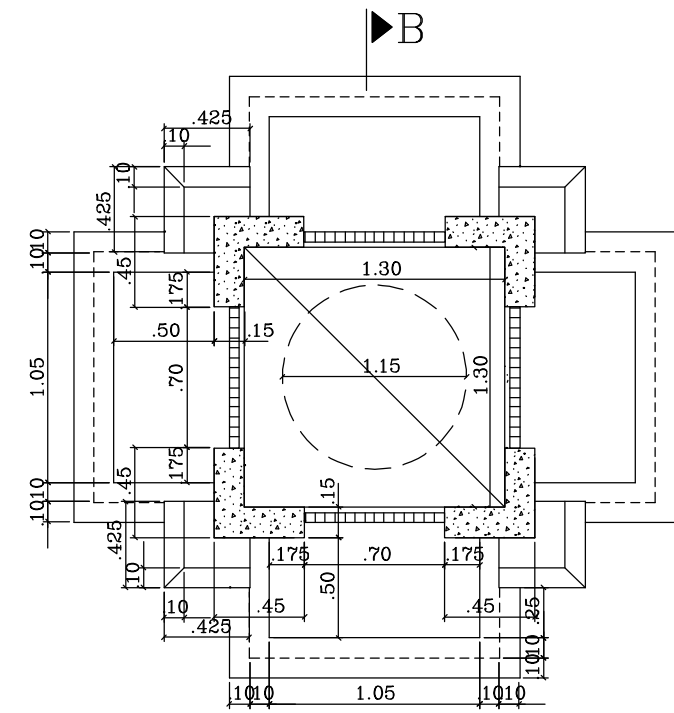


SECTION 4-4

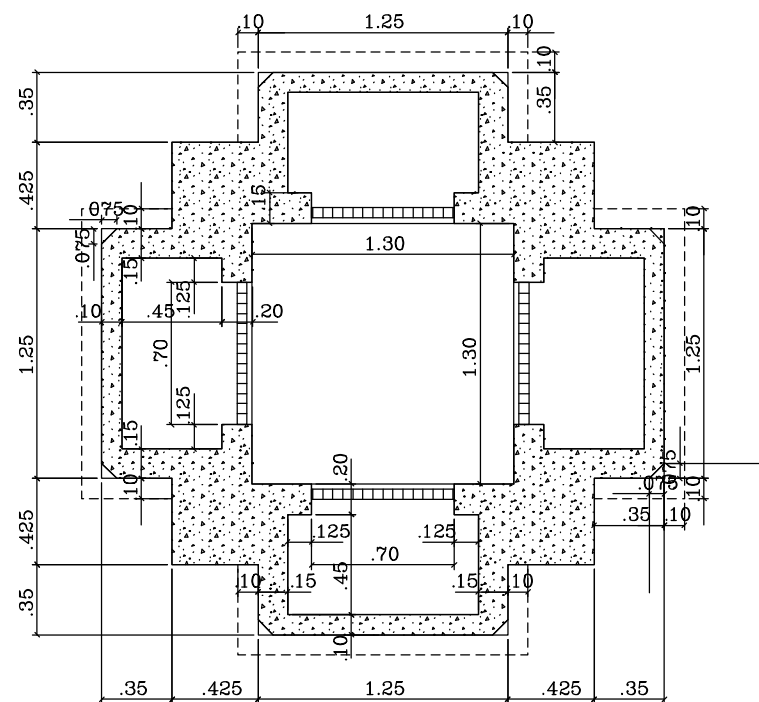


SECTION 3-3

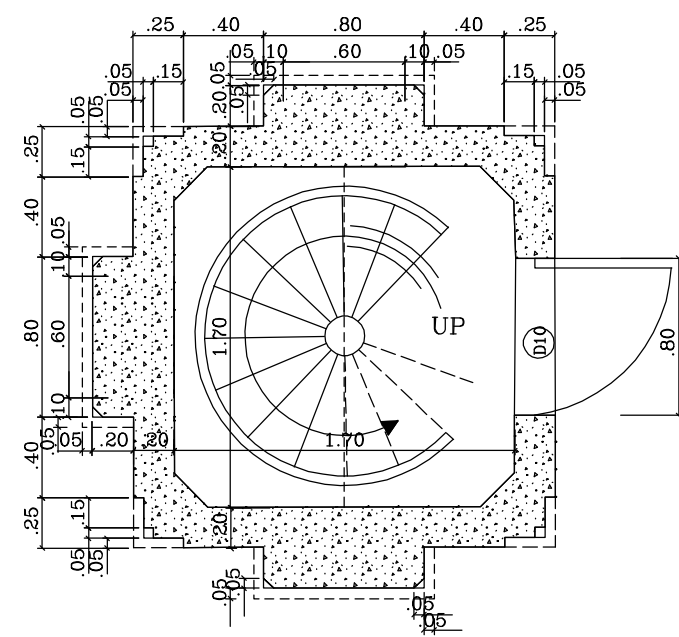


SECTION 2-2

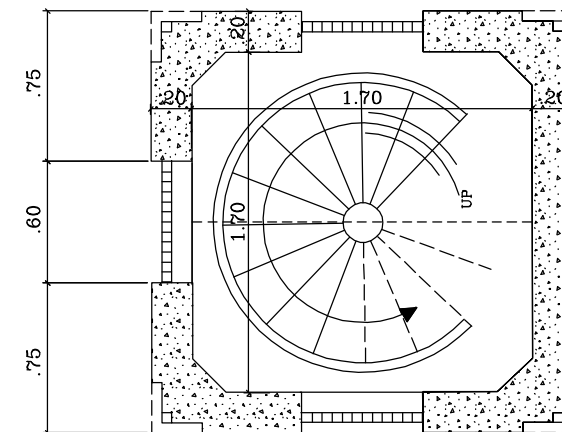

SECTION 1A-1A

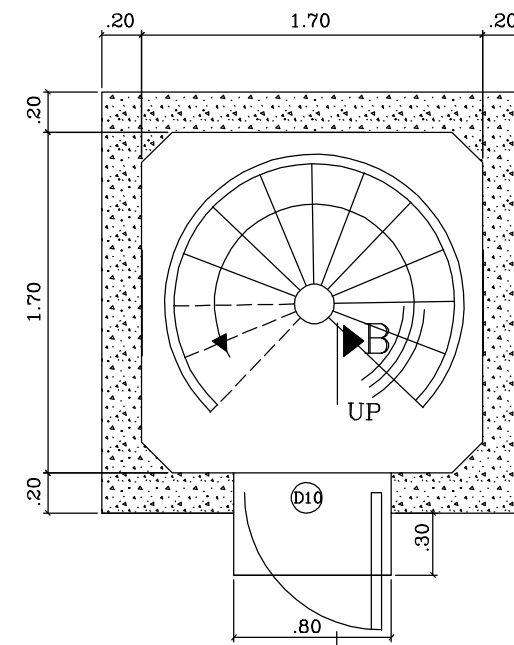

SECTION 1-1

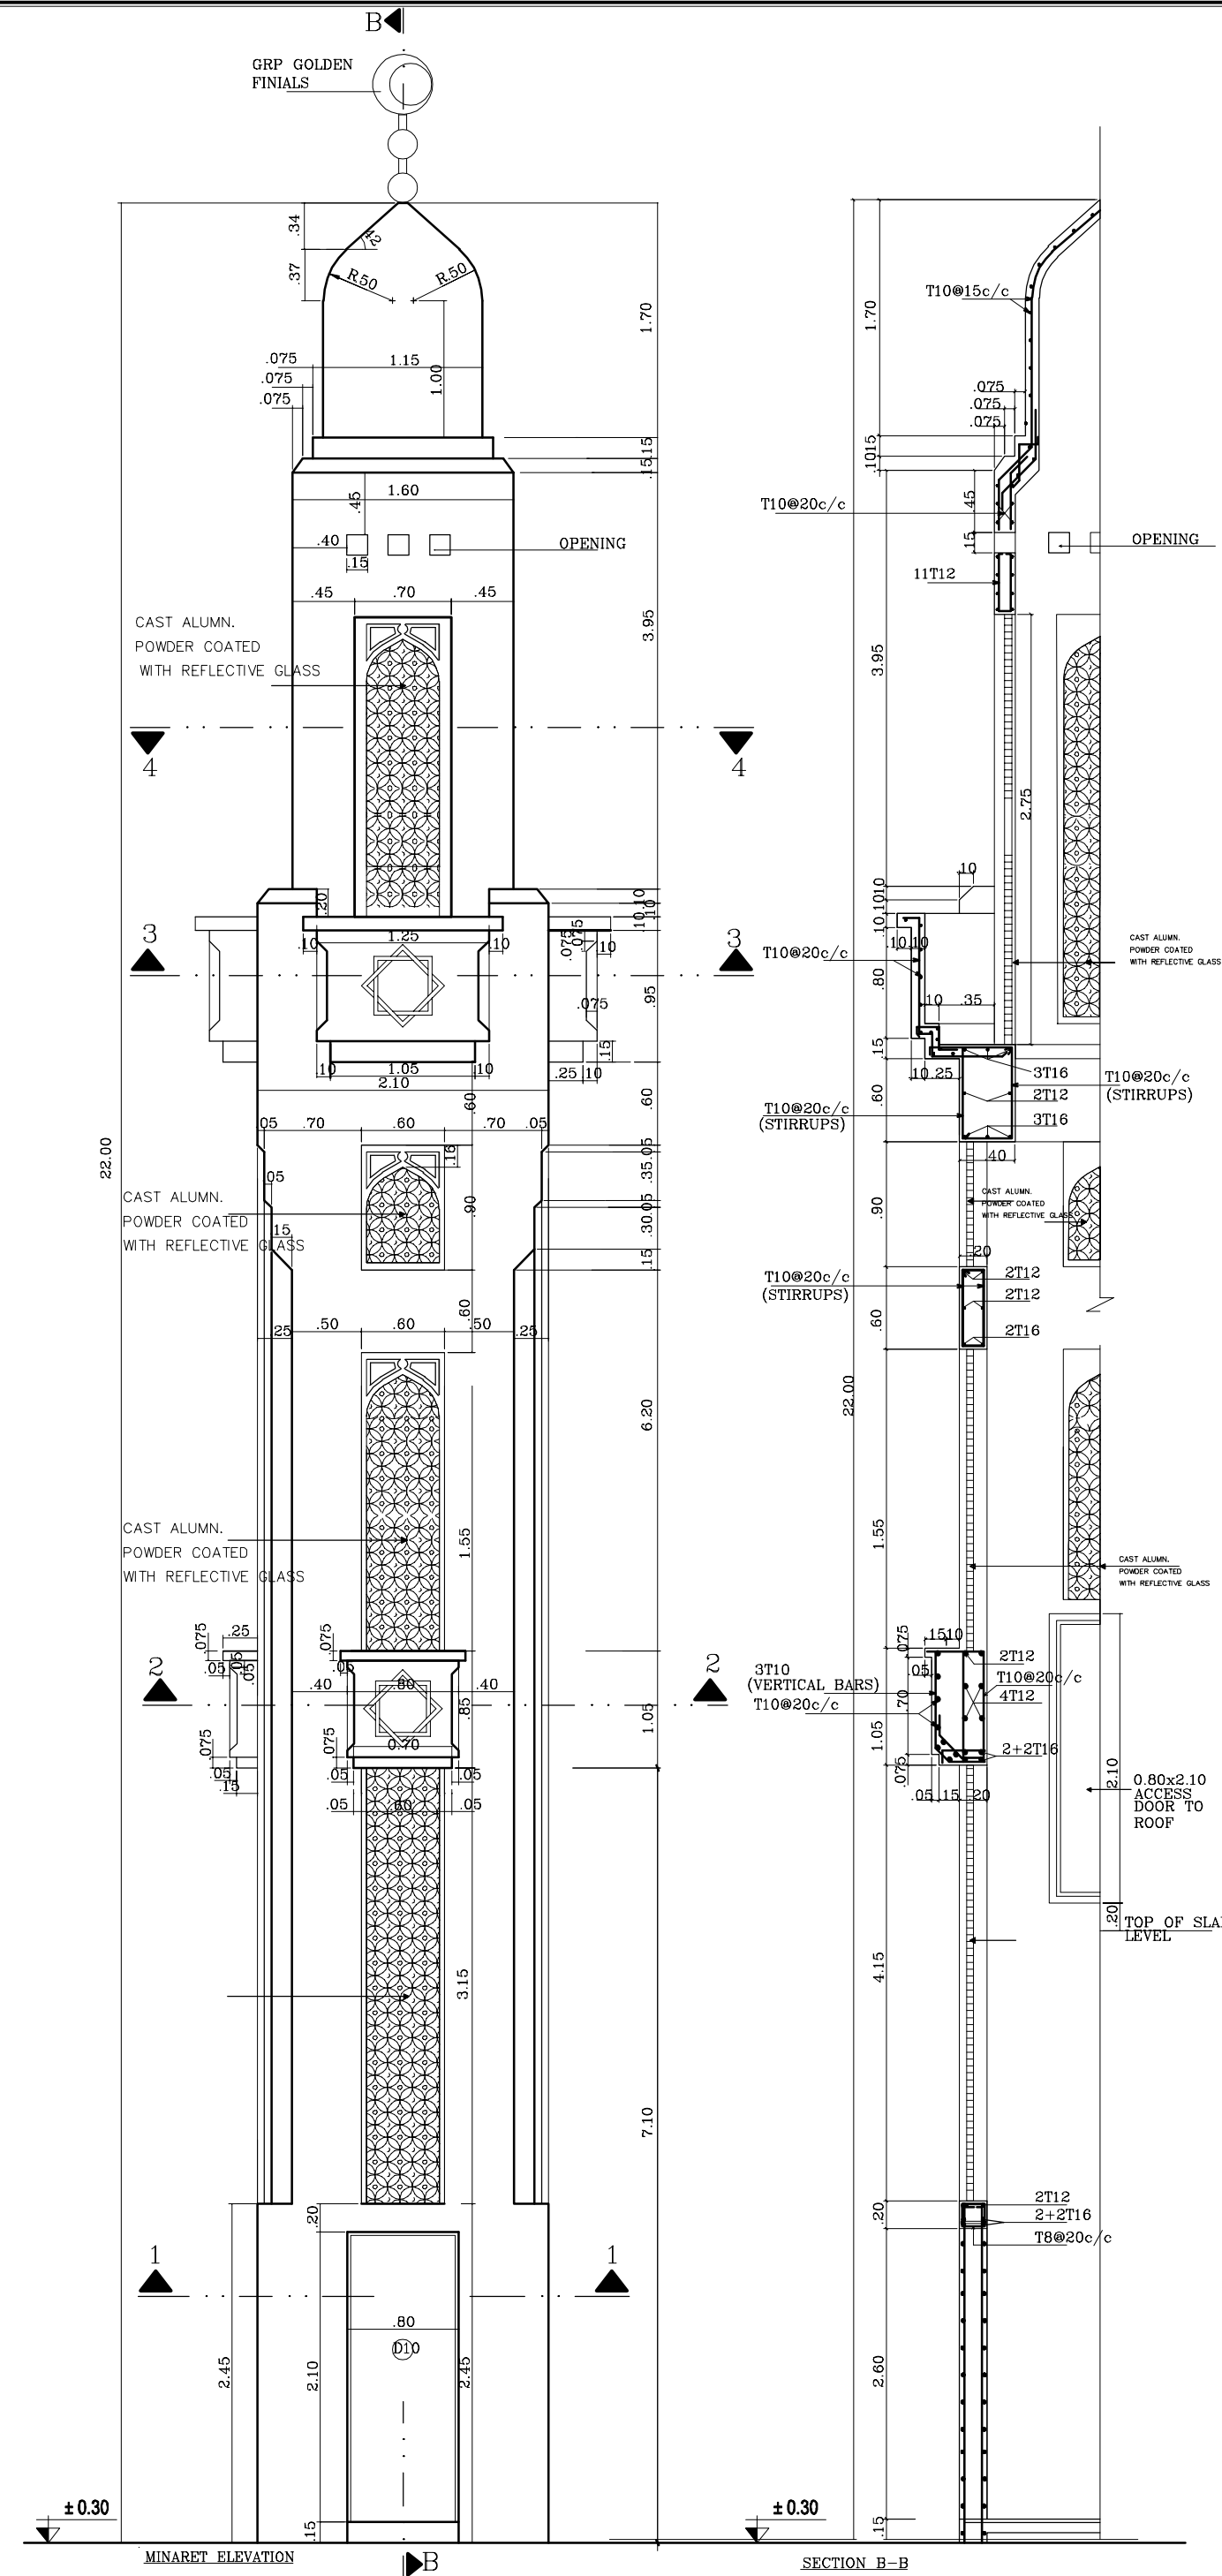

GENERAL NOTES:

1. IT IS NOT ALLOWED TO REPRODUCE THE SHEETS CONTENTS IN ANY FORM EXCEPT FOR THE PURPOSE FOR WHICH IT IS INTENDED.
2. THESE DRAWINGS ARE DIAGRAMMATIC AND SHALL NOT BE SCALED. ADDITIONAL DATA SHALL BE REQUESTED FROM THE CONSULTANCY THROUGH WRITTEN CLARIFICATION. VERIFY ALL EXISTING CONDITIONS AND DIMENSIONS BEFORE PROCEEDING WITH ANY PORTION OF ANY WORK.
3. NO CHANGES, MODIFICATIONS OR DEVIATIONS SHALL BE WRITTEN PERMISSION FROM **ALMASAH ENGINEERING CONSULTANTS**.
4. ALL WORK AS OUTLINED IN THESE DOCUMENTS, SHALL STRICTLY CONFORM TO ALL APPLICABLE CODES. IN THE EVENT OF A CONFLICT, THE MORE STRINGENT REQUIREMENT SHALL GOVERN AND BE MET.



SIA - MS-06



حكومة الشارقة
دائرة الشؤون الإسلامية

CONSULTANT STAMP



CLIENT:

GOVERNMENT OF SHARJAH -
DEPARTMENT OF ISLAMIC AFFAIRS

PROJECT:

(SIA - MS-06)
PROPOSED MASJID + ABLUTION +
IMAM HOUSE

SHEET TITLE:

ARCHITECTURAL DETAILS
FOR MINARET

ARCHITECT

Arch. Mostafa Ramadan

TYPE

ARCHITECTURE

STRUCTURAL

Eng : Mohamed Gomaa

SHEET

No.

A - 16

CHECKED BY

Eng : Mohamed Attia

Location :

Plot No :

SCALE


1:100

DATE

July - 2021


Project

No.

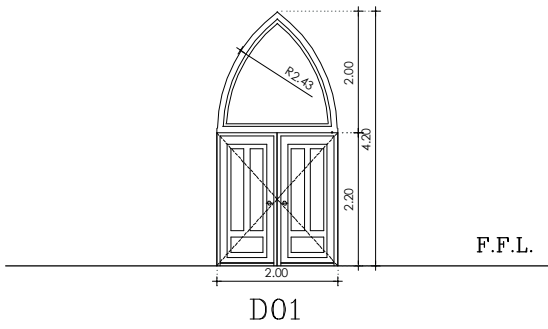


* DECORATIVE SOLID PANEL DOOR AS PER APPROVAL
WINDOW GLAZING = 6mm TH. REF./TINTED GLASS OUTSIDE AND 6mm THICK SANDBLASTED GLASS INSIDE WITH 12mm AIRSPACE IN BETWEEN.

D1 IRONMONGERY TYPE – A

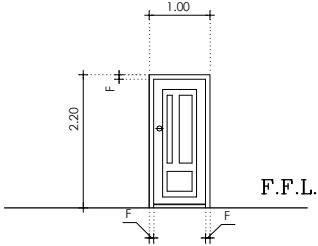


WIDE 1.00*2.20 H
* DECORATIVE SOLID PANEL DOOR AS PER APPROVAL

D2 IRONMONGERY TYPE – A

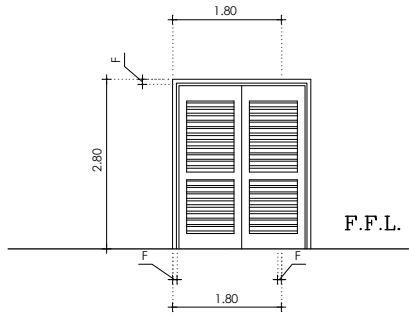


* HEAVY SECTION POWDER COATED LOUVERED ALUMINUM DOOR. COLOR AS PER APPROVAL

D3 IRONMONGERY TYPE – C

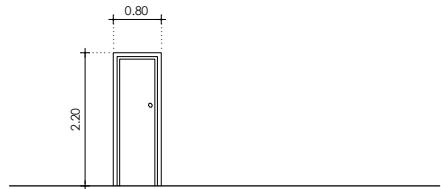


WIDE 0.80*2.20 H
IRONMONGERY TYPE – C
SINGLE LEAF WOODEN FLUSH DOOR WITH MERRANTI WOOD FRAME 4.5cm TH: AND WIDTH AS/WALL THICKNESS WITH TEAK PLY VENEERED SHUTTER WITH AN INTERNAL SOLIDITY OF 75% ALL POLISHED WITH LAQUER POLISH AS PER APPROVAL WITH DOOR CLOSER MACHINE AS PER APPROVAL FOR WOMEN ABLUTION.

D4

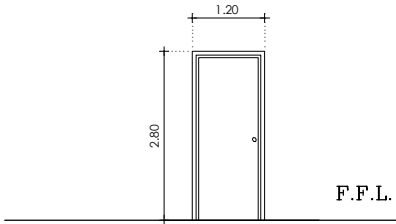


IRONMONGERY TYPE – C
SINGLE LEAF WOODEN FLUSH DOOR WITH MERRANTI WOOD FRAME 4.5cm TH: AND WIDTH AS/WALL THICKNESS WITH TEAK PLY VENEERED SHUTTER WITH AN INTERNAL SOLIDITY OF 75% ALL POLISHED WITH LAQUER POLISH AS PER APPROVAL WITH DOOR CLOSER MACHINE AS PER APPROVAL FOR WOMEN ABLUTION.

D5

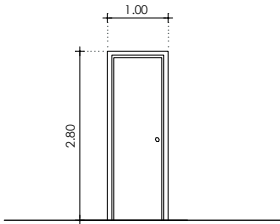

IRONMONGERY TYPE – D
SINGLE LEAF WOODEN FLUSH DOOR WITH MERRANTI WOOD FRAME 4.5cm TH: AND WIDTH AS/WALL THICKNESS WITH TEAK PLY VENEERED SHUTTER WITH AN INTERNAL SOLIDITY OF 75% ALL POLISHED WITH LAQUER POLISH AS PER APPROVAL.

D6

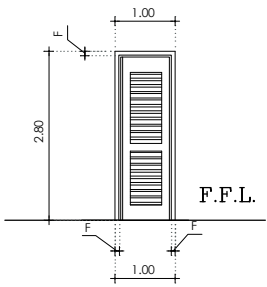

* HEAVY SECTION POWDER COATED LOUVERED ALUMINUM DOOR. COLOR AS PER APPROVAL

D7 IRONMONGERY TYPE – C

GENERAL DOOR/WINDOW NOTES

- 1-DRAWINGS ARE NOT TO BE SCALED.
- 2-THIS DRAWING IS TO BE READ IN CONJUNCTION WITH ALL OTHER RELEVANT DRAWINGS.
- 3-CONTRACTOR IS TO CONFIRM AND WORK TO ACTUAL EXIST. DIMENSIONS ON SITE.
- 4-ALL DIMENSIONS RELATE TO STRUCTURAL OPENINGS UNLESS OTHERWISE NOTED.
- 5-CONTRACTOR SHALL SUBMIT ALL NECESSARY DOOR/WINDOW SHOP DRAWINGS FOR APPROVAL PRIOR TO FABRICATION AND INSTALLATION.
- 6-ALL WOODEN DOORS TO HAVE ARCHITRAVES ON BOTH SIDES AS PER APPROVAL.
- 7-ALL FLUSH DOOR SHUTTERS SHOULD BE MIN. 75% SOLID INSIDE AS PER APPROVAL.
- 8-ALL ALUMINUM DOORS/WINDOWS TO HAVE ALUMINUM ARCHITRAVE BOTH SIDES AS PER APPROVAL UNLESS NOTED OTHERWISE.
- 9-ALL DOOR CLOSERS ARE TO HAVE 90 DEGREE HOLD OPEN FACILITY.
- 10-ALL EXTERNAL DOORS SHALL HAVE WEATHER SEALS.
- 11-ALL GLAZING BELOW 90cm ABOVE FINISH FLOOR LEVEL SHALL BE WITH TEMPERED GLASS

TIMBER OPENINGS

- 1- ALL DOORS SHALL BE COMPLETE WITH 1-1/2 PAIR OF BRASS HINGES (3 PAIR HEAVY DUTY FOR DOUBLE DOORS) & APPROVED QUALITY LOCKS, CLOSERS, HANDLES, BOLTS AND DOOR STOPS AS NOTED.
- 2- CONTRACTOR SHALL SUBMIT SAMPLES OF ALL IRON MONGERY TO BE USED FOR CONSULTANTS APPROVAL PRIOR TO PLACING AN ORDER.
- 3- DOOR FRAME SHALL BE SECURED TO OPENINGS WITH MIN. 3 No.'s 10mm dia. & 4" LONG EXPANDING BOLTS.
- 4- ALL INSIDE FACES OF TIMBER FRAMES TO BE PAINTED WITH PRESERVATIVE PAINT OF APPROVED QUALITY.
- 5- ALL PANELLED DOORS SHALL HAVE STILES, TOP RAIL & MIDDLE RAIL MIN. 4" WIDE. BOTTOM RAIL MIN. 8" WIDE. DECORATIVE PANELS AS/APPROVED DESIGN.
- 6- PROVIDE 3/4" x 9" OR 5" MARINE PLYWOOD SUBFRAMES TO ALL DOOR OPENINGS.
- 7- ALL FLUSH DOORS TO BE 100% SOLID CORE OR 80% SEMI-SOLID CORE WITH HARDWOOD LIPPING ALL AROUND AS PER SPECIFICATIONS.
- 8- PROVIDE 2" x 9" OR 2" x 5" DECORATIVE RED MERRANTI WOOD FRAME ON BOTH SIDES.

ALUMINUM OPENINGS

- 1- CONTRACTOR SHALL SUBMIT ALL SAMPLES OF ALL ALUM. SECTIONS, GLAZING, LOCKS, HANDLES ETC.. FOR APPROVAL OF CONSULTANT PRIOR TO PLACING AN ORDER.
- 2- ALL ALUMINUM OPENINGS TO HAVE .75" MARINE PLY SUB-FRAME OR TREATED RED MERANTI AS/APPROVAL.
- 3- ALL ALUMINUM OPENINGS TO BE SEALED WITH 2 PARTS POLYSULPHIDE SEALANT MIN .25" THICK.
- 4- DRAINAGE WEEP HOLES TO BE PROVIDED AT THE BOTTOMS OF ALL ALUMINUM FRAMES AS PER APPROVAL.
- 5- ALL ALUMINUM DOORS AND WINDOW S SHALL BE COMPLETE WITH APPROPRIATE HANDLES, LOCKS, SLIDING GEAR ETC., WHICH SHALL BE OF APPROVED QUALITY AND DESIGN.
- 6- WHERE EVER MARINE PLY SUBFRAME IS EXPOSED PROVIDE 1/32" THICK RED MERRANTI COVER SLIP (SCREWED) TO CONCEAL THE SAME/EXPOSED SURFACES TO BE TREATED WITH APP. PRESERVATIVE PAINT.
- 7- ALL SILL HEIGHTS ARE FROM FINISH FLOOR LEVEL UNLESS NOTED OTHERWISE.
- 8- FLY MESH SCREENS TO BE FROM INSIDE UNLESS NOTED OTHERWISE

DOOR IRONMONGERY SCHEDULE TYPE – A

1. LEVER HANDLE BOTH SIDES
2. CYLINDER WITH KEY OPERATION BOTH SIDES
3. APPROPRIATE LOCK CASE AND STRIKE PLATE
4. 4 PAIR HINGES
5. LEVER ACTION FLUSH BOLTS (TOP/BOT) BOTH LEAFS
6. OVERHEAD DOOR CLOSER
7. DOOR STOPS

TYPE – B

1. LEVER HANDLE BOTH SIDES
2. CYLINDER WITH KEY OPERATION BOTH SIDES
3. APPROPRIATE LOCK CASE AND STRIKE PLATE
4. 1? PAIR HINGES
5. OVERHEAD DOOR CLOSER
6. DOOR STOPS

TYPE – C

1. LEVER HANDLE BOTH SIDES
2. CYLINDER WITH KEY OPERATION BOTH SIDES
3. APPROPRIATE LOCK CASE AND STRIKE PLATE
4. 1%129 PAIR HINGES
5. DOOR STOPS

TYPE – D

1. LEVER HANDLE BOTH SIDES
2. THUMB TURN ONE SIDE
3. EMERGENCY RELEASE WITH INDICATOR OTHER SIDE
4. 1%129 PAIR HINGES
5. DOOR STOPS

GENERAL NOTES:

- 1.IT IS NOT ALLOWED TO REPRODUCE THE SHEETS CONTENTS IN ANY FORM EXCEPT FOR THE PURPOSE FOR WHICH IT IS INTENDED.
2. THESE DRAWINGS ARE DIAGRAMMATIC AND SHALL NOT BE SCALED. ADDITIONAL DATA SHALL BE REQUESTED FROM THE CONSULTANCY THROUGH WRITTEN CLARIFICATION. VERIFY ALL EXISTING CONDITIONS AND DIMENSIONS BEFORE PROCEEDING WITH ANY PORTION OF ANY WORK.
3. NO CHANGES, MODIFICATIONS OR DEVIATIONS SHALL BE WRITTEN PERMISSION FROM **ALMASAH ENGINEERING CONSULTANTS**.
4. ALL WORK AS OUTLINED IN THESE DOCUMENTS, SHALL STRICTLY CONFORM TO ALL APPLICABLE CODES. IN THE EVENT OF A CONFLICT, THE MORE STRINGENT REQUIREMENT SHALL GOVERN AND BE MET.

SIA - SM-06



CONSULTANT STAMP



CLIENT:

GOVERNMENT OF SHARJAH -
DEPARTMENT OF ISLAMIC AFFAIRS


PROJECT:

(SIA - SM-06)
PROPOSED MASJID + ABLUTION +
IMAM HOUSE

SHEET TITLE:

DOOR DETAILS & NOTES

ARCHITECT Arch. Mostafa Ramadan	TYPE	ARCHITECTURE
STRUCTURAL Eng : Mohamed Gomaa	SHEET No.	A - 13
CHECKED BY Eng : Mohamed Attia	Location :	
SCALE 1:100	DATE November - 2021	Plot No : Project No.

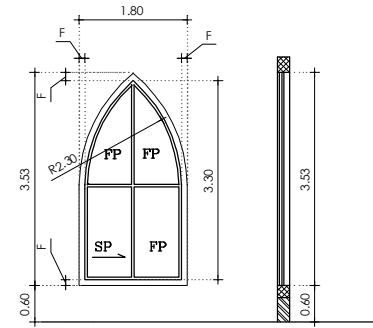


F = FRAME
FP = FIXED PANEL
SP = SLIDING PANEL

- MEDIUM SECTION POWDER COATED ALUMINUM WINDOW
COLOR AS PER APPROVAL.

WINDOW GLAZING = 6mm THICK REF./TINTED GLASS OUTSIDE AND 6mm THICK SANDBLASTED GLASS INSIDE WITH 12mm AIRSPACE IN BETWEEN. INTERVAL WINDOWS TO BE 6mm THICK SANDBLASTED GLASS. AS PER APPROVAL.

W1

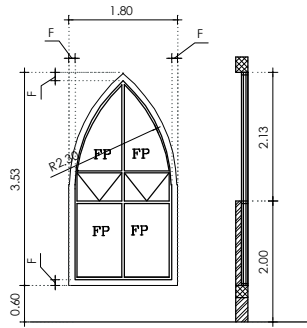


F = FRAME
FP = FIXED PANEL
SP = SLIDING PANEL

- MEDIUM SECTION POWDER COATED ALUMINUM WINDOW
COLOR AS PER APPROVAL.

WINDOW GLAZING = 6mm THICK REF./TINTED GLASS OUTSIDE AND 6mm THICK SANDBLASTED GLASS INSIDE WITH 12mm AIRSPACE IN BETWEEN. INTERVAL WINDOWS TO BE 6mm THICK SANDBLASTED GLASS. AS PER APPROVAL.


W2

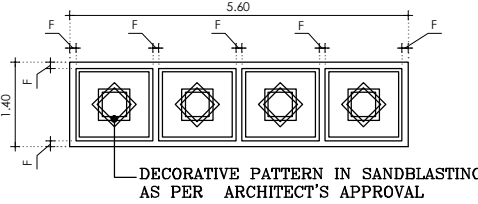

DOME WINDOW'S (6 No.'s)

- HEAVY SECTION POWDER COATED ALUMINUM WINDOW
COLOR AS PER APPROVAL.
- WINDOW GLAZING = 6mm THICK REF./TINTED GLASS OUTSIDE AND 6mm THICK SANDBLASTED GLASS INSIDE WITH 12mm AIRSPACE IN BETWEEN.

W3

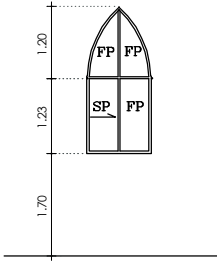


F = FRAME
FP = FIXED PANEL
SP = SLIDING PANEL

- HEAVY SECTION POWDER COATED ALUMINUM WINDOW
COLOR AS PER APPROVAL.

WINDOW GLAZING = 6mm THICK REF./TINTED GLASS OUTSIDE AND 6mm THICK SANDBLASTED GLASS INSIDE WITH 12mm AIRSPACE IN BETWEEN.

W4

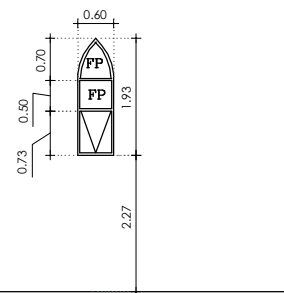


F = FRAME
FP = FIXED PANEL
SP = SLIDING PANEL

- HEAVY SECTION POWDER COATED ALUMINUM WINDOW
COLOR AS PER APPROVAL.

WINDOW GLAZING = 6mm THICK REF./TINTED GLASS OUTSIDE AND 6mm THICK SANDBLASTED GLASS INSIDE WITH 12mm AIRSPACE IN BETWEEN.

W4

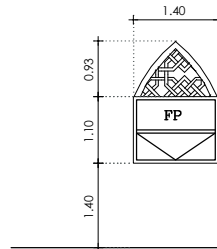


F = FRAME
FP = FIXED PANEL
SP = SLIDING PANEL

- HEAVY SECTION POWDER COATED ALUMINUM WINDOW
COLOR AS PER APPROVAL.

WINDOW GLAZING = 6mm THICK REF./TINTED GLASS OUTSIDE AND 6mm THICK SANDBLASTED GLASS INSIDE WITH 12mm AIRSPACE IN BETWEEN.

W5

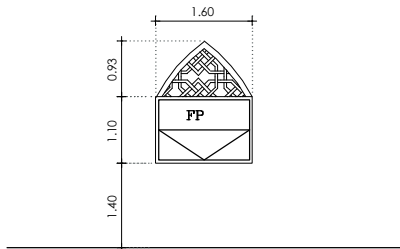


F = FRAME
FP = FIXED PANEL
SP = SLIDING PANEL

- HEAVY SECTION POWDER COATED ALUMINUM WINDOW
COLOR AS PER APPROVAL.

WINDOW GLAZING = 6mm THICK REF./TINTED GLASS OUTSIDE AND 6mm THICK SANDBLASTED GLASS INSIDE WITH 12mm AIRSPACE IN BETWEEN.

W6

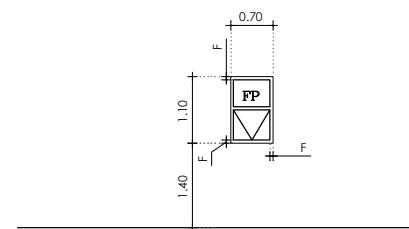


F = FRAME
FP = FIXED PANEL
SP = SLIDING PANEL

- HEAVY SECTION POWDER COATED ALUMINUM WINDOW
COLOR AS PER APPROVAL.

WINDOW GLAZING = 6mm THICK REF./TINTED GLASS OUTSIDE AND 6mm THICK SANDBLASTED GLASS INSIDE WITH 12mm AIRSPACE IN BETWEEN.

W7

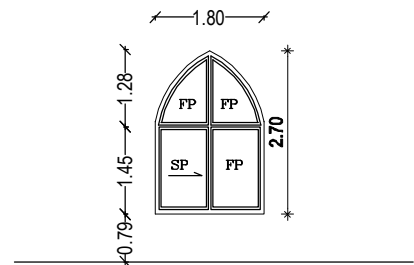


F = FRAME
FP = FIXED PANEL
SP = SLIDING PANEL

- HEAVY SECTION POWDER COATED ALUMINUM WINDOW
COLOR AS PER APPROVAL.

WINDOW GLAZING = 6mm THICK REF./TINTED GLASS OUTSIDE AND 6mm THICK SANDBLASTED GLASS INSIDE WITH 12mm AIRSPACE IN BETWEEN.

W8

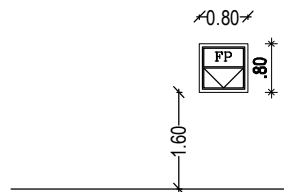

F = FRAME
FP = FIXED PANEL
SP = SLIDING PANEL

- HEAVY SECTION POWDER COATED ALUMINUM WINDOW
COLOR AS PER APPROVAL.

WINDOW GLAZING = 6mm THICK REF./TINTED GLASS OUTSIDE AND 6mm THICK SANDBLASTED GLASS INSIDE WITH 12mm AIRSPACE IN BETWEEN.

W9

GENERAL DOOR/WINDOW NOTES

DRAWINGS ARE NOT TO BE SCALED.

THIS DRAWING IS TO BE READ IN CONJUNCTION WITH ALL OTHER RELEVANT DRAWINGS.

CONTRACTOR IS TO CONFIRM AND WORK TO ACTUAL EXIST. DIMENSIONS ON SITE.

ALL DIMENSIONS RELATE TO STRUCTURAL OPENINGS UNLESS OTHERWISE NOTED.

CONTRACTOR SHALL SUBMIT ALL NECESSARY DOOR/WINDOW SHOP DRAWINGS FOR APPROVAL PRIOR TO FABRICATION AND INSTALLATION.

ALL WOODEN DOORS TO HAVE ARCHITRAVES ON BOTH SIDES AS PER APPROVAL.

ALL FLUSH DOOR SHUTTERS SHOULD BE MIN. 75% SOLID INSIDE AS PER APPROVAL.

ALL ALUMINUM DOORS/WINDOWS TO HAVE ALUMINUM ARCHITRAVE BOTH SIDES AS PER APPROVAL UNLESS NOTED OTHERWISE.

ALL DOOR CLOSERS ARE TO HAVE 90 DEGREE HOLD OPEN FACILITY.

ALL EXTERNAL DOORS SHALL HAVE WEATHER SEALS.

ALL GLAZING BELOW 90cm ABOVE FINISH FLOOR LEVEL SHALL BE WITH TEMPERED GLASS

TIMBER OPENINGS

1- ALL DOORS SHALL BE COMPLETE WITH 1-1/2 PAIR OF BRASS HINGES (3 PAIR HEAVY DUTY FOR DOUBLE DOORS) & APPROVED QUALITY LOCKS, CLOSERS, HANDLES, BOLTS AND DOOR STOPS AS NOTED.

2- CONTRACTOR SHALL SUBMIT SAMPLES OF ALL IRON MONGERY TO BE USED FOR CONSULTANTS APPROVAL PRIOR TO PLACING AN ORDER.

3- DOOR FRAME SHALL BE SECURED TO OPENINGS WITH MIN. 3 No.'s 10mm dia. & 4" LONG EXPANDING BOLTS.

4- ALL INSIDE FACES OF TIMBER FRAMES TO BE PAINTED WITH PRESERVATIVE PAINT OF APPROVED QUALITY.

5- ALL PANELLED DOORS SHALL HAVE STILES, TOP RAIL & MIDDLE RAIL MIN. 4" WIDE. BOTTOM RAIL MIN. 8" WIDE. DECORATIVE PANELS AS/APPROVED DESIGN.

6- PROVIDE 4" x 9" OR 5" MARINE PLYWOOD SUBFRAMES TO ALL DOOR OPENINGS.

7- ALL FLUSH DOORS TO BE 100% SOLID CORE OR 80% SEMI-SOLID CORE WITH HARDWOOD LIPPING ALL AROUND AS PER SPECIFICATIONS.

8- PROVIDE 2" x 9" OR 2" x 5" DECORATIVE RED MERRANTI WOOD FRAME ON BOTH SIDES.

ALUMINUM OPENINGS

1- CONTRACTOR SHALL SUBMIT ALL SAMPLES OF ALL ALUM. SECTIONS, GLAZING, LOCKS, HANDLES ETC., FOR APPROVAL OF CONSULTANT PRIOR TO PLACING AN ORDER.

2- ALL ALUMINUM OPENINGS TO HAVE .75" MARINE PLY SUB-FRAME OR TREATED RED MERRANTI AS/APPROVAL.

3- ALL ALUMINUM OPENINGS TO BE SEALED WITH 2 PARTS POLYSULPHIDE SEALANT MIN .25" THICK.

4- DRAINAGE WEEP HOLES TO BE PROVIDED AT THE BOTTOMS OF ALL ALUMINUM FRAMES AS PER APPROVAL.

5- ALL ALUMINUM DOORS AND WINDOW S SHALL BE COMPLETE WITH APPROPRIATE HANDLES, LOCKS, SLIDING GEAR ETC., WHICH SHALL BE OF APPROVED QUALITY AND DESIGN.

6- WHERE EVER MARINE PLY SUBFRAME IS EXPOSED PROVIDE 1/8"THICK RED MERRANTI COVER SLIP (SCREWED) TO CONCEAL THE SAME/EXPOSED SURFACES TO BE TREATED WITH APP. PRESERVATIVE PAINT.

7- ALL SILL HEIGHTS ARE FROM FINISH FLOOR LEVEL UNLESS NOTED OTHERWISE.

8- FLY MESH SCREENS TO BE FROM INSIDE UNLESS NOTED OTHERWISE

GENERAL NOTES:

- 1.IT IS NOT ALLOWED TO REPRODUCE THE SHEETS CONTENTS IN ANY FORM EXCEPT FOR THE PURPOSE FOR WHICH IT IS INTENDED.
2. THESE DRAWINGS ARE DIAGRAMMATIC AND SHALL NOT BE SCALED. ADDITIONAL DATA SHALL BE REQUESTED FROM THE CONSULTANCY THROUGH WRITTEN CLARIFICATION. VERIFY ALL EXISTING CONDITIONS AND DIMENSIONS BEFORE PROCEEDING WITH ANY PORTION OF ANY WORK.
3. NO CHANGES, MODIFICATIONS OR DEVIATIONS SHALL BE WRITTEN PERMISSION FROM **ALMASAH ENGINEERING CONSULTANTS**.
4. ALL WORK AS OUTLINED IN THESE DOCUMENTS, SHALL STRICTLY CONFORM TO ALL APPLICABLE CODES. IN THE EVENT OF A CONFLICT, THE MORE STRINGENT REQUIREMENT SHALL GOVERN AND BE MET.

SIA - SM-06



CONSULTANT STAMP



CLIENT:

GOVERNMENT OF SHARJAH -
DEPARTMENT OF ISLAMIC AFFAIRS

PROJECT:

(SIA - SM-06)
PROPOSED MASJID + ABLUTION +
IMAM HOUSE


SHEET TITLE:

WINDOWS DETAILS & NOTES


ARCHITECT Arch. Mostafa Ramadan	TYPE	ARCHITECTURE
STRUCTURAL Eng : Mohamed Gomaa	SHEET No.	A - 14
CHECKED BY Eng : Mohamed Attia	Location :	
SCALE 1:100	Plot No :	
DATE November - 2021	Project No.	

GENERAL NOTES.


- ALL DIMENSIONS SHOWN ON DRAWINGS ARE IN METRIC UNITS.
- DRAWINGS ARE NOT TO BE SCALED. ONLY WRITTEN DIMENSIONS SHALL BE FOLLOWED.
- ANY DISCREPANCIES, OMISSIONS OR CONFLICTS IN DRAWINGS, DIMENSIONS OR OTHERWISE ARE TO BE BROUGHT TO THE ATTENTION OF (P.W.D.) ENGINEER FOR CORRECTION OR CLARIFICATION PRIOR TO COMMENCING WORKS. NO ACTIONS ARE TO BE TAKEN ON SITE UNTIL (P.W.D.) ENGINEER HAS RESOLVED ANY DISCREPANCIES OR CONFLICTS.
- CONTRACTOR SHALL THOROUGHLY COORDINATE ARCHITECTURAL, STRUCTURAL, DRAINAGE AND A.C. DRAWINGS TO ENSURE SMOOTH SITE OPERATIONS. ALL DIMENSIONS SHALL BE CHECKED AND VERIFIED ON SITE PRIOR TO EXECUTION OF WORK.
- THE MAIN CONTRACTOR SHALL BE RESPONSIBLE FOR THE CO-OPERATION AND QUALITY OF SUB-CONTRACTORS WORK. ALL SUB-STANDARD WORK SHALL BE DEMOLISHED AND RE-BUILT TO ACCEPTABLE STANDARDS AS REQUIRED BY (P.W.D.) WITHOUT ANY EXTRA COST.
- ALL JUNCTIONS BETWEEN R.C. MEMBERS AND BLOCK WORK SHALL BE WITH 15cm WIDE GALVANIZED STEEL EXPANDED MESH (EXPANET) BEFORE COVERING BY PLASTER.
- ALL BALCONY, VERANDAH, TOILET AND KITCHEN FINISHED FLOOR LEVEL SHALL BE 2cm BELOW GENERAL FINISHED FLOOR LEVEL AND PROVIDE 5cm THICK MARBLE THRESHOLD TO BATHROOM, KITCHEN, TOILET AND ENTRANCE DOOR (FULL WIDTH OF OPENINGS) AS PER P.W.D.'S INSTRUCTION.
- ALL LEVELS INDICATED ON DRAWINGS ARE RELATED TO 0.00 LEVEL AS DESCRIBED ABOVE OR AS OTHERWISE INDICATED ON THE ROAD WHICHEVER IS HIGHER. THIS LEVEL SHALL BE HIGHER THAN THE LEVEL IN THE CENTER OF THE FINISHED LEVEL OF THE NEAREST MAIN ROAD.
- FINISHED GROUND FLOOR LEVEL SHALL BE MINIMUM 90cm ABOVE 0.00 LEVEL AS DESCRIBED ABOVE OR AS OTHERWISE INDICATED.
- ALL MATERIALS USED IN CONSTRUCTION SHALL BE OF THE BEST QUALITY TO REQUIRED BRITISH OR EQUIVALENT STANDARDS AND AS APPROVED BY CONSULTANT PRIOR TO COMMENCEMENT OF WORK.
- P.W.D. WILL HAVE THE RIGHT TO REQUEST DETAIL DRAWINGS, SHOP DRAWINGS, ETC. TO BE SUBMITTED BY CONTRACTOR FOR APPROVAL. ANY FINAL APPROVAL FOR DETAILS FOR WORKS INCLUDED OUT AS PER APPROVAL AT NO CHANGE IN COST (VARIATION) .
- ALL KITCHEN, BATHROOMS AND TOILETS SHALL HAVE MINIMUM 20cm SUNKEN PORTION FILLED WITH DENSE LIGHT WEIGHT CONCRETE SCREED LAID OVER MINIMUM 4mm THICK TORCH WELDED POLYESTER FIBRE REINFORCED BITUMINOUS WATERPROOFING MEMBRANE OF APPROVED QUALITY AND APPLIED AS PER P.W.D.'S INSTRUCTIONS.
- ROOF, BATHROOM, TOILET AND KITCHEN WATERPROOFING SHALL BE TESTED FOR MINIMUM 72 HOURS AND SHALL BE CHECKED BY P.W.D. PRIOR TO LAYING SCREED OVER IT.
- ALL BLOCK WORK BELOW GROUND LEVEL AT SILL AND JAMB TO DOOR AND WINDOW OPENING SHALL BE OF SOLID BLOCK OR CONCRETE.
- ALL CONCRETE WORK UNDERGROUND SHALL BE THOROUGHLY PROTECTED BY 3 COATS OF APPROVED QUALITY BITUMINOUS PAINT AND 100 GAUGE POLYTHENE SHEET AS INSTRUCTED BY P.W.D.
- ALL BLOCK WORK SHALL COMPLY TO B.S. 2028. ALL INTERNAL/EXTERNAL BLOCK WALLS SHALL BE 20cm THICK HOLLOW CONCRETE BLOCKS UNLESS OTHERWISE INDICATED.
- UNLESS OTHERWISE SPECIFIED ALL EXTERNAL WALLS SHALL BE RENDERED WITH MINIMUM 02cm THICK SAND /CEMENT RENDER AND ALL INTERNAL WALLS SHALL BE PLASTERED WITH MINIMUM 1.5cm THICK SMOOTH 1:4 SAND/CEMENT PLASTER USING EXPANET PROFILES AND METAL LATH.
- THE CONTRACTOR SHALL SUPPLY SHOP DRAWINGS SHOWING DETAILS OF SIZES AND INSTALLATION FOR DOOR, WINDOWS, KITCHEN CUPBOARDS, HAND RAILING, ENTRANCE GATE ETC. FOR CONSULTANTS APPROVALS (WITHIN 6 WEEKS FROM DATE OF COMMENCEMENT)
- THE CONTRACTOR SHALL SUBMIT SAMPLES OF MATERIALS FROM AT LEAST 3 LOCAL (SHARJAH) SUPPLIERS FOR APPROVAL PRIOR EXECUTION OF WORK (WITHIN 6 WEEKS FROM DATE OF COMMENCEMENT)
- THESE DRAWINGS ARE COPYRIGHT OF (P.W.D) THESE DRAWINGS ARE NOT TO BE COPIED OR REPRODUCED WITHOUT CONSULTANT'S PERMISSION. ALL THE DRAWINGS SHALL BE RETURNED BACK TO THE P.W.D. ENGINEER ON COMPLETION OF THE JOB.
- GROUND FLOOR CONSTRUCTION. UP TO PLINTH LEVEL SHALL BE AS FOLLOWING (UNLESS OTHERWISE SPECIFIED)
 - TILE FLOOR FINISH AS PER SCHEDULE OF FINISHES ON:
 - MIN. 2.5cm THICK SAND/CEMENT MORTAR BED 1:4 ON:
 - MIN. 5cm THICK SAND/CEMENT SCREED ON:
 - 2 COATS OF HOT BITUMINOUS DAMP PROOF COURSE ON TOP OF:
 - MIN. 10cm THICK P.C.C. 1:3:6 FLOOR SLAB REINFORCED WITH B.R.C. 193 FABRIC (19mm BARS @20cm C.T.C. BOTH WAYS) ON:
 - 2 LAYERS OF MIN. 1000 GAUGE POLYTHENE SHEET LAID ACROSS EACH OTHER AT RIGHT ANGLES, TURNED UP MIN. 15cm AT EACH ENDS ON:
 - THREE LAYERS OF MIN. 15cm DEEP SAKKHA LAID IN LAYERS AND WELL COMPACTED WITH MECHANICAL VIBRATOR ON:
 - WELL COMPACTED SAND PLINTH FILLING.
- SLOPING ROOF SLAB COVERED WITH ROOFING TILES SHALL BE PROTECTED WITH LIQUID WATER PROOFING MEMBRANE OF APPROVED QUALITY AND MAKE PRIOR TO FIXING TIMBER BATTENS AND ROOF TILES OVER IT.
- ALL DOOR, WINDOW AND ARCH OPENINGS SHALL HAVE MIN. 2.5cm MARINE PLYWOOD SUB FRAME OF FULL WIDTH OF WALL IN CASE NO SUB FRAME IN SPECIFIED INSIDE FACE OF ALL FRAMES TOUCHING WALL SHALL BE COATED WITH 2 COATS OF ANTI-TERMITE PAINT.
- CONTRACTOR RESPONSIBLE FOR SUPPLYING SCHEDULE OF WORK FOR APPROVAL PRIOR TO STARTING CONSTRUCTION.
- PROVIDE ALL SLIDING/OPENABLE DOORS AND WINDOW SHOULD BE IN DOUBLE GLAZED (u=0.50)
- ALUMINIUM SECTION TO BE THERMAL BREAKING

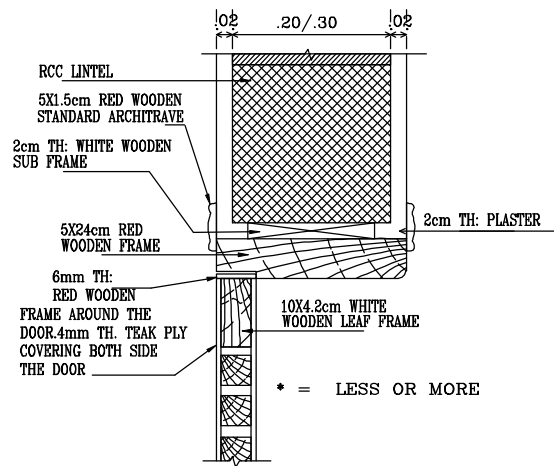

SECTIONAL DETAIL OF HOLLOW CORE DOOR

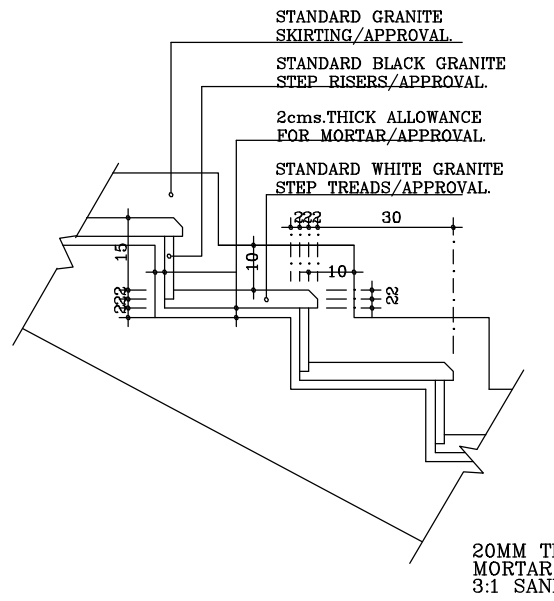


TYP: ENT: STEPS DETAIL

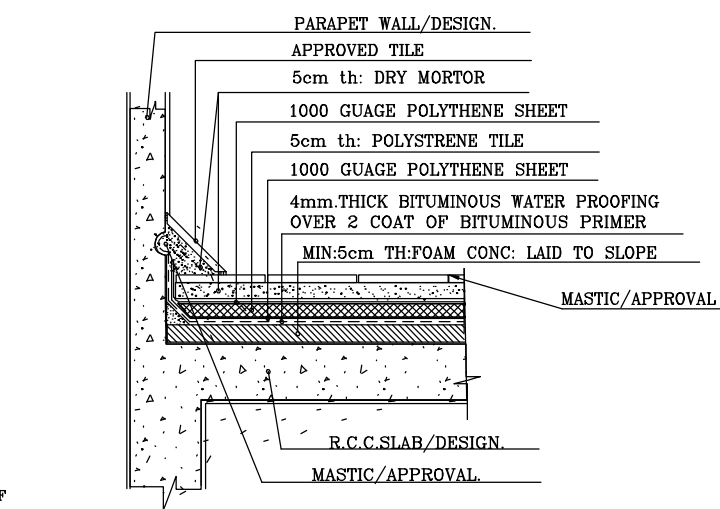


DETAIL-1

WATER PROFING HEAT INSULATION

ROOF CALCULATION		
U VALUE (R = IN SQF h/ BTu)		
1" TERRAZZO	R = 0.08	
2" DRY CEMENT, SAND	R = 0.4	
2" POLYSTYRENE (35 KG/CU.M)	R = 9.47	
0.16" ASPHALT ROLL ROOFING	R = 0.024	
2" LIGHT WEIGHT CONCRETE	R = 1.54	
8" HEAVY WEIGHT CONCRETE	R = 0.59	
TOTAL(R)= 12.104 SQ.FT h/ BTu		
u=1/R OR	u = 0.08 BTu/SQ.FT h	
* POLYSTYRENE FOR HEAT INSULATION OR ANY EQUIVALENT MATERIAL AS PER ENGINEER APPROVAL		

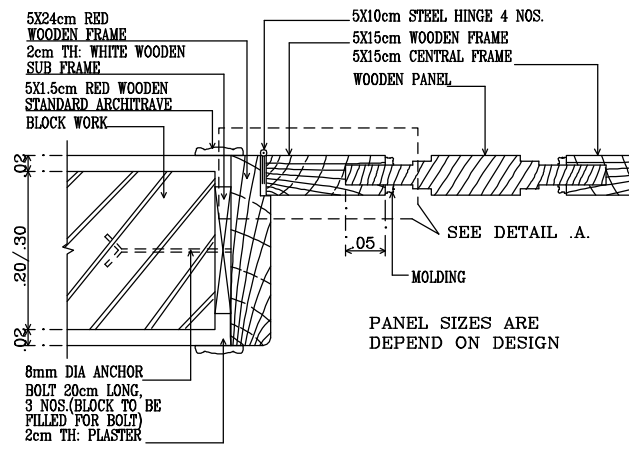


SECTIONAL DETAIL OF SOLID OR PANEL DOOR

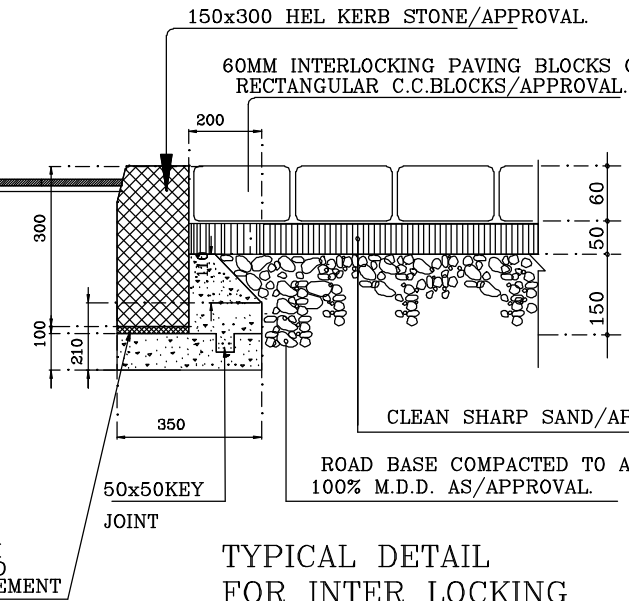

TYPICAL DETAIL FOR INTER LOCKING

PROVIDE 120 CM. WIDE INTER LOCKING ALL AROUND THE BUILDING AS/ SITE AND AS / APPROVAL OF ENGINEER.

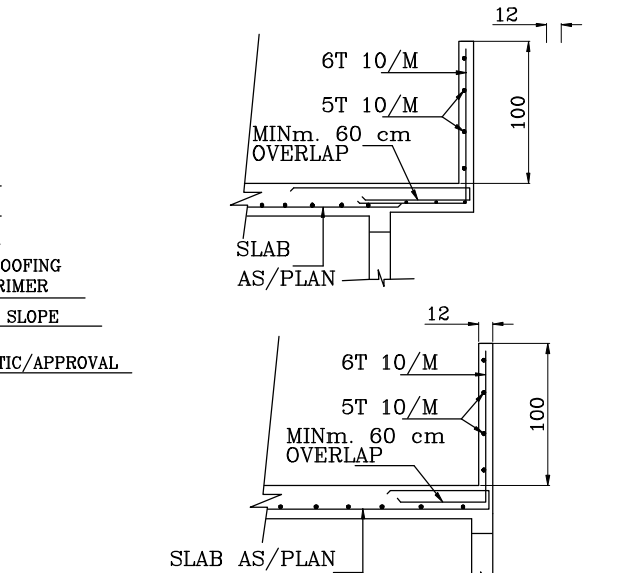



TYPICAL DETAIL FOR DRIVE WAY

NTS. (ALL DIMENSIONS IN MM.)


- 6" (1.5cm) ROOF TILES
- 2" (5cm) TH: DRY MORTAR
- 1000 GAUGE POLYTHENE SHEET
- 2" (5cm) THICK POLYSTYRENE TILE
- 1000 GAUGE POLYTHENE SHEET
- 4mm TH: BITUMINOUS WATERPROOFING OVER 2 COATS OF BITUMINOUS PRIMER
- MIN. 2" (5cm) TH: FOAM CONC. LAID TO SLOPE
- SLAB AS PER SCHEDULE (14cm ASSUMED)
- 1" (2.5cm) SAND PLASTER

PARAPET DETAILS


THE CONSTRUCTION OF ANY MULTI STORY BUILDINGS OR VILLAS STOP THE FIRST SLAB LEVEL MUST HAVE TO PROVIDE 10CM THICK RCC PARAPET WALL FOR FUTURE CONSTRUCTION AS PER DETAIL

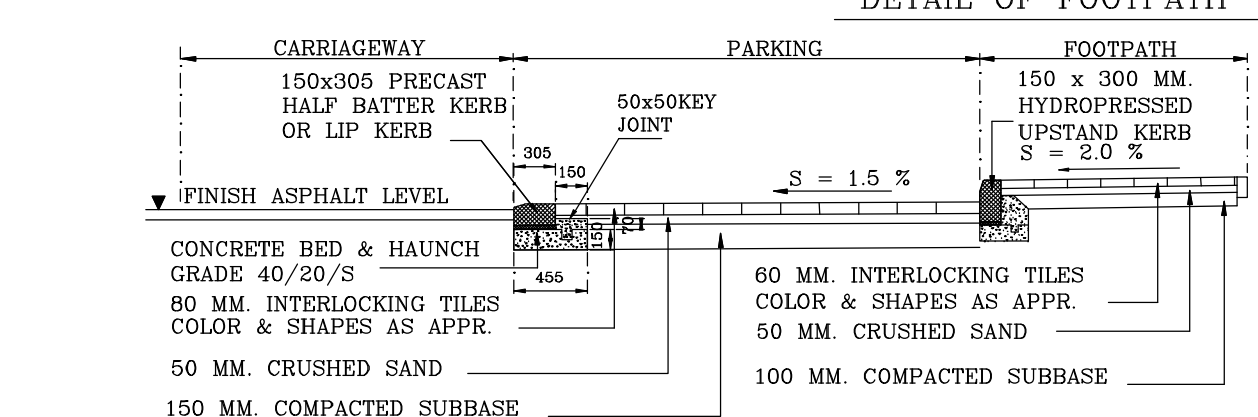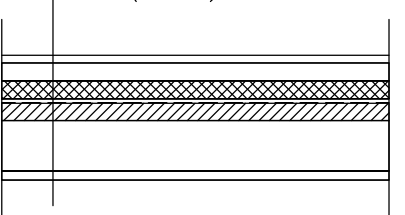

DETAIL OF FOOTPATH & PARKING

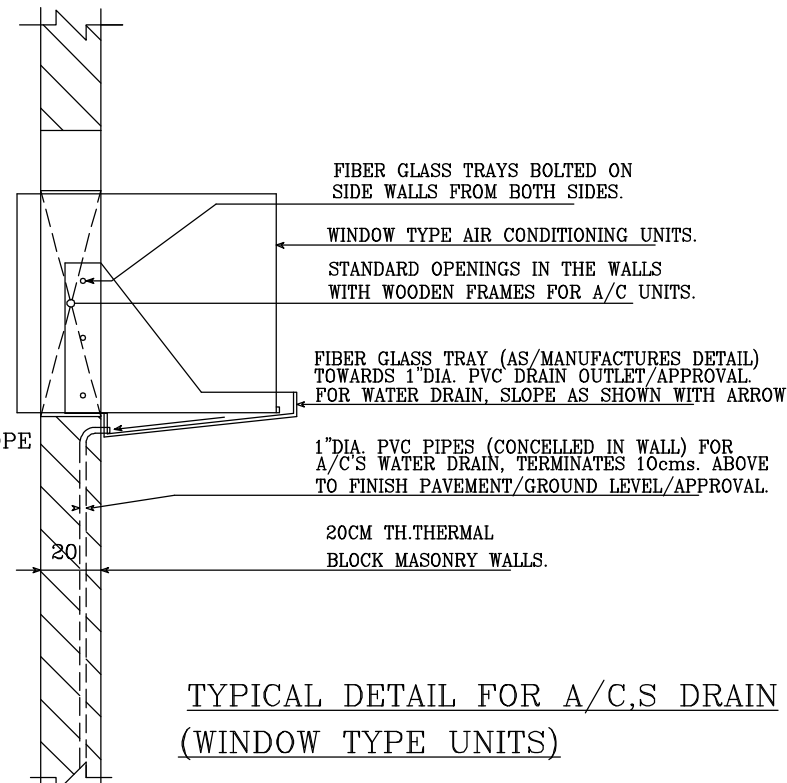

TYPICAL DETAIL FOR A/C.S DRAIN (WINDOW TYPE UNITS)

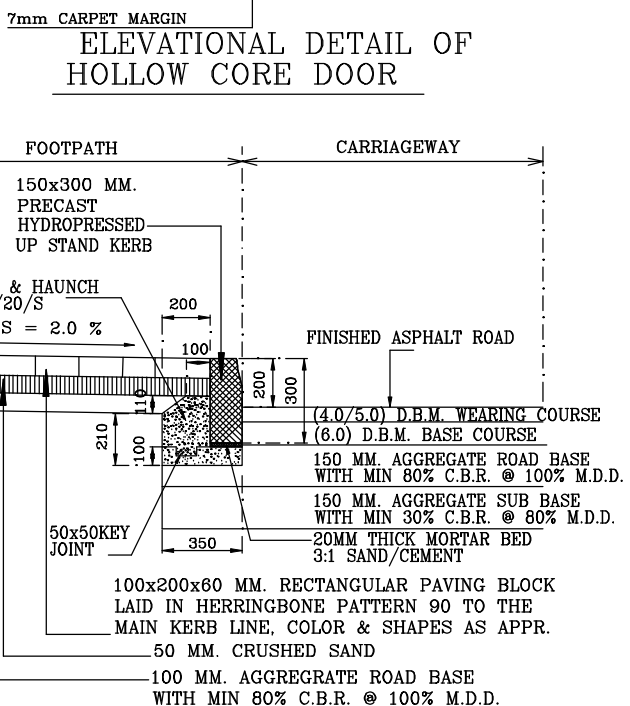

ELEVATIONAL DETAIL OF HOLLOW CORE DOOR

GENERAL NOTES:

- IT IS NOT ALLOWED TO REPRODUCE THE SHEETS CONTENTS IN ANY FORM EXCEPT FOR THE PURPOSE FOR WHICH IT IS INTENDED.
- THESE DRAWINGS ARE DIAGRAMMATIC AND SHALL NOT BE SCALED. ADDITIONAL DATA SHALL BE REQUESTED FROM THE CONSULTANCY THROUGH WRITTEN CLARIFICATION. VERIFY ALL EXISTING CONDITIONS AND DIMENSIONS BEFORE PROCEEDING WITH ANY PORTION OF ANY WORK.
- NO CHANGES, MODIFICATIONS OR DEVIATIONS SHALL BE WRITTEN PERMISSION FROM **ALMASAH ENGINEERING CONSULTANTS**.
- ALL WORK AS OUTLINED IN THESE DOCUMENTS, SHALL STRICTLY CONFORM TO ALL APPLICABLE CODES. IN THE EVENT OF A CONFLICT, THE MORE STRINGENT REQUIREMENT SHALL GOVERN AND BE MET.

SIA - SM-06



حُكُومَةُ الشَّارِقَةِ
دائرة الشؤون الإسلامية

CONSULTANT STAMP



CLIENT: GOVERNMENT OF SHARJAH - DEPARTMENT OF ISLAMIC AFFAIRS		
PROJECT: (SIA - SM-06) PROPOSED MASJID + ABLUTION + IMAM HOUSE		
SHEET TITLE: GEN -DETAILS & HEAT		
ARCHITECT Arch. Mostafa Ramadan	TYPE	ARCHITECTURE
STRUCTURAL Eng : Mohamed Gomaa	SHEET No.	A - 15
CHECKED BY Eng : Mohamed Attia	Location :	
SCALE 1:100	DATE November - 2021	Project No.