


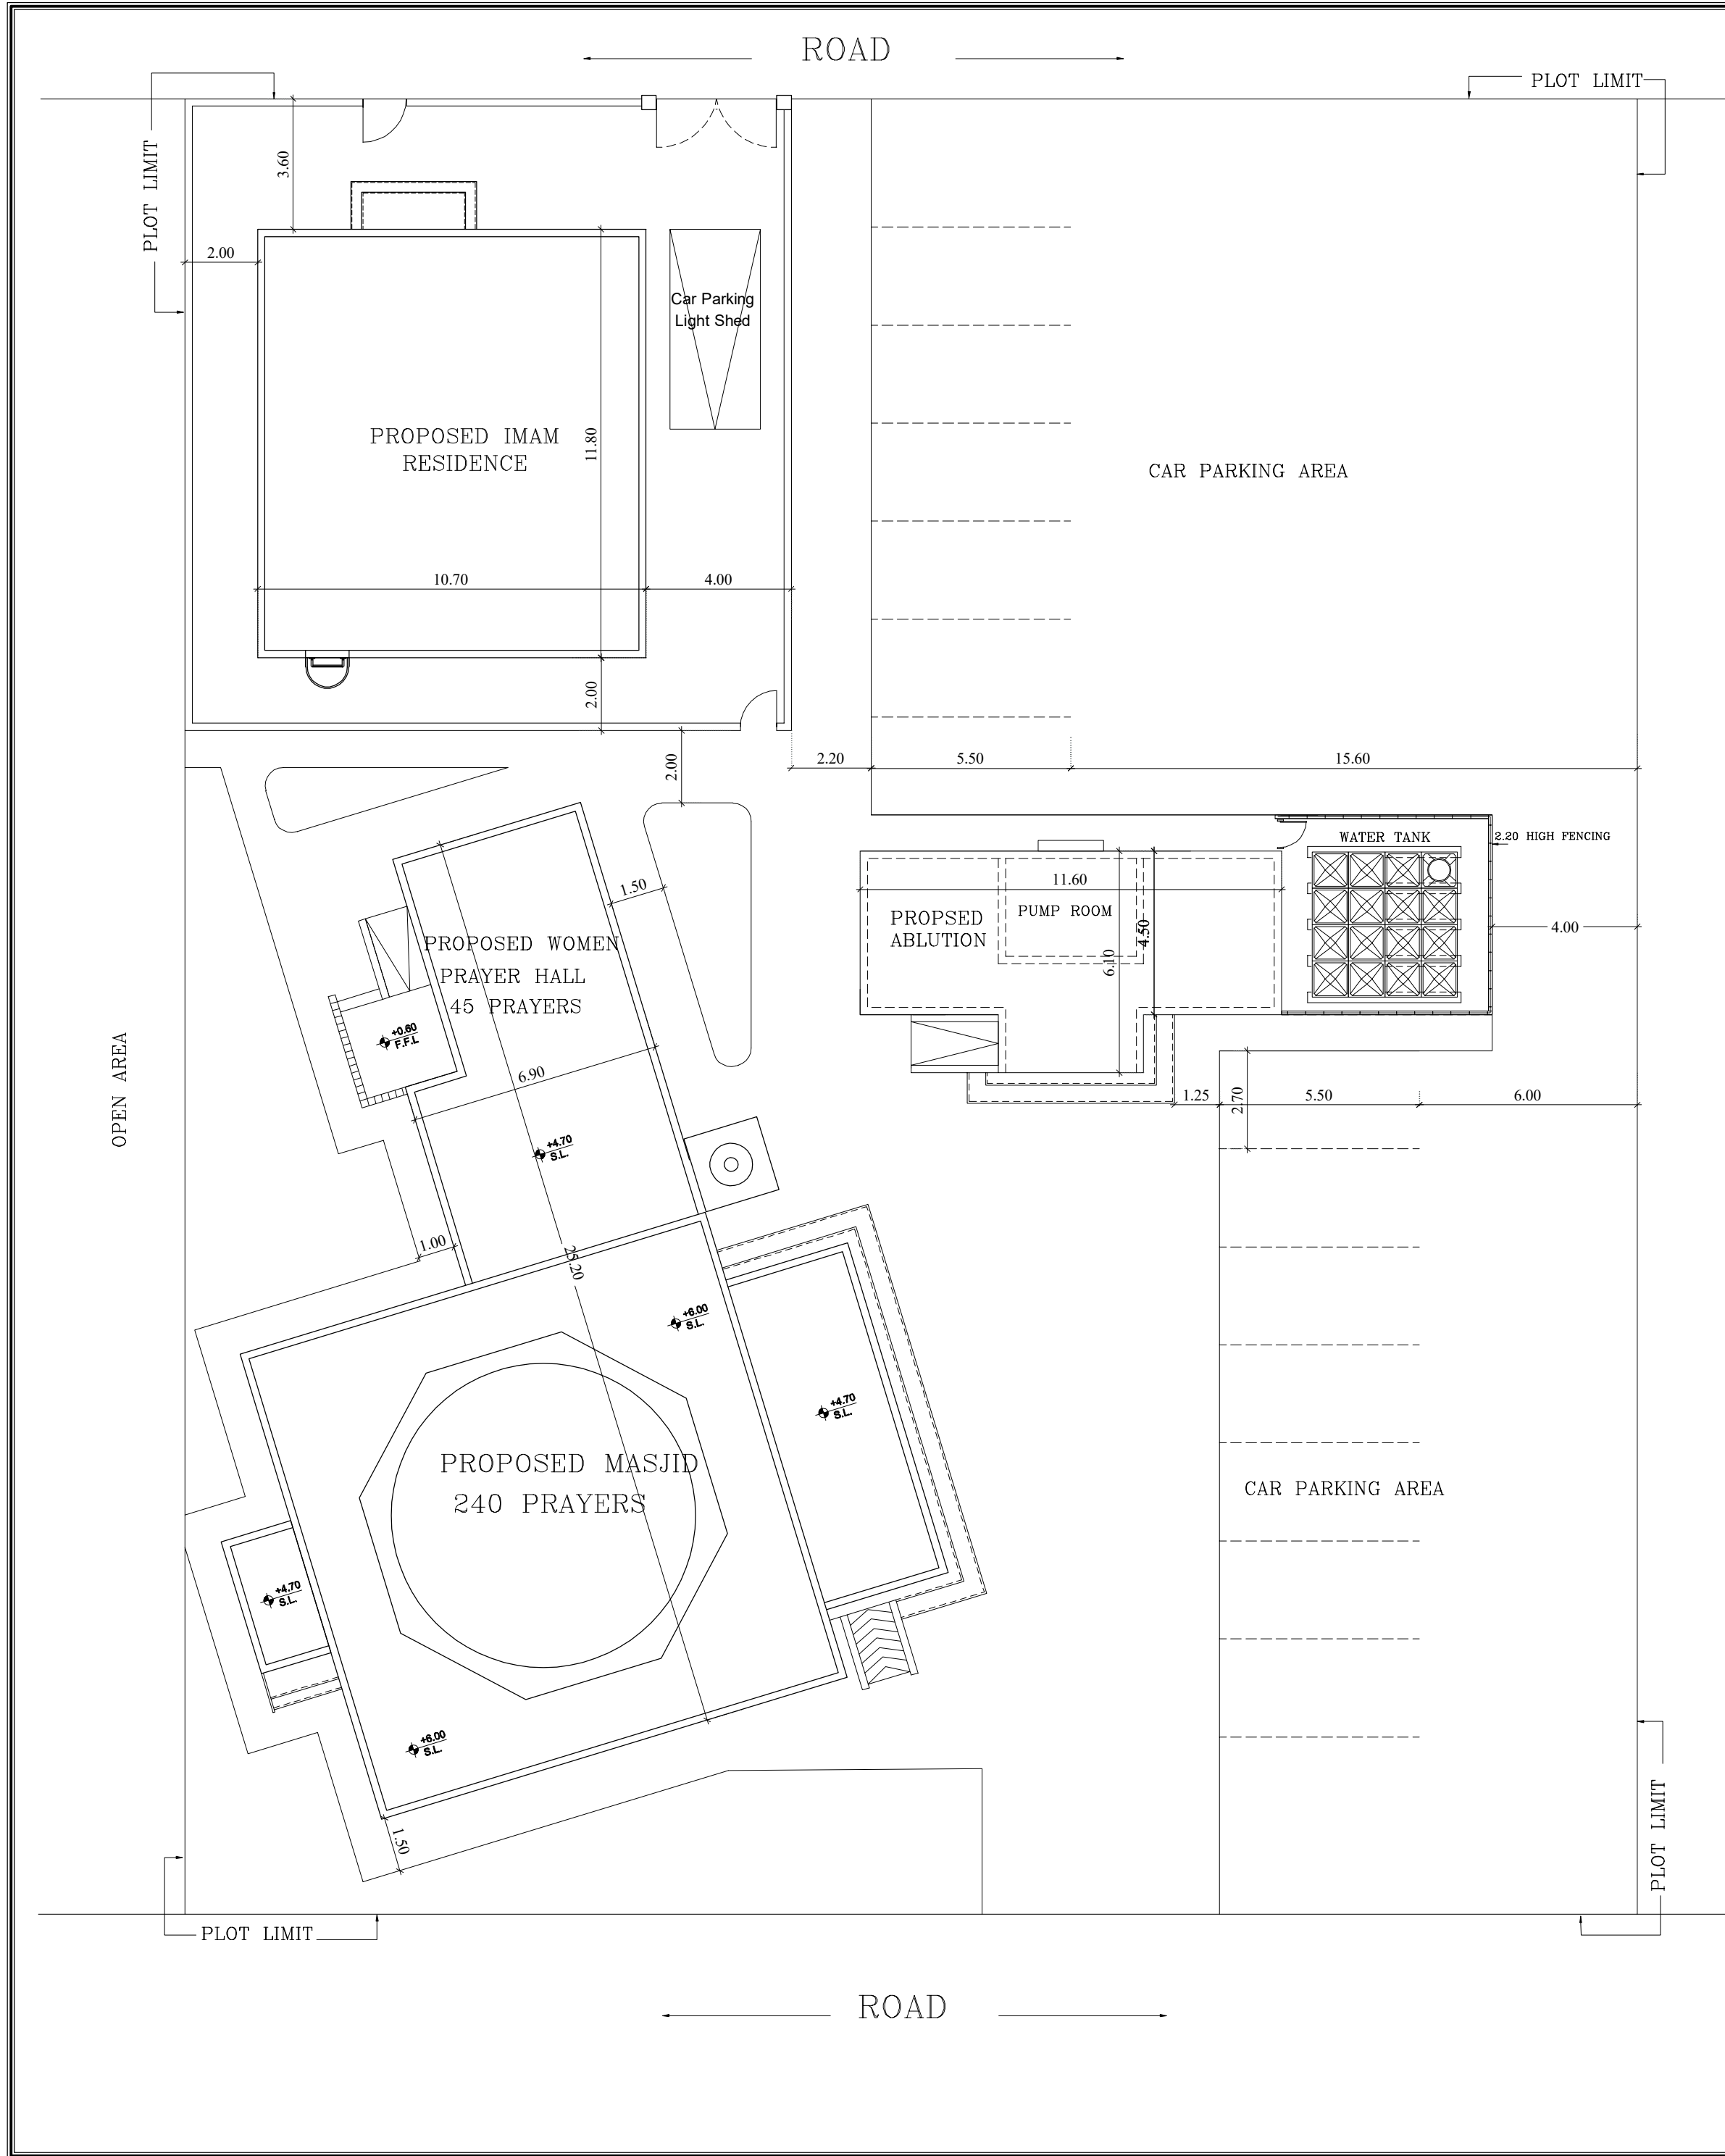

GOVERNMENT OF SHARJAH
Department Of Islamic Affairs

حكومة الشارقة
دائرة الشؤون الإسلامية

التاريخ: 16 ذو القعدة 1442هـ
الموافق: 27 يونيو 2021م
المرجع: بر/أهـ / 936 / 2021

الموقع: سعادة المهندس / خالد بطي عبيد بن بطي
رئيس دائرة التخطيط و المساحة

الاسم على كورحة الدور ك: يوجد:

الموضوع: مخططات المساجد مسابقة الاعتماد

تهديكم الدائرة أطيب تحياتها وتتمنياتها لكم بدوام التوفيق والسداد، هذا وبالإشارة إلى الموضوع أعلاه، يرجى التكرم بالإيجاز إلى جهة الاختصاص لديكم باعتماد مخططات النماذج التالية:

اسم النموذج	م
SIA - SM-01	1
SIA - SM-02	2
SIA - SM-03	3
SIA - SM-04	4
SIA - SM-05	5
SIA - SM-06	6

وحيث أن هذه النماذج سيتم إستخدامها بشكل متكرر في مشاريع دائرة الشؤون الإسلامية بالإمارة، يرجى التفضل بإعفاء مصكّب / الماسة للاستشارات الهندسية من رسوم اعتماد المخططات، مع تسليمه المخططات الأصلية المعتمدة من قبلكم. شاكرين لكم حسن تعاونكم معنا ، ، ،

لمزيد من الاستفسار يرجى الاتصال على :

المهندس / محمد عطية ، هاتف رقم 0558049138 - الماسة للاستشارات الهندسية.

المهندس / عبدالله أبو بكر الياسي ، هاتف رقم 0551736666 - دائرة الشؤون الإسلامية

وتغذيا بقرينة الإحترام والتقدير،،،

عبدالله خليفة يعروف السبوسي
رئيس الدائرة

Hand: 05058888971 | Tel: 0971 6 6361101 | برائ: 0971 6 6361101 | Fax: 0971 6 6361101 | Email: info@sia.gov.ae | Islamic_affairs | www.sia.gov.ae | 056 1888 292 | P.O. Box: 1087 | ص ب: 1087 | الرقم المجاني: 800 17



Built Up Area Schedule			
S.NO	FLOOR DETAILS	AREA	
		SQ.M	SQ.FT
1	Masjid Area	302.14	3251.05
2	Ablution Block Area	66.50	715.54
3	Imam House Area	126.26	1358.56
Total Built Up Area		494.90	5325.15

- GENERAL NOTES:**
- IT IS NOT ALLOWED TO REPRODUCE THE SHEETS CONTENTS IN ANY FORM EXCEPT FOR THE PURPOSE FOR WHICH IT IS INTENDED.
 - THESE DRAWINGS ARE DIAGRAMMATIC AND SHALL NOT BE SCALED. ADDITIONAL DATA SHALL BE REQUESTED FROM THE CONSULTANCY THROUGH WRITTEN CLARIFICATION. VERIFY ALL EXISTING CONDITIONS AND DIMENSIONS BEFORE PROCEEDING WITH ANY PORTION OF ANY WORK.
 - NO CHANGES, MODIFICATIONS OR DEVIATIONS SHALL BE WRITTEN PERMISSION FROM **ALMASAH ENGINEERING CONSULTANTS**.
 - ALL WORK AS OUTLINED IN THESE DOCUMENTS, SHALL STRICTLY CONFORM TO ALL APPLICABLE CODES. IN THE EVENT OF A CONFLICT, THE MORE STRINGENT REQUIREMENT SHALL GOVERN AND BE MET.

SIA - SM-02

حكومة الشارقة
دائرة الشؤون الإسلامية

CONSULTANT STAMP

الماسية
للإستشارات الهندسية
مخططات فقط
AL-MASAH
Engineering Consultant
Drawings Only

الماسية
للإستشارات الهندسية
AL MASAH
Engineering Consultants

Sharjah 06 5 444 521 06 5 444 523 Office: 306, Al Faisal 2 Bldg., King Faisal St.

CLIENT: **GOVERNMENT OF SHARJAH - DEPARTMENT OF ISLAMIC AFFAIRS**

PROJECT: **(SIA - SM-02) PROPOSED MASJID + ABLUTION + IMAM HOUSE**

SHEET TITLE: **SETTING OUT PLAN**

ARCHITECT Arch. Mostafa Ramadan	TYPE	ARCHITECTURE
STRUCTURAL Eng : Mohamed Gomaa	SHEET No.	A - 01
CHECKED BY Eng : Mohamed Attia	Location :	
SCALE 1:100	DATE March - 2022	Project No.

GENERAL NOTES:

1. IT IS NOT ALLOWED TO REPRODUCE THE SHEETS CONTENTS IN ANY FORM EXCEPT FOR THE PURPOSE FOR WHICH IT IS INTENDED.
2. THESE DRAWINGS ARE DIAGRAMMATIC AND SHALL NOT BE SCALED. ADDITIONAL DATA SHALL BE REQUESTED FROM THE CONSULTANCY THROUGH WRITTEN CLARIFICATION. VERIFY ALL EXISTING CONDITIONS AND DIMENSIONS BEFORE PROCEEDING WITH ANY PORTION OF ANY WORK.
3. NO CHANGES, MODIFICATIONS OR DEVIATIONS SHALL BE WRITTEN PERMISSION FROM **ALMASAH ENGINEERING CONSULTANTS**.
4. ALL WORK AS OUTLINED IN THESE DOCUMENTS, SHALL STRICTLY CONFORM TO ALL APPLICABLE CODES. IN THE EVENT OF A CONFLICT, THE MORE STRINGENT REQUIREMENT SHALL GOVERN AND BE MET.

SIA - SM-02



حكومة الشارقة
دائرة الشؤون الإسلامية

CONSULTANT STAMP



Sharjah ☎ 06 5 444 521 ☎ 06 5 444 523 Office: 306, Al Faisal 2 Bldg., King Faisal St.

CLIENT:

GOVERNMENT OF SHARJAH -
DEPARTMENT OF ISLAMIC AFFAIRS


PROJECT:

(SIA - SM-02)
PROPOSED MASJID + ABLUTION +
IMAM HOUSE

SHEET TITLE:

GROUND FLOOR PLAN

ARCHITECT Arch. Mostafa Ramadan	TYPE ARCHITECTURE
STRUCTURAL Eng : Mohamed Gomaa	SHEET No. A - 02
CHECKED BY Eng : Mohamed Attia	Location : Plot No :
SCALE 1:100	DATE March - 2022
	Project No.

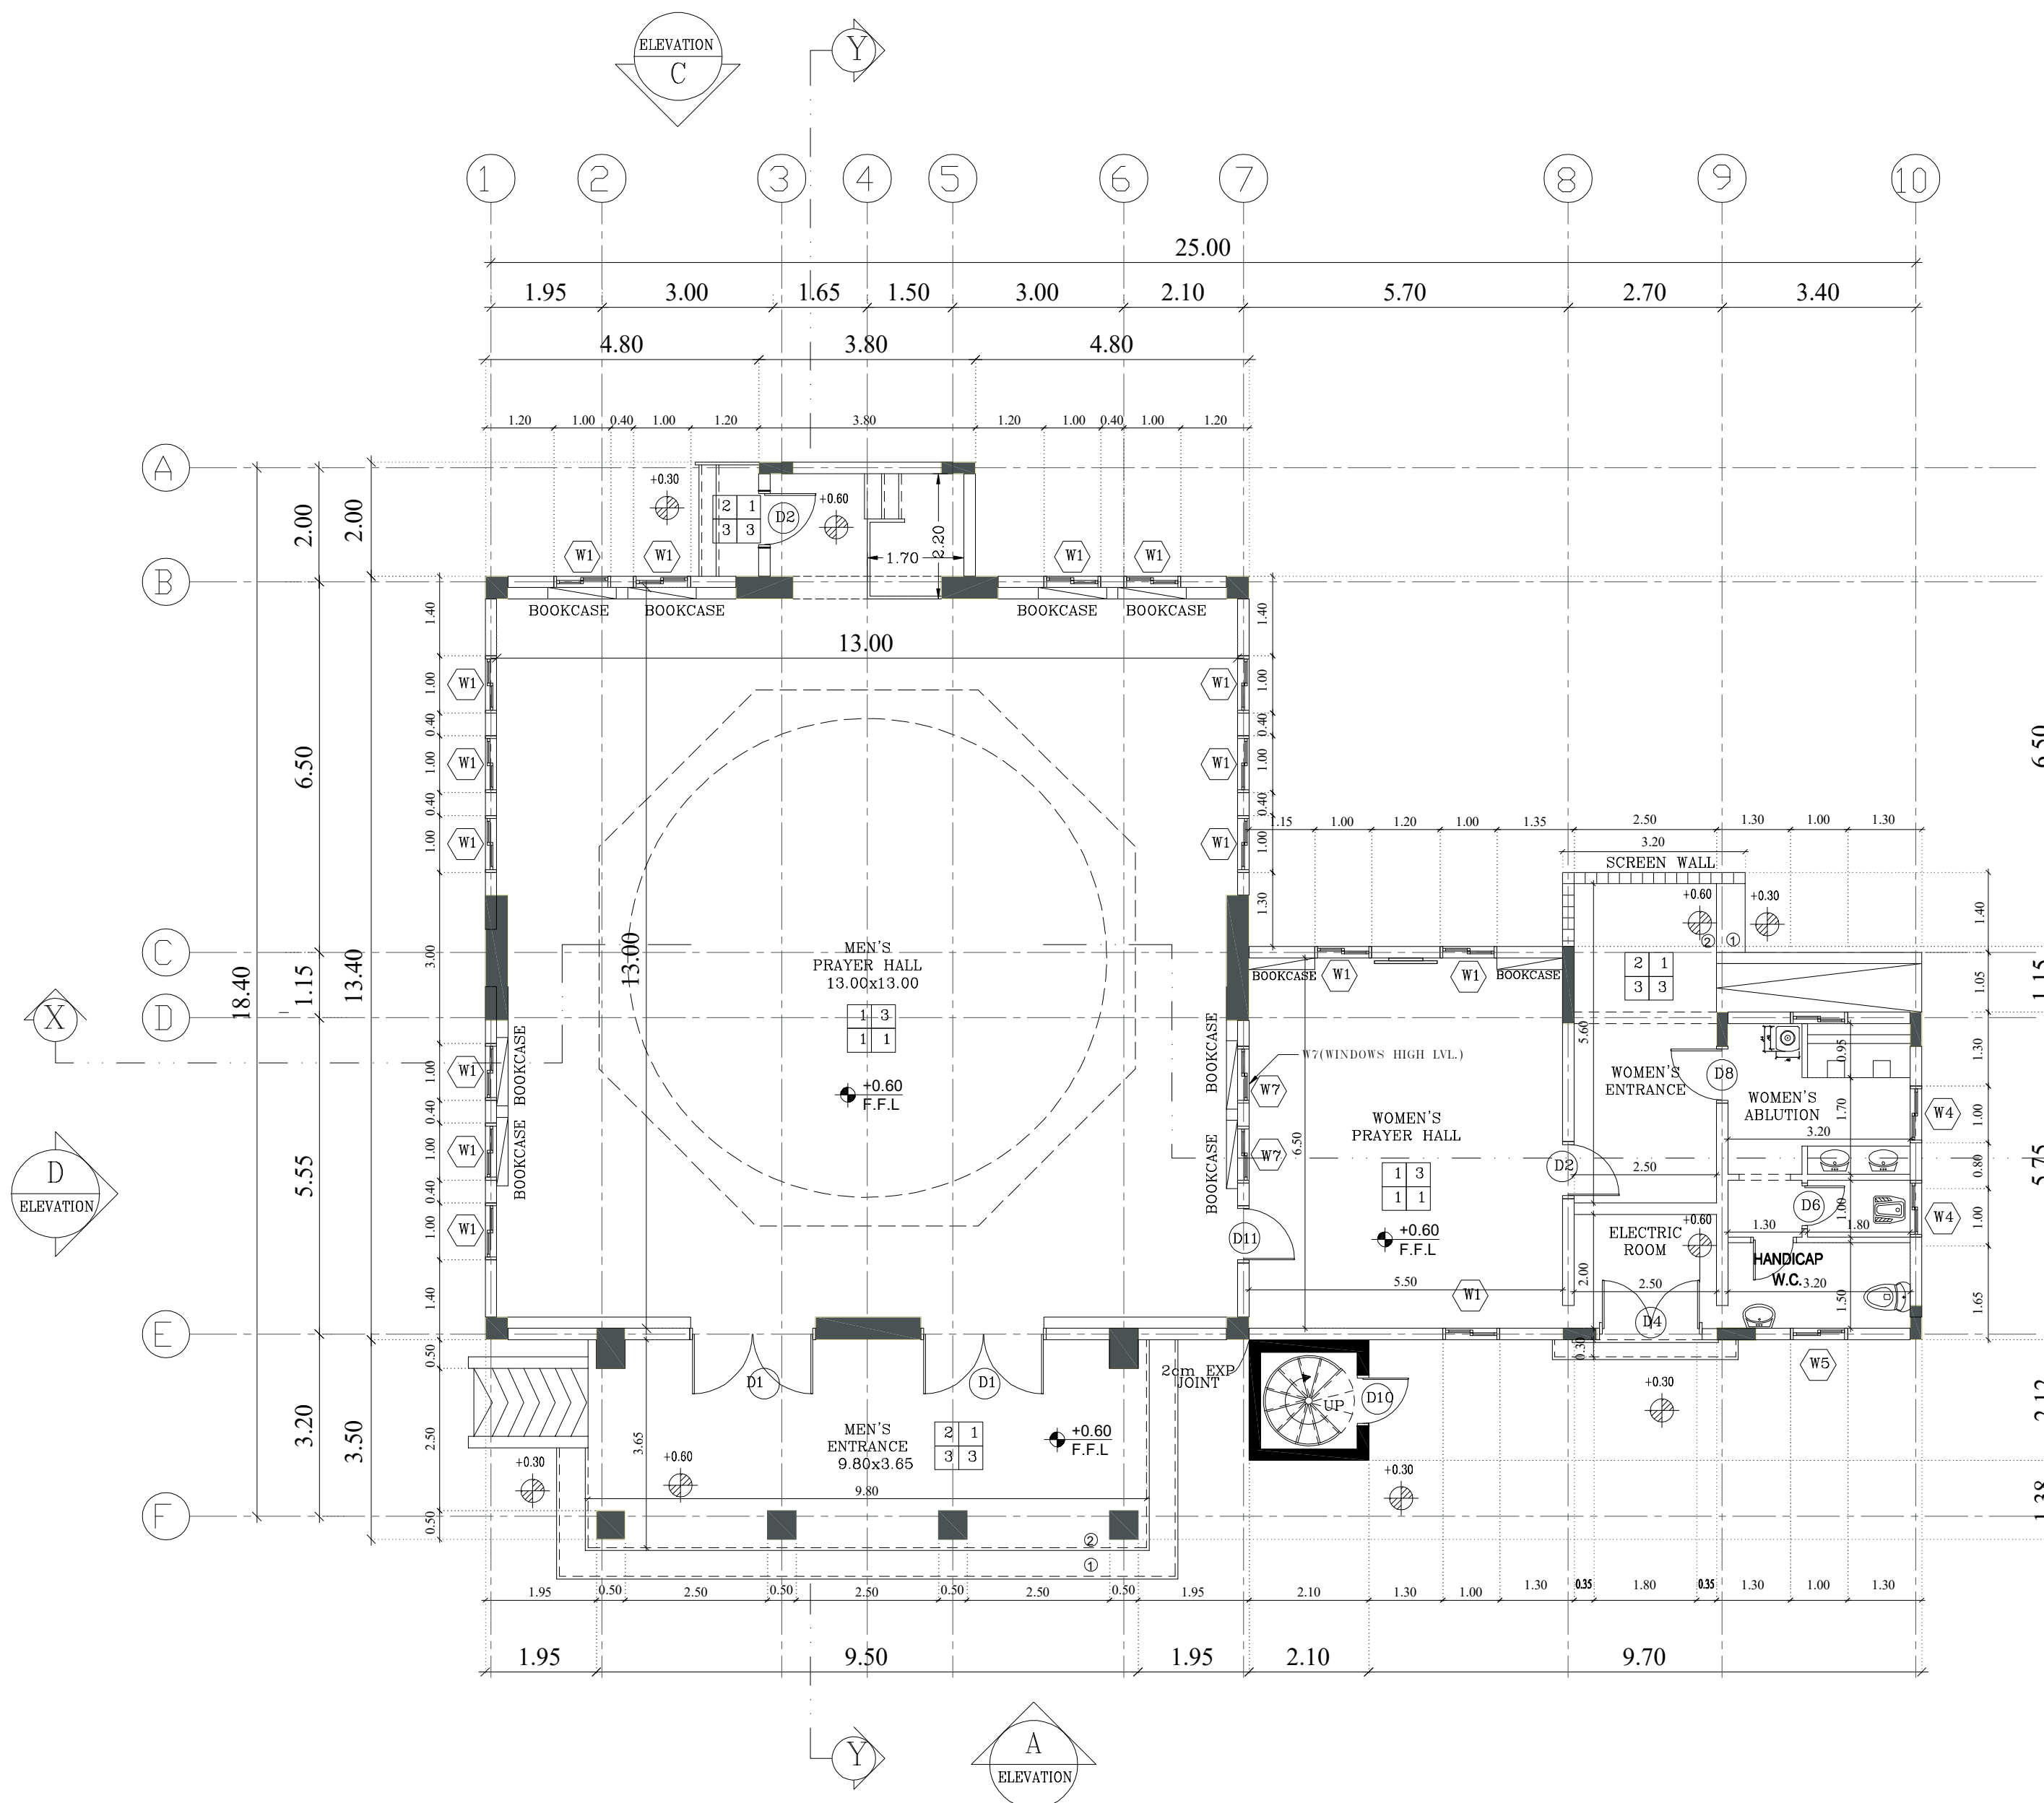

GENERAL NOTES:

1. IT IS NOT ALLOWED TO REPRODUCE THE SHEETS CONTENTS IN ANY FORM EXCEPT FOR THE PURPOSE FOR WHICH IT IS INTENDED.
2. THESE DRAWINGS ARE DIAGRAMMATIC AND SHALL NOT BE SCALED. ADDITIONAL DATA SHALL BE REQUESTED FROM THE CONSULTANCY THROUGH WRITTEN CLARIFICATION. VERIFY ALL EXISTING CONDITIONS AND DIMENSIONS BEFORE PROCEEDING WITH ANY PORTION OF ANY WORK.
3. NO CHANGES, MODIFICATIONS OR DEVIATIONS SHALL BE WRITTEN PERMISSION FROM **ALMASAH ENGINEERING CONSULTANTS**.
4. ALL WORK AS OUTLINED IN THESE DOCUMENTS, SHALL STRICTLY CONFORM TO ALL APPLICABLE CODES. IN THE EVENT OF A CONFLICT, THE MORE STRINGENT REQUIREMENT SHALL GOVERN AND BE MET.

SIA - SM-02



حكومة الشارقة
دائرة الشؤون الإسلامية

CONSULTANT STAMP



Sharjah ☎ 06 5 444 521 ☎ 06 5 444 523 Office: 306, Al Fisal 2 Bldg., King Faisal St.

CLIENT:

GOVERNMENT OF SHARJAH -
DEPARTMENT OF ISLAMIC AFFAIRS


PROJECT:


(SIA - SM-02)
PROPOSED MASJID + ABLUTION +
IMAM HOUSE

SHEET TITLE:

ROOF FLOOR PLAN

ARCHITECT Arch. Mostafa Ramadan	TYPE ARCHITECTURE
STRUCTURAL Eng : Mohamed Gomaa	SHEET No. A - 03
CHECKED BY Eng : Mohamed Attia	Location : Plot No :
SCALE 1:100	DATE March - 2022
Project No.	

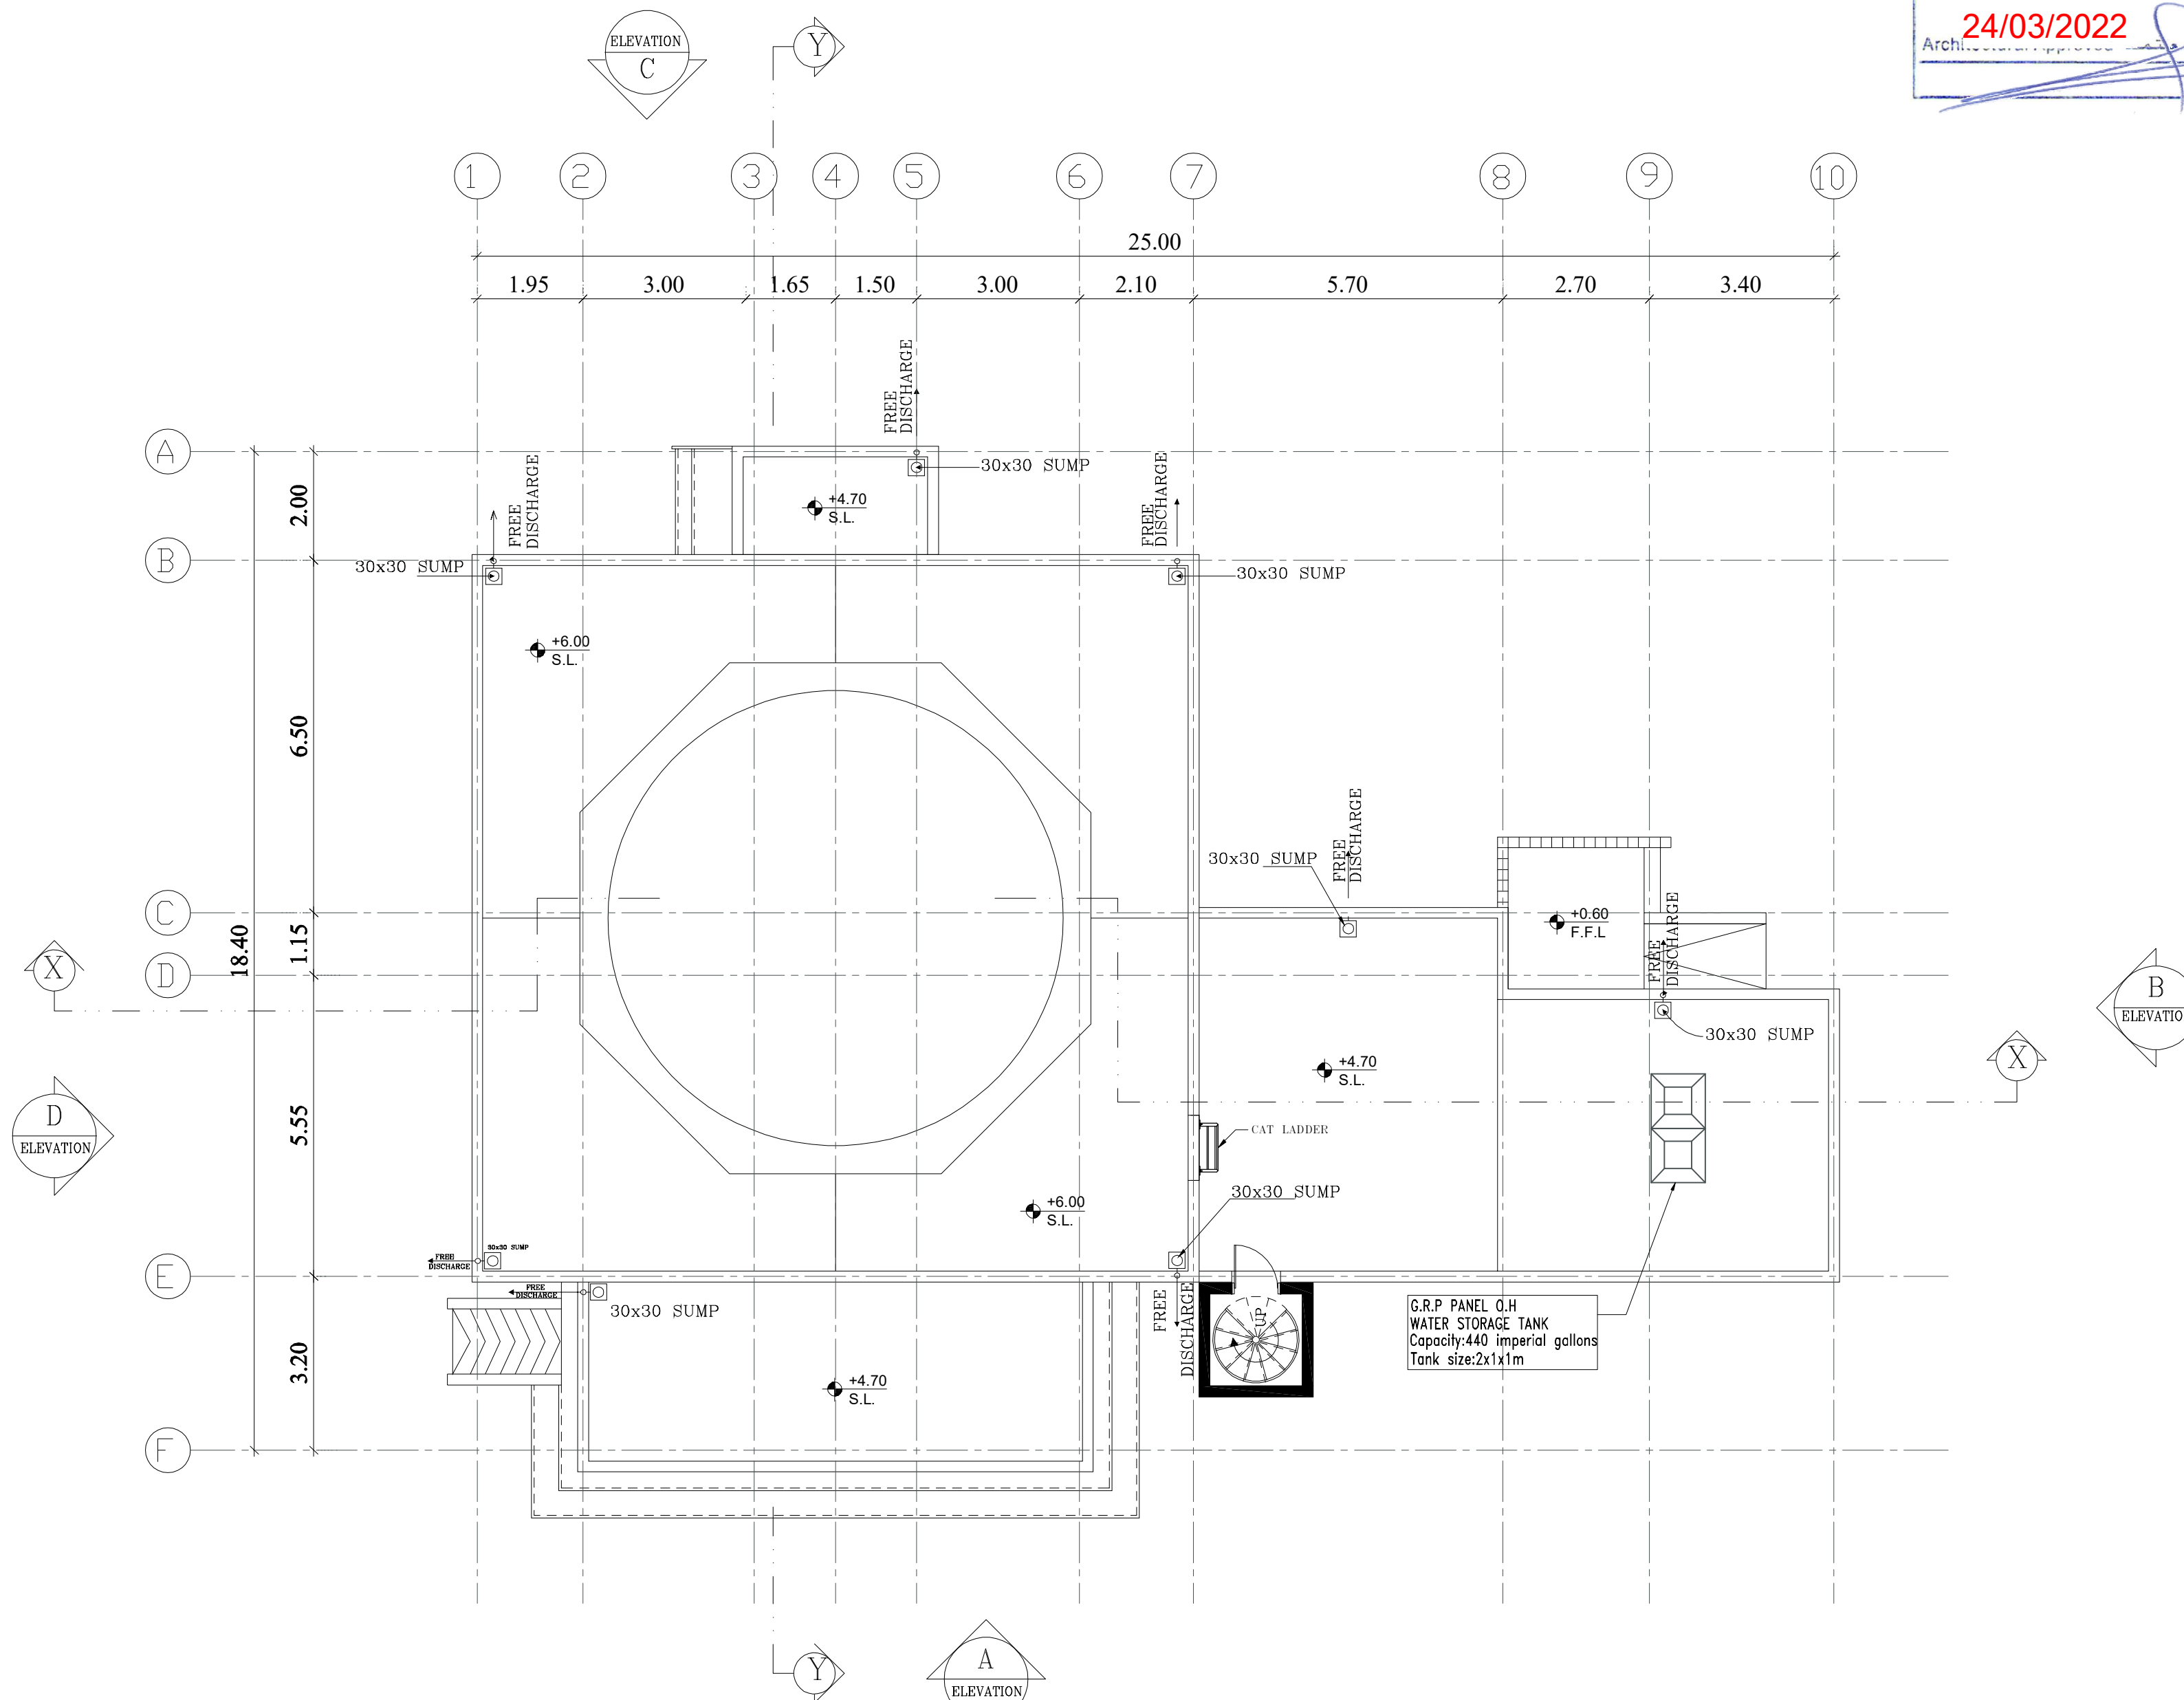

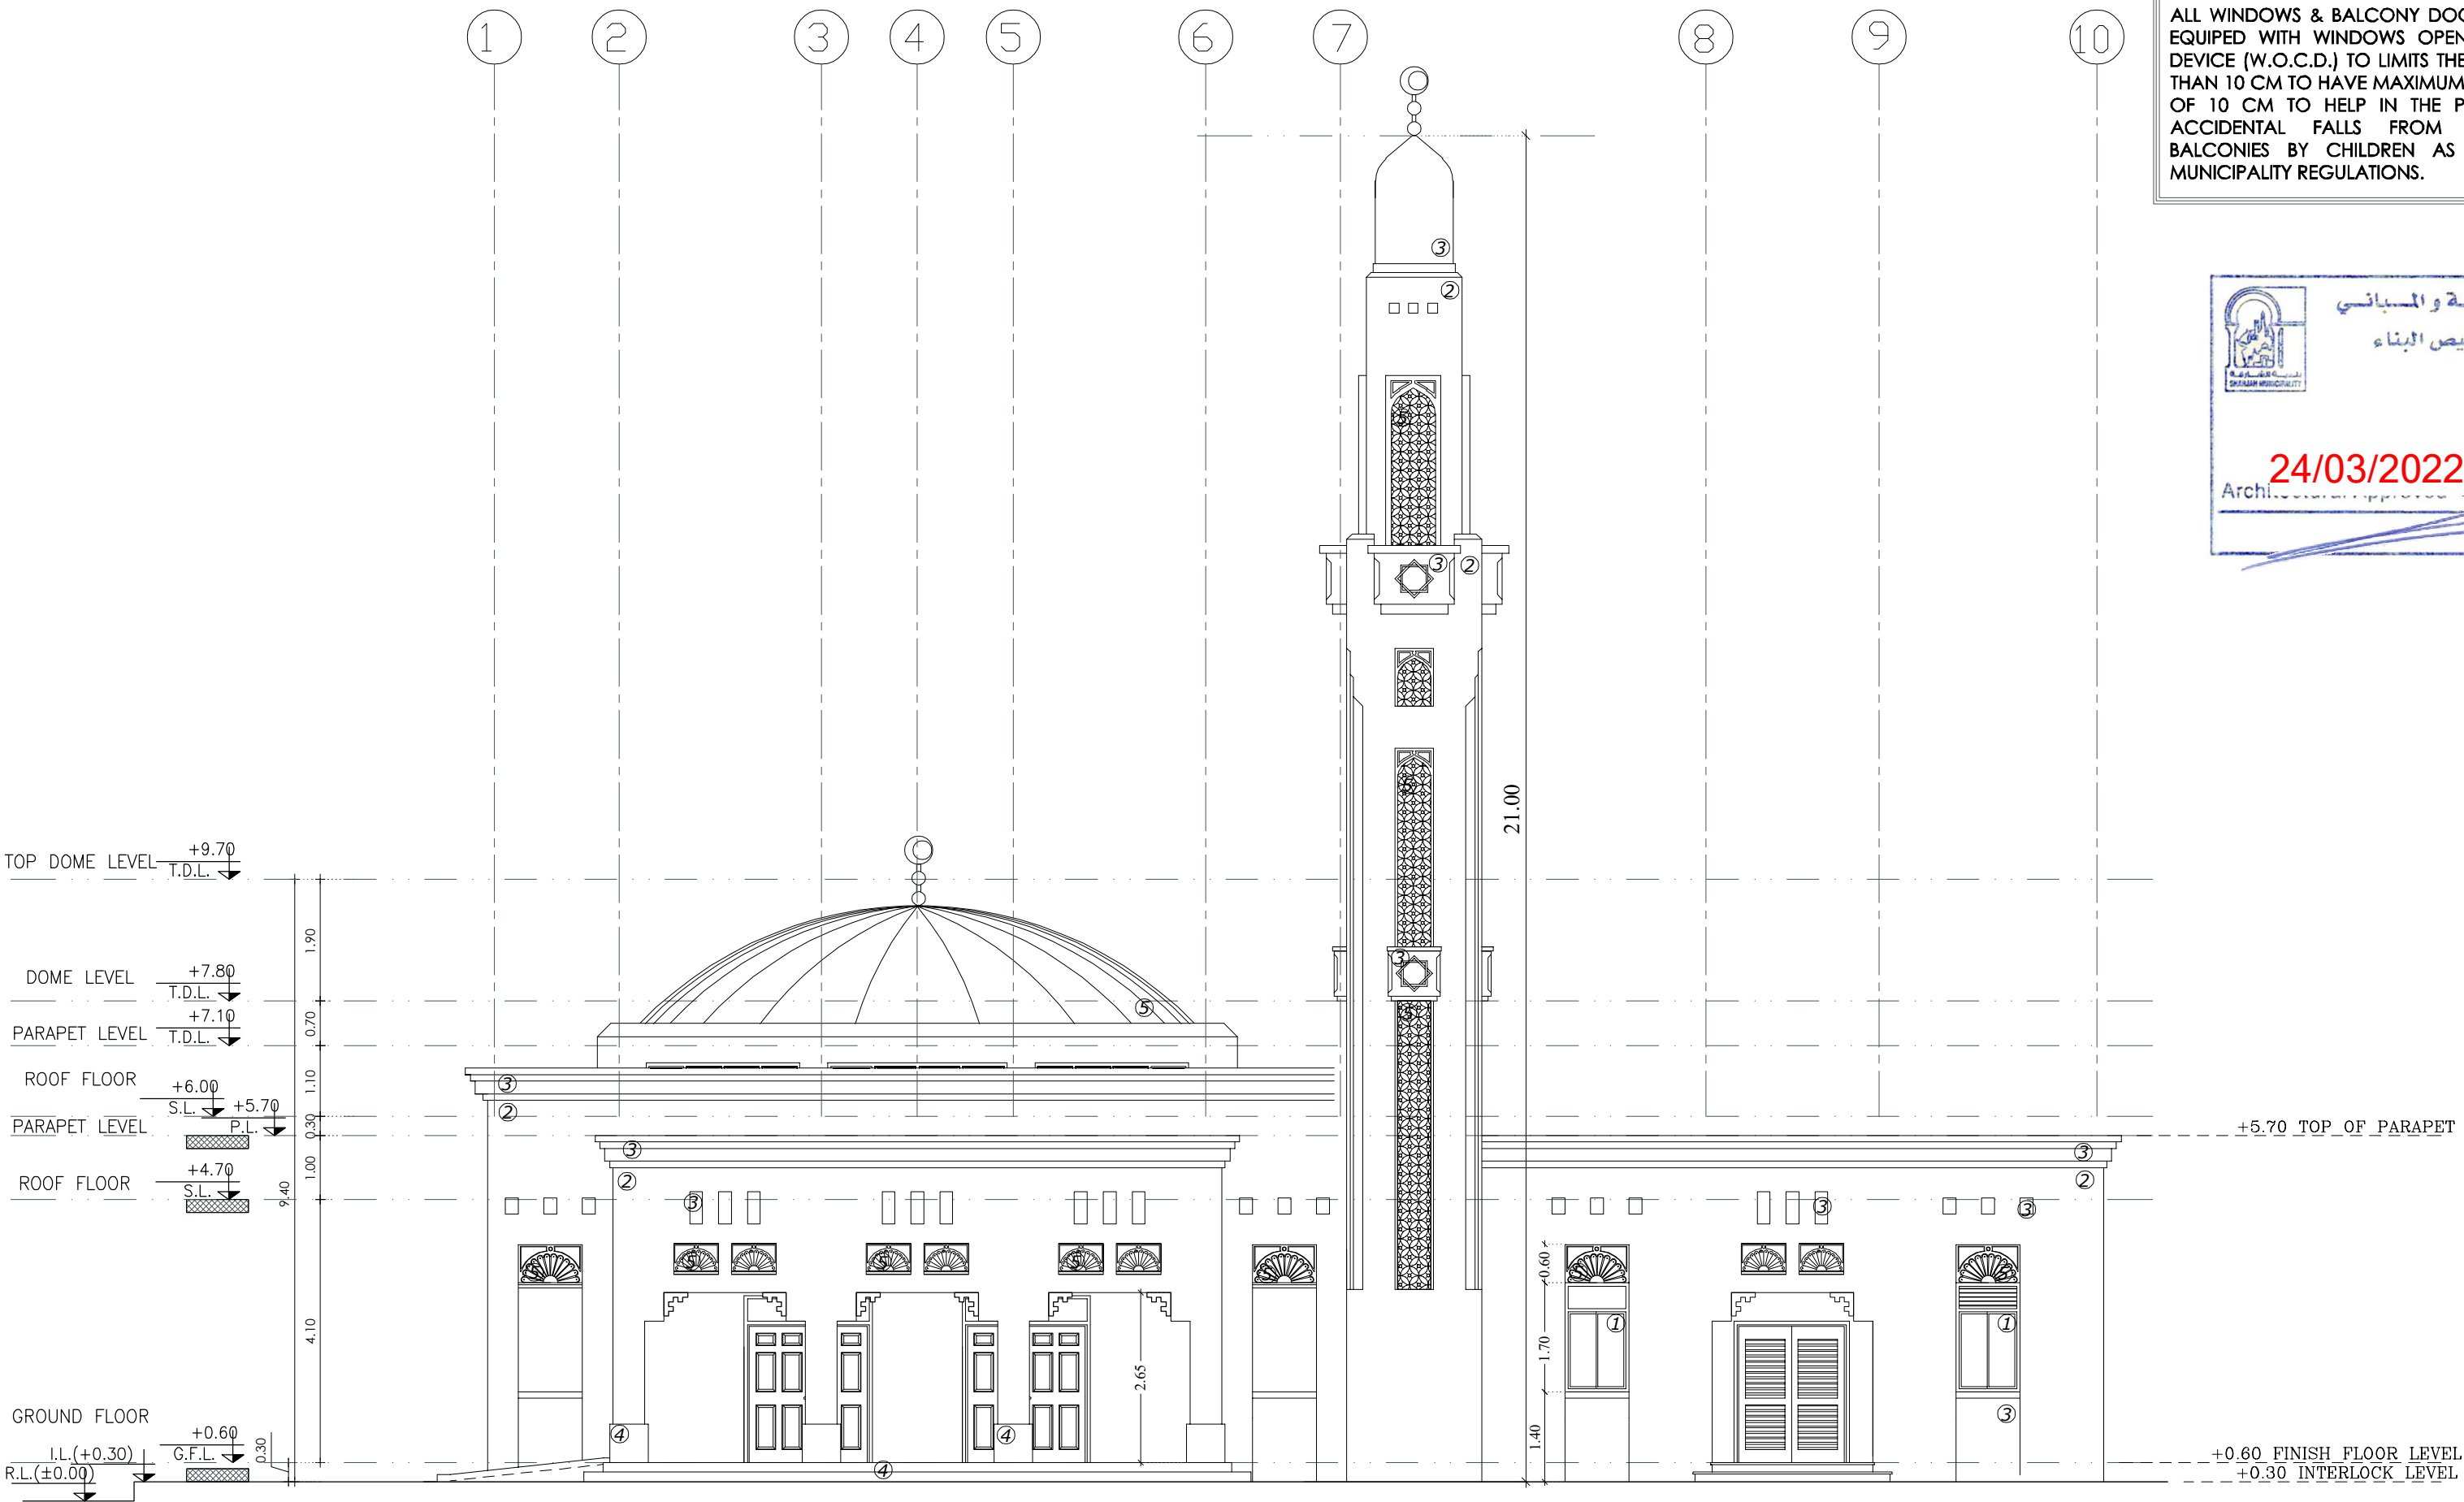

ELEVATION -A

ELEVATION FINISHES

- 1- REFLECTIVE GLASS
- 2- GRAFFIO DECOR WHITE PAINT OR STONE CLADDING
- 3- GRAFFIO DECOR OFF WHITE PAINT OR STONE CLADDING
- 4- GRANITE FINISHING
- 5- G.R.C.

ALL WINDOWS & BALCONY DOORS SHOULD BE EQUIPED WITH WINDOWS OPENING CONTROL DEVICE (W.O.C.D.) TO LIMITS THE OPENING LESS THAN 10 CM TO HAVE MAXIMUM OPENING LIMIT OF 10 CM TO HELP IN THE PREVENTION OF ACCIDENTAL FALLS FROM WINDOWS & BALCONIES BY CHILDREN AS PER SHARJAH MUNICIPALITY REGULATIONS.



GENERAL NOTES:


1. IT IS NOT ALLOWED TO REPRODUCE THE SHEETS CONTENTS IN ANY FORM EXCEPT FOR THE PURPOSE FOR WHICH IT IS INTENDED.
2. THESE DRAWINGS ARE DIAGRAMMATIC AND SHALL NOT BE SCALED. ADDITIONAL DATA SHALL BE REQUESTED FROM THE CONSULTANCY THROUGH WRITTEN CLARIFICATION. VERIFY ALL EXISTING CONDITIONS AND DIMENSIONS BEFORE PROCEEDING WITH ANY PORTION OF ANY WORK.
3. NO CHANGES, MODIFICATIONS OR DEVIATIONS SHALL BE WRITTEN PERMISSION FROM **ALMASAH ENGINEERING CONSULTANTS**.
4. ALL WORK AS OUTLINED IN THESE DOCUMENTS, SHALL STRICTLY CONFORM TO ALL APPLICABLE CODES. IN THE EVENT OF A CONFLICT, THE MORE STRINGENT REQUIREMENT SHALL GOVERN AND BE MET.

SIA - SM-02



حكومة الشارقة
دائرة الشؤون الإسلامية

CONSULTANT STAMP

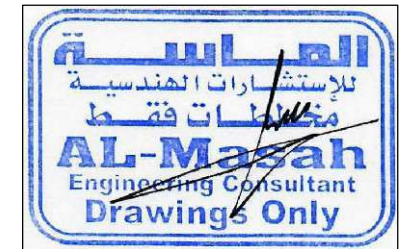

Sharjah ☎ 06 5 444 521 ☎ 06 5 444 523 📍 Office: 306, Al Faisal 2 Bldg., King Faisal St.

CLIENT:

GOVERNMENT OF SHARJAH -
DEPARTMENT OF ISLAMIC AFFAIRS

PROJECT:

(SIA - SM-02)
PROPOSED MASJID + ABLUTION +
IMAM HOUSE

SHEET TITLE:

ELEVATION -A

ARCHITECT

Arch. Mostafa Ramadan

TYPE

ARCHITECTURE

STRUCTURAL

Eng : Mohamed Gomaa

SHEET

No.

A - 04

CHECKED BY

Eng : Mohamed Attia

Location :

Plot No :

SCALE


1:100

DATE

March - 2022

Project

No.

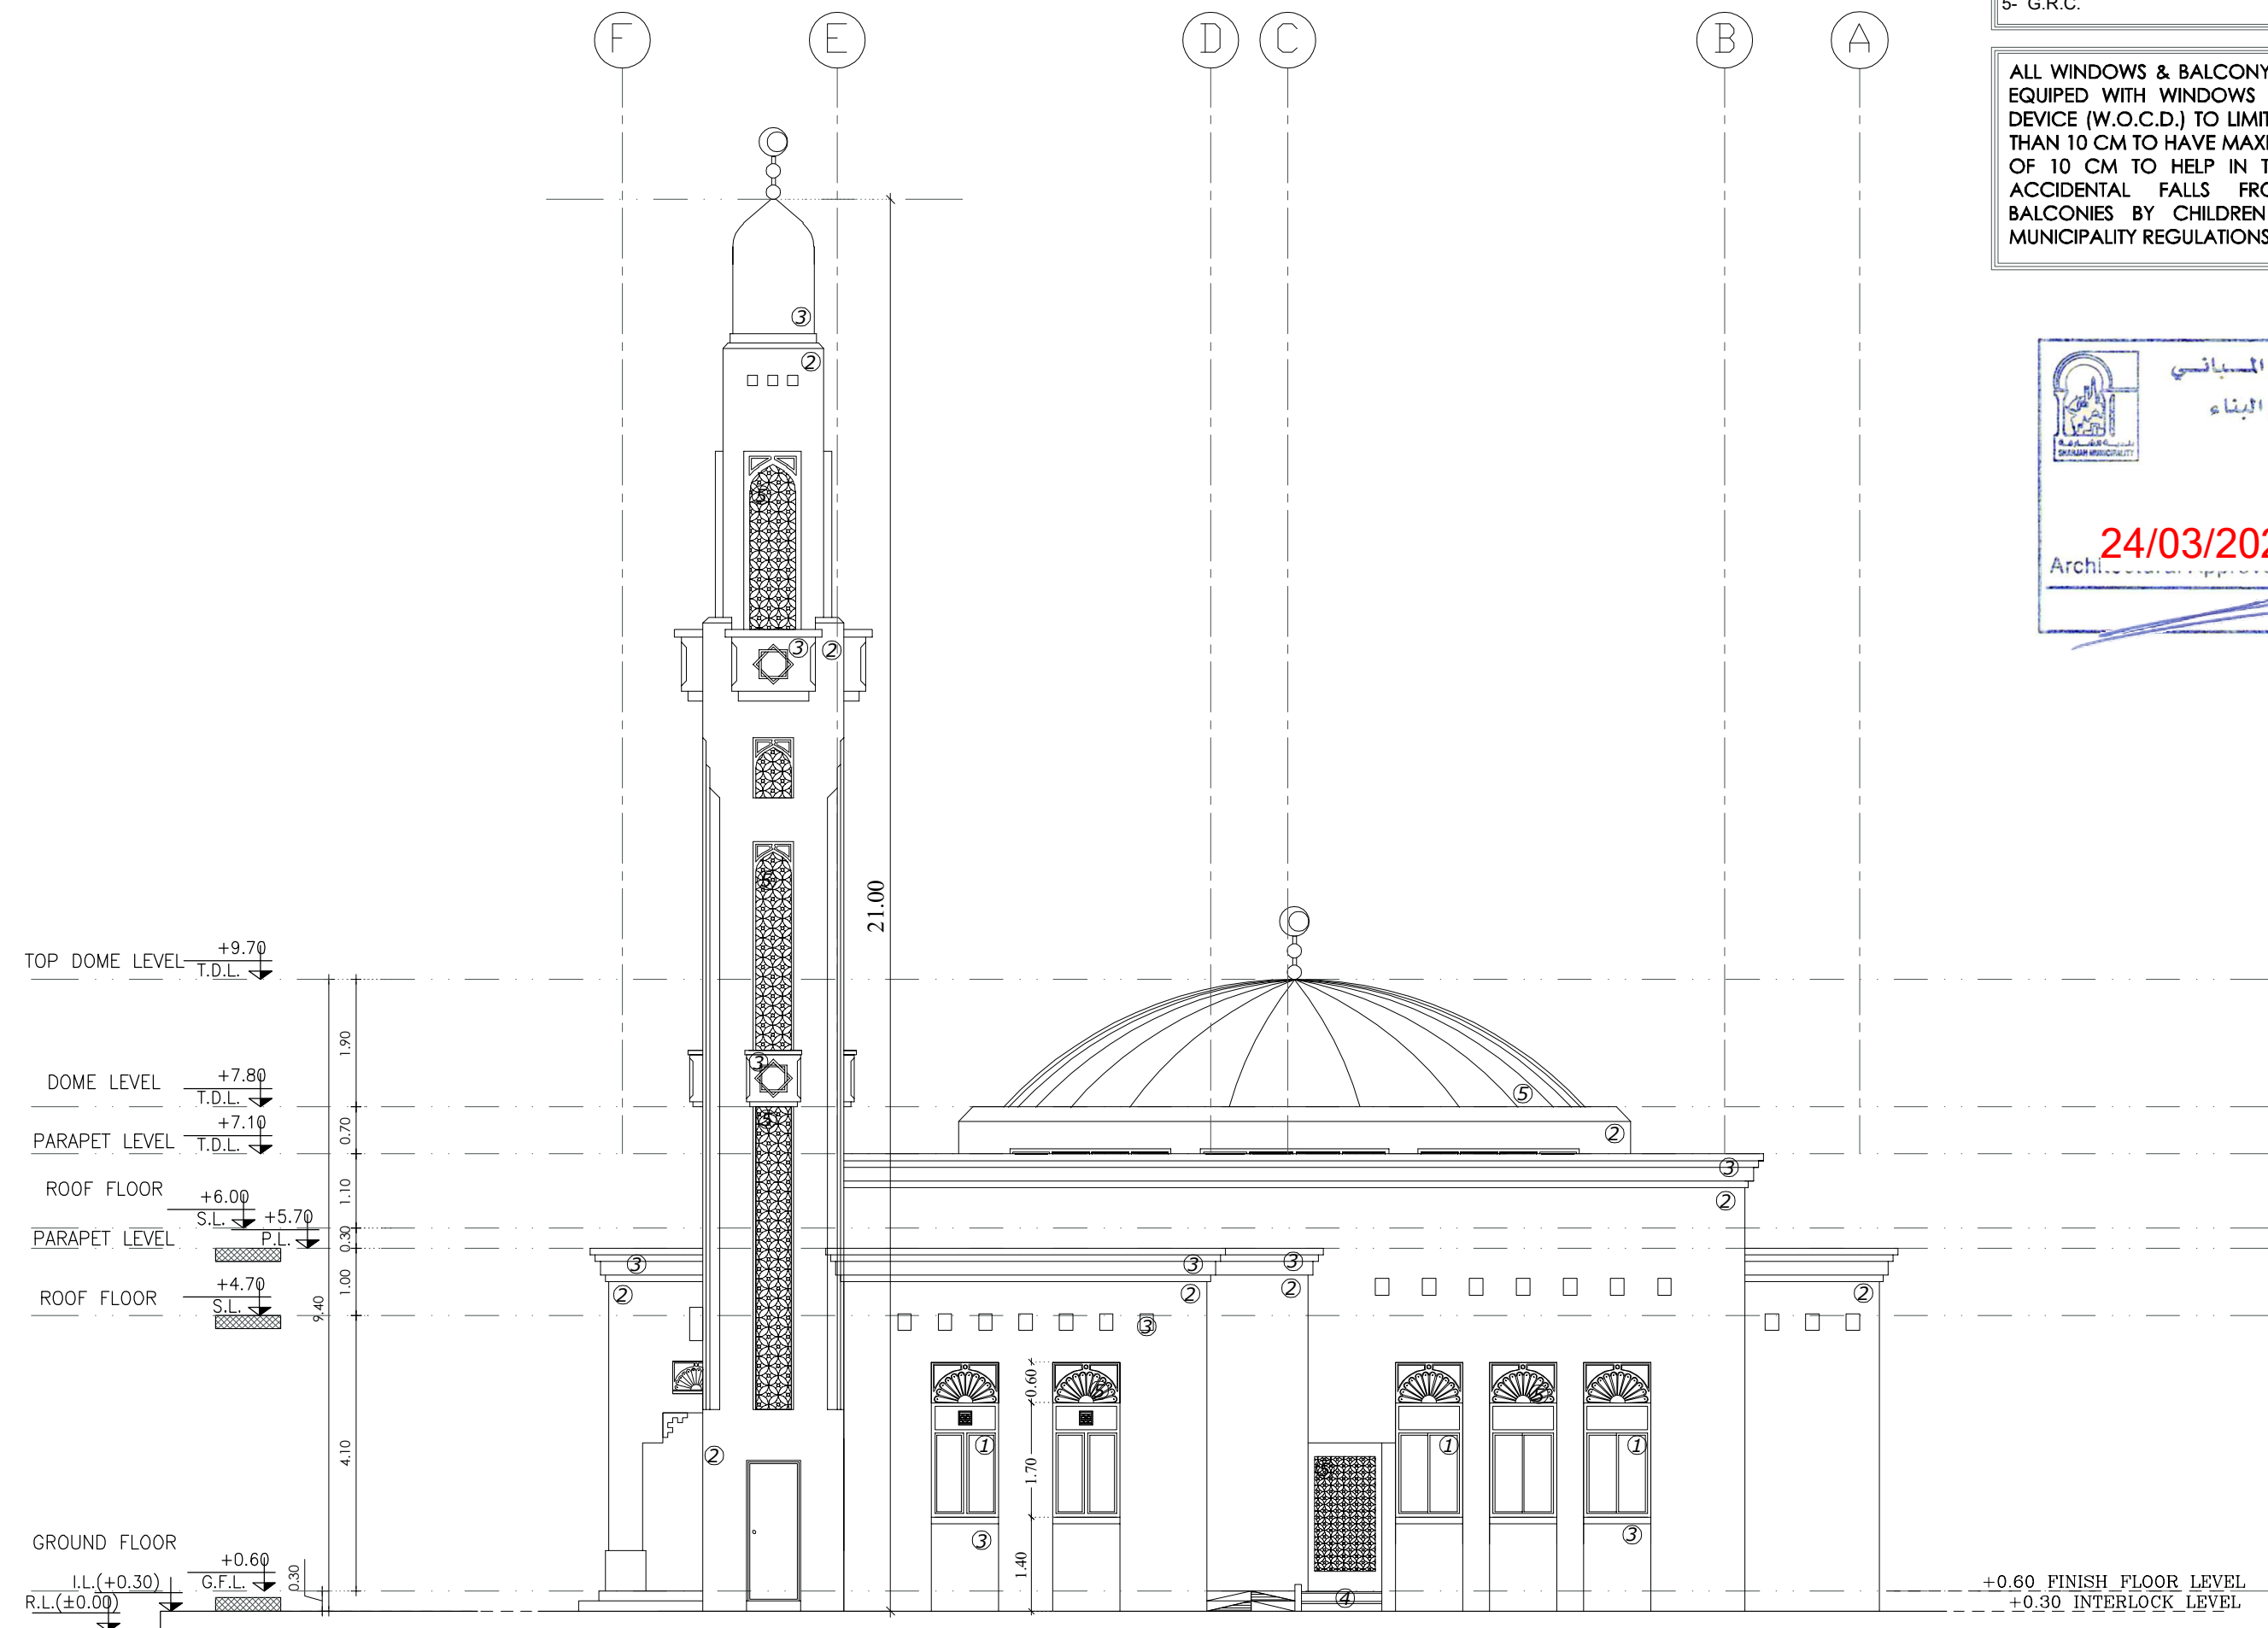

ELEVATION -B

ELEVATION FINISHES

- 1- REFLECTIVE GLASS
- 2- GRAFFIO DECOR WHITE PAINT OR STONE CLADDING
- 3- GRAFFIO DECOR OFF WHITE PAINT OR STONE CLADDING
- 4- GRANITE FINISHING
- 5- G.R.C.

ALL WINDOWS & BALCONY DOORS SHOULD BE EQUIPPED WITH WINDOWS OPENING CONTROL DEVICE (W.O.C.D.) TO LIMITS THE OPENING LESS THAN 10 CM TO HAVE MAXIMUM OPENING LIMIT OF 10 CM TO HELP IN THE PREVENTION OF ACCIDENTAL FALLS FROM WINDOWS & BALCONIES BY CHILDREN AS PER SHARJAH MUNICIPALITY REGULATIONS.



GENERAL NOTES:

1. IT IS NOT ALLOWED TO REPRODUCE THE SHEETS CONTENTS IN ANY FORM EXCEPT FOR THE PURPOSE FOR WHICH IT IS INTENDED.
2. THESE DRAWINGS ARE DIAGRAMMATIC AND SHALL NOT BE SCALED. ADDITIONAL DATA SHALL BE REQUESTED FROM THE CONSULTANCY THROUGH WRITTEN CLARIFICATION. VERIFY ALL EXISTING CONDITIONS AND DIMENSIONS BEFORE PROCEEDING WITH ANY PORTION OF ANY WORK.
3. NO CHANGES, MODIFICATIONS OR DEVIATIONS SHALL BE WRITTEN PERMISSION FROM **ALMASAH ENGINEERING CONSULTANTS**.
4. ALL WORK AS OUTLINED IN THESE DOCUMENTS, SHALL STRICTLY CONFORM TO ALL APPLICABLE CODES. IN THE EVENT OF A CONFLICT, THE MORE STRINGENT REQUIREMENT SHALL GOVERN AND BE MET.

SIA - SM-02



حُكُومَةُ الشَّارِقَةِ
دائرة الشؤون الإسلامية

CONSULTANT STAMP




CLIENT: **GOVERNMENT OF SHARJAH -
DEPARTMENT OF ISLAMIC AFFAIRS**

PROJECT: **(SIA - SM-02)
PROPOSED MASJID + ABLUTION +
IMAM HOUSE**

SHEET TITLE: **ELEVATION -B**

ARCHITECT Arch. Mostafa Ramadan	TYPE ARCHITECTURE
STRUCTURAL Eng : Mohamed Gomaa	SHEET No. A - 05
CHECKED BY Eng : Mohamed Attia	Location : Plot No : Project No.
SCALE 1:100	DATE March - 2022

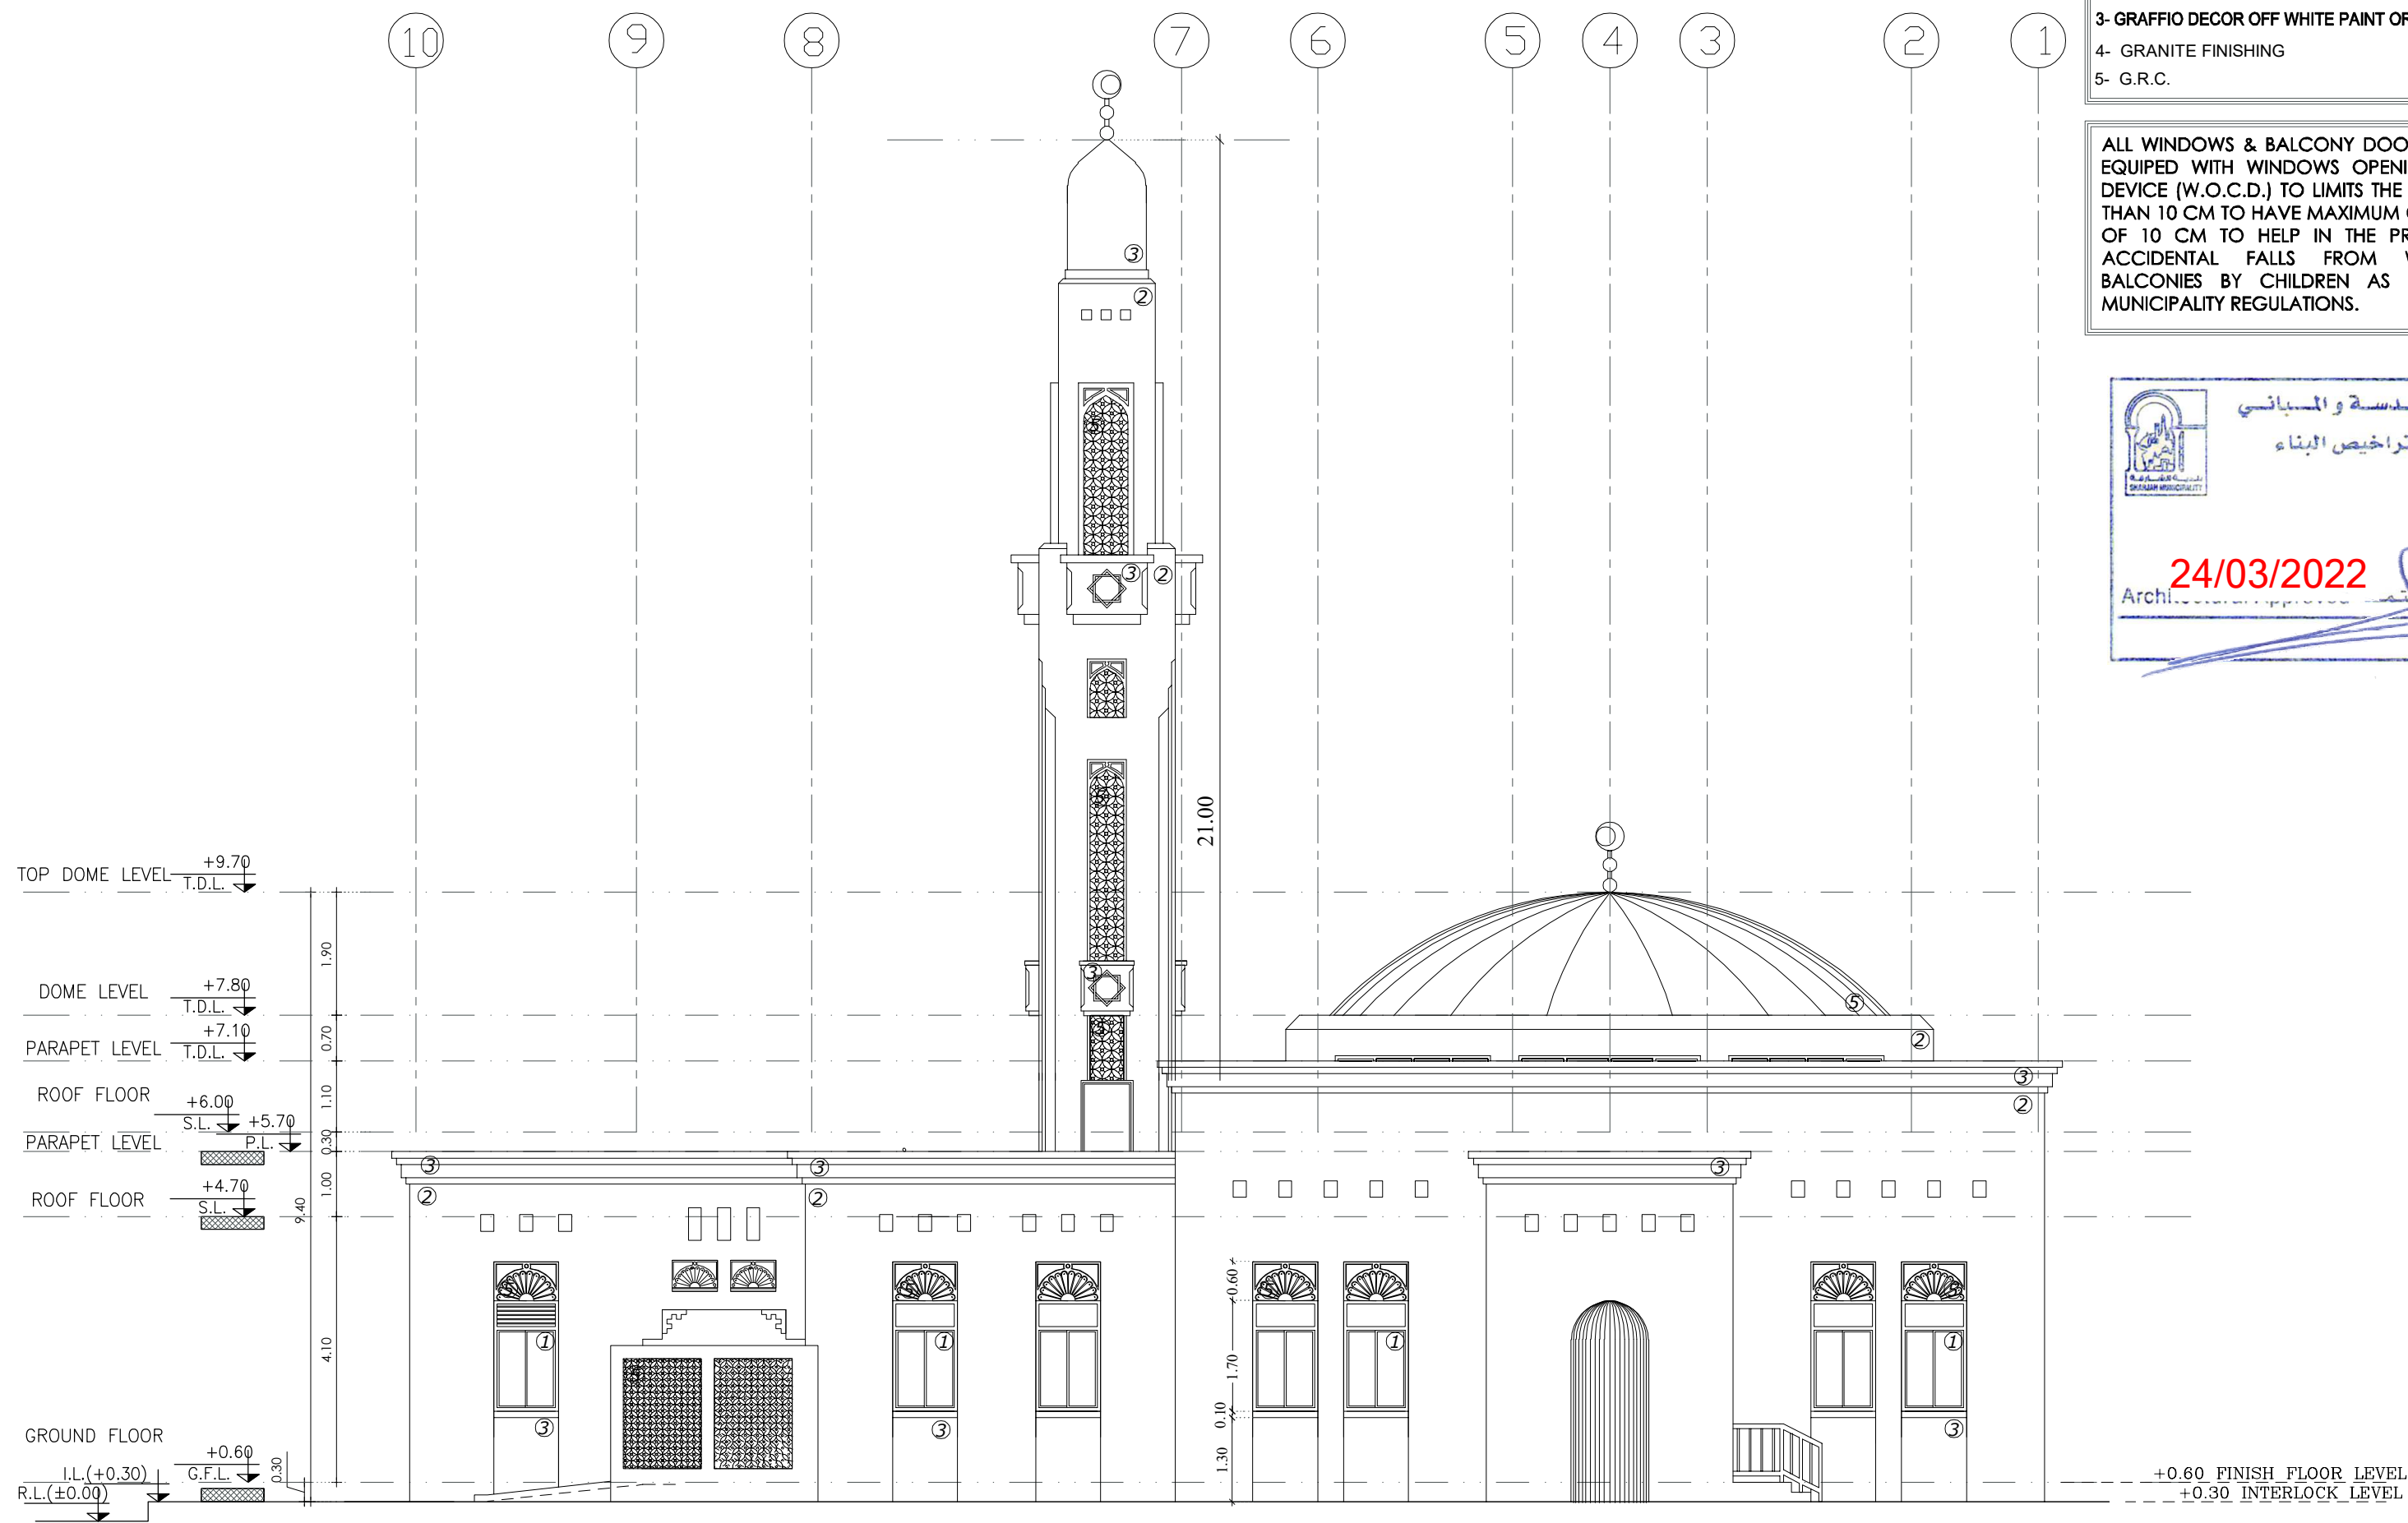

ELEVATION -C

- ELEVATION FINISHES**
- 1- REFLECTIVE GLASS
 - 2- GRAFFIO DECOR WHITE PAINT OR STONE CLADDING
 - 3- GRAFFIO DECOR OFF WHITE PAINT OR STONE CLADDING
 - 4- GRANITE FINISHING
 - 5- G.R.C.

ALL WINDOWS & BALCONY DOORS SHOULD BE EQUIPED WITH WINDOWS OPENING CONTROL DEVICE (W.O.C.D.) TO LIMITS THE OPENING LESS THAN 10 CM TO HAVE MAXIMUM OPENING LIMIT OF 10 CM TO HELP IN THE PREVENTION OF ACCIDENTAL FALLS FROM WINDOWS & BALCONIES BY CHILDREN AS PER SHARJAH MUNICIPALITY REGULATIONS.



- GENERAL NOTES:**
1. IT IS NOT ALLOWED TO REPRODUCE THE SHEETS CONTENTS IN ANY FORM EXCEPT FOR THE PURPOSE FOR WHICH IT IS INTENDED.
 2. THESE DRAWINGS ARE DIAGRAMMATIC AND SHALL NOT BE SCALED. ADDITIONAL DATA SHALL BE REQUESTED FROM THE CONSULTANCY THROUGH WRITTEN CLARIFICATION. VERIFY ALL EXISTING CONDITIONS AND DIMENSIONS BEFORE PROCEEDING WITH ANY PORTION OF ANY WORK.
 3. NO CHANGES, MODIFICATIONS OR DEVIATIONS SHALL BE WRITTEN PERMISSION FROM **ALMASAH ENGINEERING CONSULTANTS**.
 4. ALL WORK AS OUTLINED IN THESE DOCUMENTS, SHALL STRICTLY CONFORM TO ALL APPLICABLE CODES. IN THE EVENT OF A CONFLICT, THE MORE STRINGENT REQUIREMENT SHALL GOVERN AND BE MET.

SIA - SM-02



حُكُومَةُ الشَّارِقَةِ
دائرة الشؤون الإسلامية

CONSULTANT STAMP



CLIENT: **GOVERNMENT OF SHARJAH -
DEPARTMENT OF ISLAMIC AFFAIRS**

PROJECT: **(SIA - SM-02)
PROPOSED MASJID + ABLUTION +
IMAM HOUSE**

SHEET TITLE: **ELEVATION -C**

ARCHITECT Arch. Mostafa Ramadan	TYPE ARCHITECTURE
STRUCTURAL Eng : Mohamed Goma	SHEET No. A - 06
CHECKED BY Eng : Mohamed Attia	Location : Plot No :
SCALE 1:100	DATE March - 2022
Project No.	

GENERAL NOTES:



- 1.IT IS NOT ALLOWED TO REPRODUCE THE SHEETS CONTENTS IN ANY FORM EXCEPT FOR THE PURPOSE FOR WHICH IT IS INTENDED.
2. THESE DRAWINGS ARE DIAGRAMMATIC AND SHALL NOT BE SCALED. ADDITIONAL DATA SHALL BE REQUESTED FROM THE CONSULTANCY THROUGH WRITTEN CLARIFICATION. VERIFY ALL EXISTING CONDITIONS AND DIMENSIONS BEFORE PROCEEDING WITH ANY PORTION OF ANY WORK.
3. NO CHANGES, MODIFICATIONS OR DEVIATIONS SHALL BE WRITTEN PERMISSION FROM **ALMASAH ENGINEERING CONSULTANTS**.
4. ALL WORK AS OUTLINED IN THESE DOCUMENTS, SHALL STRICTLY CONFORM TO ALL APPLICABLE CODES. IN THE EVENT OF A CONFLICT, THE MORE STRINGENT REQUIREMENT SHALL GOVERN AND BE MET.

SIA - SM-02



حكومة الشارقة
دائرة الشؤون الإسلامية

CONSULTANT STAMP

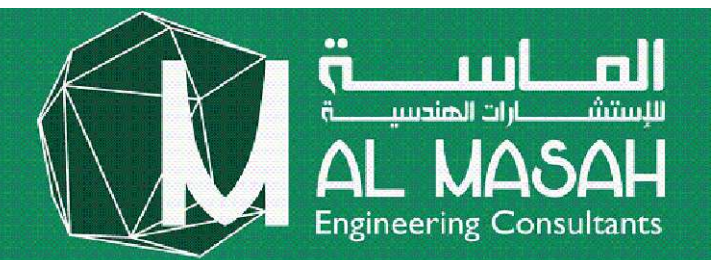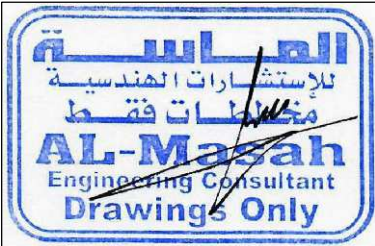

Sharjah ☎ 06 5 444 521 ☎ 06 5 444 523 📍 Office: 306, Al Faisal 2 Bldg., King Faisal St.

CLIENT:

GOVERNMENT OF SHARJAH -
DEPARTMENT OF ISLAMIC AFFAIRS

PROJECT:

(SIA - SM-02)
PROPOSED MASJID + ABLUTION +
IMAM HOUSE

SHEET TITLE:


ELEVATION -D

ARCHITECT Arch. Mostafa Ramadan	TYPE ARCHITECTURE
STRUCTURAL Eng : Mohamed Gomaa	SHEET No. A - 07
CHECKED BY Eng : Mohamed Attia	Location : Plot No :
SCALE 1:100	DATE March - 2022
	Project No.

ELEVATION FINISHES

- 1- REFLECTIVE GLASS
- 2- GRAFFIO DECOR WHITE PAINT OR STONE CLADDING
- 3- GRAFFIO DECOR OFF WHITE PAINT OR STONE CLADDING
- 4- GRANITE FINISHING
- 5- G.R.C.

ALL WINDOWS & BALCONY DOORS SHOULD BE EQUIPED WITH WINDOWS OPENING CONTROL DEVICE (W.O.C.D.) TO LIMITS THE OPENING LESS THAN 10 CM TO HAVE MAXIMUM OPENING LIMIT OF 10 CM TO HELP IN THE PREVENTION OF ACCIDENTAL FALLS FROM WINDOWS & BALCONIES BY CHILDREN AS PER SHARJAH MUNICIPALITY REGULATIONS.

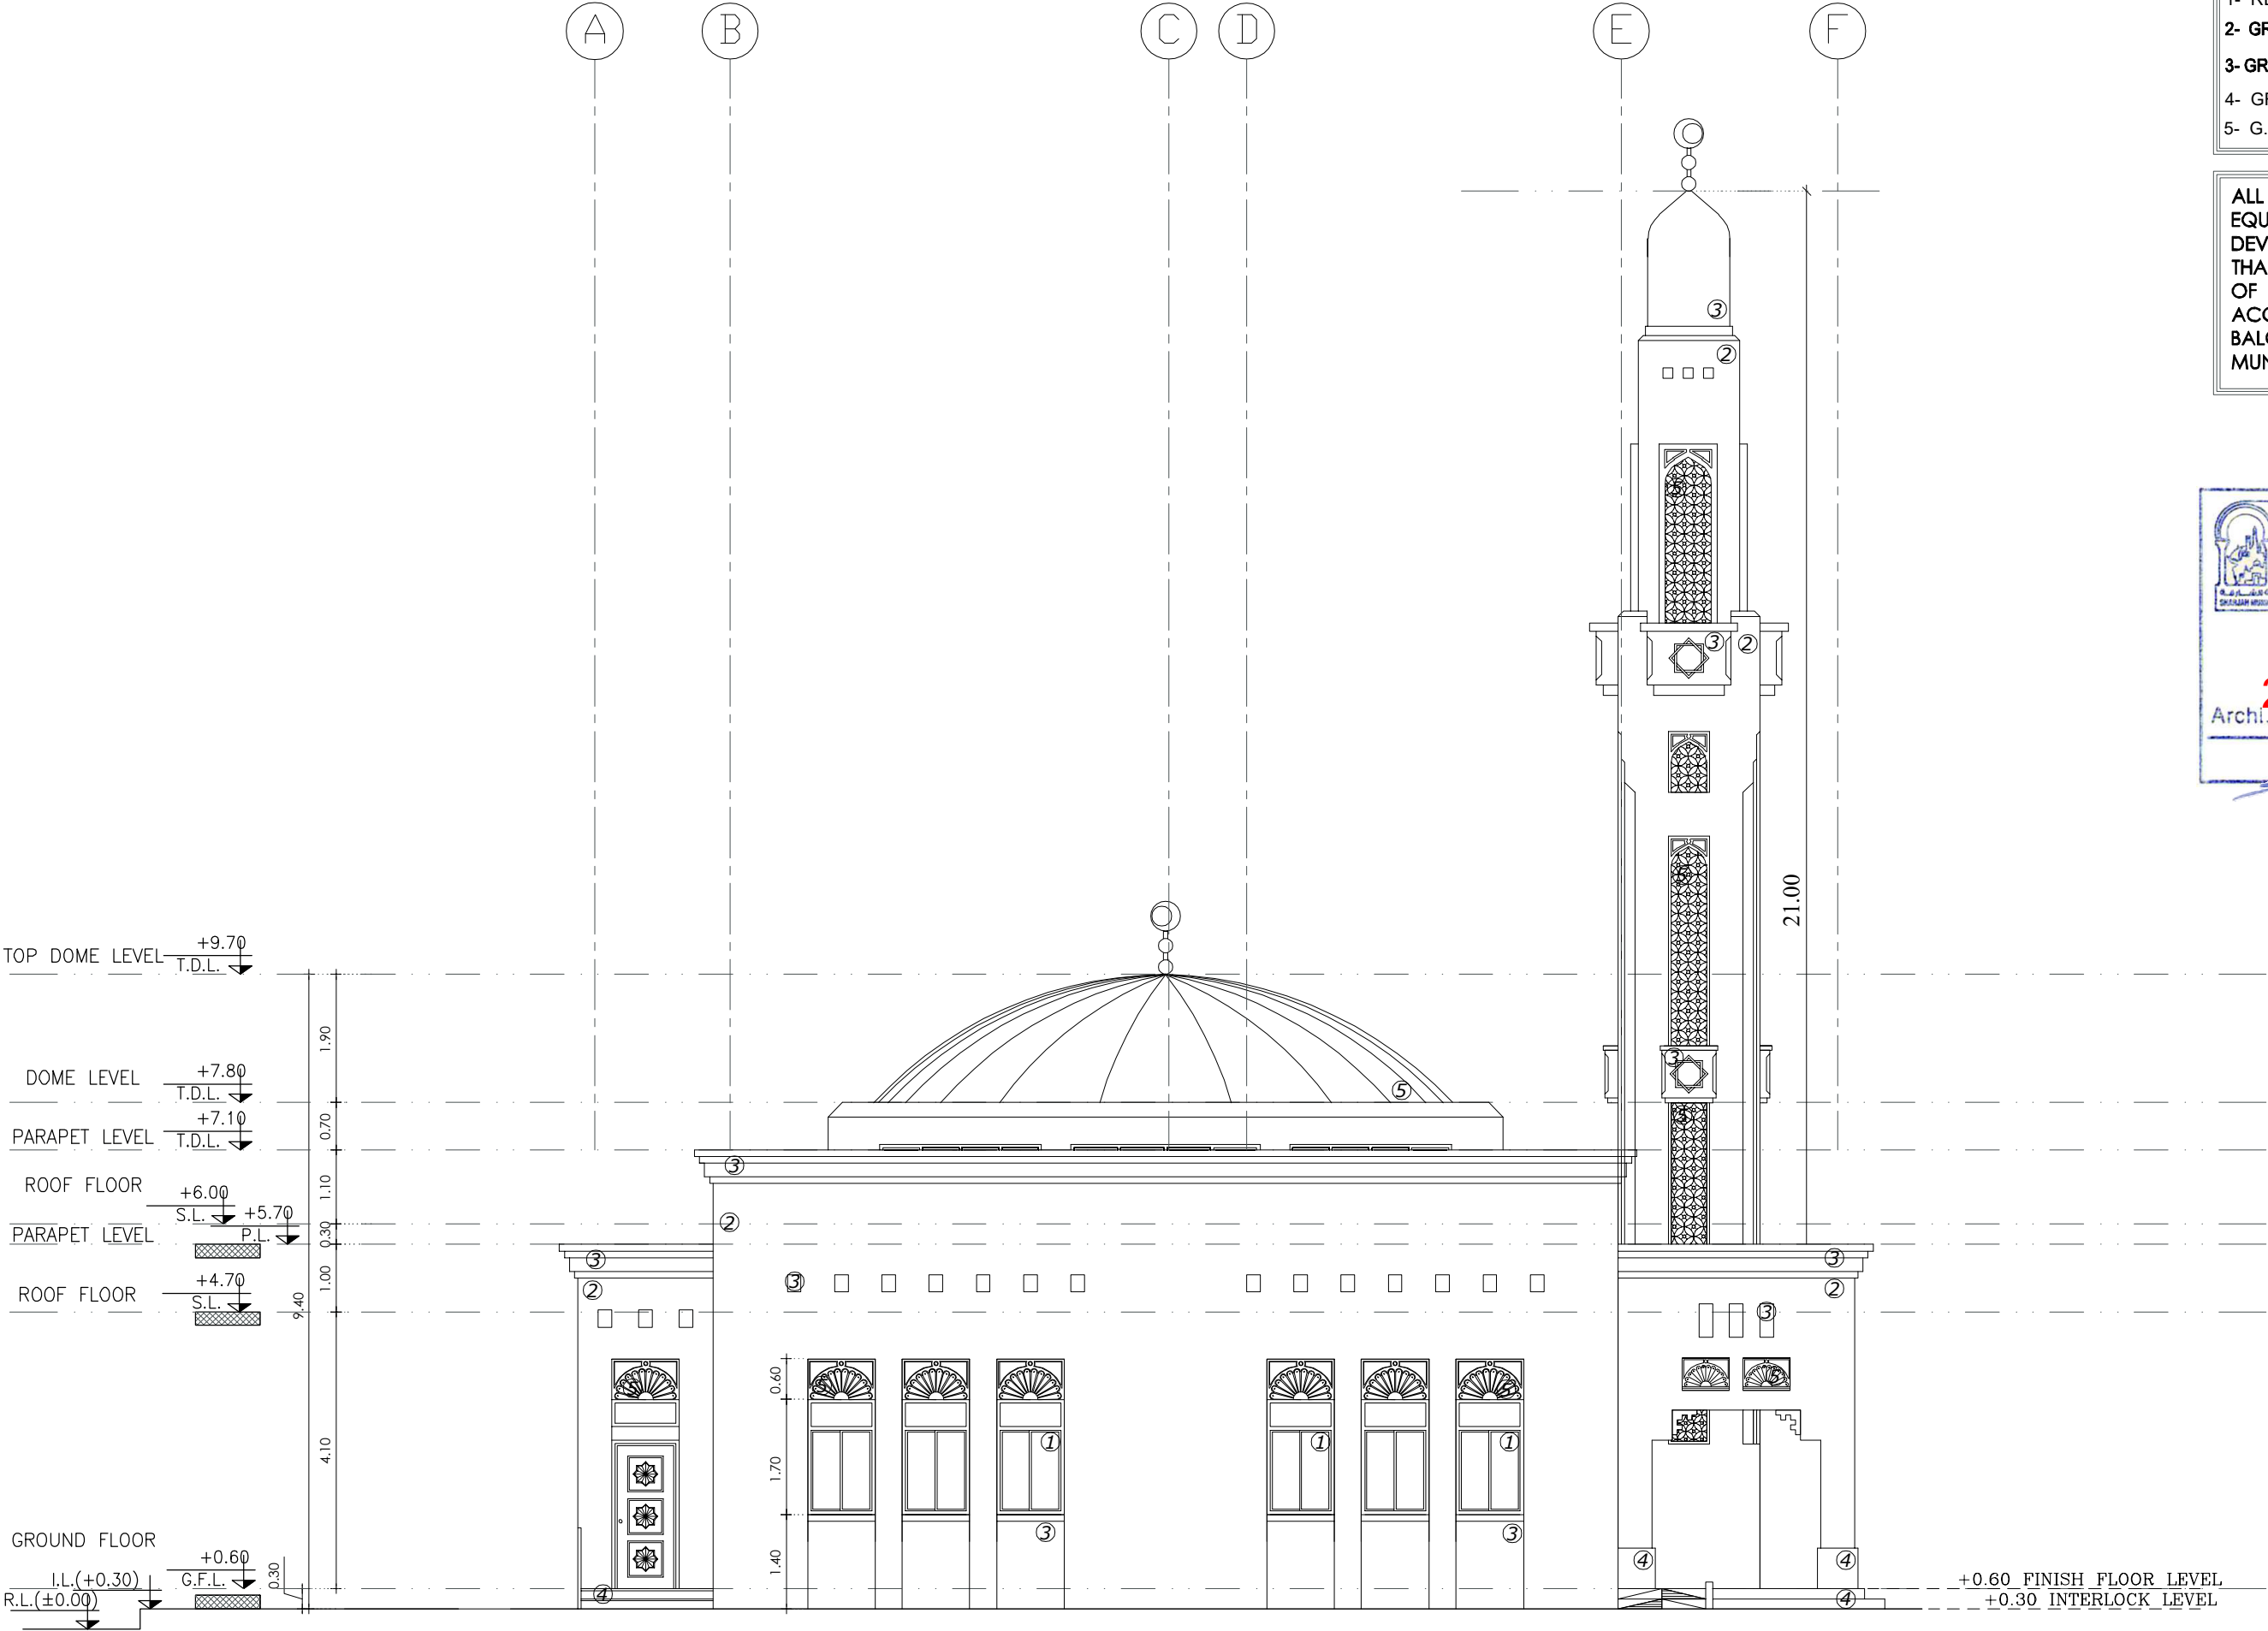

ELEVATION -D

- GENERAL NOTES:**
- IT IS NOT ALLOWED TO REPRODUCE THE SHEETS CONTENTS IN ANY FORM EXCEPT FOR THE PURPOSE FOR WHICH IT IS INTENDED.
 - THESE DRAWINGS ARE DIAGRAMMATIC AND SHALL NOT BE SCALED. ADDITIONAL DATA SHALL BE REQUESTED FROM THE CONSULTANCY THROUGH WRITTEN CLARIFICATION. VERIFY ALL EXISTING CONDITIONS AND DIMENSIONS BEFORE PROCEEDING WITH ANY PORTION OF ANY WORK.
 - NO CHANGES, MODIFICATIONS OR DEVIATIONS SHALL BE WRITTEN PERMISSION FROM **ALMASAH ENGINEERING CONSULTANTS**.
 - ALL WORK AS OUTLINED IN THESE DOCUMENTS, SHALL STRICTLY CONFORM TO ALL APPLICABLE CODES. IN THE EVENT OF A CONFLICT, THE MORE STRINGENT REQUIREMENT SHALL GOVERN AND BE MET.

SIA - SM-02



حكومة الشارقة
دائرة الشؤون الإسلامية

CONSULTANT STAMP



Sharjah ☎ 06 5 444 521 ☎ 06 5 444 523 ☎ Office: 306, Al Faisal 2 Bldg., King Faisal St.


CLIENT: **GOVERNMENT OF SHARJAH -
DEPARTMENT OF ISLAMIC AFFAIRS**

PROJECT: **(SIA - SM-02)
PROPOSED MASJID + ABLUTION +
IMAM HOUSE**

SHEET TITLE: **SECTION X-X**


ARCHITECT Arch. Mostafa Ramadan	TYPE ARCHITECTURE
STRUCTURAL Eng : Mohamed Gomaa	SHEET No. A - 08
CHECKED BY Eng : Mohamed Attia	Location : Plot No :
SCALE 1:100	DATE March - 2022
	Project No.

© ALL COPYRIGHTS IS RESERVED

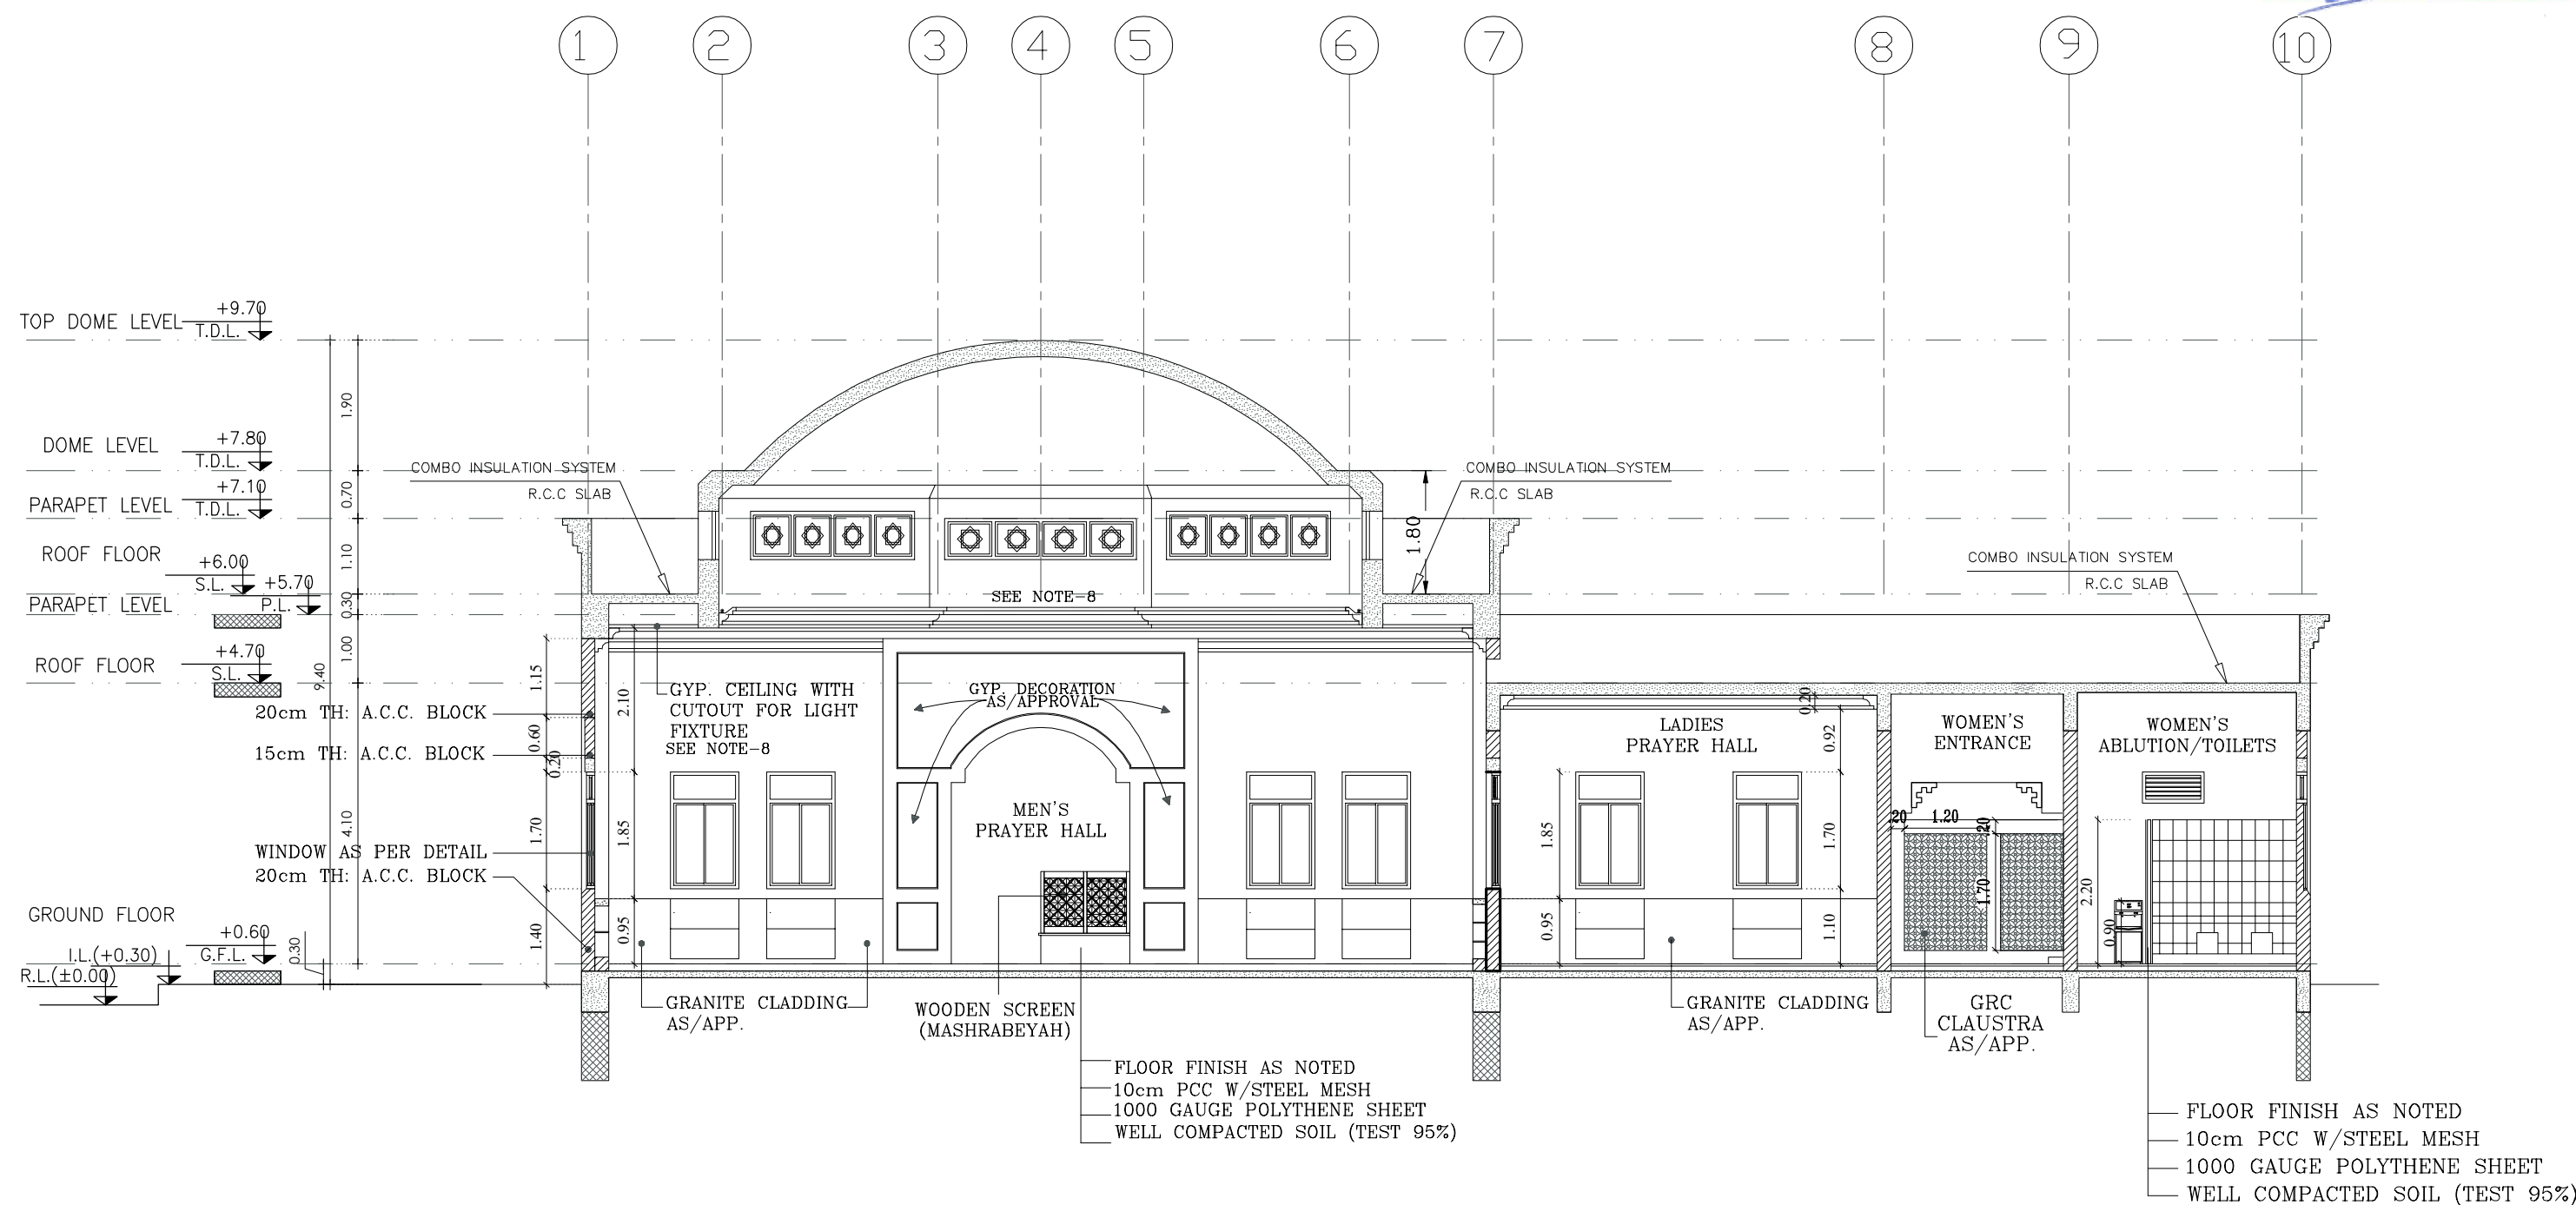


SECTION X-X

- * NOTES ::**
- ALL EXTERNAL WALLS TO BE 20.cm THERMAL BLOCK.
 - WINDOWS TO BE DOUBLE REFLECTIVE GLASS

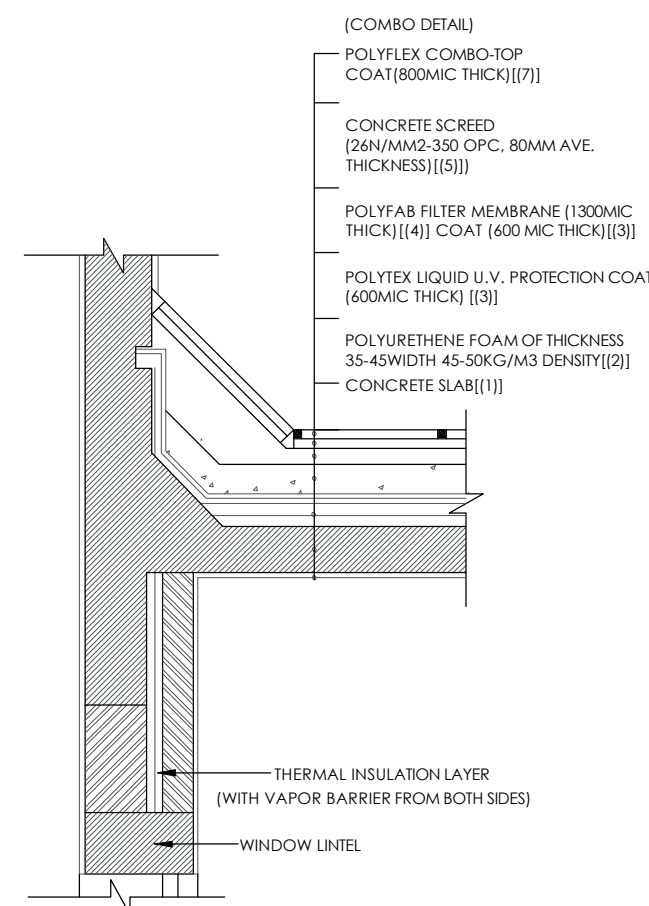

DETAIL 1
(SCALE = 1 : 25)

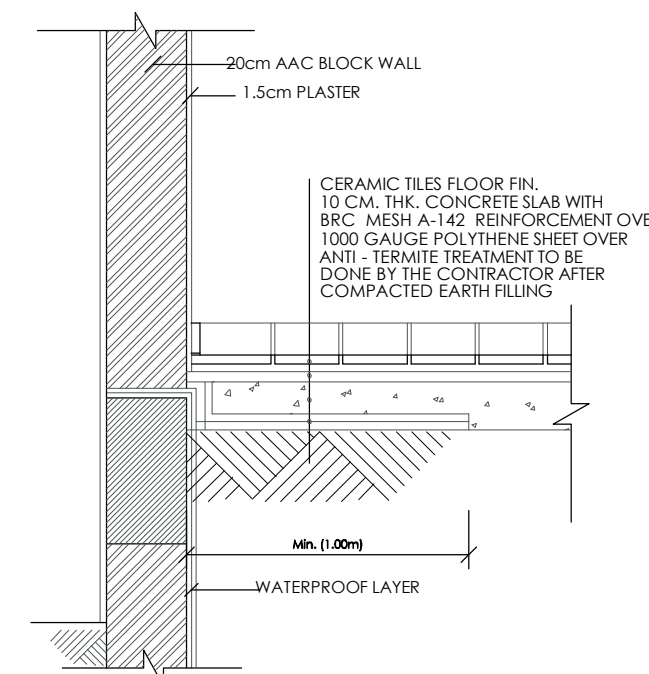

DETAIL 2
(SCALE = 1 : 25)



GENERAL NOTES:

1. IT IS NOT ALLOWED TO REPRODUCE THE SHEETS CONTENTS IN ANY FORM EXCEPT FOR THE PURPOSE FOR WHICH IT IS INTENDED.
2. THESE DRAWINGS ARE DIAGRAMMATIC AND SHALL NOT BE SCALED. ADDITIONAL DATA SHALL BE REQUESTED FROM THE CONSULTANCY THROUGH WRITTEN CLARIFICATION. VERIFY ALL EXISTING CONDITIONS AND DIMENSIONS BEFORE PROCEEDING WITH ANY PORTION OF ANY WORK.
3. NO CHANGES, MODIFICATIONS OR DEVIATIONS SHALL BE WRITTEN PERMISSION FROM **ALMASAH ENGINEERING CONSULTANTS**.
4. ALL WORK AS OUTLINED IN THESE DOCUMENTS, SHALL STRICTLY CONFORM TO ALL APPLICABLE CODES. IN THE EVENT OF A CONFLICT, THE MORE STRINGENT REQUIREMENT SHALL GOVERN AND BE MET.

SIA - SM-02



حُكُومَةُ الشَّارِقَة
دائرة الشؤون الإسلامية

CONSULTANT STAMP



Sharjah ☎ 06 5 444 521 ☎ 06 5 444 523 ☎ Office: 306, Al Faisal 2 Bldg., King Faisal St.

CLIENT:

GOVERNMENT OF SHARJAH -
DEPARTMENT OF ISLAMIC AFFAIRS

PROJECT:


(SIA - SM-02)
PROPOSED MASJID + ABLUTION +
IMAM HOUSE

SHEET TITLE:


SECTION Y-Y

ARCHITECT Arch. Mostafa Ramadan	TYPE	ARCHITECTURE
STRUCTURAL Eng : Mohamed Gomaa	SHEET No.	A - 09
CHECKED BY Eng : Mohamed Attia	Location :	
SCALE 1:100	DATE March - 2022	Project No.

© ALL COPYRIGHTS IS RESERVED

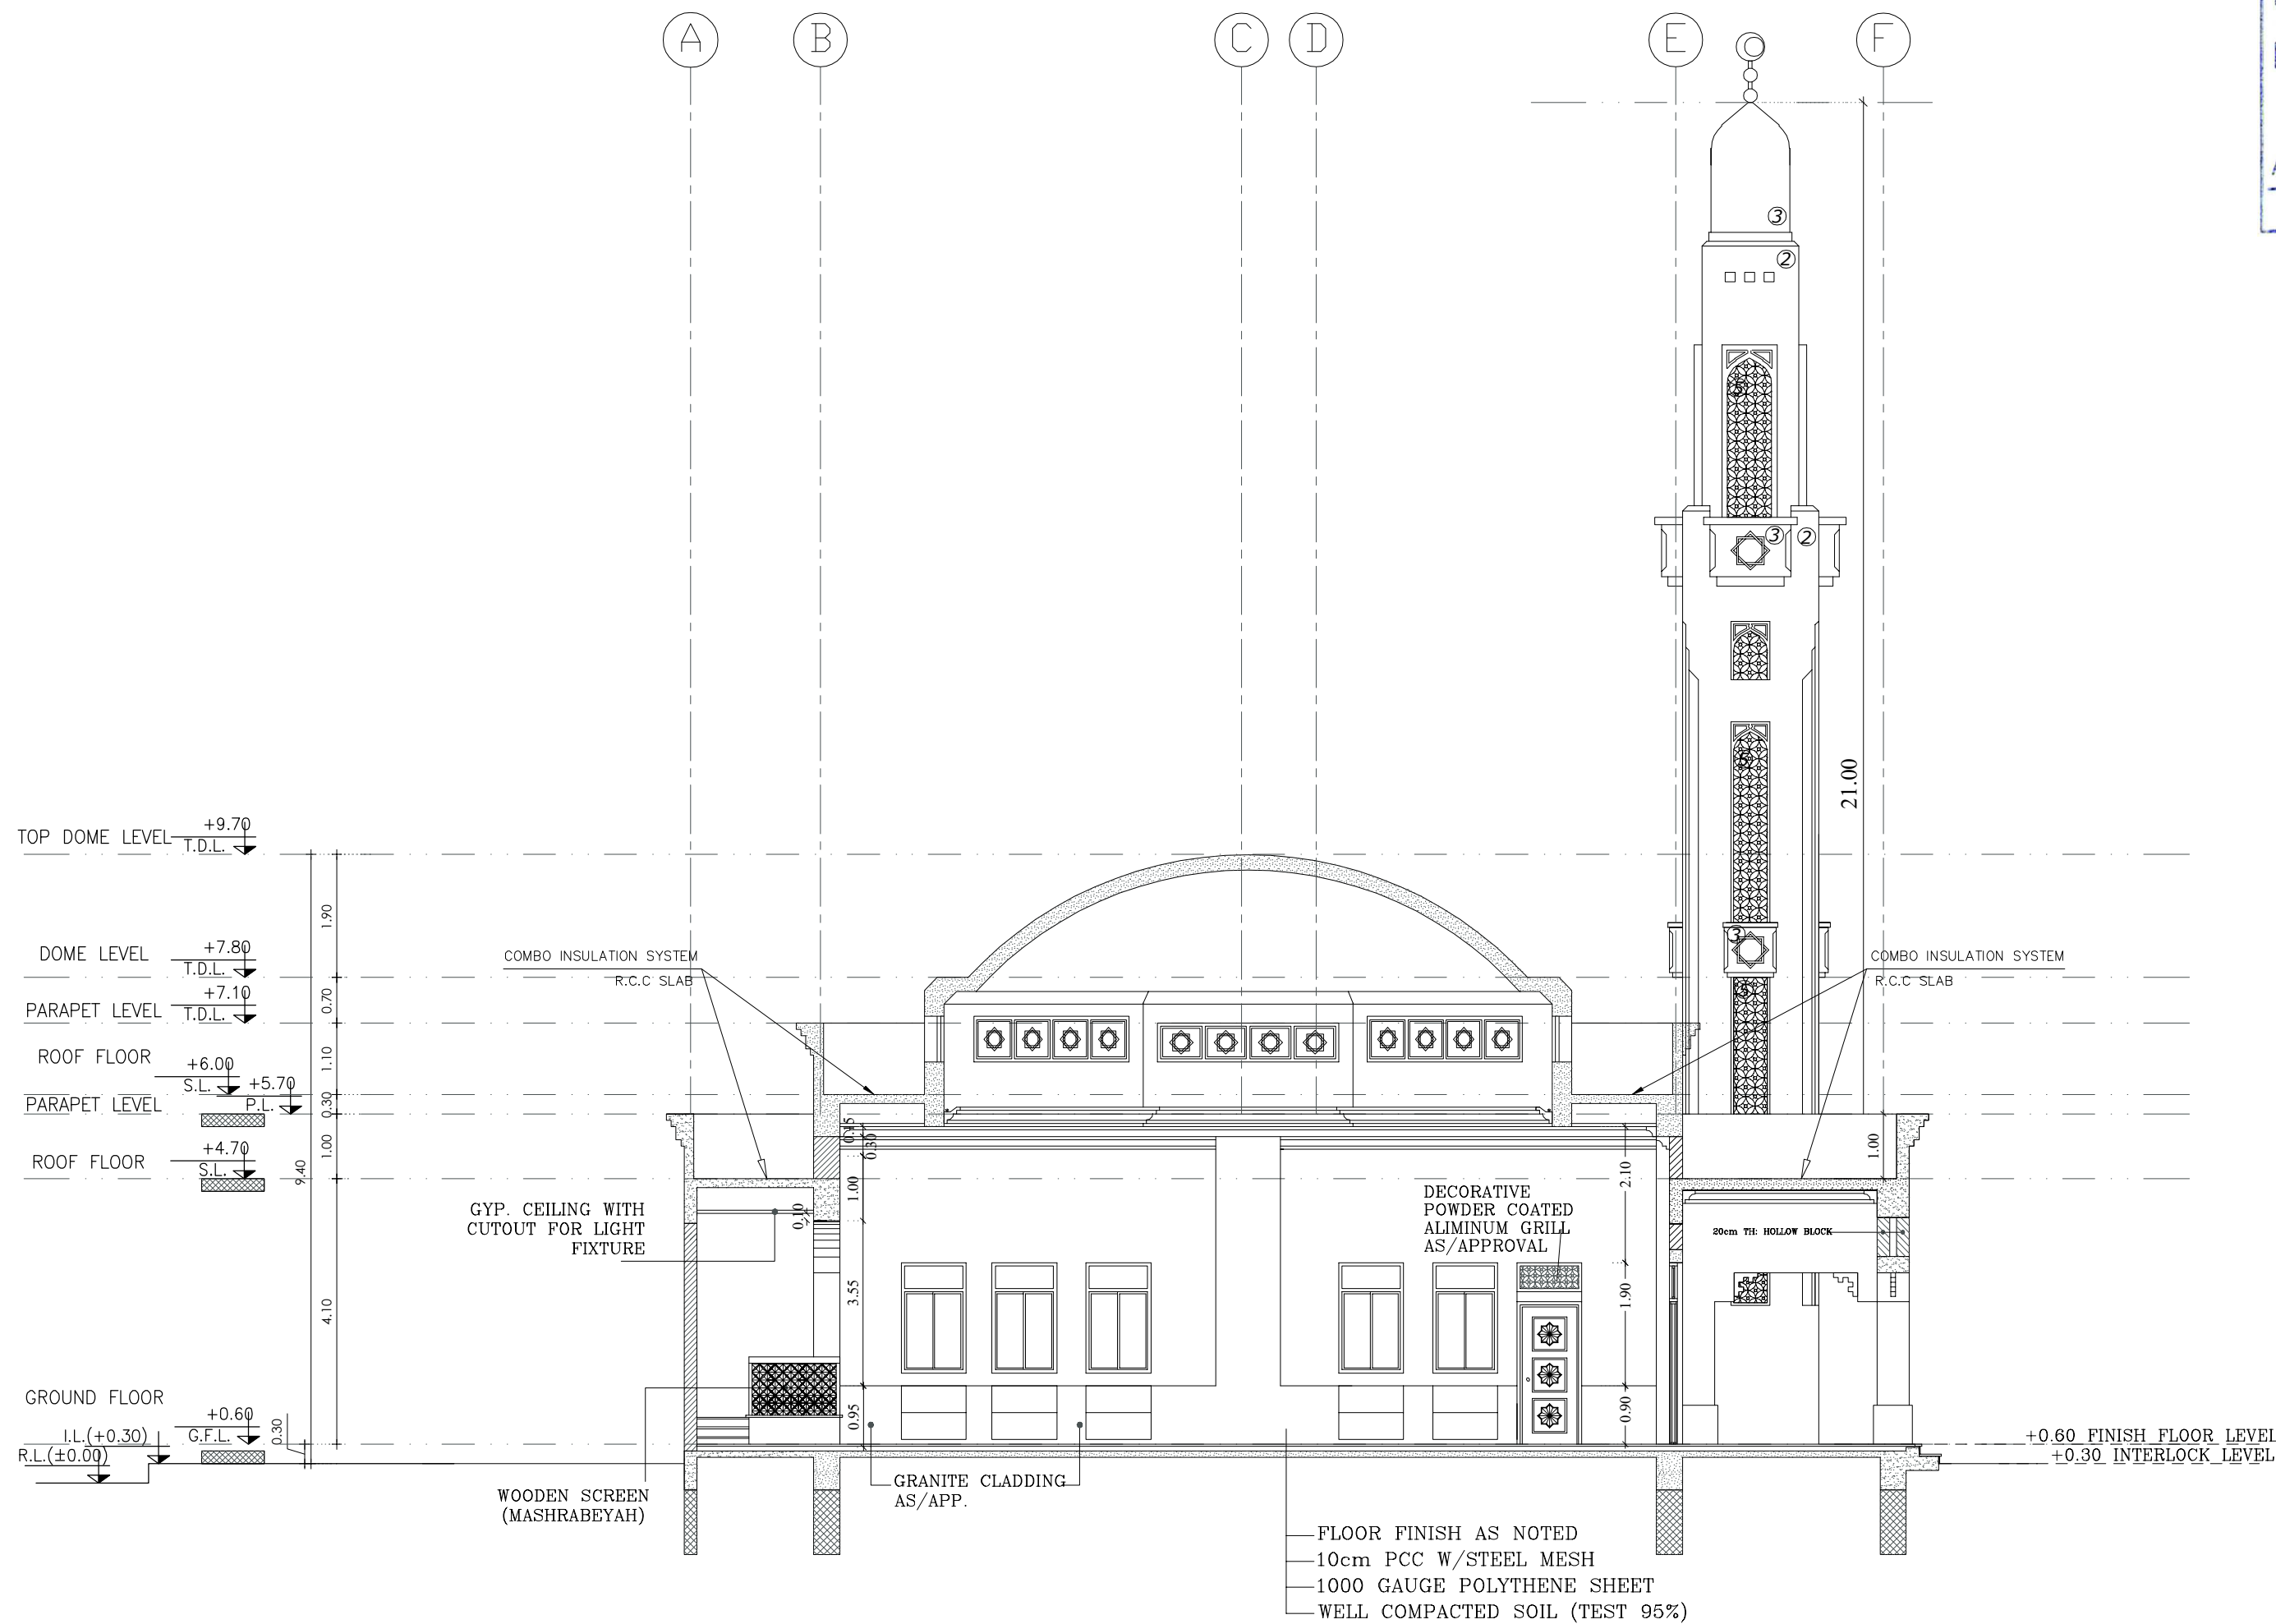


SECTION Y-Y

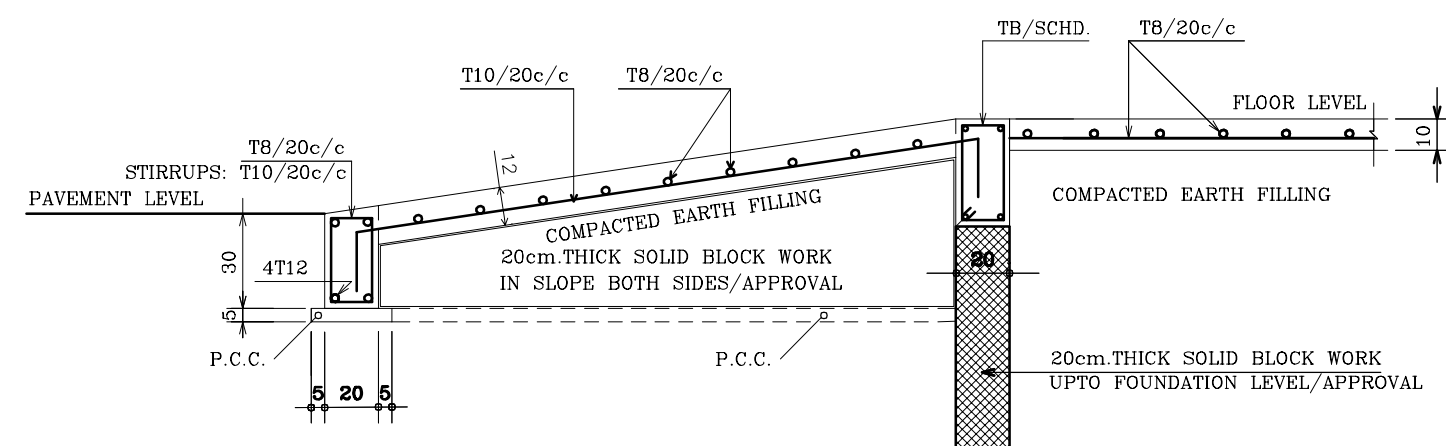


RAMP DETAIL

* NOTES ::


- 1- ALL EXTERNAL WALLS TO BE 20.cm THERMAL BLOCK.
- 2- WINDOWS TO BE DOUBLE REFLECTIVE GLASS

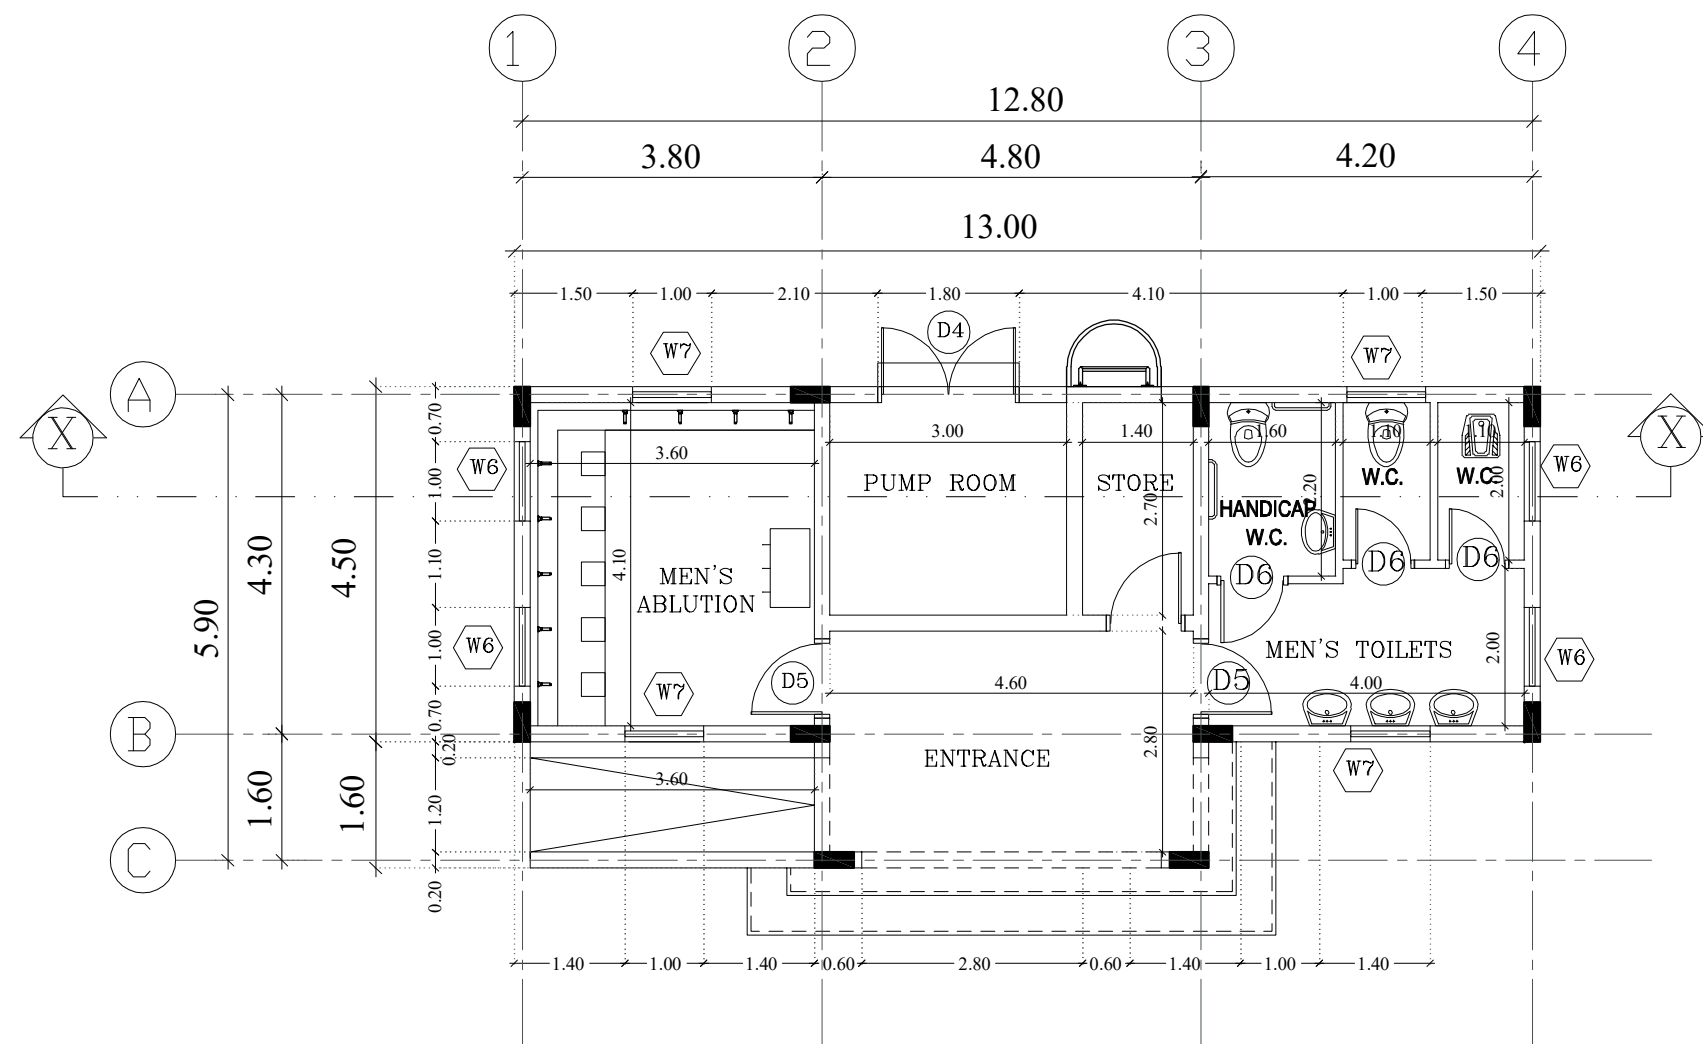

GROUND FLOOR PLAN
(SCALE = 1 : 100)

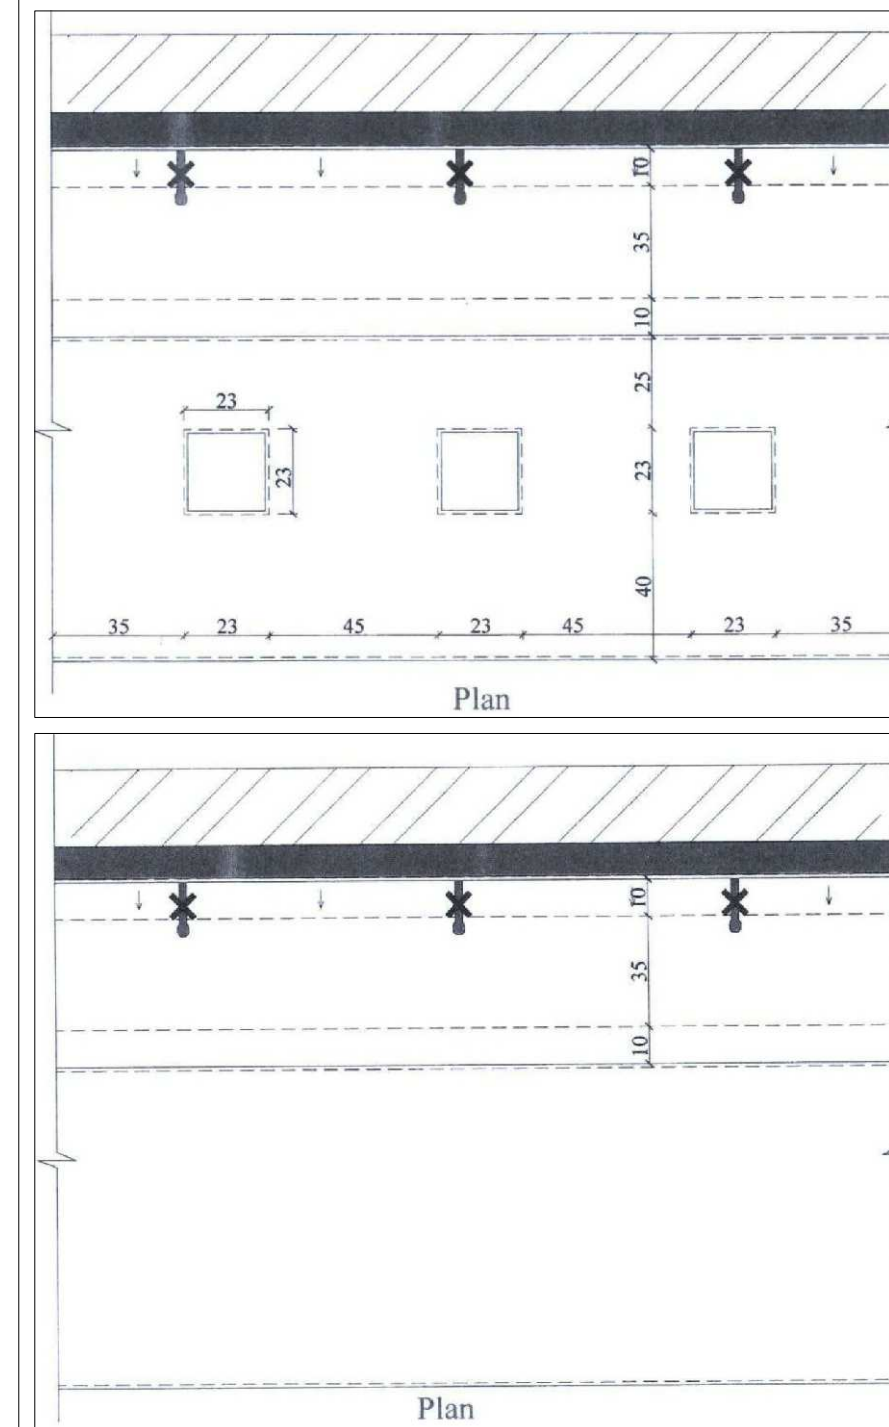

ABLUTION DETAILS

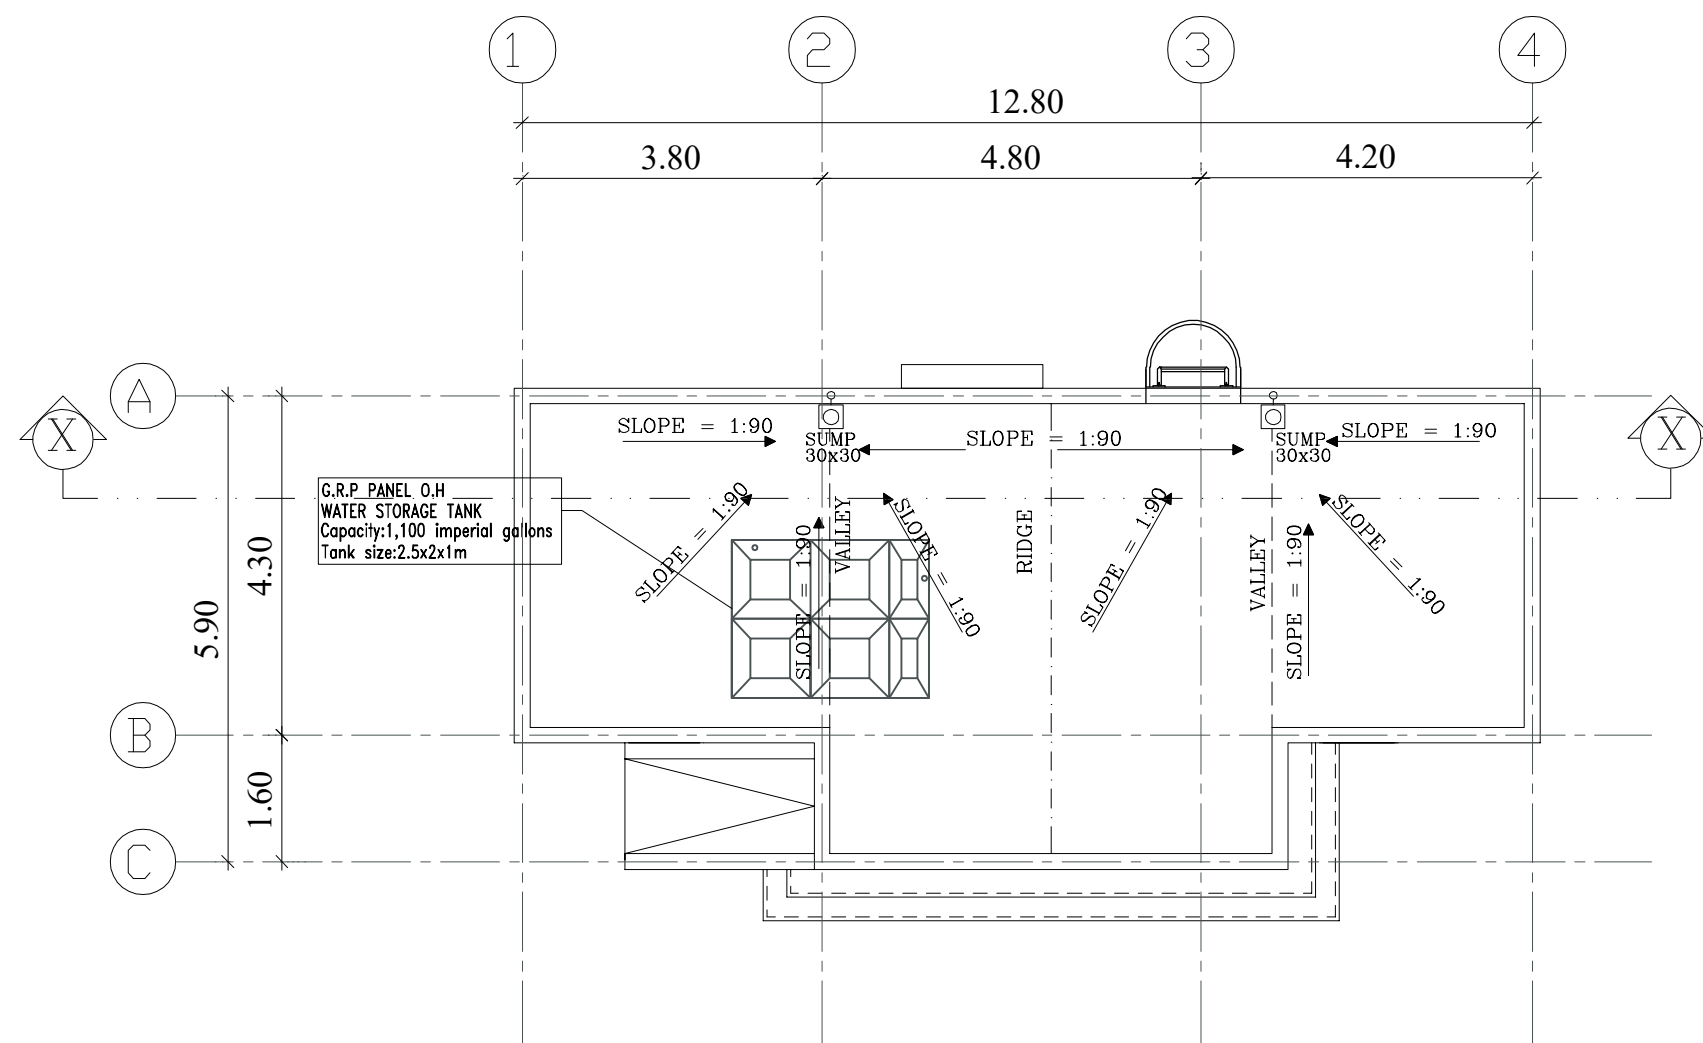

ROOF FLOOR PLAN
(SCALE = 1 : 100)

GENERAL NOTES:

1. IT IS NOT ALLOWED TO REPRODUCE THE SHEETS CONTENTS IN ANY FORM EXCEPT FOR THE PURPOSE FOR WHICH IT IS INTENDED.
2. THESE DRAWINGS ARE DIAGRAMMATIC AND SHALL NOT BE SCALED. ADDITIONAL DATA SHALL BE REQUESTED FROM THE CONSULTANCY THROUGH WRITTEN CLARIFICATION. VERIFY ALL EXISTING CONDITIONS AND DIMENSIONS BEFORE PROCEEDING WITH ANY PORTION OF ANY WORK.
3. NO CHANGES, MODIFICATIONS OR DEVIATIONS SHALL BE WRITTEN PERMISSION FROM **ALMASAH ENGINEERING CONSULTANTS**.
4. ALL WORK AS OUTLINED IN THESE DOCUMENTS, SHALL STRICTLY CONFORM TO ALL APPLICABLE CODES. IN THE EVENT OF A CONFLICT, THE MORE STRINGENT REQUIREMENT SHALL GOVERN AND BE MET.



SIA - SM-02



حُكُومَةُ الشَّارِقَةِ
دائرة الشؤون الإسلامية

CONSULTANT STAMP



CLIENT: **GOVERNMENT OF SHARJAH - DEPARTMENT OF ISLAMIC AFFAIRS**

PROJECT: **(SIA - SM-02) PROPOSED MASJID + ABLUTION + IMAM HOUSE**



SHEET TITLE: **ABLUTION GROUND & ROOF FLOOR PLAN**

ARCHITECT: Arch. Mostafa Ramadan TYPE: ARCHITECTURE

STRUCTURAL: Eng : Mohamed Gomaa SHEET No.: A - 10

CHECKED BY: Eng : Mohamed Attia Location : Plot No :

SCALE: 1:100 DATE: March - 2022 Project No.:

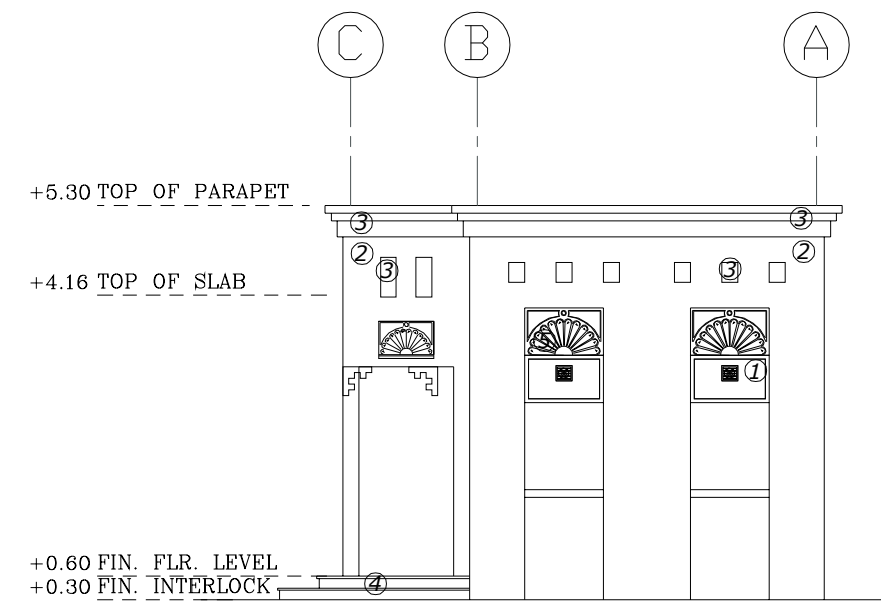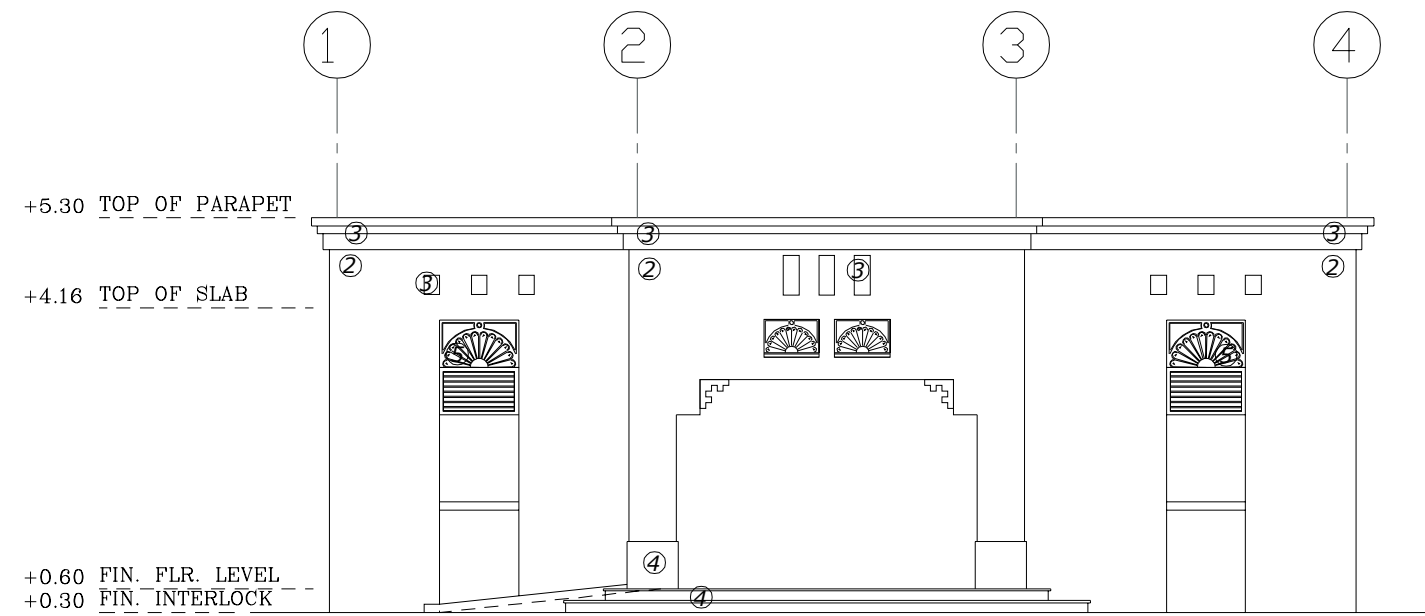

ALL WINDOWS & BALCONY DOORS SHOULD BE EQUIPPED WITH WINDOWS OPENING CONTROL DEVICE (W.O.C.D.) TO LIMITS THE OPENING LESS THAN 10 CM TO HAVE MAXIMUM OPENING LIMIT OF 10 CM TO HELP IN THE PREVENTION OF ACCIDENTAL FALLS FROM WINDOWS & BALCONIES BY CHILDREN AS PER SHARJAH MUNICIPALITY REGULATIONS.



ELEVATION FINISHES

- 1- REFLECTIVE GLASS
- 2- GRAFFIO DECOR WHITE PAINT OR STONE CLADDING
- 3- GRAFFIO DECOR OFF PAINT OR STONE CLADDING
- 4- GRANITE FINISHING
- 5- G.R.C.



GENERAL NOTES:


1. IT IS NOT ALLOWED TO REPRODUCE THE SHEETS CONTENTS IN ANY FORM EXCEPT FOR THE PURPOSE FOR WHICH IT IS INTENDED.
2. THESE DRAWINGS ARE DIAGRAMMATIC AND SHALL NOT BE SCALED. ADDITIONAL DATA SHALL BE REQUESTED FROM THE CONSULTANCY THROUGH WRITTEN CLARIFICATION. VERIFY ALL EXISTING CONDITIONS AND DIMENSIONS BEFORE PROCEEDING WITH ANY PORTION OF ANY WORK.
3. NO CHANGES, MODIFICATIONS OR DEVIATIONS SHALL BE WRITTEN PERMISSION FROM **ALMASAH ENGINEERING CONSULTANTS**.
4. ALL WORK AS OUTLINED IN THESE DOCUMENTS, SHALL STRICTLY CONFORM TO ALL APPLICABLE CODES. IN THE EVENT OF A CONFLICT, THE MORE STRINGENT REQUIREMENT SHALL GOVERN AND BE MET.

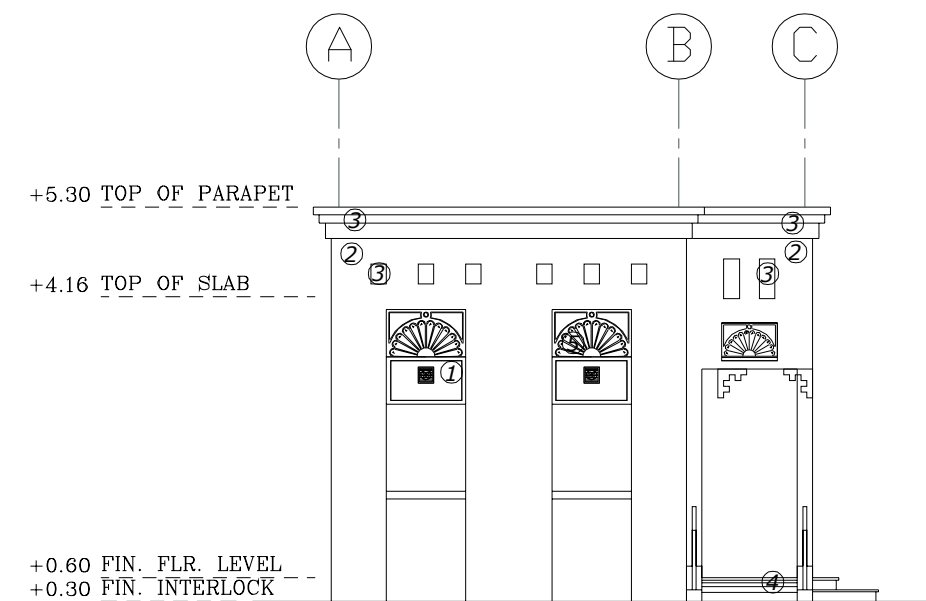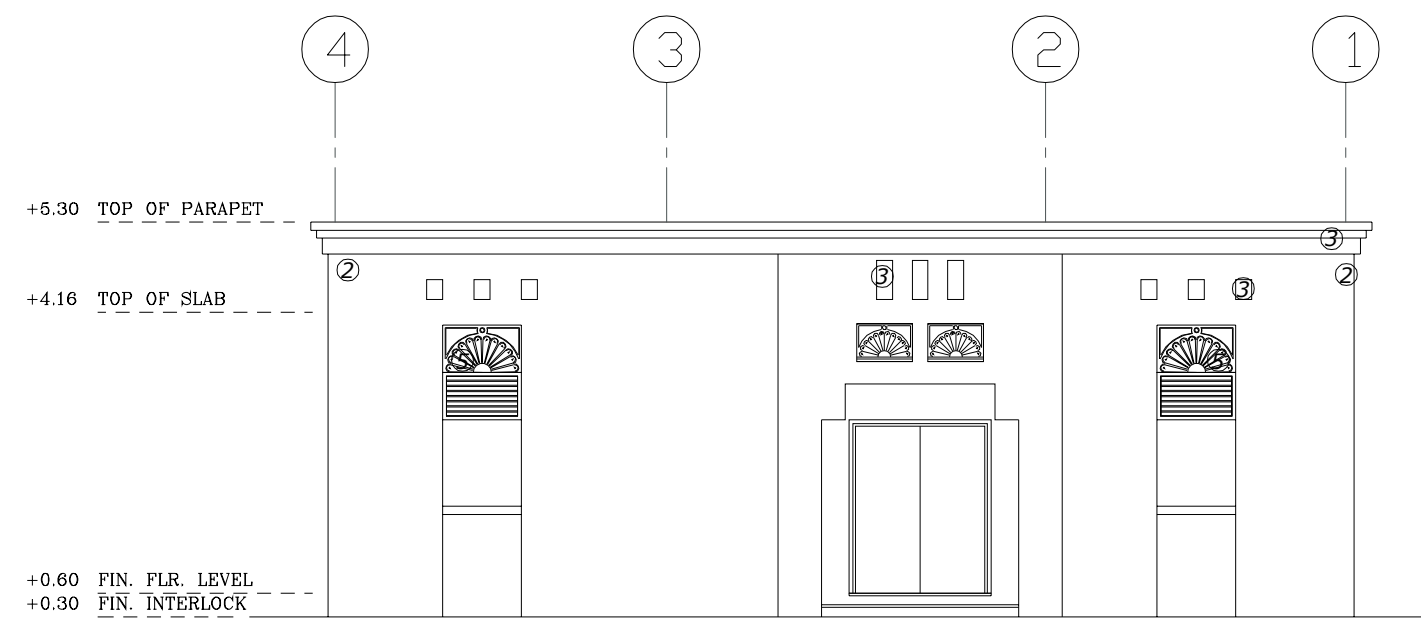

SIA - SM-02





CONSULTANT STAMP

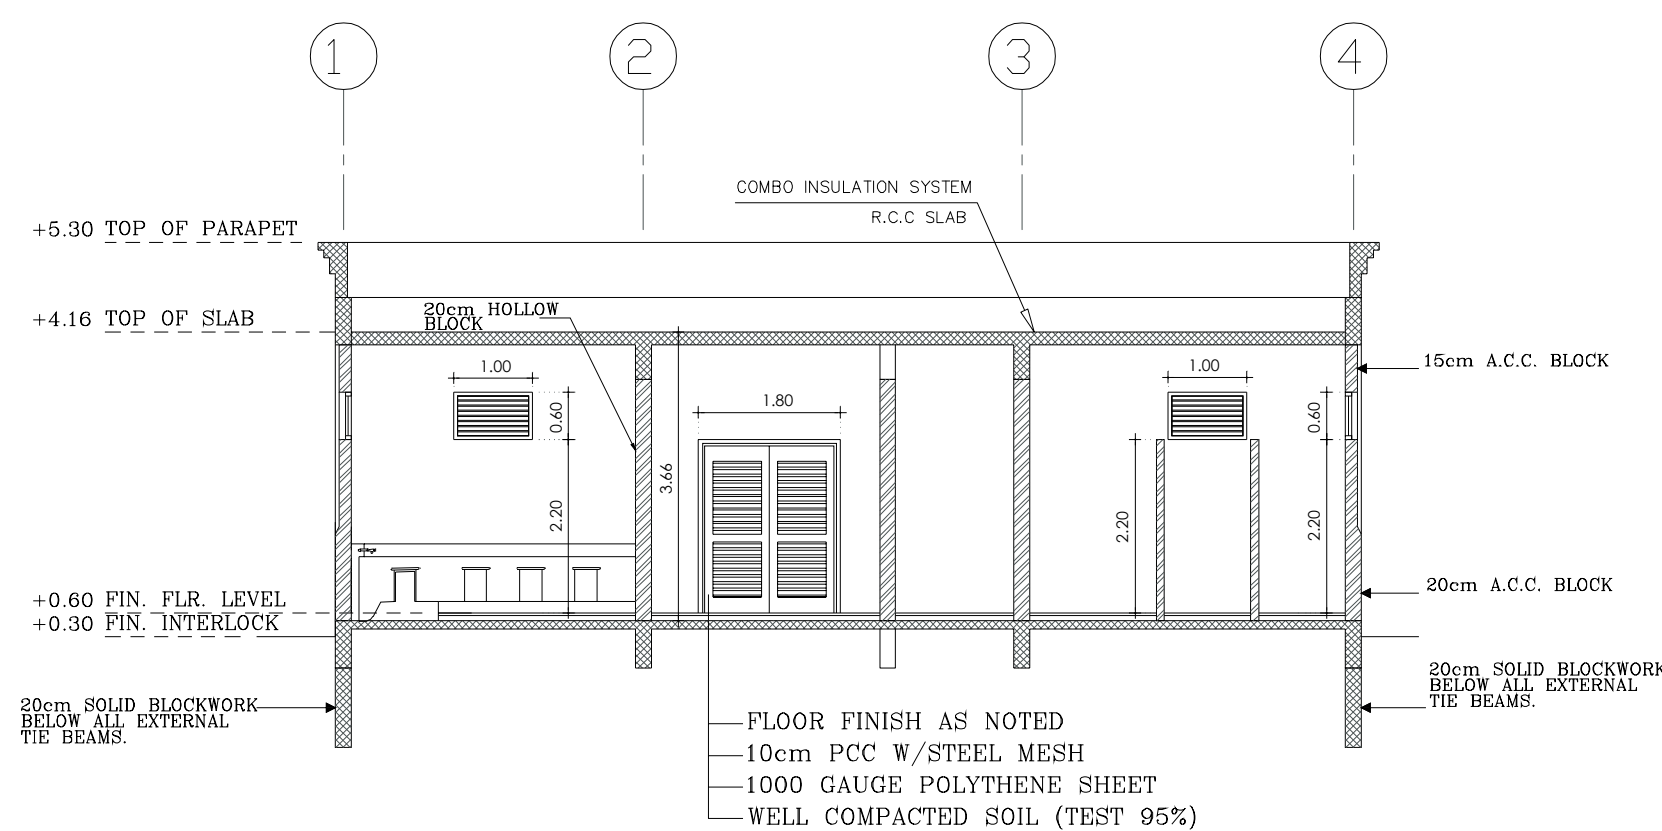

* NOTES :.

- 1- ALL EXTERNAL WALLS TO BE 20.cm THERMAL BLOCK.
2- WINDOWS TO BE DOUBLE REFLECTIVE GLASS

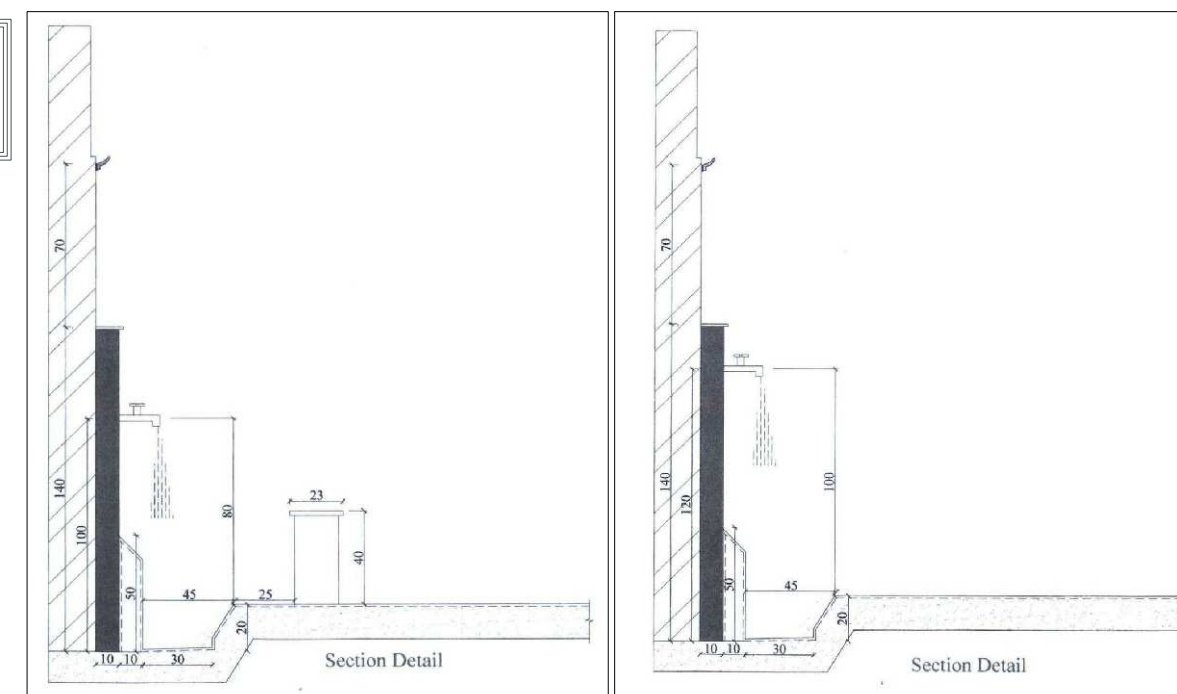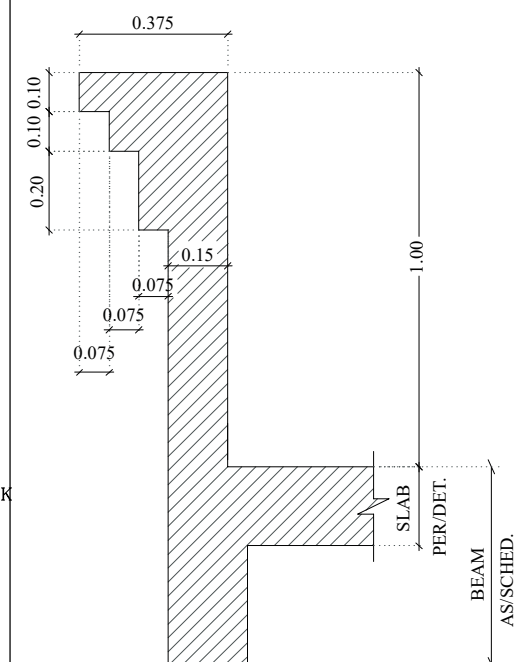

 **الماسية**
للإستشارات الهندسية
AL MASAH
Engineering Consultants

Sharjah ☎ 06 5 444 521 ☎ 06 5 444 523 ☎ Office: 306, Al Faisal 2 Bldg., King Faisal St.

CLIENT:

GOVERNMENT OF SHARJAH -
DEPARTMENT OF ISLAMIC AFFAIRS

PROJECT:

CT: (SIA - SM-02)
PROPOSED MASJID + ABLUTION +
IMAM HOUSE

SHEET TITLE:

ABLUTION
ELEVATIONS & SECTION

ARCHITECT

Arch. Mostafa Ramadan

TYPE

ARCHITECTURE

STRUCTURAL

Eng : Mohamed Gomaa

SHEET

No.

T	A - 11
---	--------

CHECKED BY

Eng : Mohamed Attia

Location :

Plot No :	
-----------	--

SCALE

1:100

DATE

March - 2022

	Project
--	---------

Project No.	
-------------	--



- GENERAL NOTES:**
1. IT IS NOT ALLOWED TO REPRODUCE THE SHEETS CONTENTS IN ANY FORM EXCEPT FOR THE PURPOSE FOR WHICH IT IS INTENDED.
 2. THESE DRAWINGS ARE DIAGRAMMATIC AND SHALL NOT BE SCALED. ADDITIONAL DATA SHALL BE REQUESTED FROM THE CONSULTANCY THROUGH WRITTEN CLARIFICATION. VERIFY ALL EXISTING CONDITIONS AND DIMENSIONS BEFORE PROCEEDING WITH ANY PORTION OF ANY WORK.
 3. NO CHANGES, MODIFICATIONS OR DEVIATIONS SHALL BE WRITTEN PERMISSION FROM **ALMASAH ENGINEERING CONSULTANTS**.
 4. ALL WORK AS OUTLINED IN THESE DOCUMENTS, SHALL STRICTLY CONFORM TO ALL APPLICABLE CODES. IN THE EVENT OF A CONFLICT, THE MORE STRINGENT REQUIREMENT SHALL GOVERN AND BE MET.

SIA - SM-02



حكومة الشارقة
دائرة الشؤون الإسلامية

CONSULTANT STAMP



Sharjah ☎ 06 5 444 521 ☎ 06 5 444 523 ☎ Office: 306, Al Fisal 2 Bldg., King Fisal St.


CLIENT: **GOVERNMENT OF SHARJAH - DEPARTMENT OF ISLAMIC AFFAIRS**

PROJECT: **(SIA - SM-02) PROPOSED MASJID + ABLUTION + IMAM HOUSE**


SHEET TITLE: **IMAM HOUSE GROUND & ROOF FLOOR PLAN**

ARCHITECT Arch. Mostafa Ramadan	TYPE ARCHITECTURE
STRUCTURAL Eng : Mohamed Gomaa	SHEET No. A - 12
CHECKED BY Eng : Mohamed Attia	Location : Plot No :
SCALE 1:100	DATE March - 2022
Project No.	

© ALL COPYRIGHTS IS RESERVED

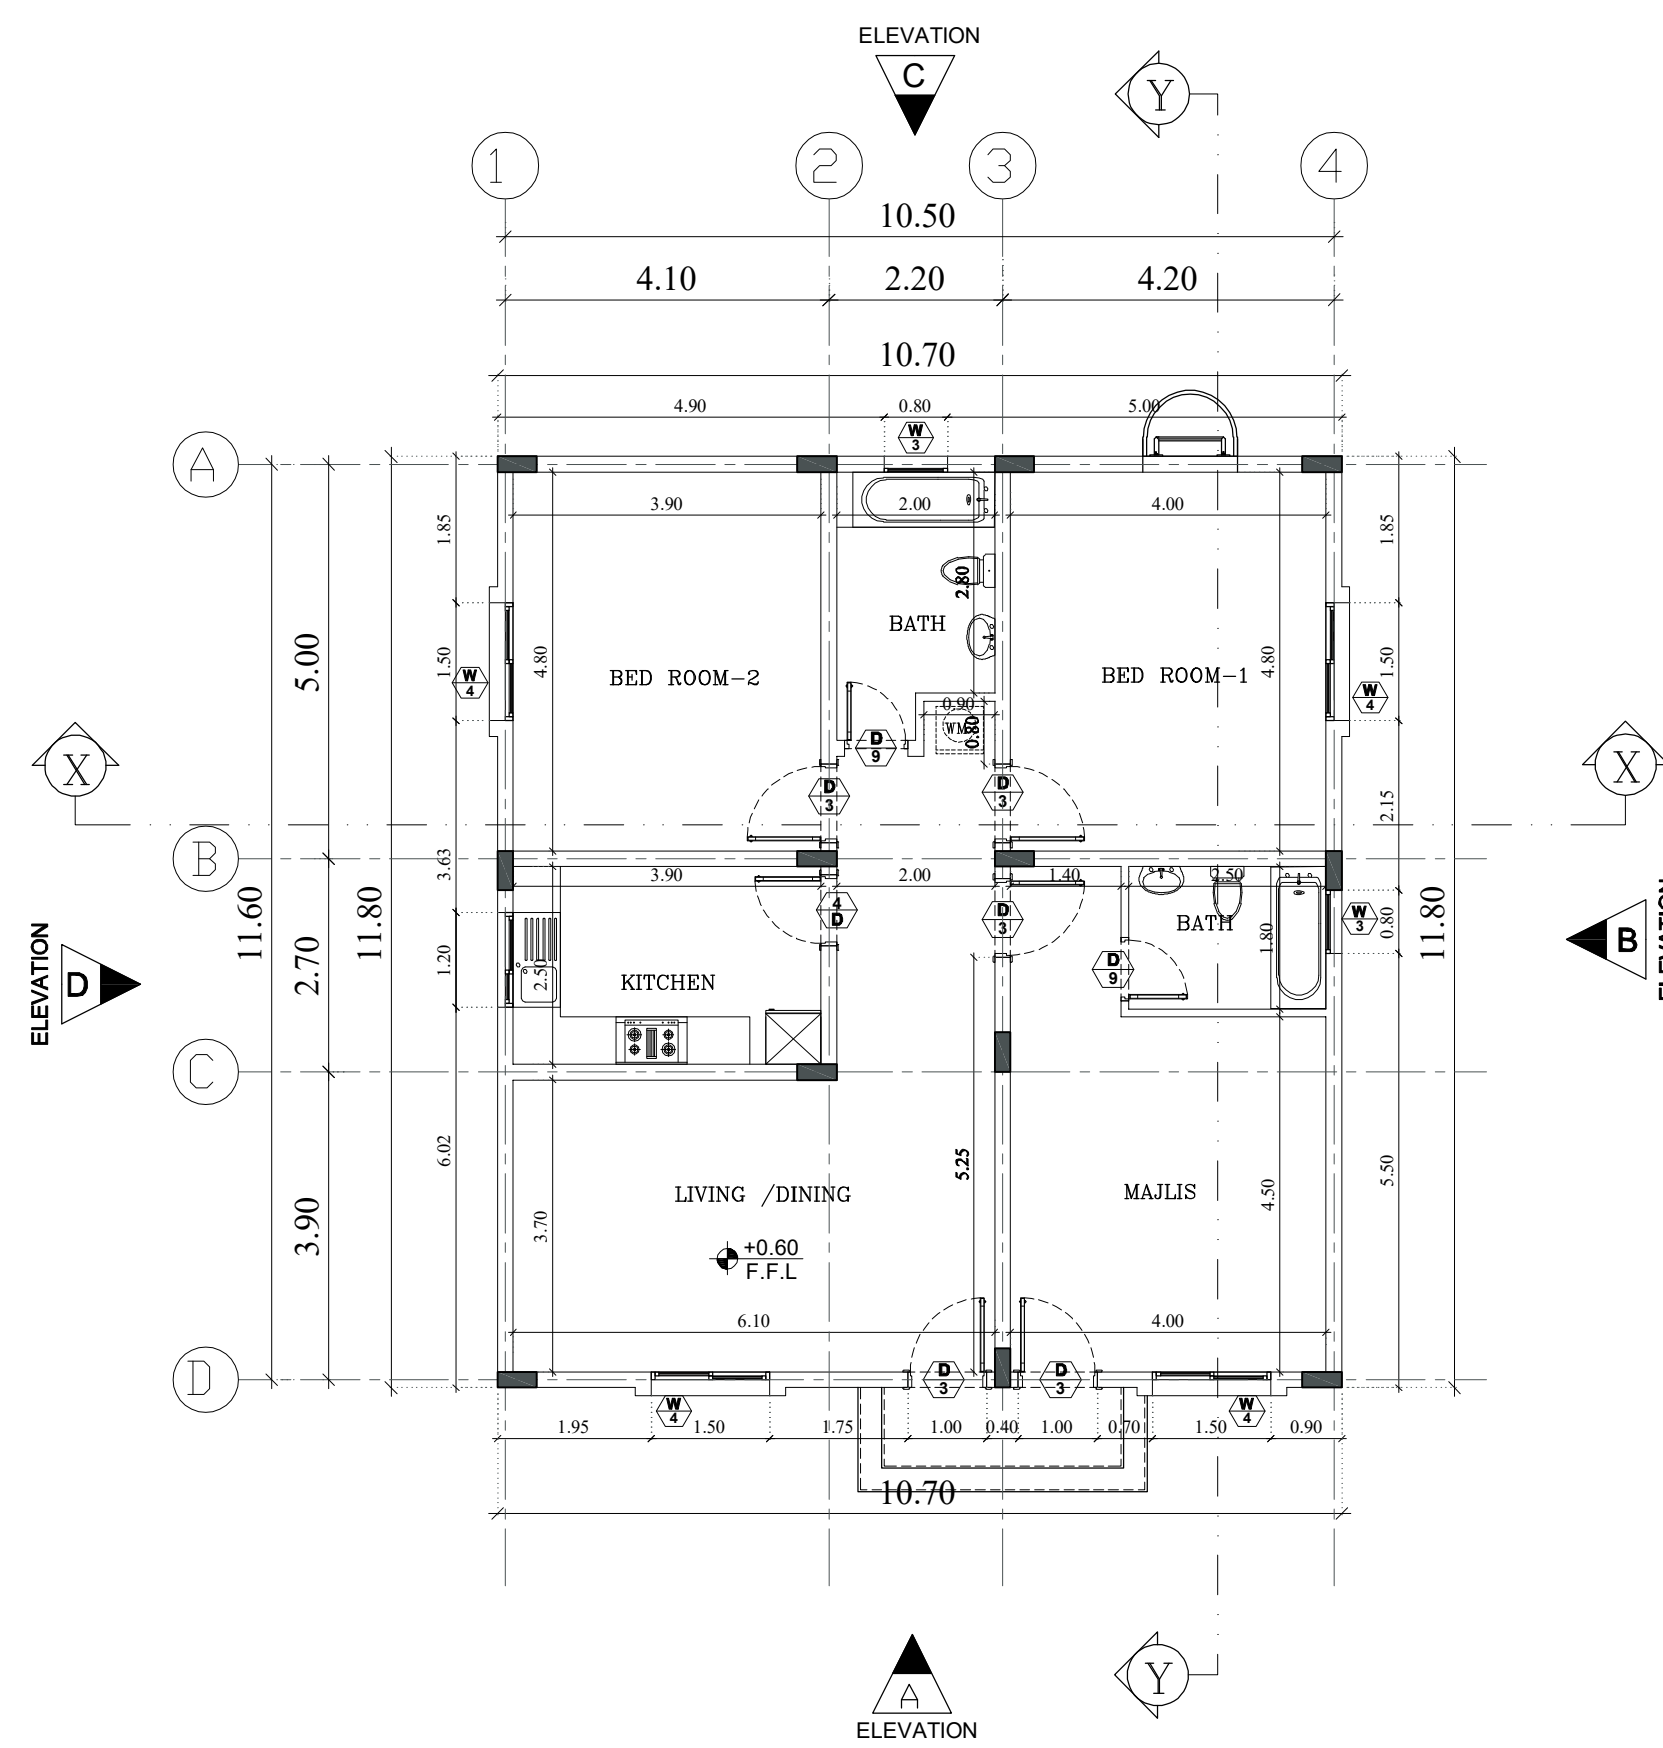


GROUND FLOOR PLAN
(SCALE = 1 : 100)

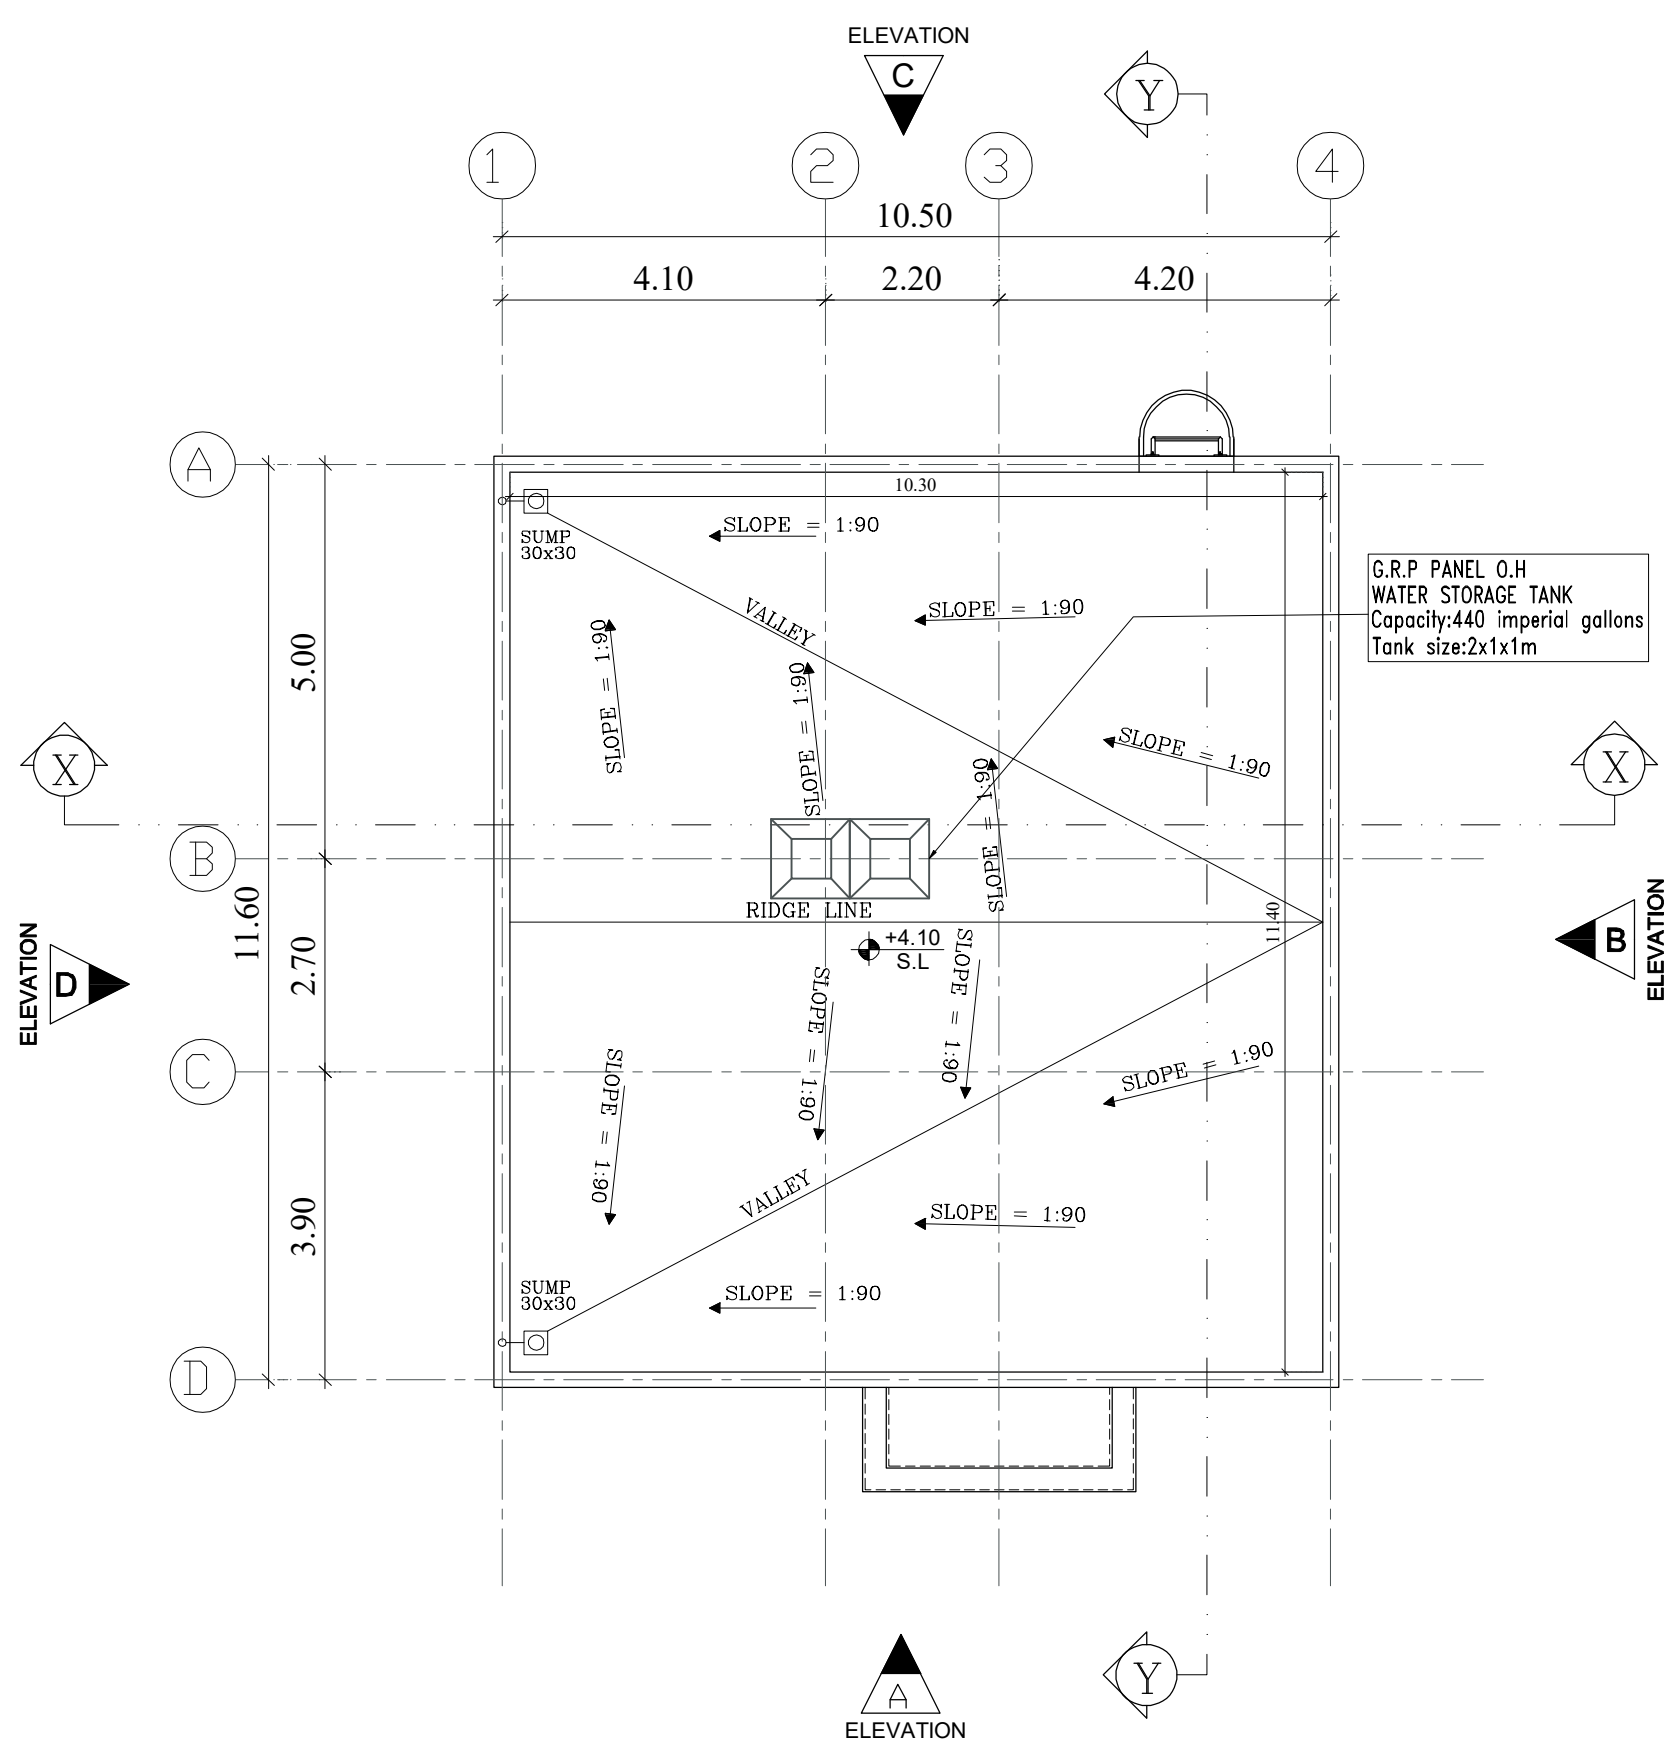

ROOF FLOOR PLAN
(SCALE = 1 : 100)



ELEVATION -A
(SCALE = 1 : 100)

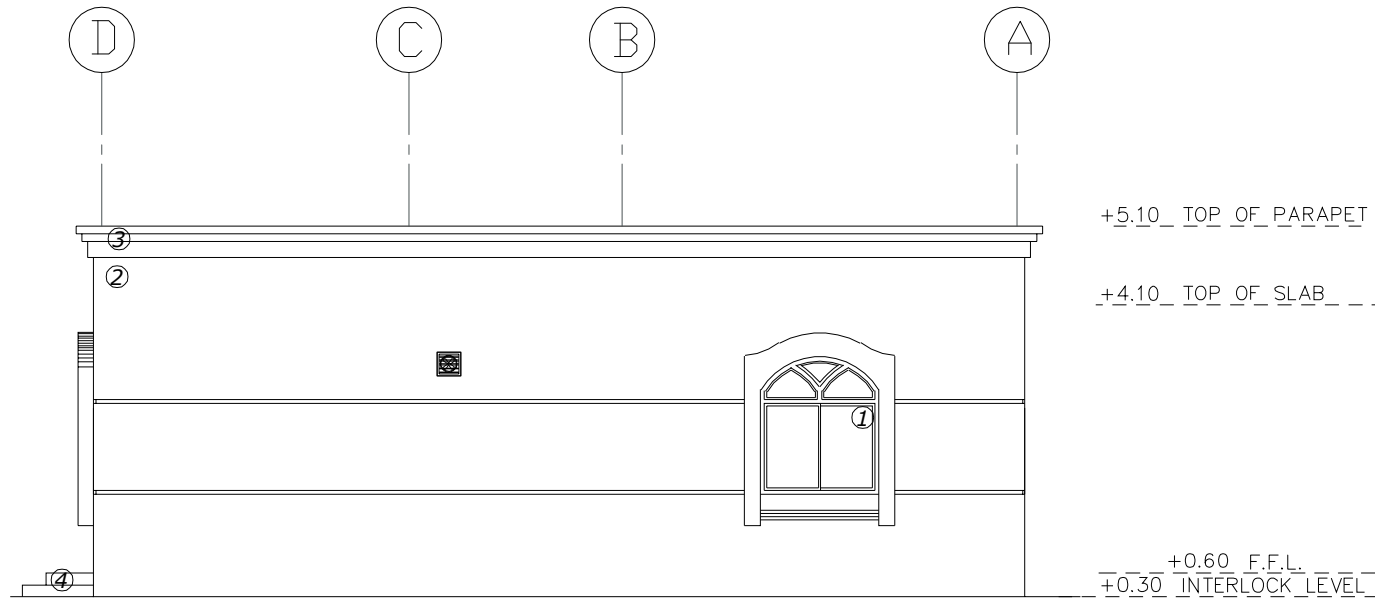

ELEVATION -B
(SCALE = 1 : 100)

- ELEVATION FINISHES**
- 1- REFLECTIVE GLASS
 - 2- GRAFFIO DECOR WHITE PAINT OR STONE CLADDING
 - 3- GRAFFIO DECOR OFF PAINT OR STONE CLADDING
 - 4- GRANITE FINISHING
 - 5- G.R.C.

ALL WINDOWS & BALCONY DOORS SHOULD BE EQUIPED WITH WINDOWS OPENING CONTROL DEVICE (W.O.C.D.) TO LIMITS THE OPENING LESS THAN 10 CM TO HAVE MAXIMUM OPENING LIMIT OF 10 CM TO HELP IN THE PREVENTION OF ACCIDENTAL FALLS FROM WINDOWS & BALCONIES BY CHILDREN AS PER SHARJAH MUNICIPALITY REGULATIONS.

- GENERAL NOTES:**
- 1.IT IS NOT ALLOWED TO REPRODUCE THE SHEETS CONTENTS IN ANY FORM EXCEPT FOR THE PURPOSE FOR WHICH IT IS INTENDED.
 2. THESE DRAWINGS ARE DIAGRAMMATIC AND SHALL NOT BE SCALED. ADDITIONAL DATA SHALL BE REQUESTED FROM THE CONSULTANCY THROUGH WRITTEN CLARIFICATION. VERIFY ALL EXISTING CONDITIONS AND DIMENSIONS BEFORE PROCEEDING WITH ANY PORTION OF ANY WORK.
 3. NO CHANGES, MODIFICATIONS OR DEVIATIONS SHALL BE WRITTEN PERMISSION FROM **ALMASAH ENGINEERING CONSULTANTS**.
 4. ALL WORK AS OUTLINED IN THESE DOCUMENTS, SHALL STRICTLY CONFORM TO ALL APPLICABLE CODES. IN THE EVENT OF A CONFLICT, THE MORE STRINGENT REQUIREMENT SHALL GOVERN AND BE MET.





SIA - SM-02




حكومة الشارقة
دائرة الشؤون الإسلامية

CONSULTANT STAMP

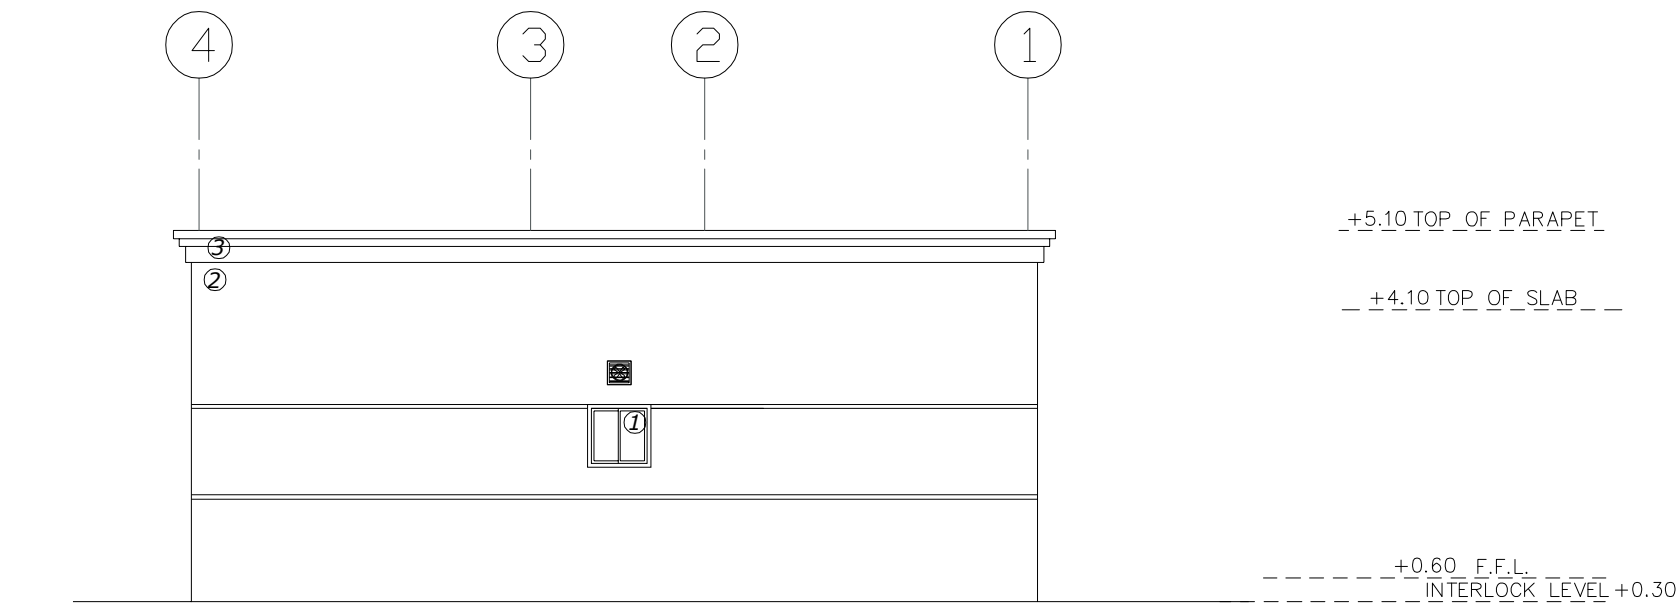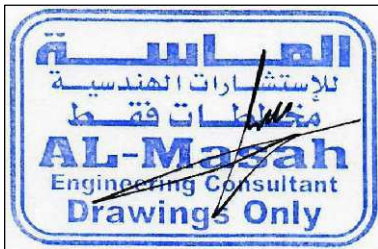


ELEVATION -C
(SCALE = 1 : 100)

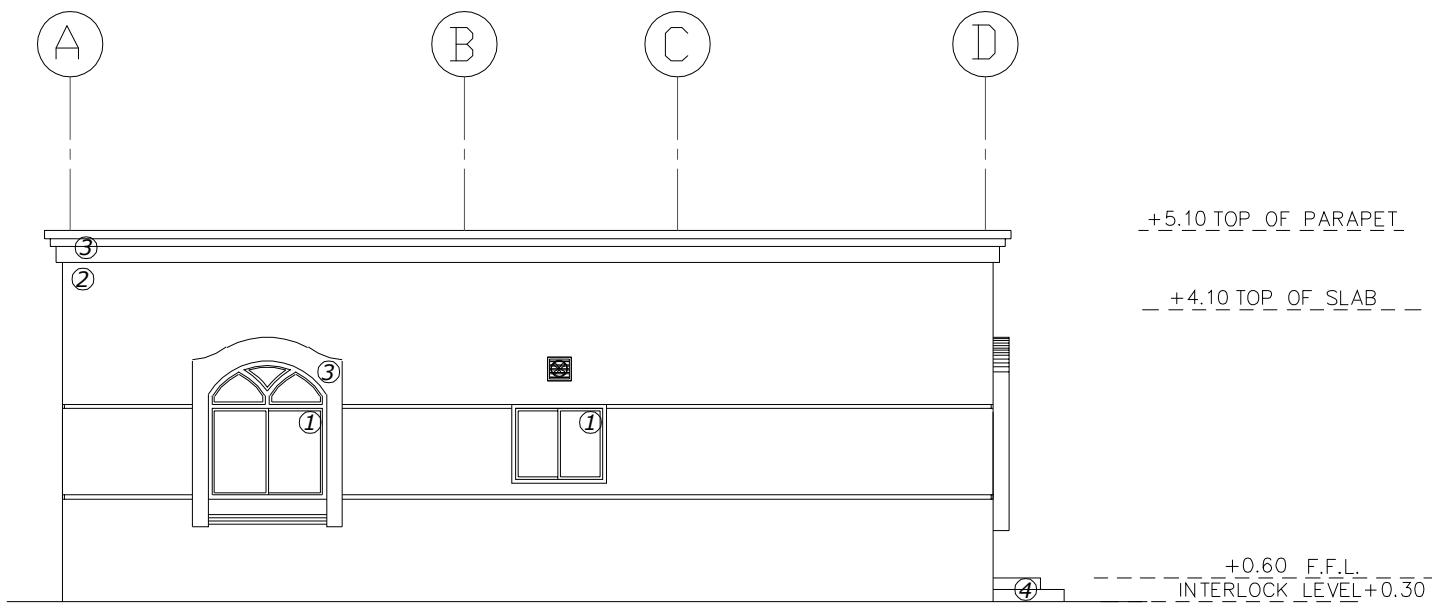


ELEVATION -D
(SCALE = 1 : 100)

*** NOTES .:**


- 1- ALL EXTERNAL WALLS TO BE 20.cm THERMAL BLOCK.
- 2- WINDOWS TO BE DOUBLE REFLECTIVE GLASS

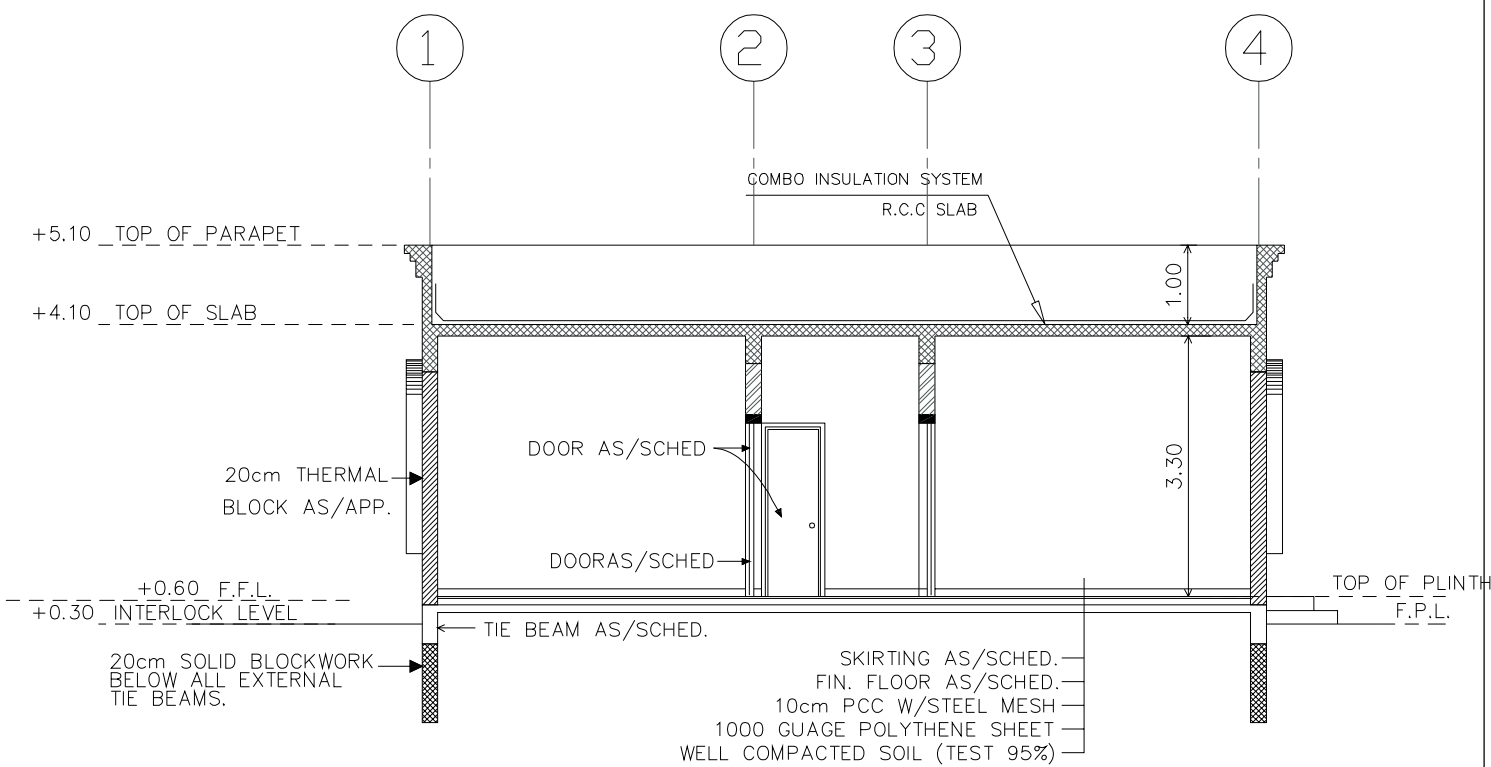

SECTION X-X
(SCALE = 1 : 100)

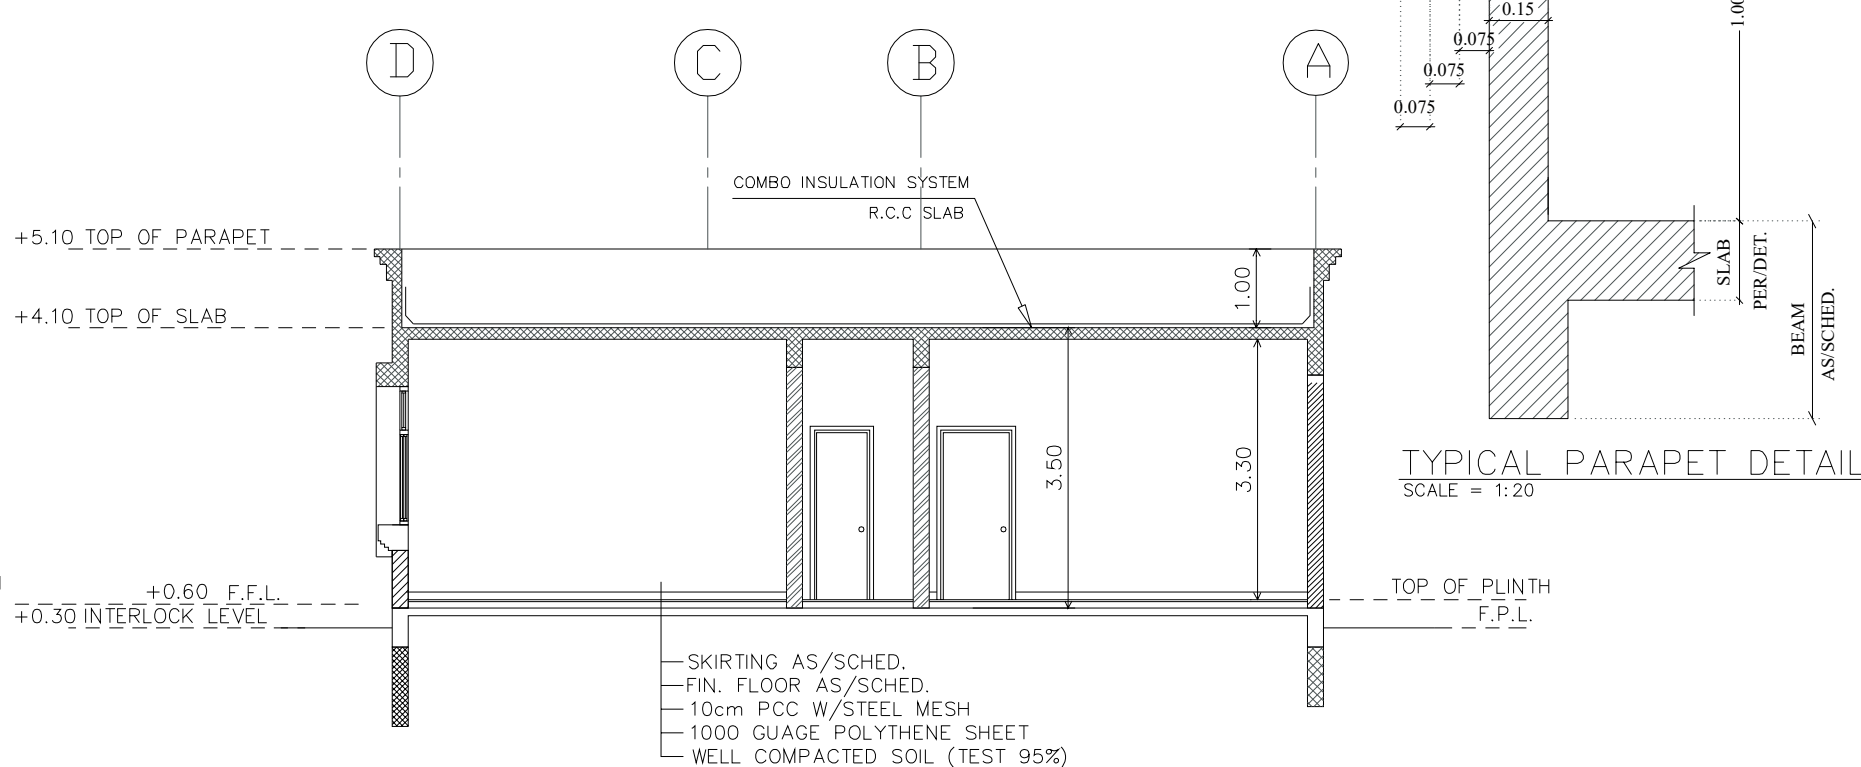

SECTION Y-Y
(SCALE = 1 : 100)

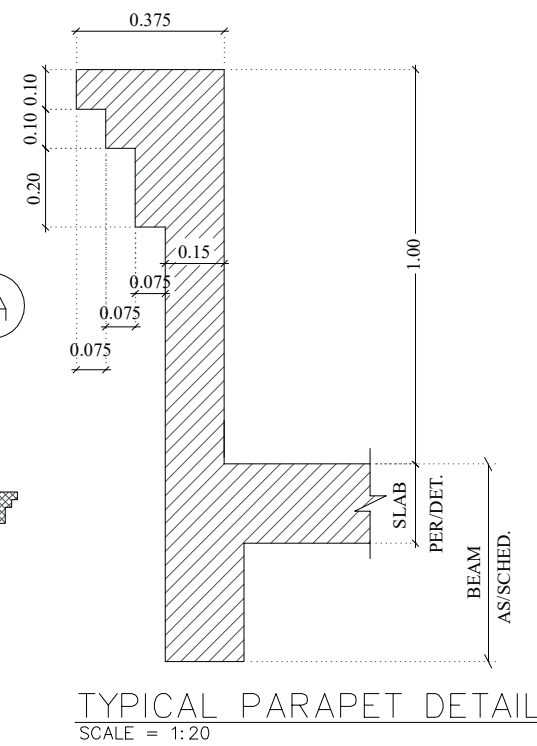

CLIENT:

GOVERNMENT OF SHARJAH -
DEPARTMENT OF ISLAMIC AFFAIRS

PROJECT:

(SIA - SM-02)
PROPOSED MASJID + ABLUTION +
IMAM HOUSE

SHEET TITLE:

IMAM HOUSE
ELEVATIONS & SECTION

ARCHITECT

Arch. Mostafa Ramadan

TYPE

ARCHITECTURE

STRUCTURAL

Eng : Mohamed Gomaa

SHEET

No.

A - 13

CHECKED BY

Eng : Mohamed Attia

Location :

Plot No :

SCALE







1:100

DATE

March - 2022

Project

No.

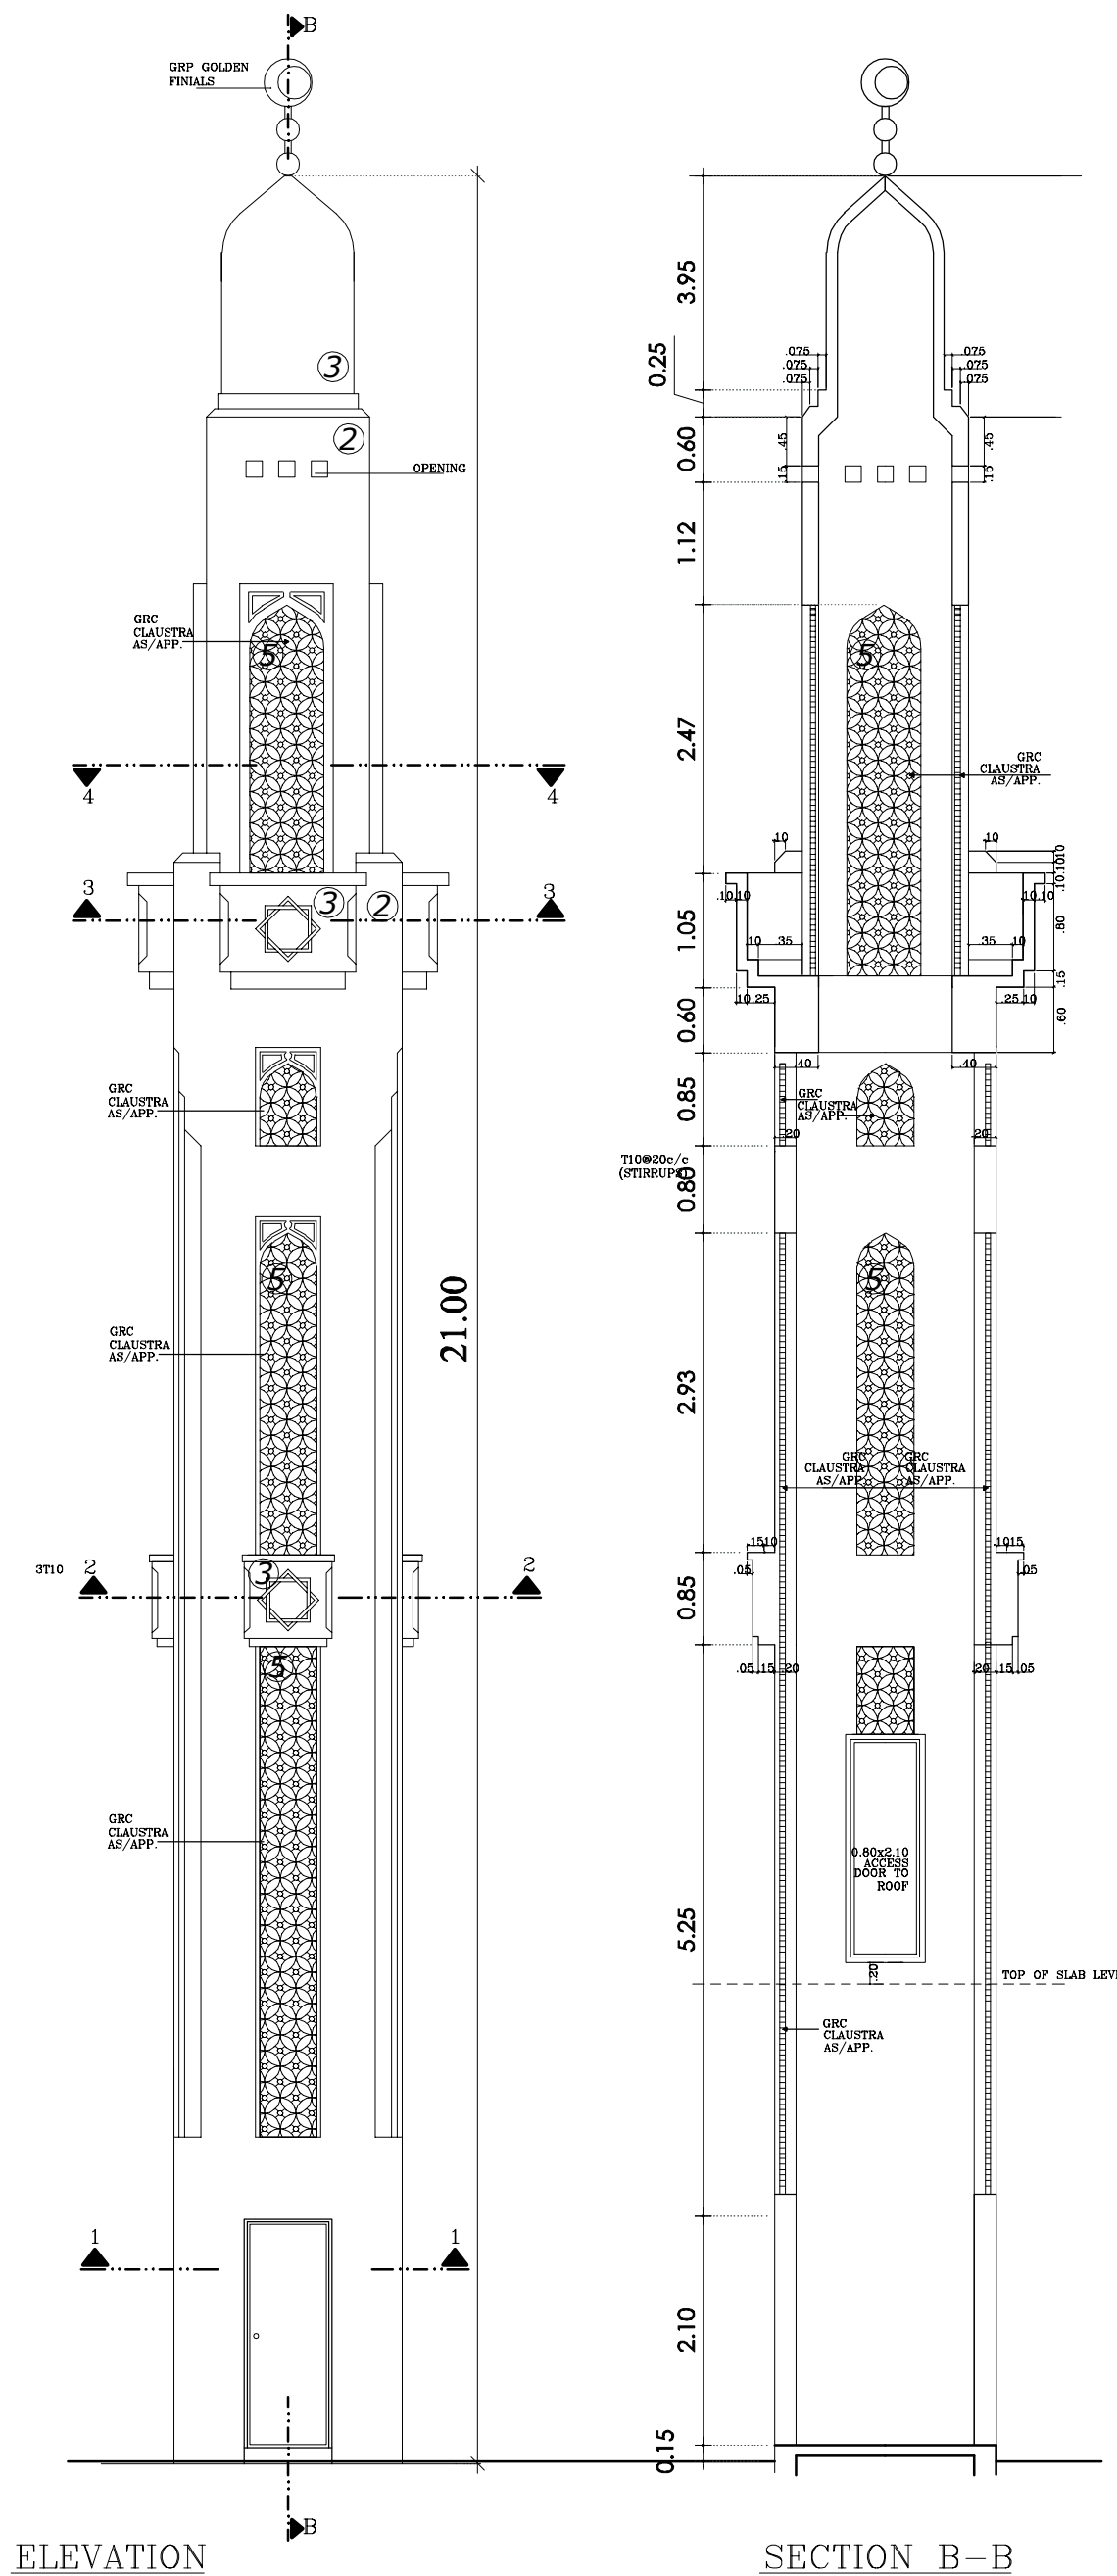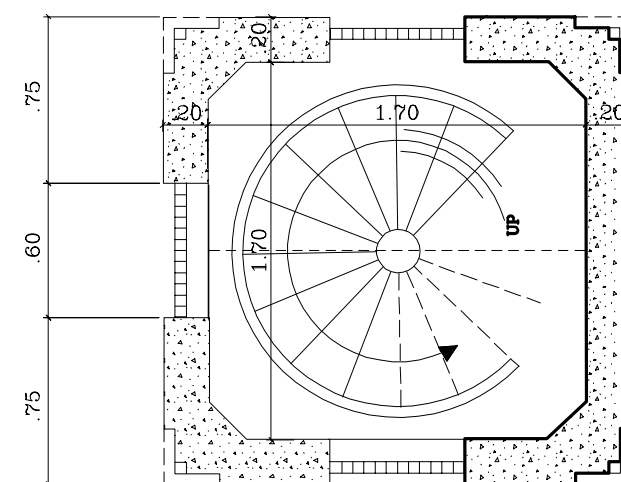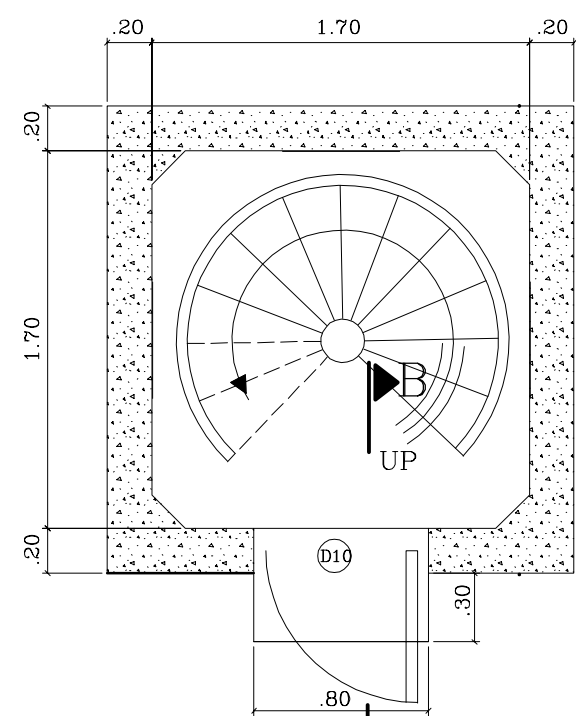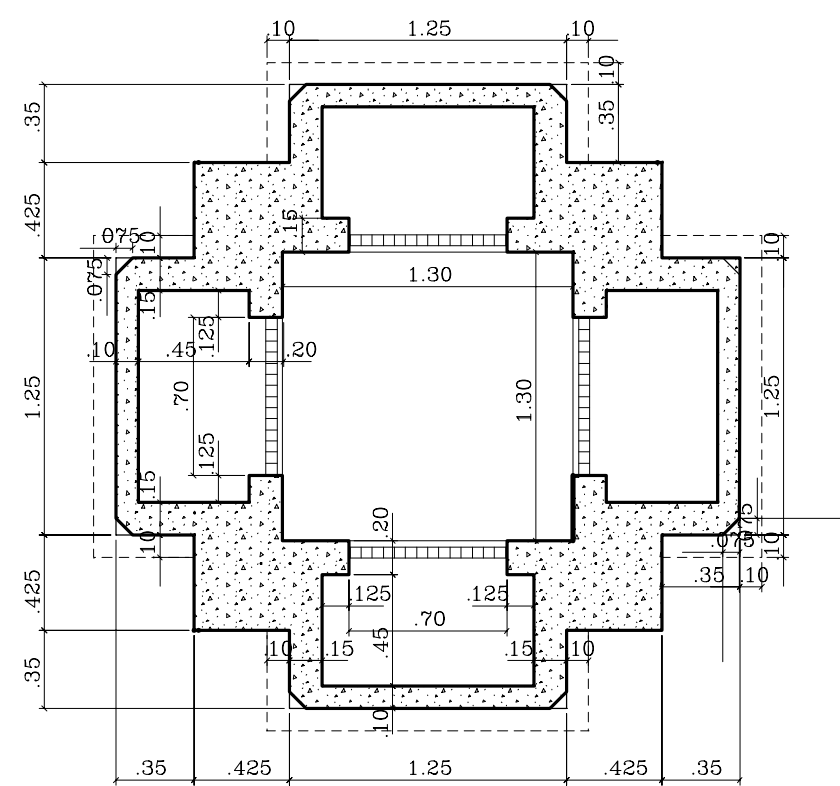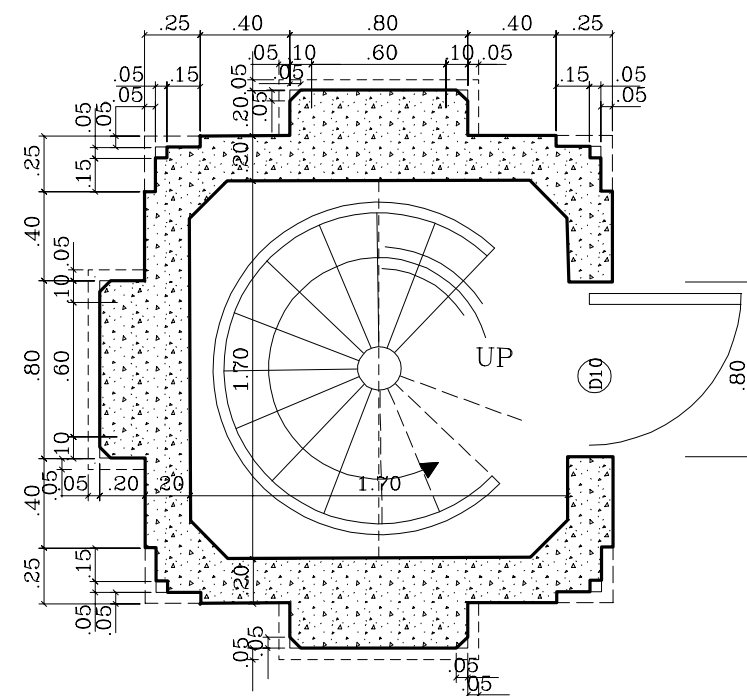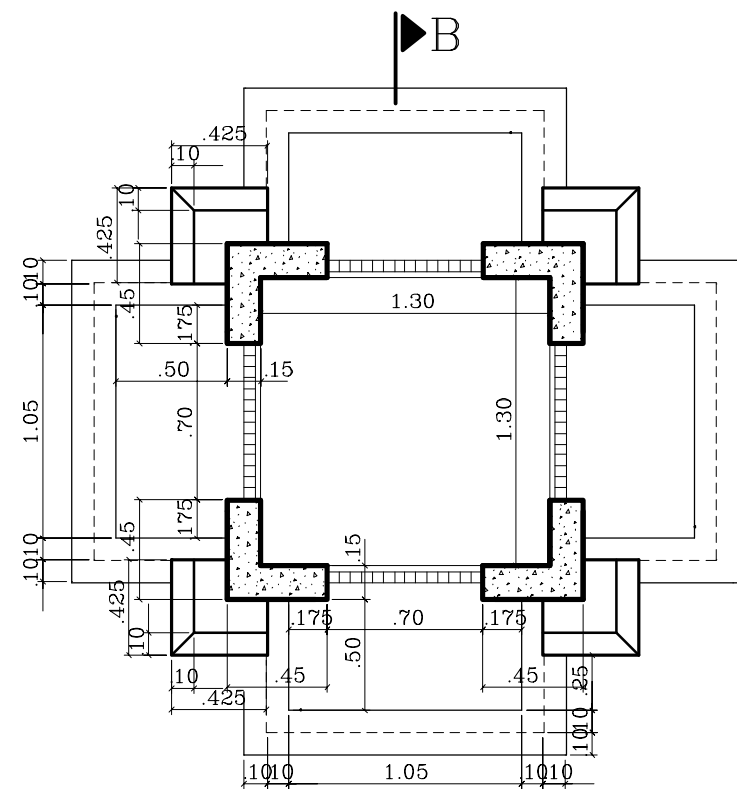

GENERAL NOTES:

1. IT IS NOT ALLOWED TO REPRODUCE THE SHEETS CONTENTS IN ANY FORM EXCEPT FOR THE PURPOSE FOR WHICH IT IS INTENDED.
2. THESE DRAWINGS ARE DIAGRAMMATIC AND SHALL NOT BE SCALED. ADDITIONAL DATA SHALL BE REQUESTED FROM THE CONSULTANCY THROUGH WRITTEN CLARIFICATION. VERIFY ALL EXISTING CONDITIONS AND DIMENSIONS BEFORE PROCEEDING WITH ANY PORTION OF ANY WORK.
3. NO CHANGES, MODIFICATIONS OR DEVIATIONS SHALL BE WRITTEN PERMISSION FROM **ALMASAH ENGINEERING CONSULTANTS**.
4. ALL WORK AS OUTLINED IN THESE DOCUMENTS, SHALL STRICTLY CONFORM TO ALL APPLICABLE CODES. IN THE EVENT OF A CONFLICT, THE MORE STRINGENT REQUIREMENT SHALL GOVERN AND BE MET.

SIA - SM-02



حُكُومَةُ الشَّارِقَةِ
دائرة الشؤون الإسلامية

دائرة الشؤون الإسلامية

CONSULTANT STAMP



CLIENT:

GOVERNMENT OF SHARJAH -
DEPARTMENT OF ISLAMIC AFFAIRS

PROJECT:

(SIA - SM-02)
PROPOSED MASJID + ABLUTION +
IMAM HOUSE

SHEET TITLE:

ARCHITECTURAL DETAILS
FOR MINARET

ARCHITECT

Arch. Mostafa Ramadan

TYPE

ARCHITECTURE

STRUCTURAL

Eng : Mohamed Gomaa

	SHEET	
--	-------	--

A - 14

CHECKED BY

Eng : Mohamed Attia

Location :

Plot No :

SCALE


1:100

DATE

March - 2022

	Project	

Project No.	
-------------	--

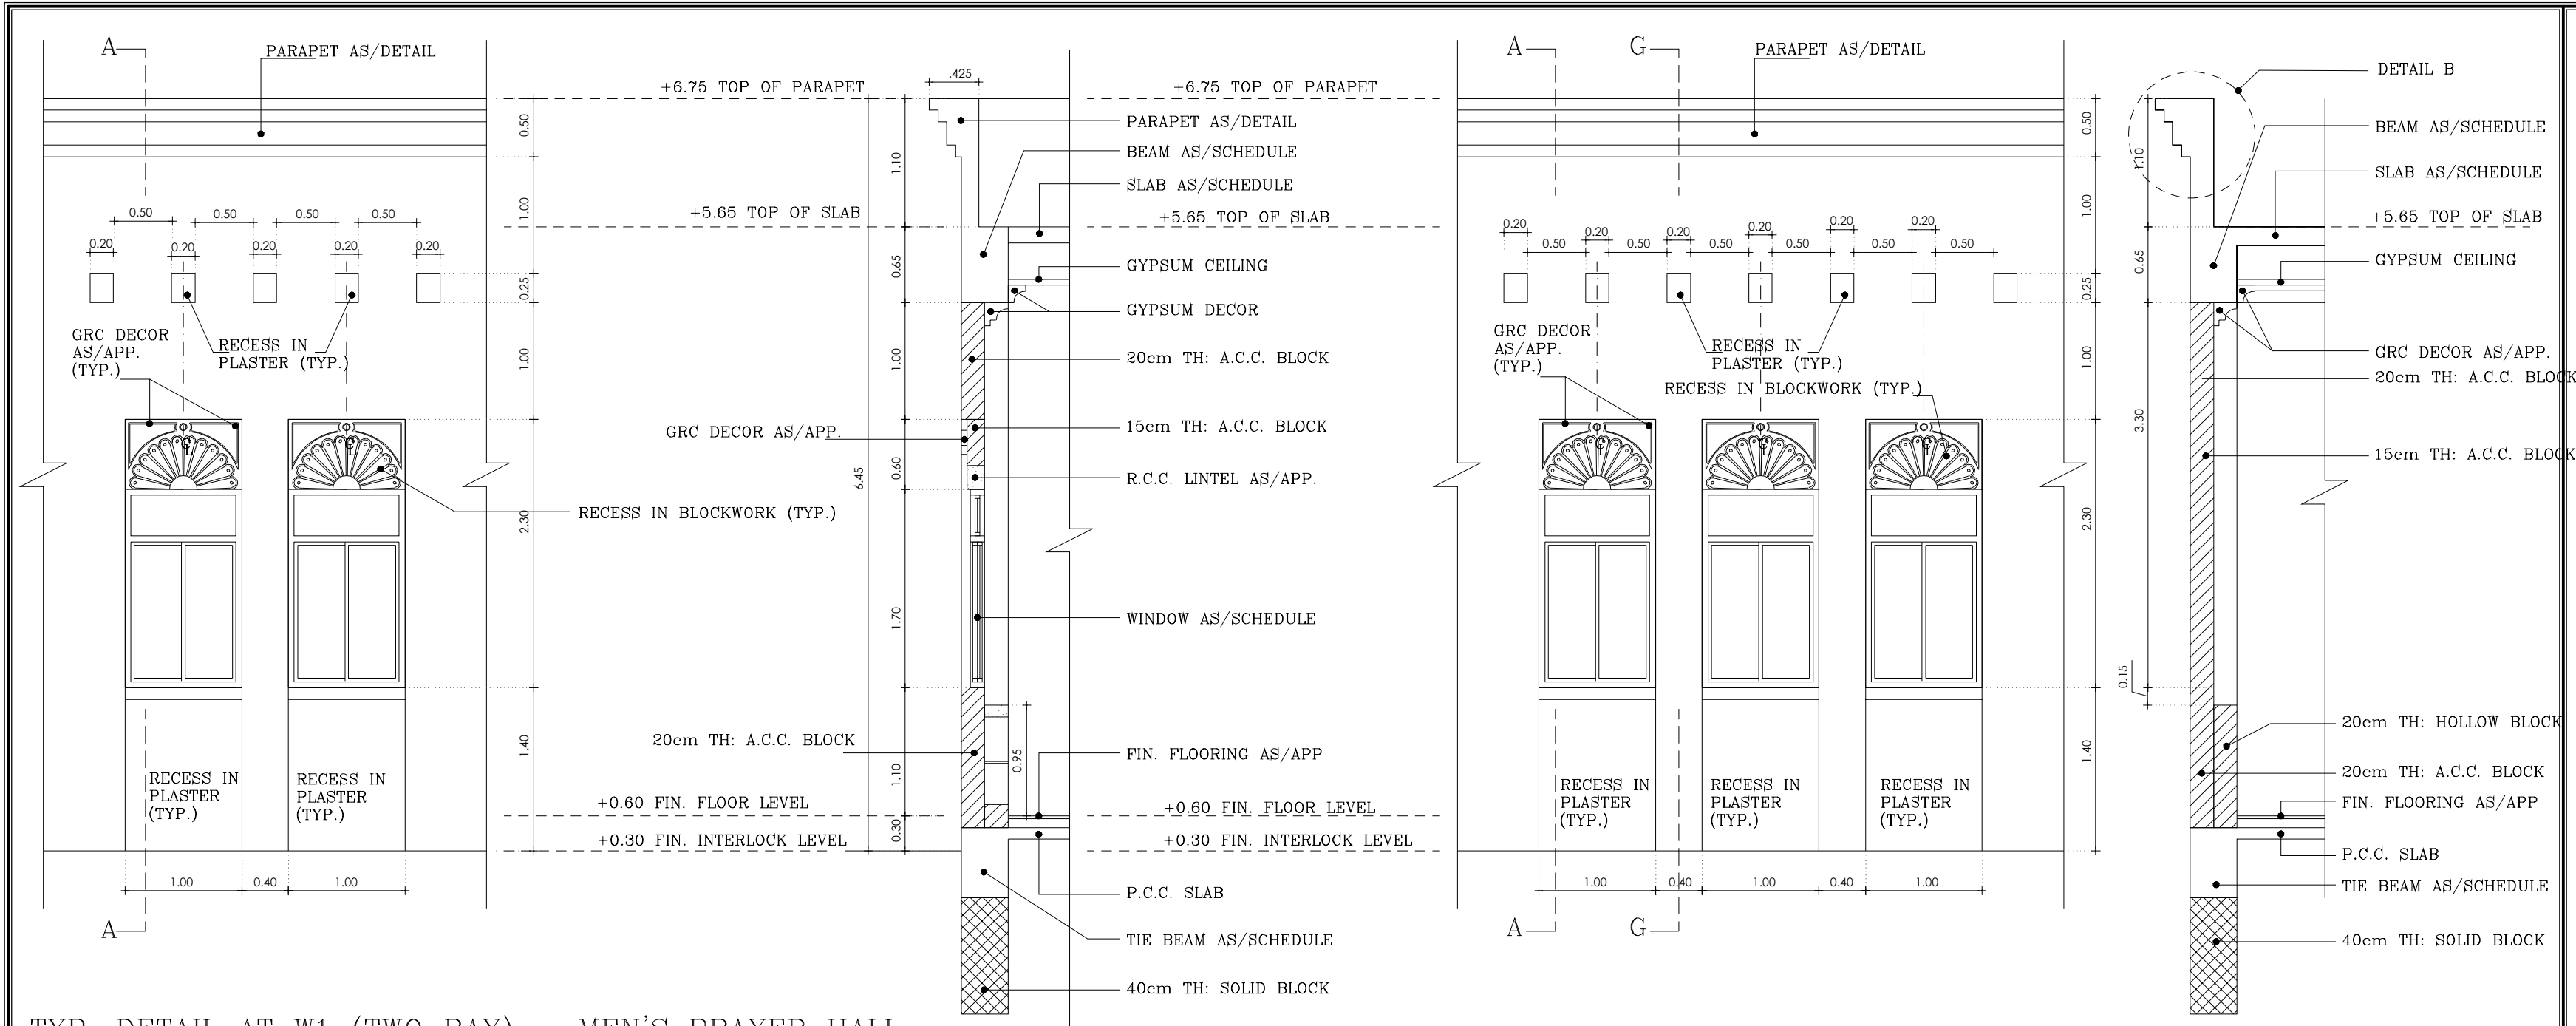


TYP. DETAIL AT W1 (TWO BAY) – MEN’S PRAYER HALL

SECTION A–A

TYP. DETAIL AT W1 (THREE BAY) – MEN’S PRAYER HALL

SECTION G–G

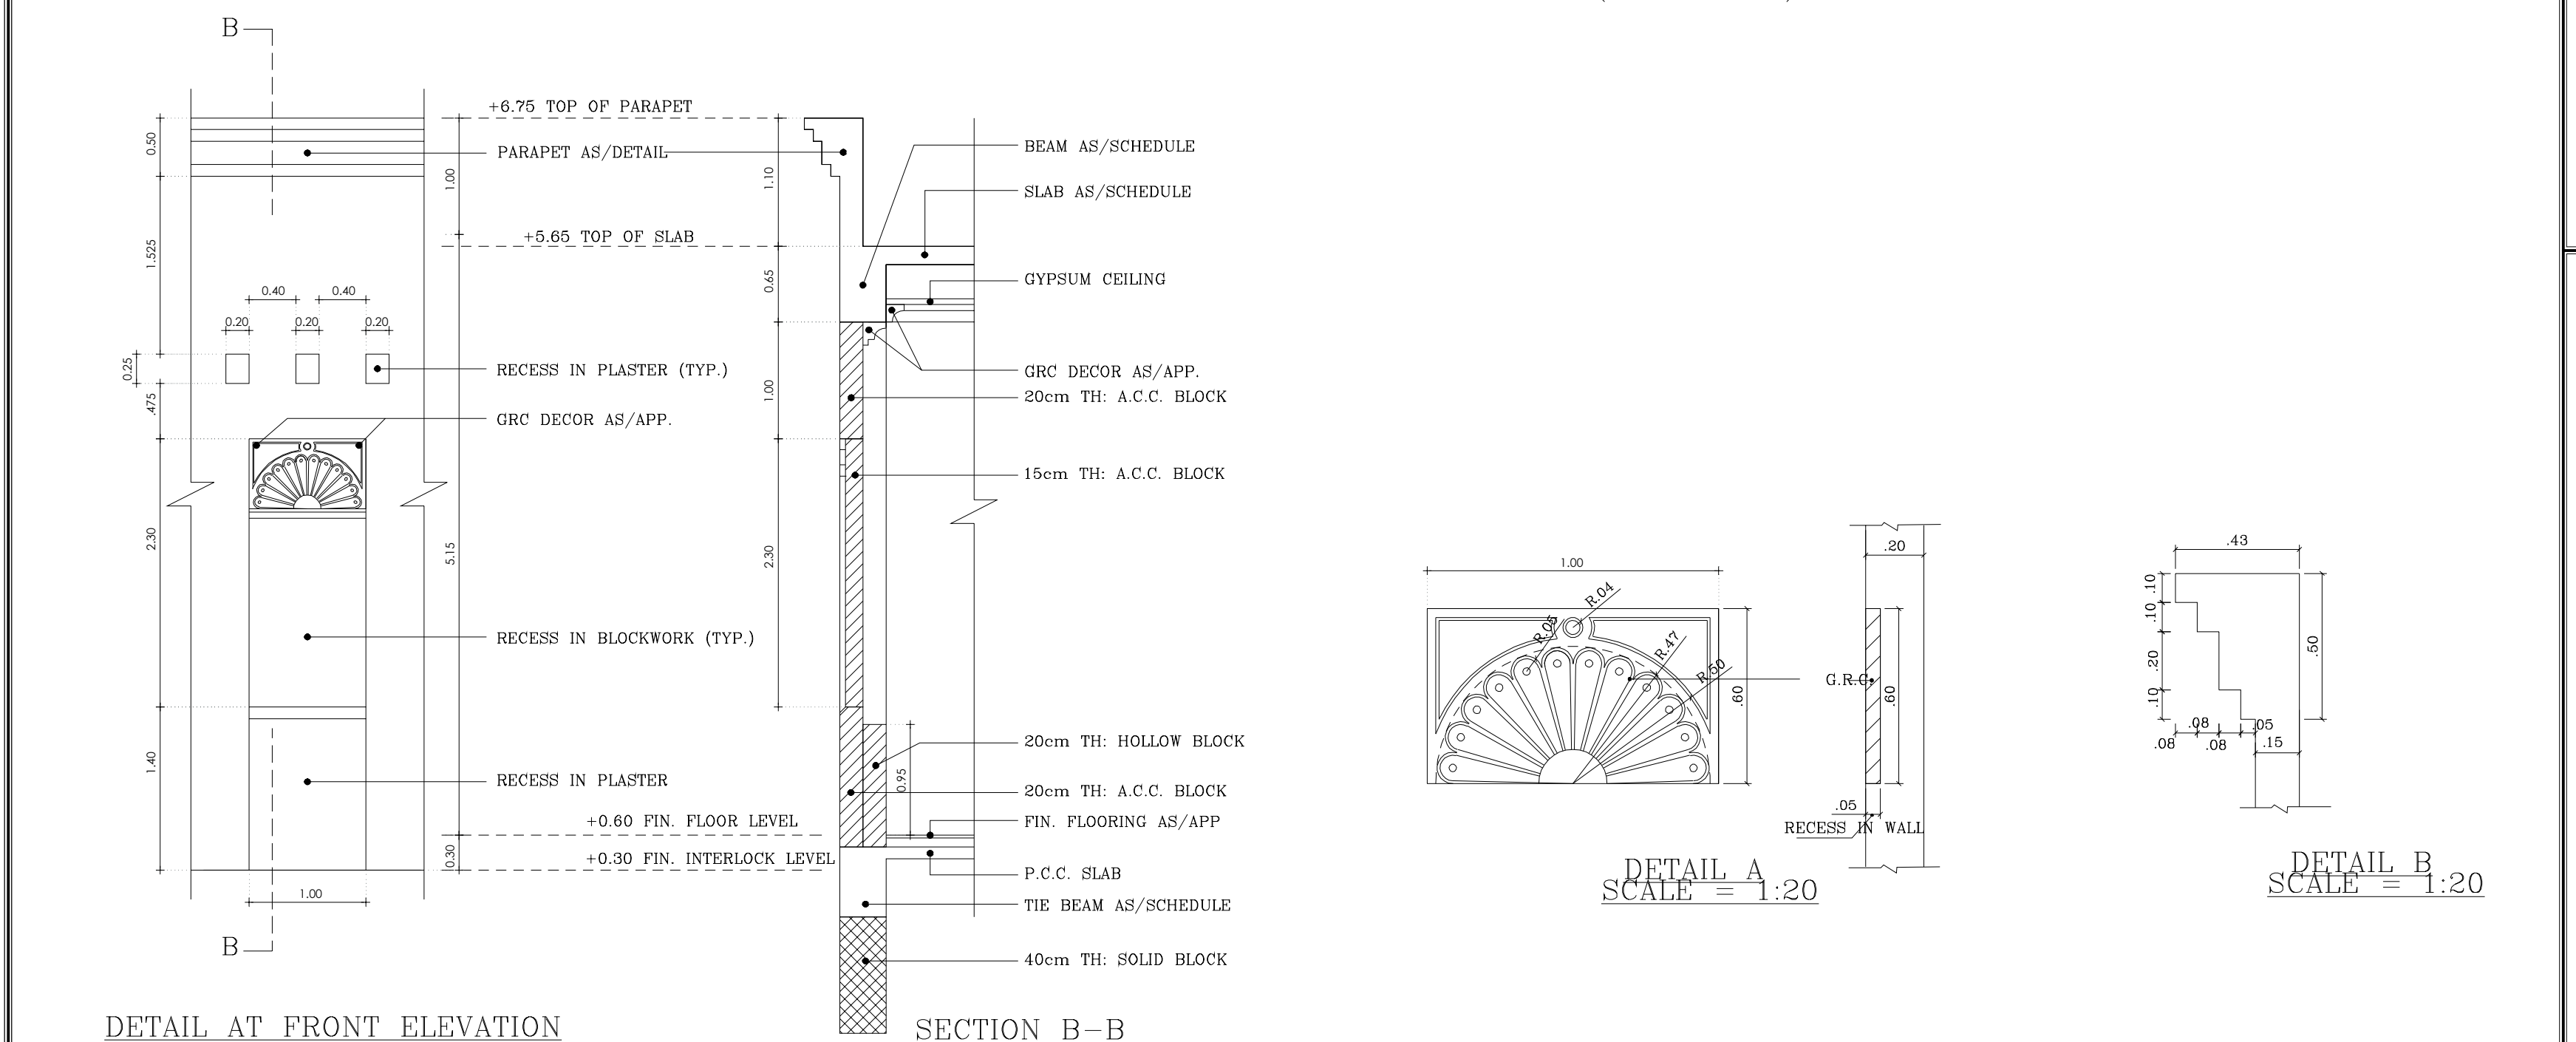

DETAIL AT FRONT ELEVATION

SECTION B–B

- GENERAL NOTES:**
1. IT IS NOT ALLOWED TO REPRODUCE THE SHEETS CONTENTS IN ANY FORM EXCEPT FOR THE PURPOSE FOR WHICH IT IS INTENDED.
 2. THESE DRAWINGS ARE DIAGRAMMATIC AND SHALL NOT BE SCALED. ADDITIONAL DATA SHALL BE REQUESTED FROM THE CONSULTANCY THROUGH WRITTEN CLARIFICATION. VERIFY ALL EXISTING CONDITIONS AND DIMENSIONS BEFORE PROCEEDING WITH ANY PORTION OF ANY WORK.
 3. NO CHANGES, MODIFICATIONS OR DEVIATIONS SHALL BE WRITTEN PERMISSION FROM **ALMASAH ENGINEERING CONSULTANTS**.
 4. ALL WORK AS OUTLINED IN THESE DOCUMENTS, SHALL STRICTLY CONFORM TO ALL APPLICABLE CODES. IN THE EVENT OF A CONFLICT, THE MORE STRINGENT REQUIREMENT SHALL GOVERN AND BE MET.

SIA - SM-02




حكومة الشارقة
دائرة الشؤون الإسلامية

CONSULTANT STAMP



CLIENT: GOVERNMENT OF SHARJAH - DEPARTMENT OF ISLAMIC AFFAIRS			
PROJECT: (SIA - SM-02) PROPOSED MASJID + ABLUATION + IMAM HOUSE			
SHEET TITLE: ARCHITECTURE DETAILS			
ARCHITECT Arch. Mostafa Ramadan	TYPE	ARCHITECTURE	
STRUCTURAL Eng : Mohamed Gomaa	SHEET No.	A - 15	
CHECKED BY Eng : Mohamed Attia	Location :		
SCALE 1:100	DATE March - 2022	Project No.	

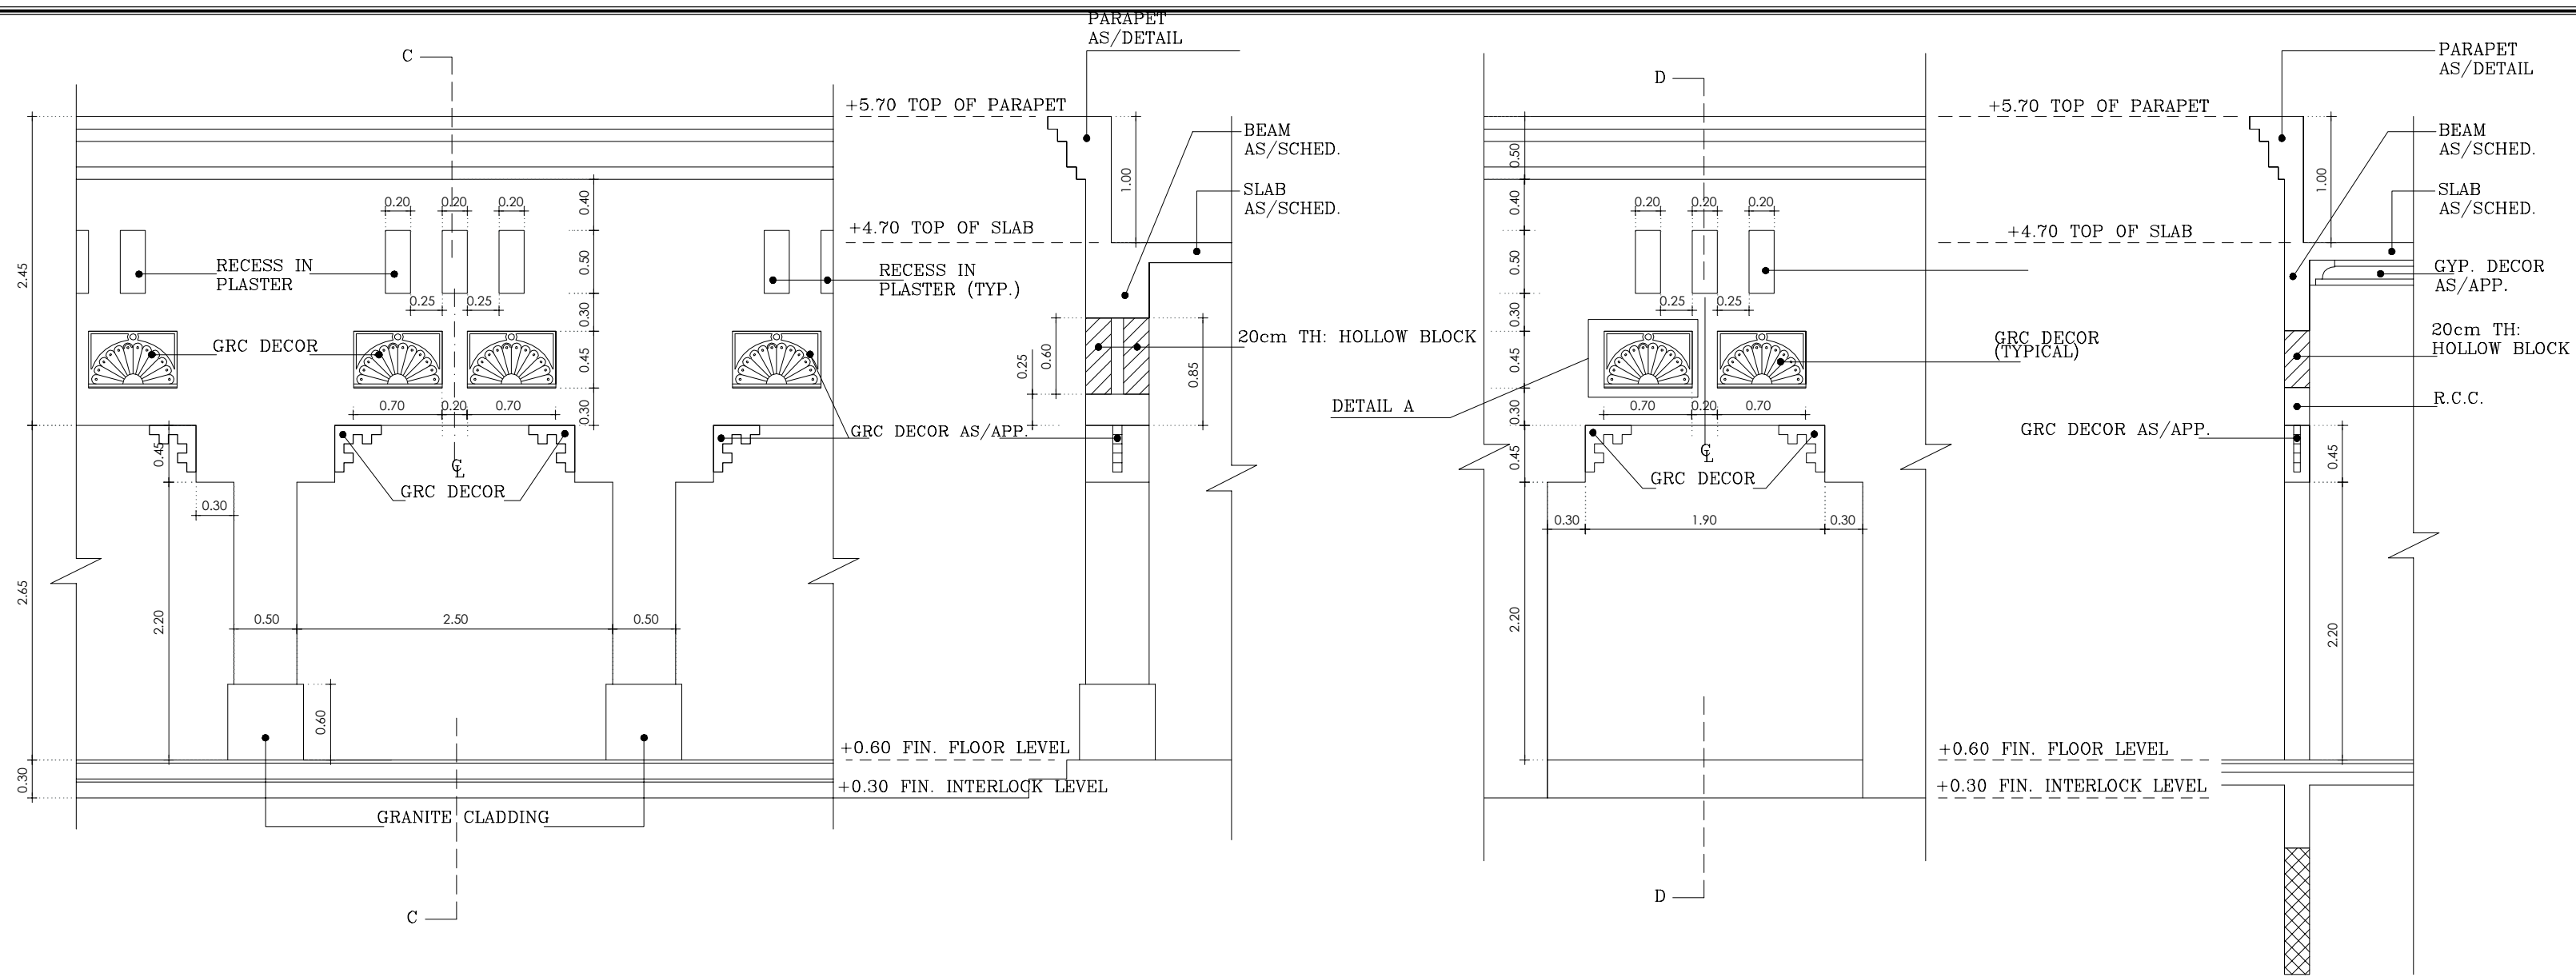


TYP. DETAIL AT FRONT ENTRANCE – MAIN MOSQUE

SECTION C–C

TYP. DETAIL AT LADIES ENTRANCE

SECTION D–D

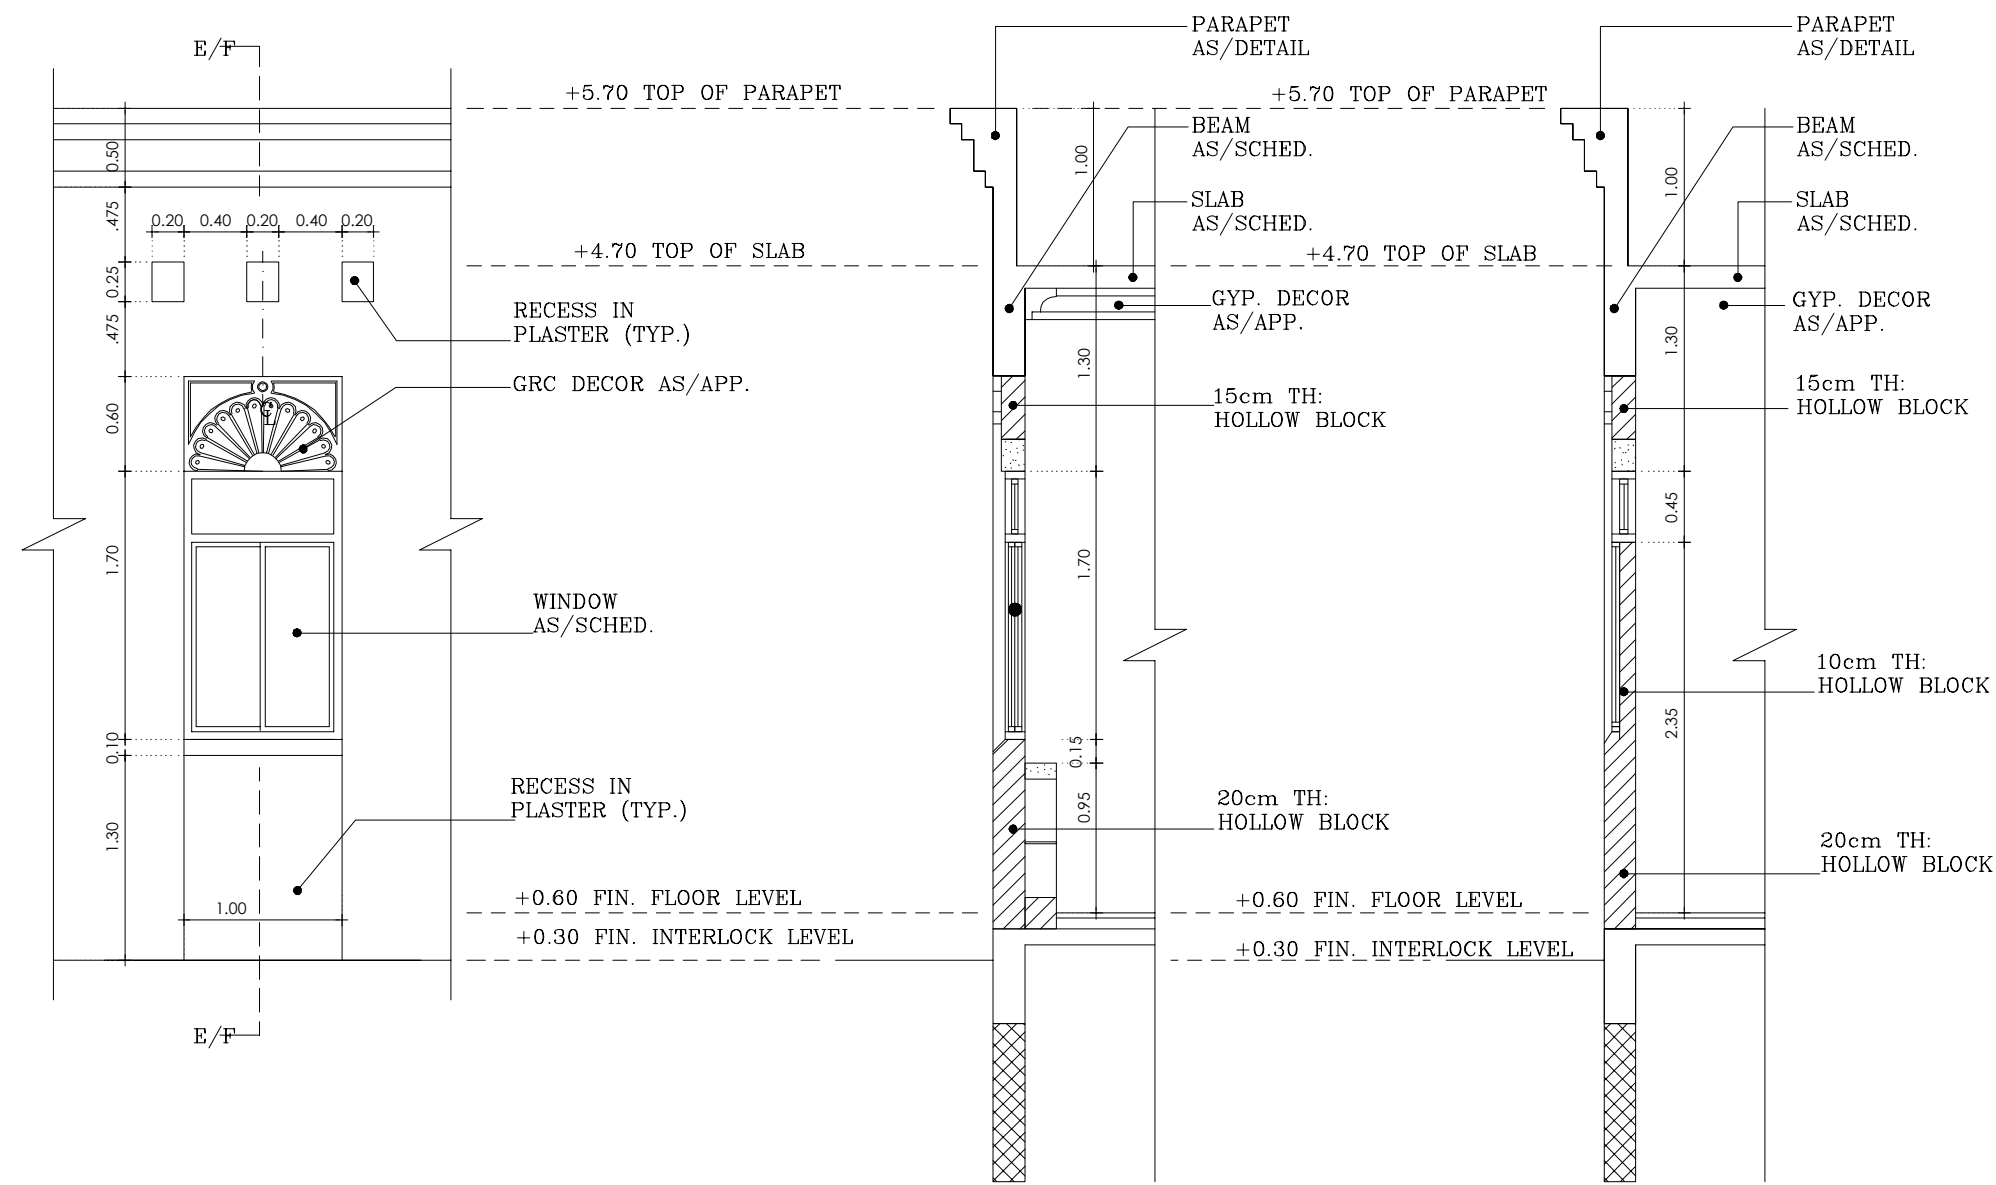

DETAIL AT W1/W4/W5

SECTION E–E AT W1 (LADIES PRAYER)

SECTION F–F AT W4/W5

GENERAL NOTES:


1. IT IS NOT ALLOWED TO REPRODUCE THE SHEETS CONTENTS IN ANY FORM EXCEPT FOR THE PURPOSE FOR WHICH IT IS INTENDED.
2. THESE DRAWINGS ARE DIAGRAMMATIC AND SHALL NOT BE SCALED. ADDITIONAL DATA SHALL BE REQUESTED FROM THE CONSULTANCY THROUGH WRITTEN CLARIFICATION. VERIFY ALL EXISTING CONDITIONS AND DIMENSIONS BEFORE PROCEEDING WITH ANY PORTION OF ANY WORK.
3. NO CHANGES, MODIFICATIONS OR DEVIATIONS SHALL BE WRITTEN PERMISSION FROM **ALMASAH ENGINEERING CONSULTANTS**.
4. ALL WORK AS OUTLINED IN THESE DOCUMENTS, SHALL STRICTLY CONFORM TO ALL APPLICABLE CODES. IN THE EVENT OF A CONFLICT, THE MORE STRINGENT REQUIREMENT SHALL GOVERN AND BE MET.

SIA - SM-02



حُكُومَةُ الشَّارِقَةِ
دائرة الشؤون الإسلامية

CONSULTANT STAMP

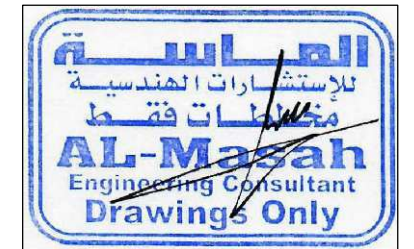

CLIENT:

GOVERNMENT OF SHARJAH -
DEPARTMENT OF ISLAMIC AFFAIRS


PROJECT:

(SIA - SM-02)
PROPOSED MASJID + ABLUTION +
IMAM HOUSE

SHEET TITLE:


ARCHITECTURE DETAILS

ARCHITECT Arch. Mostafa Ramadan	TYPE ARCHITECTURE
STRUCTURAL Eng : Mohamed Gomaa	SHEET No. A - 16
CHECKED BY Eng : Mohamed Attia	Location : Plot No :
SCALE 1:100	DATE March - 2022
	Project No.

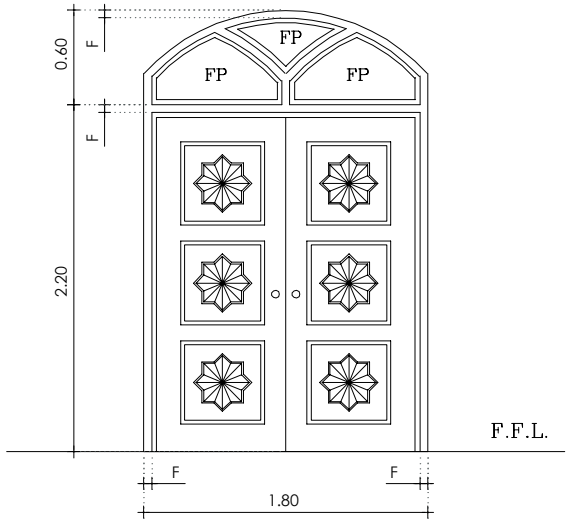


* DECORATIVE SOLID PANEL DOOR AS PER APPROVAL
WINDOW GLAZING = 6mm TH. REF./TINTED GLASS OUTSIDE AND 6mm THICK SANDBLASTED GLASS INSIDE WITH 12mm AIRSPACE IN BETWEEN.

D1 IRONMONGERY TYPE - A

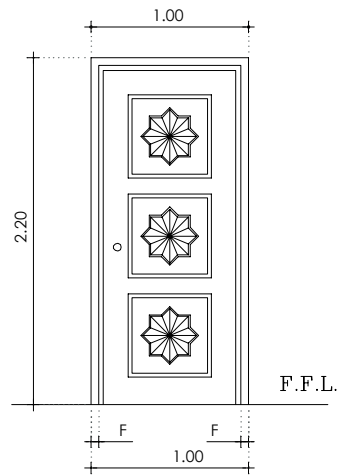


* DECORATIVE SOLID PANEL DOOR AS PER APPROVAL

D2 IRONMONGERY TYPE - A

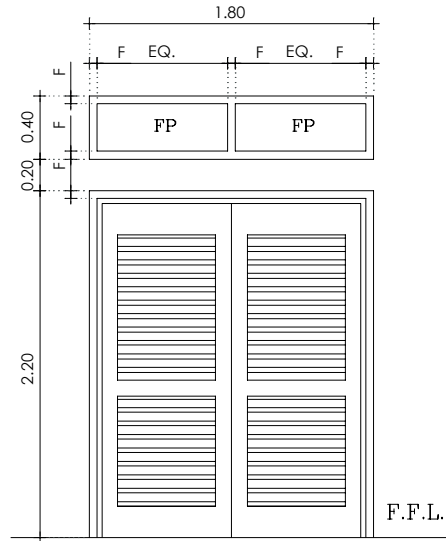


* HEAVY SECTION POWDER COATED LOUVERED ALUMINUM DOOR. COLOR AS PER APPROVAL

D3 IRONMONGERY TYPE - C

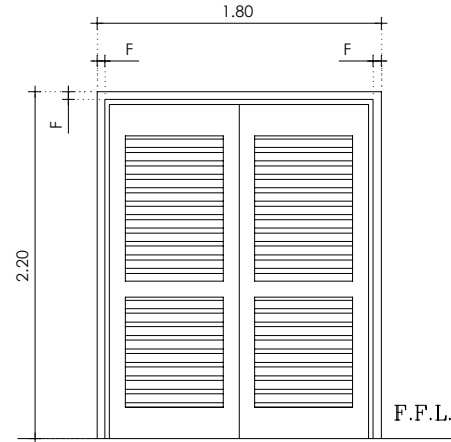

* HEAVY SECTION POWDER COATED LOUVERED ALUMINUM DOOR. COLOR AS PER APPROVAL


D4 IRONMONGERY TYPE - C

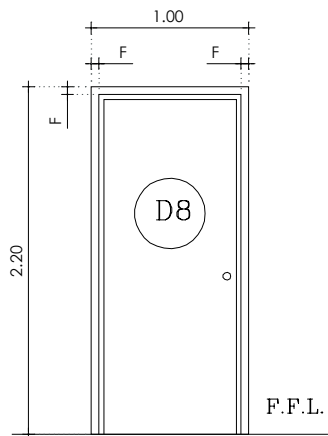

IRONMONGERY TYPE - C

SINGLE LEAF WOODEN FLUSH DOOR WITH MERRANTI WOOD FRAME 4.5cm TH: AND WIDTH AS/WALL THICKNESS WITH TEAK PLY VENEERED SHUTTER WITH AN INTERNAL SOLIDITY OF 75% ALL POLISHED WITH LAQUER POLISH AS PER APPROVAL. WITH DOOR CLOSER MACHINE AS PER APPROVAL FOR WOMEN ABLUTION.


D8

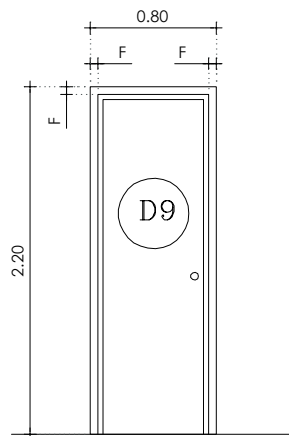

IRONMONGERY TYPE - D


SINGLE LEAF WOODEN FLUSH DOOR WITH MERRANTI WOOD FRAME 4.5cm TH: AND WIDTH AS/WALL THICKNESS WITH TEAK PLY VENEERED SHUTTER WITH AN INTERNAL SOLIDITY OF 75% ALL POLISHED WITH LAQUER POLISH AS PER APPROVAL.

D9

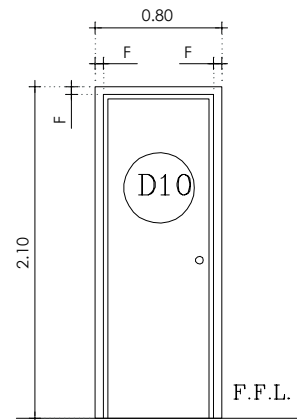

* MEDIUM SECTION POWDER COATED LOUVERED ALUMINUM DOOR. COLOR AS PER APPROVAL

D10 IRONMONGERY TYPE - C

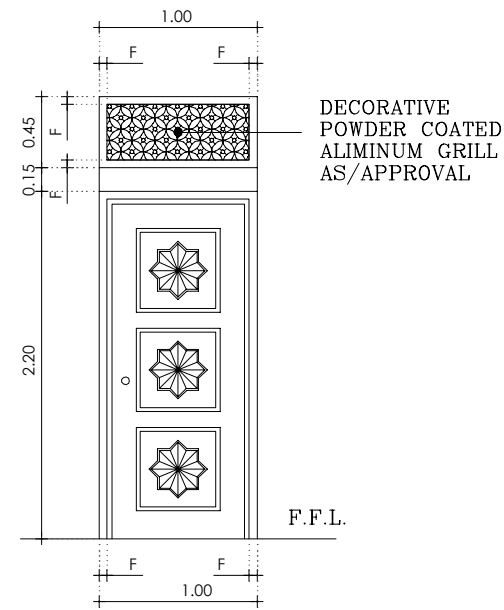

D11 IRONMONGERY TYPE - A

GENERAL DOOR/WINDOW NOTES

- 1-DRAWINGS ARE NOT TO BE SCALED.
- 2-THIS DRAWING IS TO BE READ IN CONJUNCTION WITH ALL OTHER RELEVANT DRAWINGS.
- 3-CONTRACTOR IS TO CONFIRM AND WORK TO ACTUAL EXIST. DIMENSIONS ON SITE.
- 4-ALL DIMENSIONS RELATE TO STRUCTURAL OPENINGS UNLESS OTHERWISE NOTED.
- 5-CONTRACTOR SHALL SUBMIT ALL NECESSARY DOOR/WINDOW SHOP DRAWINGS FOR APPROVAL PRIOR TO FABRICATION AND INSTALLATION.
- 6-ALL WOODEN DOORS TO HAVE ARCHITRAVES ON BOTH SIDES AS PER APPROVAL.
- 7-ALL FLUSH DOOR SHUTTERS SHOULD BE MIN. 75% SOLID INSIDE AS PER APPROVAL.
- 8-ALL ALUMINUM DOORS/WINDOWS TO HAVE ALUMINUM ARCHITRAVE BOTH SIDES AS PER APPROVAL UNLESS NOTED OTHERWISE.
- 9-ALL DOOR CLOSERS ARE TO HAVE 90 DEGREE HOLD OPEN FACILITY.
- 10ALL EXTERNAL DOORS SHALL HAVE WEATHER SEALS.
- 11ALL GLAZING BELOW 90cm ABOVE FINISH FLOOR LEVEL SHALL BE WITH TEMPERED GLASS

TIMBER OPENINGS

- 1- ALL DOORS SHALL BE COMPLETE WITH 1-1/2 PAIR OF BRASS HINGES (3 PAIR HEAVY DUTY FOR DOUBLE DOORS) & APPROVED QUALITY LOCKS, CLOSERS, HANDLES, BOLTS AND DOOR STOPS AS NOTED.
- 2-CONTRACTOR SHALL SUBMIT SAMPLES OF ALL IRON MONGERY TO BE USED FOR CONSULTANTS APPROVAL PRIOR TO PLACING AN ORDER.
- 3-DOOR FRAME SHALL BE SECURED TO OPENINGS WITH MIN. 3 No.'s 10mm dia. & 4" LONG EXPANDING BOLTS.
- 4-ALL INSIDE FACES OF TIMBER FRAMES TO BE PAINTED WITH PRESERVATIVE PAINT OF APPROVED QUALITY.
- 5-ALL PANELLED DOORS SHALL HAVE STILES, TOP RAIL & MIDDLE RAIL MIN. 4" WIDE. BOTTOM RAIL MIN. 8" WIDE. DECORATIVE PANELS AS/APPROVED DESIGN.
- 6-PROVIDE 3/4" x 9" OR 5" MARINE PLYWOOD SUBFRAMES TO ALL DOOR OPENINGS.
- 7- ALL FLUSH DOORS TO BE 100% SOLID CORE OR 80% SEMI-SOLID CORE WITH HARDWOOD LIPPING ALL AROUND AS PER SPECIFICATIONS.
- 8-PROVIDE 2" x 9" OR 2" x 5" DECORATIVE RED MERRANTI WOOD FRAME ON BOTH SIDES.

ALUMINUM OPENINGS

- 1-CONTRACTOR SHALL SUBMIT ALL SAMPLES OF ALL ALUM. SECTIONS, GLAZING, LOCKS, HANDLES ETC., FOR APPROVAL OF CONSULTANT PRIOR TO PLACING AN ORDER.
- 2-ALL ALUMINUM OPENINGS TO HAVE .75" MARINE PLY SUB-FRAME OR TREATED RED MERANTI AS/APPROVAL.
- 3-ALL ALUMINUM OPENINGS TO BE SEALED WITH 2 PARTS POLYSULPHIDE SEALANT MIN .25" THICK.
- 4-DRAINAGE WEEP HOLES TO BE PROVIDED AT THE BOTTOMS OF ALL ALUMINUM FRAMES AS PER APPROVAL.
- 5-ALL ALUMINUM DOORS AND WINDOW S SHALL BE COMPLETE WITH APPROPRIATE HANDLES, LOCKS, SLIDING GEAR ETC., WHICH SHALL BE OF APPROVED QUALITY AND DESIGN.
- 6-WHERE EVER MARINE PLY SUBFRAME IS EXPOSED PROVIDE 1 9/32THICK RED MERRANTI COVER SLIP (SCREWED) TO CONCEAL THE SAME/EXPOSED SURFACES TO BE TREATED WITH APP. PRESERVATIVE PAINT.
- 7-ALL SILL HEIGHTS ARE FROM FINISH FLOOR LEVEL UNLESS NOTED OTHERWISE.
- 8-FLY MESH SCREENS TO BE FROM INSIDE UNLESS NOTED OTHERWISE

DOOR IRONMONGERY SCHEDULE TYPE - A

1. LEVER HANDLE BOTH SIDES
2. CYLINDER WITH KEY OPERATION BOTH SIDES
3. APPROPRIATE LOCK CASE AND STRIKE PLATE
4. 4 PAIR HINGES
5. LEVER ACTION FLUSH BOLTS (TOP/BOT) BOTH LEAF'S
6. OVERHEAD DOOR CLOSER
7. DOOR STOPS

TYPE - B

1. LEVER HANDLE BOTH SIDES
2. CYLINDER WITH KEY OPERATION BOTH SIDES
3. APPROPRIATE LOCK CASE AND STRIKE PLATE
4. 1? PAIR HINGES
5. OVERHEAD DOOR CLOSER
6. DOOR STOPS

TYPE - C

1. LEVER HANDLE BOTH SIDES
 2. CYLINDER WITH KEY OPERATION BOTH SIDES
 3. APPROPRIATE LOCK CASE AND STRIKE PLATE
 4. 1%129 PAIR HINGES
 5. DOOR STOPS
- #### TYPE - D
1. LEVER HANDLE BOTH SIDES
 2. THUMB TURN ONE SIDE
 3. EMERGENCY RELEASE WITH INDICATOR OTHER SIDE
 4. 1%129 PAIR HINGES
 5. DOOR STOPS

GENERAL NOTES:


- 1.IT IS NOT ALLOWED TO REPRODUCE THE SHEETS CONTENTS IN ANY FORM EXCEPT FOR THE PURPOSE FOR WHICH IT IS INTENDED.
2. THESE DRAWINGS ARE DIAGRAMMATIC AND SHALL NOT BE SCALED. ADDITIONAL DATA SHALL BE REQUESTED FROM THE CONSULTANCY THROUGH WRITTEN CLARIFICATION. VERIFY ALL EXISTING CONDITIONS AND DIMENSIONS BEFORE PROCEEDING WITH ANY PORTION OF ANY WORK.
3. NO CHANGES, MODIFICATIONS OR DEVIATIONS SHALL BE WRITTEN PERMISSION FROM **ALMASAH ENGINEERING CONSULTANTS**.
4. ALL WORK AS OUTLINED IN THESE DOCUMENTS, SHALL STRICTLY CONFORM TO ALL APPLICABLE CODES. IN THE EVENT OF A CONFLICT, THE MORE STRINGENT REQUIREMENT SHALL GOVERN AND BE MET.

SIA - SM-02



حُكُومَةُ الشَّارِقَةِ
دائرة الشؤون الإسلامية

CONSULTANT STAMP

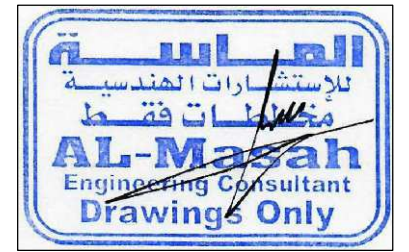

CLIENT:

**GOVERNMENT OF SHARJAH -
DEPARTMENT OF ISLAMIC AFFAIRS**



PROJECT:

**(SIA - SM-02)
PROPOSED MASJID + ABLUTION +
IMAM HOUSE**




SHEET TITLE:

DETAIL OF DOORS

ARCHITECT Arch. Mostafa Ramadan	TYPE	ARCHITECTURE
STRUCTURAL Eng : Mohamed Gomaa	SHEET No.	A - 17
CHECKED BY Eng : Mohamed Attia	Location :	
SCALE 1:100	DATE March - 2022	Plot No : Project No.

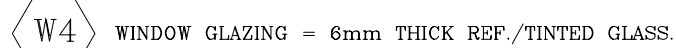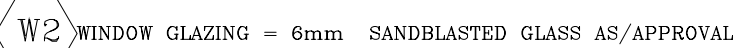

1. IT IS NOT ALLOWED TO REPRODUCE THE SHEETS CONTENTS IN ANY FORM EXCEPT FOR THE PURPOSE FOR WHICH IT IS INTENDED.
2. THESE DRAWINGS ARE DIAGRAMMATIC AND SHALL NOT BE SCALED. ADDITIONAL DATA SHALL BE REQUESTED FROM THE CONSULTANCY THROUGH WRITTEN CLARIFICATION. VERIFY ALL EXISTING CONDITIONS AND DIMENSIONS BEFORE PROCEEDING WITH ANY PORTION OF ANY WORK.
3. NO CHANGES, MODIFICATIONS OR DEVIATIONS SHALL BE WRITTEN PERMISSION FROM **ALMASAH ENGINEERING CONSULTANTS**.
4. ALL WORK AS OUTLINED IN THESE DOCUMENTS, SHALL STRICTLY CONFORM TO ALL APPLICABLE CODES. IN THE EVENT OF A CONFLICT, THE MORE STRINGENT REQUIREMENT SHALL GOVERN AND BE MET.

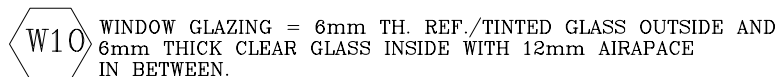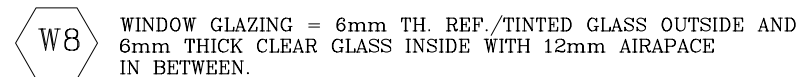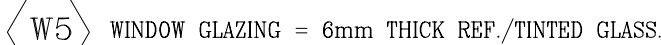


- 1- DRAWINGS ARE NOT TO BE SCALED.
- 2- THIS DRAWING IS TO BE READ IN CONJUNCTION WITH ALL OTHER RELEVANT DRAWINGS.
- 3- CONTRACTOR IS TO CONFIRM AND WORK TO ACTUAL EXISTING DIMENSIONS ON SITE.
- 4- ALL DIMENSIONS RELATE TO STRUCTURAL OPENINGS UNLESS OTHERWISE NOTED.
- 5- CONTRACTOR SHALL SUBMIT ALL NECESSARY DOOR/WINDOW SHOP DRAWINGS FOR APPROVAL PRIOR TO FABRICATION AND INSTALLATION.
- 6- ALL WOODEN DOORS TO HAVE ARCHITRAVES ON BOTH SIDES AS PER APPROVAL.
- 7- ALL FLUSH DOOR SHUTTERS SHOULD BE MIN. 75% SOLID INSIDE AS PER APPROVAL.
- 8- ALL ALUMINUM DOORS/WINDOWS TO HAVE ALUMINUM ARCHITRAVE BOTH SIDES AS PER APPROVAL UNLESS NOTED OTHERWISE.
- 9- ALL DOOR CLOSERS ARE TO HAVE 90 DEGREE HOLD OPEN FUNCTIONALITY.
- 10- ALL EXTERNAL DOORS SHALL HAVE WEATHER SEALS.
- 11- ALL GLAZING BELOW 90cm ABOVE FINISH FLOOR LEVEL SHALL BE WITH TEMPERED GLASS

- 1- ALL DOORS SHALL BE COMPLETE WITH 1-1/2 PAIR OF BRASS HINGES (3 PAIR HEAVY DUTY FOR DOUBLE DOORS) & APPROVED QUALITY LOCKS, CLOSERS, HANDLES, BOLTS AND DOOR STOPS AS NOTED.
- 2- CONTRACTOR SHALL SUBMIT SAMPLES OF ALL IRON MONGERY TO BE USED FOR CONSULTANTS APPROVAL PRIOR TO PLACING AN ORDER.
- 3- DOOR FRAME SHALL BE SECURED TO OPENINGS WITH MIN. 3 No.'s 10mm dia. & 4' LONG EXPANDING BOLTS.
- 4- ALL INSIDE FACES OF TIMBER FRAMES TO BE PAINTED WITH PRESERVATIVE PAINT OF APPROVED QUALITY.
- 5- ALL PANNELLED DOORS SHALL HAVE STILES, TOP RAIL & MIDDLE RAIL MIN. 4" WIDE. BOTTOM RAIL MIN. 8" WIDE. DECORATIVE PANELS AS/APPROVED DESIGN.
- 6- PROVIDE 3/4" x 9" or 5" MARINE PLYWOOD SUBFRAMES TO ALL DOOR OPENINGS.
- 7- ALL FLUSH DOORS TO BE 100% SOLID CORE OR 80% SEMI-SOLID CORE WITH HARDWOOD LIPPING ALL AROUND AS PER SPECIFICATIONS.
- 8- PROVIDE 2" x 9" or 2" x 5" DECORATIVE RED MERRANTINI WOOD FRAME ON BOTH SIDES.



- 1- CONTRACTOR SHALL SUBMIT ALL SAMPLES OF ALL ALUM. SECTIONS, GLAZING, LOCKS, HANDLES ETC., FOR APPROVAL OF CONSULTANT PRIOR TO PLACING AN ORDER.
- 2- ALL ALUMINUM OPENINGS TO HAVE .75" MARINE PLY SUB-FRAME OR TREATED RED MERANTI AS/ APPROVAL.
- 3- ALL ALUMINUM OPENINGS TO BE SEALED WITH 2 PARTS POLYSULPHIDE SEALANT MIN .25" THICK.
- 4- DRAINAGE WEEP HOLES TO BE PROVIDED AT THE BOTTOMS OF ALL ALUMINUM FRAMES AS PER APPROVAL.
- 5- ALL ALUMINUM DOORS AND WINDOW S SHALL BE COMPLETE WITH APPROPRIATE HANDLES, LOCKS, SLIDING GEAR ETC., WHICH SHALL BE OF APPROVED QUALITY AND DESIGN.
- 6- WHERE EVER MARINE PLY SUBFRAME IS EXPOSED PROVIDE 1/8"THICK RED MERANTI COVER SLIP (SCREWED) TO CONCEAL THE SAME/ EXPOSED SURFACES TO BE TREATED WITH APP. PRESERVATIVE PAINT.
- 7- ALL SILL HEIGHTS ARE FROM FINISH FLOOR LEVEL UNLESS NOTED OTHERWISE.
- 8- FLY MESH SCREENS TO BE FROM INSIDE UNLESS NOTED OTHERWISE

- 1- ALL DIMENSIONS SHOWN ON DRAWINGS ARE IN METRIC UNITS.
- 2- DRAWINGS ARE NOT TO BE SCALED. ONLY WRITTEN DIMENSIONS SHALL BE FOLLOWED.
- 3- ANY DISCREPANCIES, OMISSIONS OR CONFLICTS IN DRAWING DIMENSIONS SHALL BE RESOLVED AS TO BE BROUGHT TO THE ATTENTION OF (P.W.D.)ENGINEER FOR CORRECTION OR CLARIFICATION PRIOR TO COMMENCING WORKS. NO ACTIONS ARE TO BE TAKEN ON SITE UNTIL (P.W.D.) ENGINEER HAS RESOLVED ANY DISCREPANCIES OR CONFLICTS.
- 4- CONTRACTOR SHALL THOROUGHLY COORDINATE ARCHITECTURAL,STRUCTURAL,DRAINAGE AND A.C. DRAWINGS TO ENSURE NO CONFLICTS OR DISCREPANCIES. ALL DIMENSIONS SHALL BE CHECKED AND VERIFIED ON SITE PRIOR TO EXECUTION OF WORK.
- 5- THE MAIN CONTRACTOR SHALL BE RESPONSIBLE FOR THE CO-OPERATION AND QUALITY OF SUB-CONTRACTORS. ALL SUB-STANDARD WORK SHALL BE DEMOLISHED AND RE-BUILT TO ACCEPTABLE STANDARDS AS REQUIRED BY (P.W.D.) WITHOUT ANY EXTRA COST.
- 6- ALL JOINTS BETWEEN R.C. MEMBERS AND BLOCK WORK SHALL BE WITH 10mm (3/8") GALVANIZED WIRE, EXPANDED MESH (EXPAMET) BEFORE COVERING BY PLASTER.

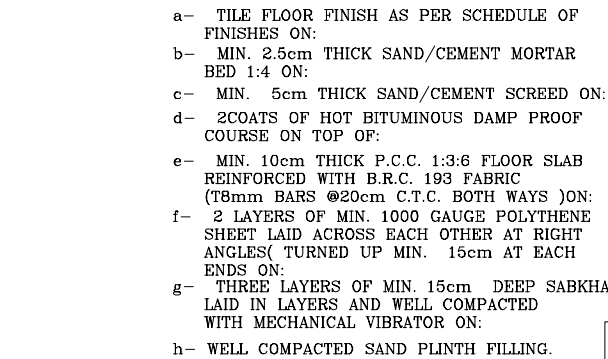


HEAT INSULATION

ROOF CALCULATION		
U VALUE (R = IN SQ'F h/BTU)		
1" TERRAZZO	R = 0.08	
2" DRY CEMENT, SAND	R = 0.4	
2" POLYSTYRENE (35 KG/CU.M)	R = 9.47	
0.16" ASPHALT ROLL ROOFING	R = 0.024	
2" LIGHT WEIGHT CONCRETE	R = 1.54	
8" HEAVY WEIGHT CONCRETE	R = 0.59	
TOTAL(R)= 12.104 SQ.FT h/BTU		
u=1/R	OR	u = 0.08 BTU/SQ.FT h
* POLYSTYRENE FOR HEAT INSULATION OR ANY EQUIVALENT MATERIAL AS PER ENGINEER APPROVAL.		

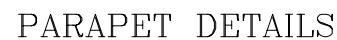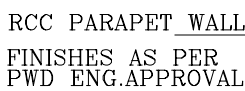

THE CONSTRUCTION OF ANY MULTI STORY BUILDINGS OR VILLAS STOP THE FIRST SLAB LEVEL MUST HAVE TO PROVIDE 10CM THICK RCC PARAPET WALL FOR FUTURE CONSTRUCTION AS PER DETAIL

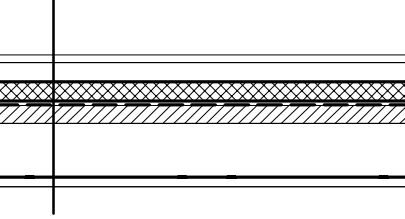

1. IT IS NOT ALLOWED TO REPRODUCE THE SHEETS CONTENTS IN ANY FORM EXCEPT FOR THE PURPOSE FOR WHICH IT IS INTENDED.
2. THESE DRAWINGS ARE DIAGRAMMATIC AND SHALL NOT BE SCALED. ADDITIONAL DATA SHALL BE REQUESTED FROM THE CONSULTANCY THROUGH WRITTEN CLARIFICATION. VERIFY ALL EXISTING CONDITIONS AND DIMENSIONS BEFORE PROCEEDING WITH ANY PORTION OF ANY WORK.
3. NO CHANGES, MODIFICATIONS OR DEVIATIONS SHALL BE WRITTEN PERMISSION FROM **ALMASAH ENGINEERING CONSULTANTS**.
4. ALL WORK AS OUTLINED IN THESE DOCUMENTS, SHALL STRICTLY CONFORM TO ALL APPLICABLE CODES. IN THE EVENT OF A CONFLICT, THE MORE STRINGENT REQUIREMENT SHALL GOVERN AND BE MET.

SIA - SM-02



حُكُومَةُ الشَّارِقَةِ
دائرة الشؤون الإسلامية

CONSULTANT STAMP



CLIENT:

GOVERNMENT OF SHARJAH -
DEPARTMENT OF ISLAMIC AFFAIRS

PROJECT:

(SIA - SM-02)
PROPOSED MASJID + ABLUTION +
IMAM HOUSE

SHEET TITLE:

ARCHITECTURE DETAILS

ARCHITECT Arch. Mostafa Ramadan		TYPE	ARCHITECTURE
STRUCTURAL Eng : Mohamed Gomaa		SHEET No.	A - 19
CHECKED BY Eng : Mohamed Attia		Location :	
		Plot No :	
SCALE 1:100	DATE March - 2022	Project No.	