




SIA - SM-01

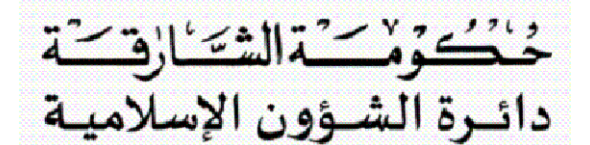


PROJECT: (SIA - SM-01)
PROPOSED MASJID + ABLUTION +
IMAM HOUSE

SHEET TITLE: **SETTING OUT PLAN**

ARCHITECT Arch. Mostafa Ramadan		TYPE	ARCHITECTURE
STRUCTURAL Eng : Mohamed Gomaa		SHEET No.	A - 01
CHECKED BY Eng : Mohamed Attia		Location :	
		Plot No :	
SCALE 1:100	DATE May - 2022	Project No.	



ARCHITECT Arch. Mostafa Ramadan		TYPE	ARCHITECTURE
STRUCTURAL Eng : Mohamed Gomaa		SHEET No.	A - 02
CHECKED BY Eng : Mohamed Attia		Location :	
		Plot No :	
SCALE 1:100	DATE May - 2022	Project No.	

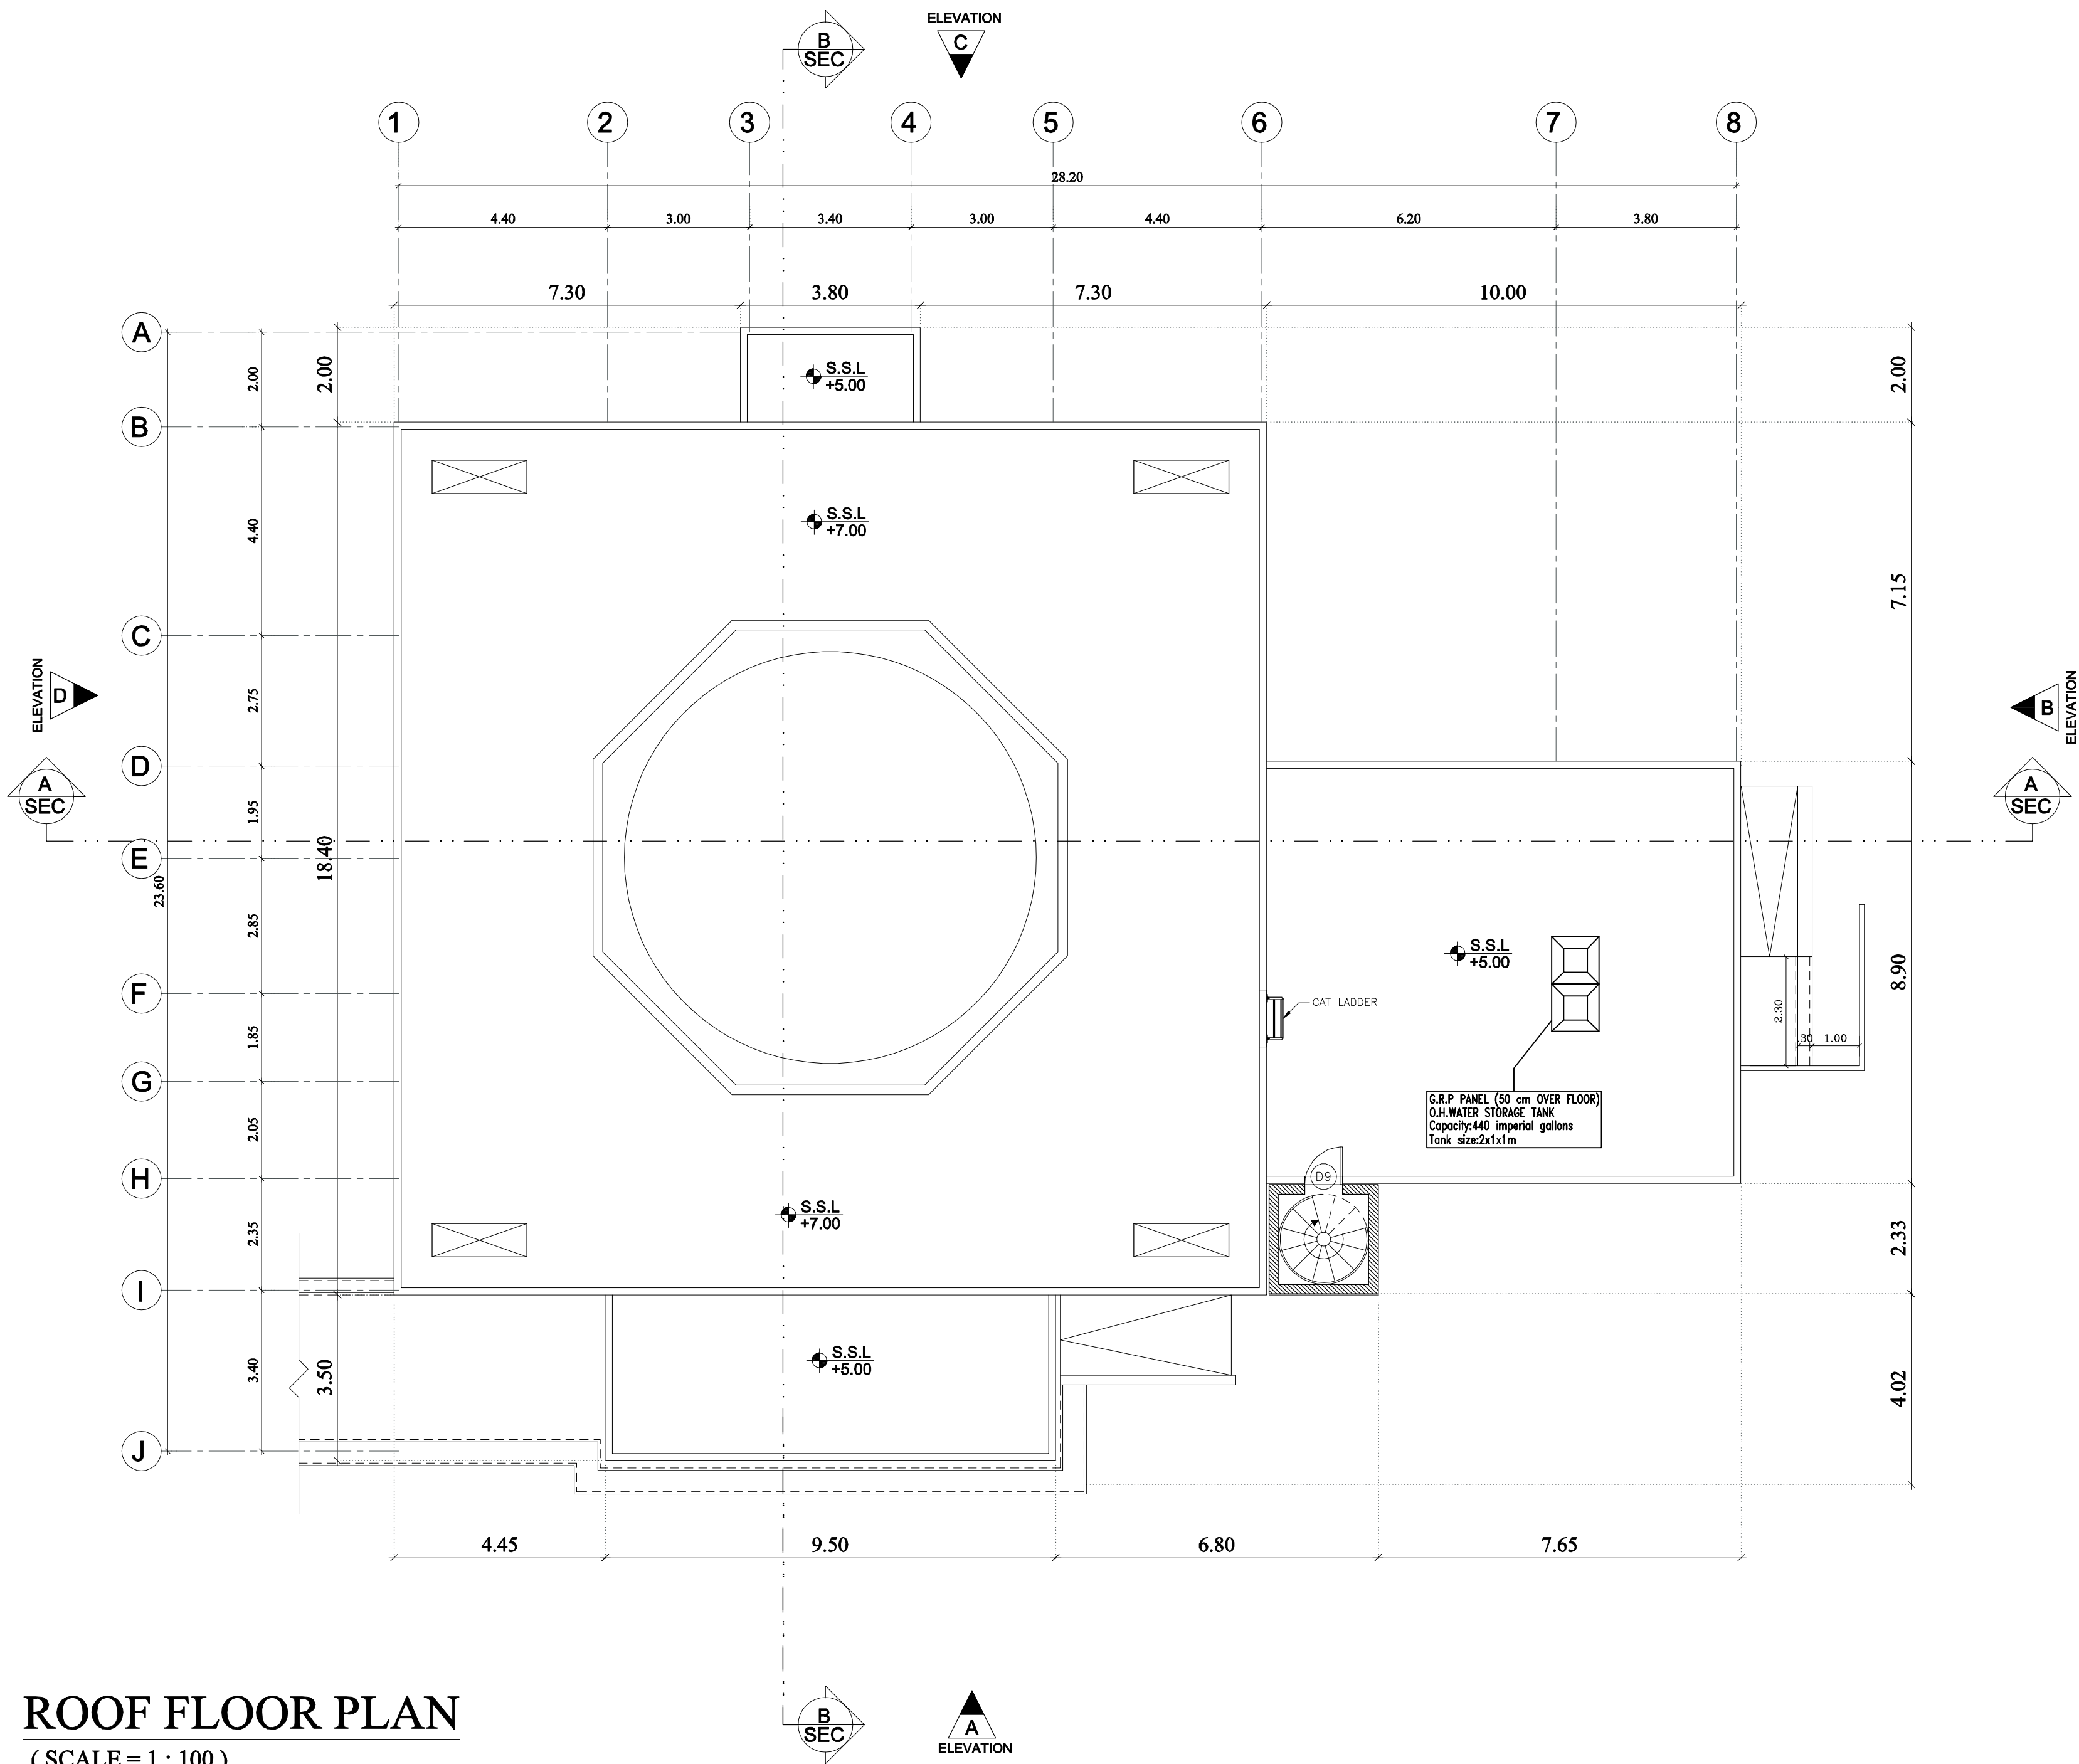

ROOF FLOOR PLAN
(SCALE = 1 : 100)

- GENERAL NOTES:**
1. IT IS NOT ALLOWED TO REPRODUCE THE SHEETS CONTENTS IN ANY FORM EXCEPT FOR THE PURPOSE FOR WHICH IT IS INTENDED.
 2. THESE DRAWINGS ARE DIAGRAMMATIC AND SHALL NOT BE SCALED. ADDITIONAL DATA SHALL BE REQUESTED FROM THE CONSULTANCY THROUGH WRITTEN CLARIFICATION. VERIFY ALL EXISTING CONDITIONS AND DIMENSIONS BEFORE PROCEEDING WITH ANY PORTION OF ANY WORK.
 3. NO CHANGES, MODIFICATIONS OR DEVIATIONS SHALL BE WRITTEN PERMISSION FROM **ALMASAH ENGINEERING CONSULTANTS**.
 4. ALL WORK AS OUTLINED IN THESE DOCUMENTS, SHALL STRICTLY CONFORM TO ALL APPLICABLE CODES. IN THE EVENT OF A CONFLICT, THE MORE STRINGENT REQUIREMENT SHALL GOVERN AND BE MET.



SIA - SM-01




حُكُومَةُ الشَّارِجَةِ
دائرة الشؤون الإسلامية

CONSULTANT STAMP



CLIENT: GOVERNMENT OF SHARJAH - DEPARTMENT OF ISLAMIC AFFAIRS			
PROJECT: (SIA - SM-01) PROPOSED MASJID + ABLUTION + IMAM HOUSE			
SHEET TITLE: ROOF FLOOR PLAN			
ARCHITECT Arch. Mostafa Ramadan	TYPE	ARCHITECTURE	
STRUCTURAL Eng : Mohamed Goma	SHEET No.	A - 03	
CHECKED BY Eng : Mohamed Attia	Location :		
SCALE 1:100	DATE May - 2022	Project No.	

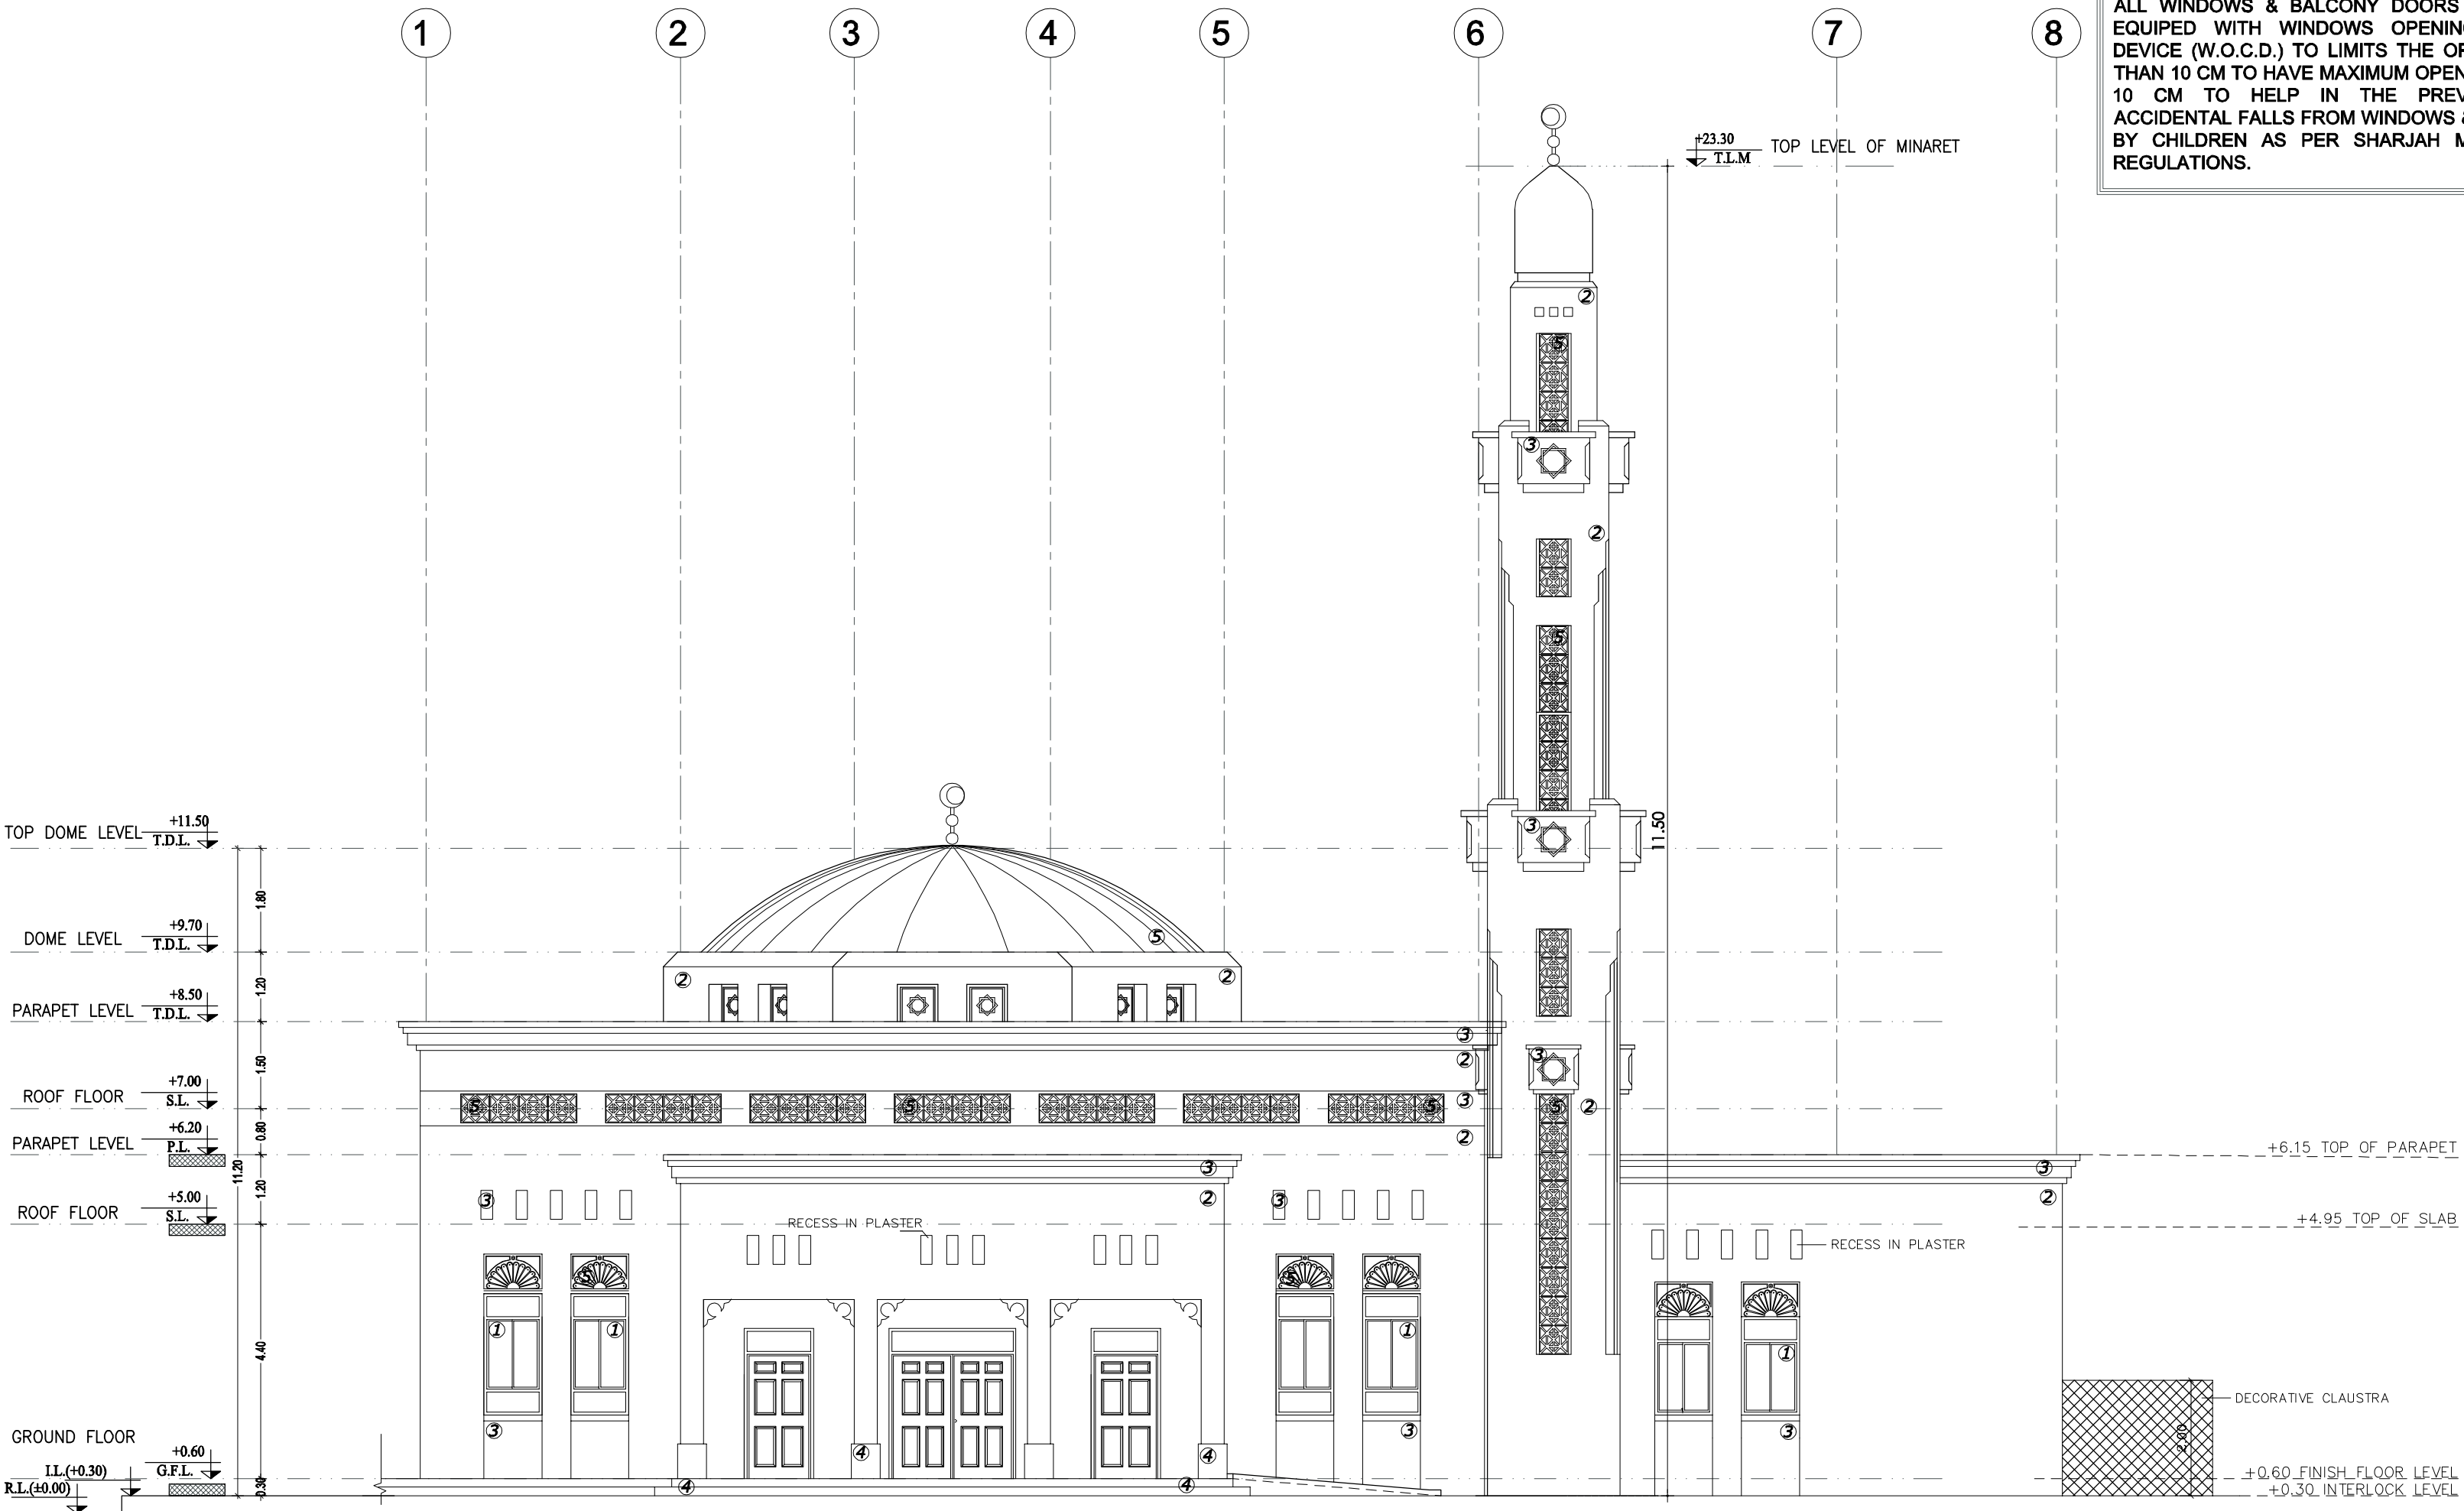

ELEVATION -A
(SCALE = 1 : 100)

ELEVATION FINISHES

- 1- REFLECTIVE GLASS
- 2- GRAFFIO DECOR WHITE PAINT OR STONE CLADDING
- 3- GRAFFIO DECOR OFF WHITE PAINT OR STONE CLADDING
- 4- GRANITE FINISHING
- 5- G.R.C.

ALL WINDOWS & BALCONY DOORS SHOULD BE EQUIPED WITH WINDOWS OPENING CONTROL DEVICE (W.O.C.D.) TO LIMITS THE OPENING LESS THAN 10 CM TO HAVE MAXIMUM OPENING LIMIT OF 10 CM TO HELP IN THE PREVENTION OF ACCIDENTAL FALLS FROM WINDOWS & BALCONIES BY CHILDREN AS PER SHARJAH MUNICIPALITY REGULATIONS.

GENERAL NOTES:

- 1.IT IS NOT ALLOWED TO REPRODUCE THE SHEETS CONTENTS IN ANY FORM EXCEPT FOR THE PURPOSE FOR WHICH IT IS INTENDED.
2. THESE DRAWINGS ARE DIAGRAMMATIC AND SHALL NOT BE SCALED. ADDITIONAL DATA SHALL BE REQUESTED FROM THE CONSULTANCY THROUGH WRITTEN CLARIFICATION. VERIFY ALL EXISTING CONDITIONS AND DIMENSIONS BEFORE PROCEEDING WITH ANY PORTION OF ANY WORK.
3. NO CHANGES, MODIFICATIONS OR DEVIATIONS SHALL BE WRITTEN PERMISSION FROM **ALMASAH ENGINEERING CONSULTANTS**.
4. ALL WORK AS OUTLINED IN THESE DOCUMENTS, SHALL STRICTLY CONFORM TO ALL APPLICABLE CODES. IN THE EVENT OF A CONFLICT, THE MORE STRINGENT REQUIREMENT SHALL GOVERN AND BE MET.



SIA - SM-01



حكومة الشارقة
دائرة الشؤون الإسلامية

CONSULTANT STAMP



CLIENT:

GOVERNMENT OF SHARJAH -
DEPARTMENT OF ISLAMIC AFFAIRS

PROJECT:

(SIA - SM-01)
PROPOSED MASJID + ABLUTION +
IMAM HOUSE

SHEET TITLE:

ELEVATION -A

ARCHITECT

Arch. Mostafa Ramadan

TYPE

ARCHITECTURE

STRUCTURAL

Eng : Mohamed Gomaa

SHEET

No.

A - 04

CHECKED BY

Eng : Mohamed Attia

Location :

Plot No :

SCALE

1:100

DATE


May - 2022

Project

No.

ELEVATION - B

(SCALE = 1 : 100)

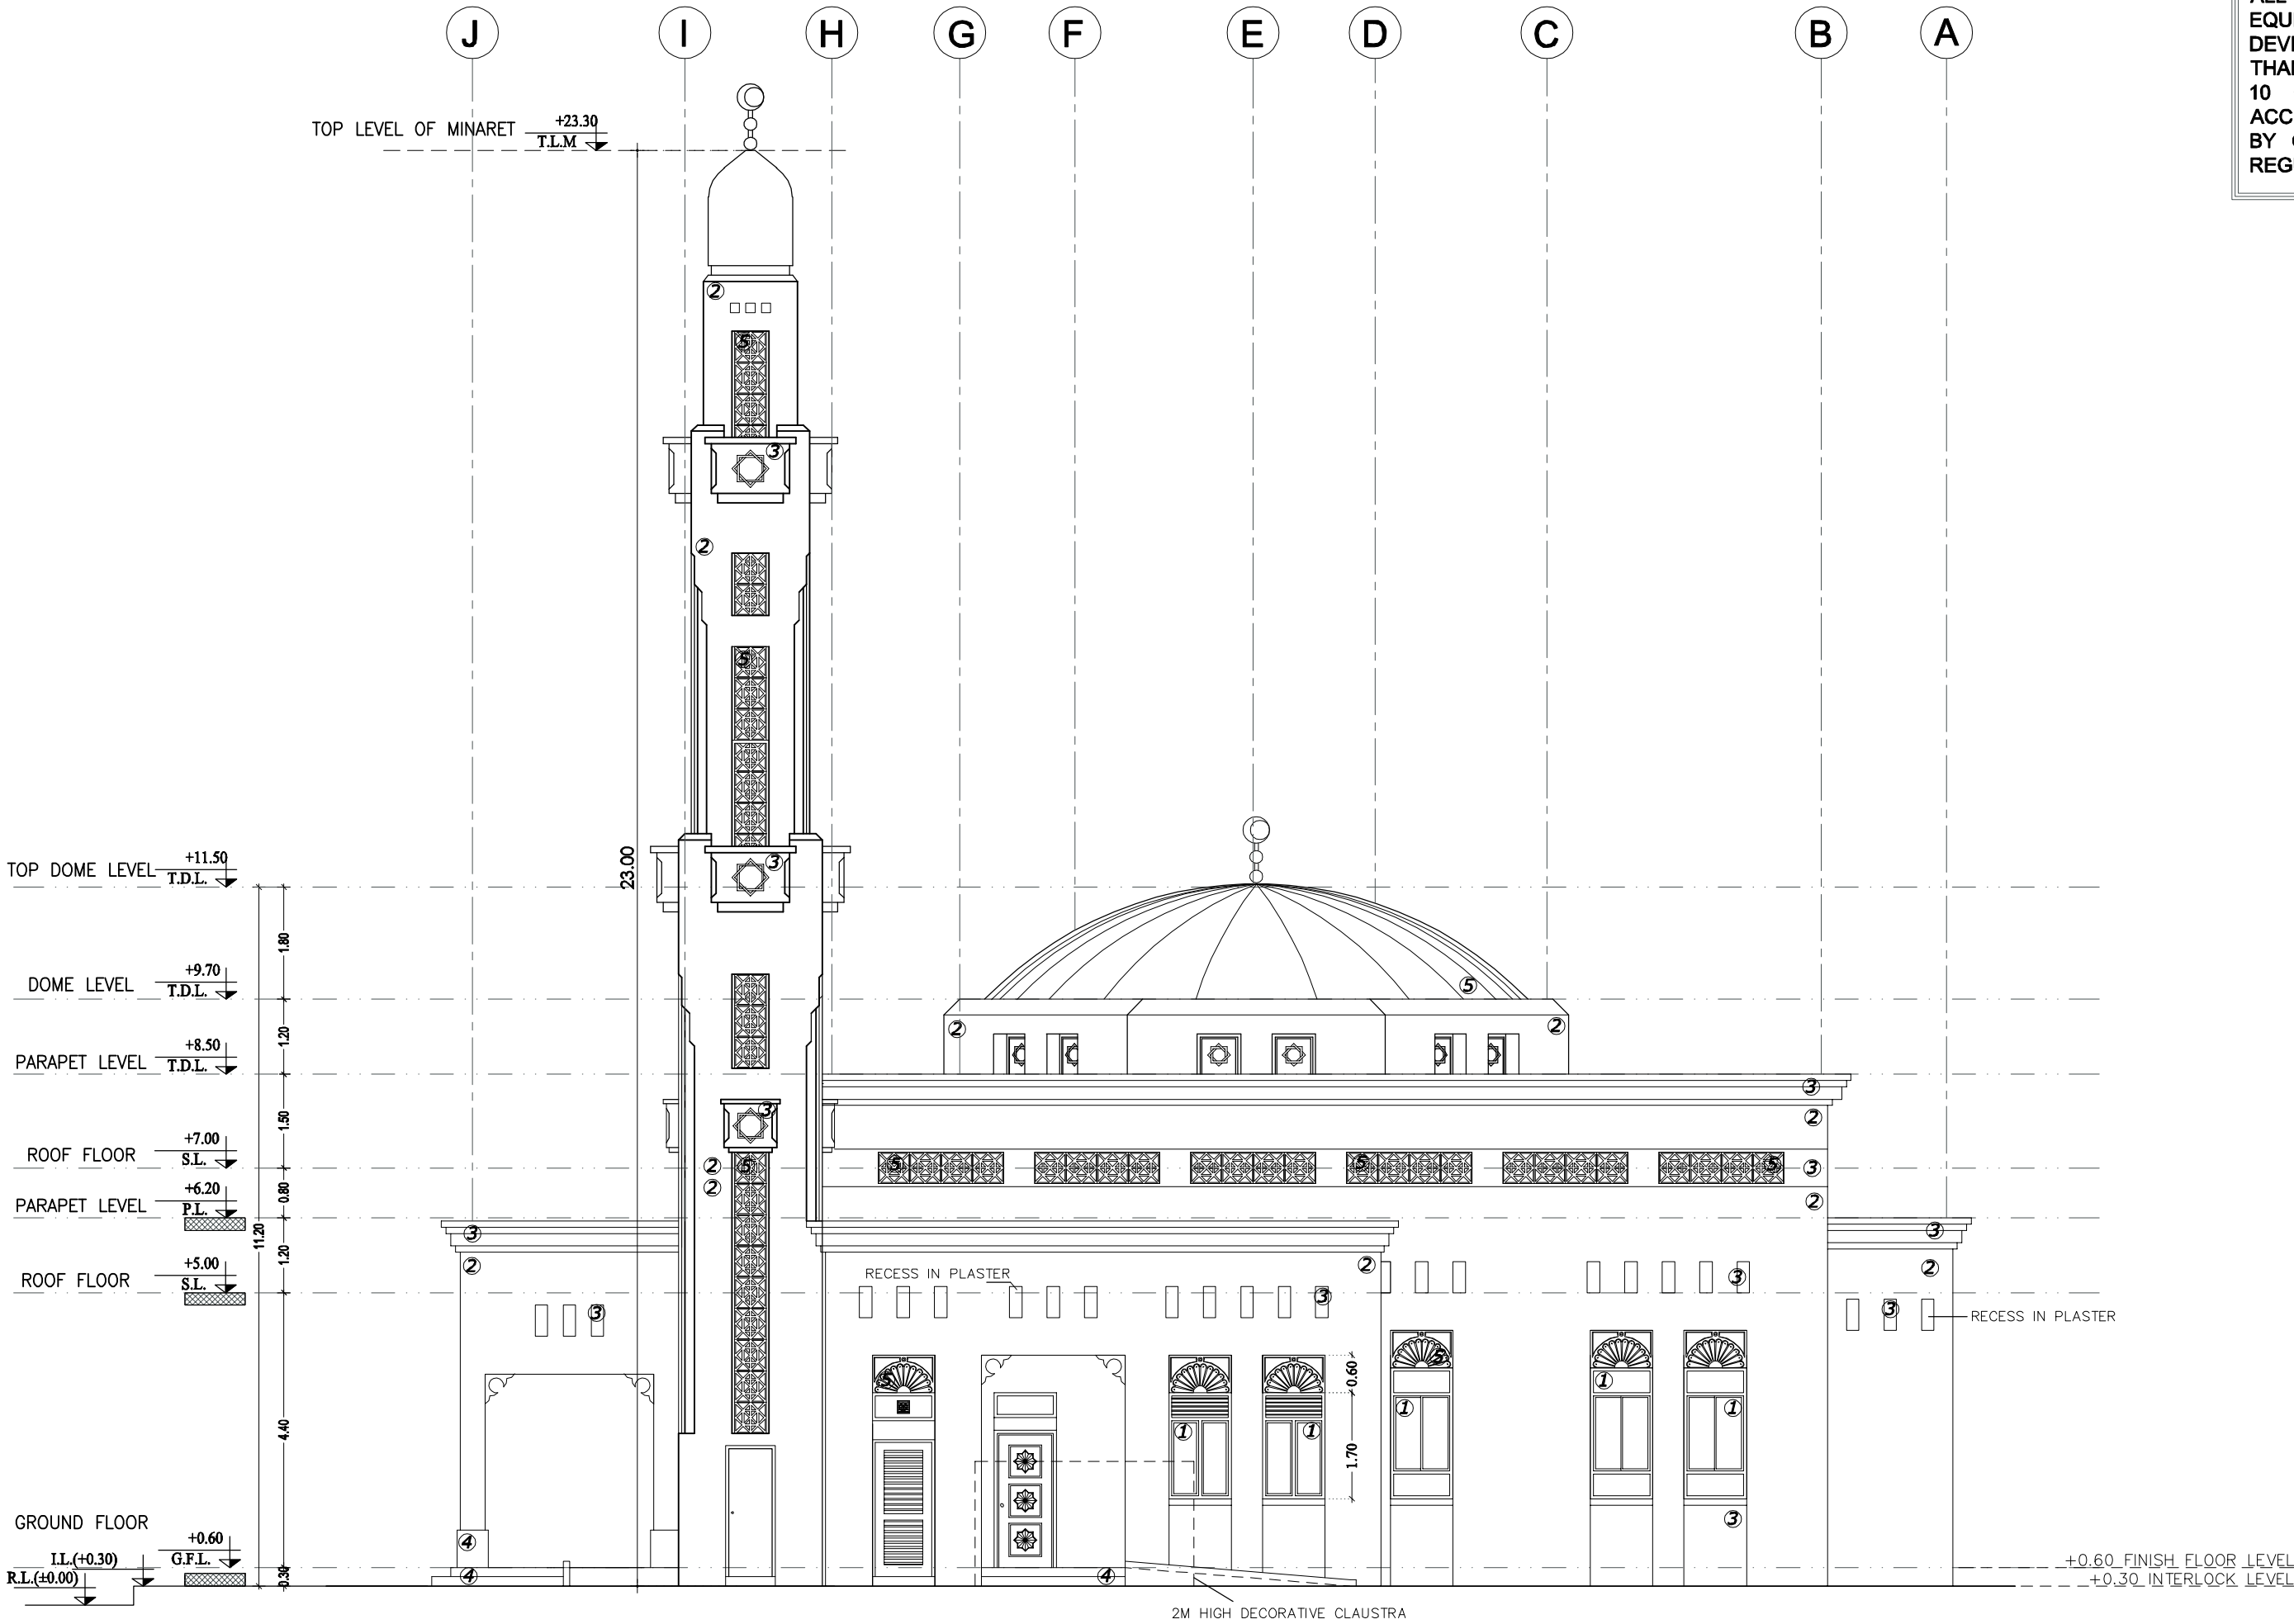

ELEVATION FINISHES

- 1- REFLECTIVE GLASS
- 2- GRAFFIO DECOR WHITE PAINT OR STONE CLADDING
- 3- GRAFFIO DECOR OFF WHITE PAINT OR STONE CLADDING
- 4- GRANITE FINISHING
- 5- G.R.C.

ALL WINDOWS & BALCONY DOORS SHOULD BE EQUIPED WITH WINDOWS OPENING CONTROL DEVICE (W.O.C.D.) TO LIMITS THE OPENING LESS THAN 10 CM TO HAVE MAXIMUM OPENING LIMIT OF 10 CM TO HELP IN THE PREVENTION OF ACCIDENTAL FALLS FROM WINDOWS & BALCONIES BY CHILDREN AS PER SHARJAH MUNICIPALITY REGULATIONS.

GENERAL NOTES:

1. IT IS NOT ALLOWED TO REPRODUCE THE SHEETS CONTENTS IN ANY FORM EXCEPT FOR THE PURPOSE FOR WHICH IT IS INTENDED.
2. THESE DRAWINGS ARE DIAGRAMMATIC AND SHALL NOT BE SCALED. ADDITIONAL DATA SHALL BE REQUESTED FROM THE CONSULTANCY THROUGH WRITTEN CLARIFICATION. VERIFY ALL EXISTING CONDITIONS AND DIMENSIONS BEFORE PROCEEDING WITH ANY PORTION OF ANY WORK.
3. NO CHANGES, MODIFICATIONS OR DEVIATIONS SHALL BE WRITTEN PERMISSION FROM **ALMASAH ENGINEERING CONSULTANTS**.
4. ALL WORK AS OUTLINED IN THESE DOCUMENTS, SHALL STRICTLY CONFORM TO ALL APPLICABLE CODES. IN THE EVENT OF A CONFLICT, THE MORE STRINGENT REQUIREMENT SHALL GOVERN AND BE MET.



SIA - SM-01



حُكُومَةُ الشَّارِقَةِ
دائرة الشؤون الإسلامية

CONSULTANT STAMP



CLIENT: GOVERNMENT OF SHARJAH - DEPARTMENT OF ISLAMIC AFFAIRS


PROJECT: (SIA - SM-01) PROPOSED MASJID + ABLUTION + IMAM HOUSE

SHEET TITLE: ELEVATION -B

ARCHITECT Arch. Mostafa Ramadan	TYPE ARCHITECTURE
STRUCTURAL Eng : Mohamed Gomaa	SHEET No. A - 05
CHECKED BY Eng : Mohamed Attia	Location : Plot No :
SCALE 1:100	DATE May - 2022
Project No.	

ELEVATION - C

(SCALE = 1 : 100)

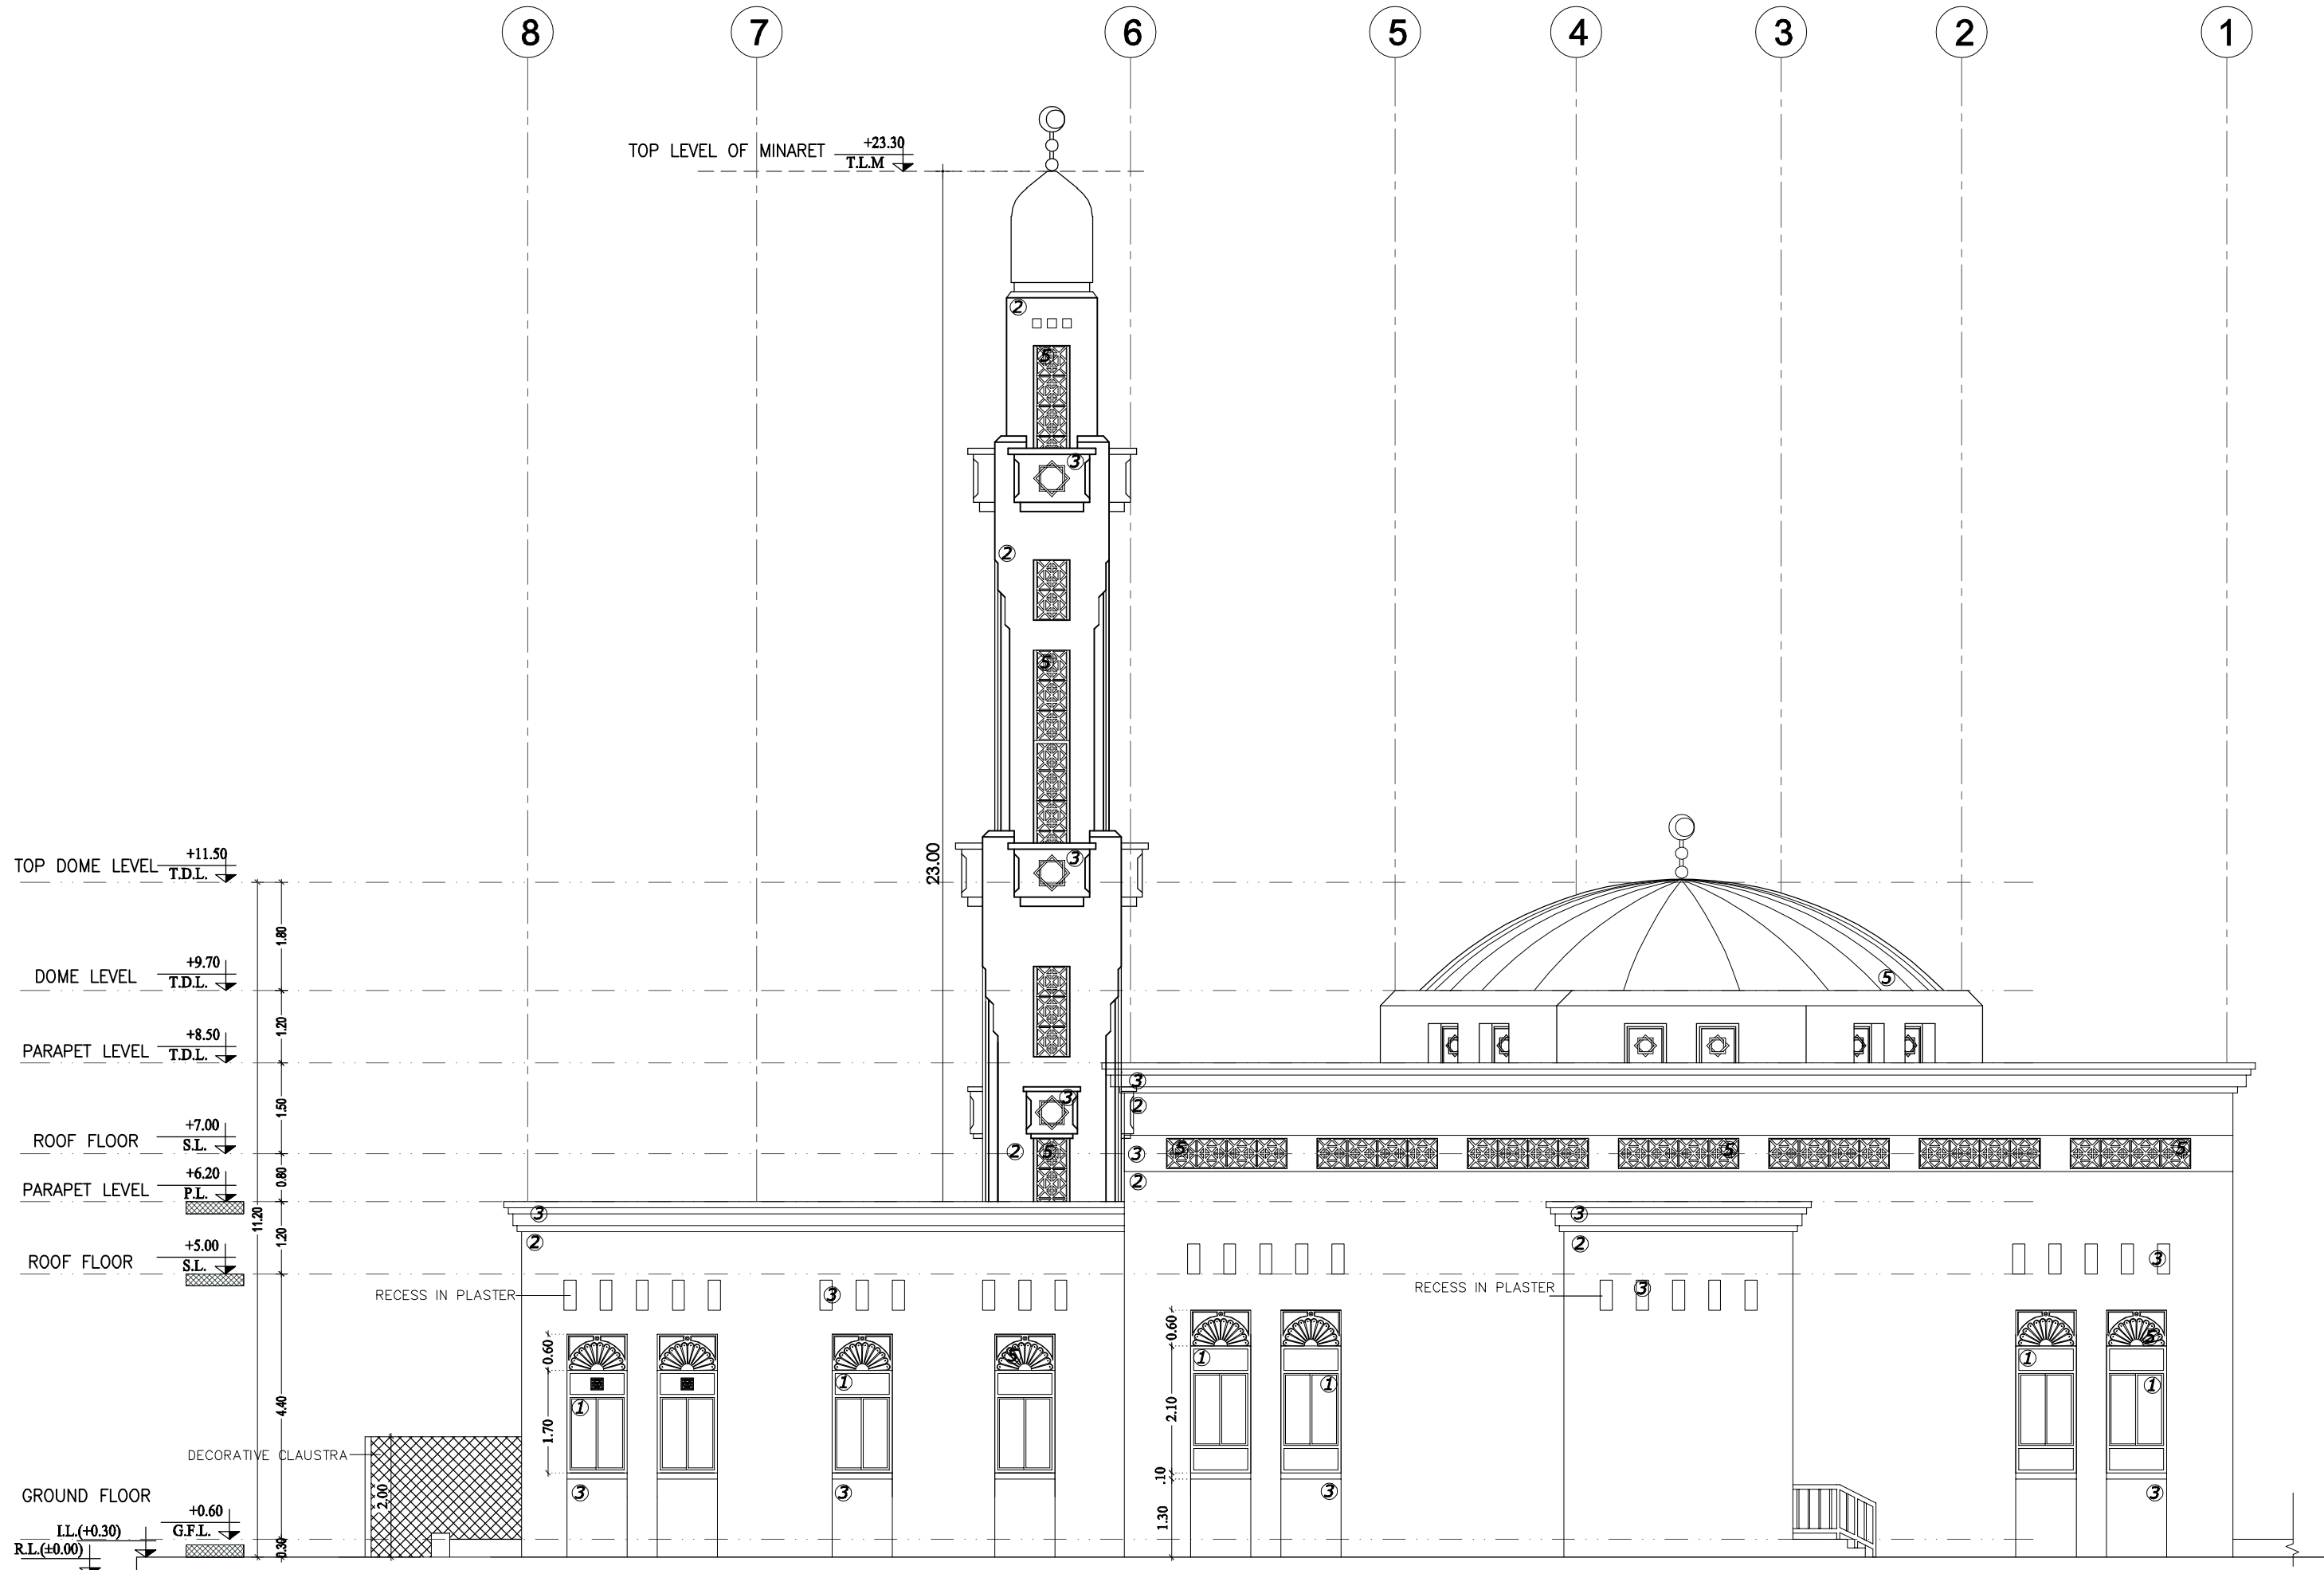

ELEVATION FINISHES

- 1- REFLECTIVE GLASS
- 2- GRAFFIO DECOR WHITE PAINT OR STONE CLADDING
- 3- GRAFFIO DECOR OFF WHITE PAINT OR STONE CLADDING
- 4- GRANITE FINISHING
- 5- G.R.C.

ALL WINDOWS & BALCONY DOORS SHOULD BE EQUIPED WITH WINDOWS OPENING CONTROL DEVICE (W.O.C.D.) TO LIMITS THE OPENING LESS THAN 10 CM TO HAVE MAXIMUM OPENING LIMIT OF 10 CM TO HELP IN THE PREVENTION OF ACCIDENTAL FALLS FROM WINDOWS & BALCONIES BY CHILDREN AS PER SHARJAH MUNICIPALITY REGULATIONS.

GENERAL NOTES:

- 1.IT IS NOT ALLOWED TO REPRODUCE THE SHEETS CONTENTS IN ANY FORM EXCEPT FOR THE PURPOSE FOR WHICH IT IS INTENDED.
2. THESE DRAWINGS ARE DIAGRAMMATIC AND SHALL NOT BE SCALED. ADDITIONAL DATA SHALL BE REQUESTED FROM THE CONSULTANCY THROUGH WRITTEN CLARIFICATION. VERIFY ALL EXISTING CONDITIONS AND DIMENSIONS BEFORE PROCEEDING WITH ANY PORTION OF ANY WORK.
3. NO CHANGES, MODIFICATIONS OR DEVIATIONS SHALL BE WRITTEN PERMISSION FROM **ALMASAH ENGINEERING CONSULTANTS**.
4. ALL WORK AS OUTLINED IN THESE DOCUMENTS, SHALL STRICTLY CONFORM TO ALL APPLICABLE CODES. IN THE EVENT OF A CONFLICT, THE MORE STRINGENT REQUIREMENT SHALL GOVERN AND BE MET.




SIA - SM-01



حكومة الشارقة
دائرة الشؤون الإسلامية

CONSULTANT STAMP

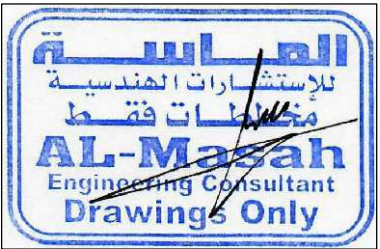

CLIENT: **GOVERNMENT OF SHARJAH -
DEPARTMENT OF ISLAMIC AFFAIRS**


PROJECT: **(SIA - SM-01)
PROPOSED MASJID + ABLUTION +
IMAM HOUSE**

SHEET TITLE: **ELEVATION - C**

ARCHITECT Arch. Mostafa Ramadan	TYPE ARCHITECTURE
STRUCTURAL Eng : Mohamed Gomaa	SHEET No. A - 06
CHECKED BY Eng : Mohamed Attia	Location : Plot No :
SCALE 1:100	DATE May - 2022
	Project No.

SECTION D

(SCALE = 1 : 100)

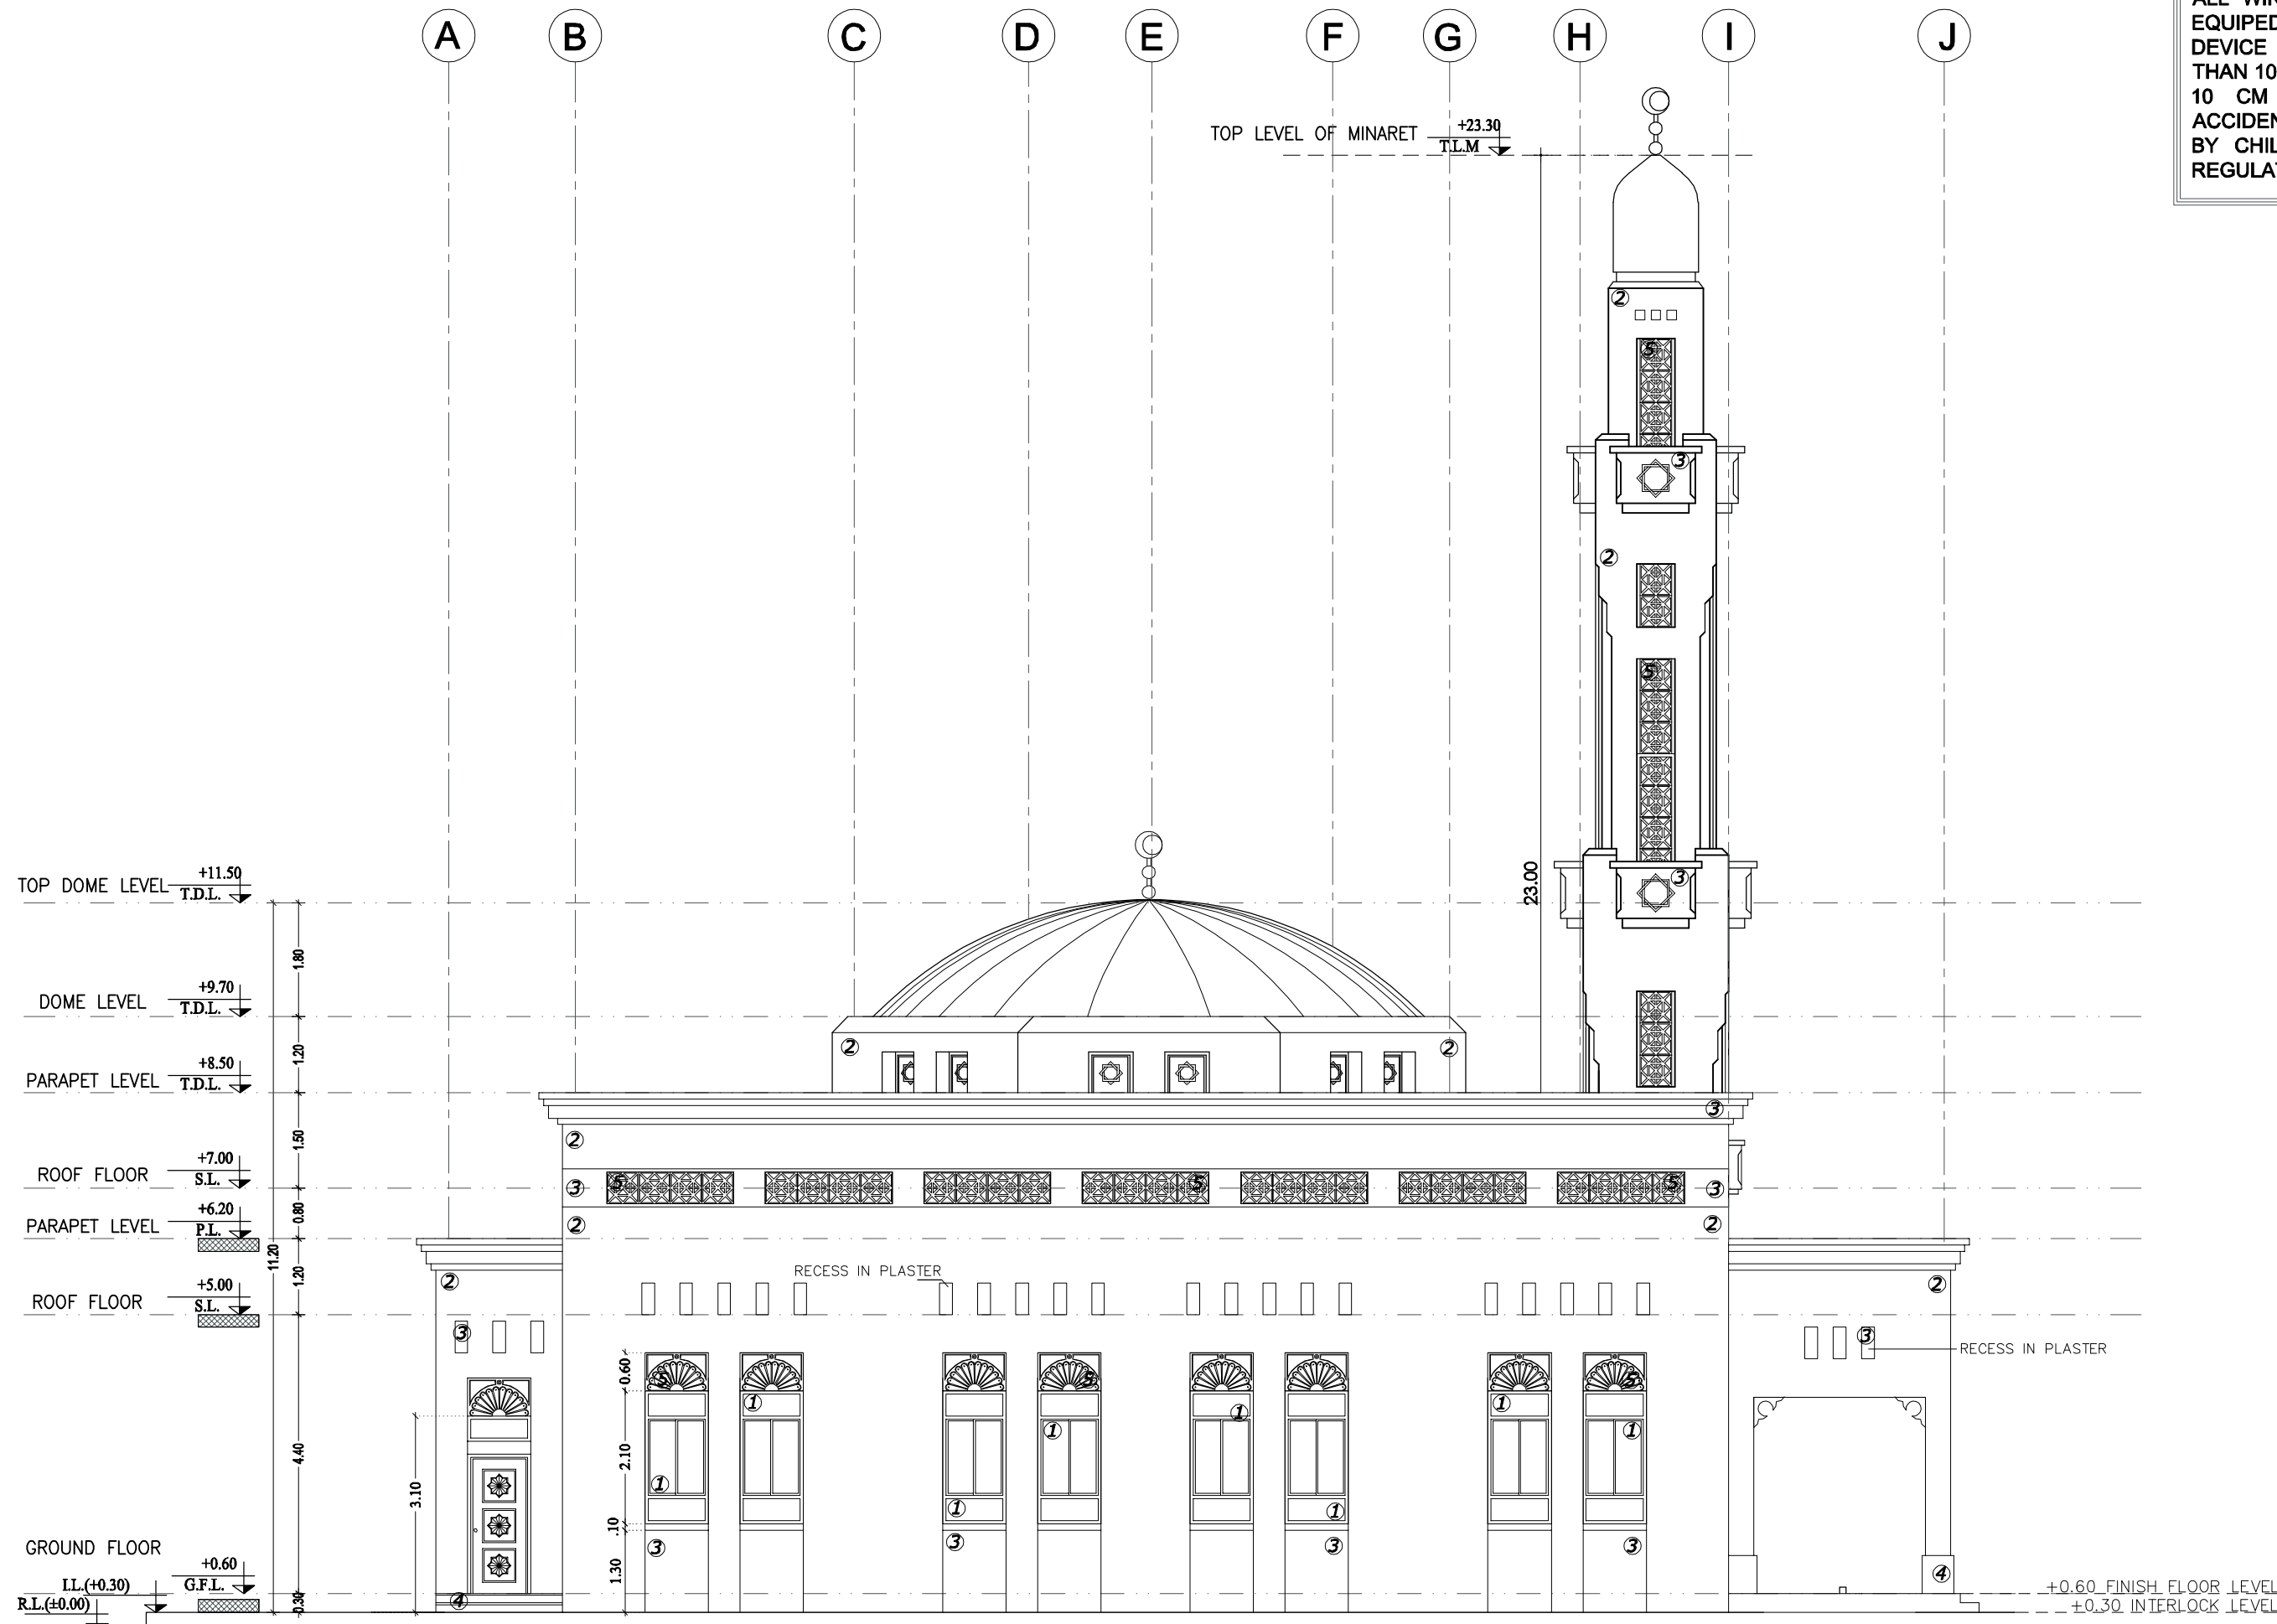

ELEVATION FINISHES

- 1- REFLECTIVE GLASS
- 2- GRAFFIO DECOR WHITE PAINT OR STONE CLADDING
- 3- GRAFFIO DECOR OFF WHITE PAINT OR STONE CLADDING
- 4- GRANITE FINISHING
- 5- G.R.C.

ALL WINDOWS & BALCONY DOORS SHOULD BE EQUIPED WITH WINDOWS OPENING CONTROL DEVICE (W.O.C.D.) TO LIMITS THE OPENING LESS THAN 10 CM TO HAVE MAXIMUM OPENING LIMIT OF 10 CM TO HELP IN THE PREVENTION OF ACCIDENTAL FALLS FROM WINDOWS & BALCONIES BY CHILDREN AS PER SHARJAH MUNICIPALITY REGULATIONS.

GENERAL NOTES:

- 1.IT IS NOT ALLOWED TO REPRODUCE THE SHEETS CONTENTS IN ANY FORM EXCEPT FOR THE PURPOSE FOR WHICH IT IS INTENDED.
2. THESE DRAWINGS ARE DIAGRAMMATIC AND SHALL NOT BE SCALED. ADDITIONAL DATA SHALL BE REQUESTED FROM THE CONSULTANCY THROUGH WRITTEN CLARIFICATION. VERIFY ALL EXISTING CONDITIONS AND DIMENSIONS BEFORE PROCEEDING WITH ANY PORTION OF ANY WORK.
3. NO CHANGES, MODIFICATIONS OR DEVIATIONS SHALL BE WRITTEN PERMISSION FROM **ALMASAH ENGINEERING CONSULTANTS**.
4. ALL WORK AS OUTLINED IN THESE DOCUMENTS, SHALL STRICTLY CONFORM TO ALL APPLICABLE CODES. IN THE EVENT OF A CONFLICT, THE MORE STRINGENT REQUIREMENT SHALL GOVERN AND BE MET.



SIA - SM-01



حكومة الشارقة
دائرة الشؤون الإسلامية

CONSULTANT STAMP



CLIENT:

GOVERNMENT OF SHARJAH -
DEPARTMENT OF ISLAMIC AFFAIRS


PROJECT:

(SIA - SM-01)
PROPOSED MASJID + ABLUTION +
IMAM HOUSE

SHEET TITLE:


ELEVATION -D

ARCHITECT Arch. Mostafa Ramadan	TYPE ARCHITECTURE	
STRUCTURAL Eng : Mohamed Gomaa	SHEET No.	A - 07
CHECKED BY Eng : Mohamed Attia	Location :	
SCALE 1:100	DATE May - 2022	Plot No :
	Project No.	

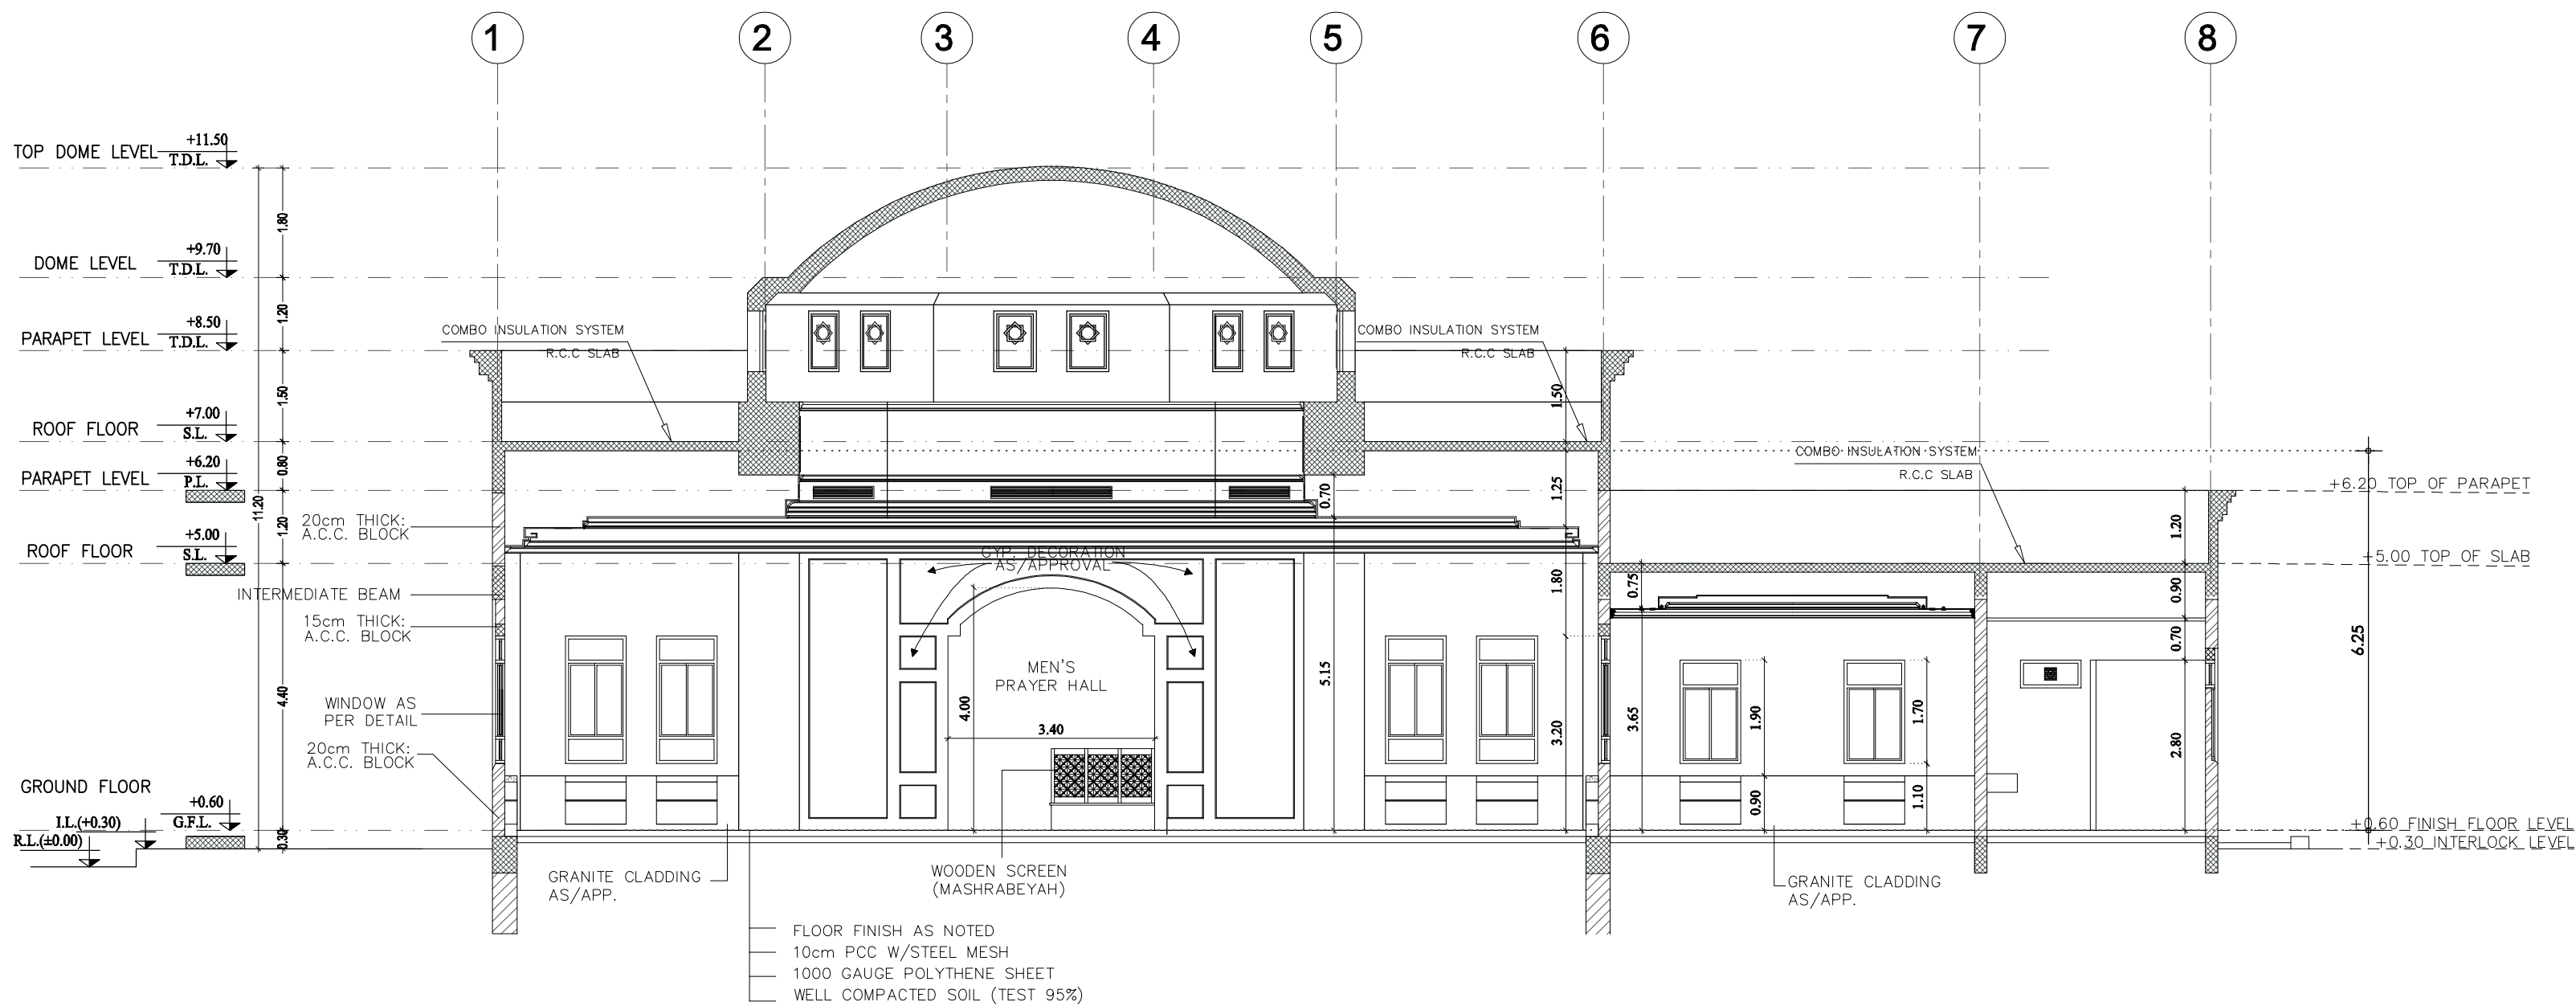


SECTION A-A
(SCALE = 1 : 100)

- * NOTES :.
- 1- ALL EXTERNAL WALLS TO BE 20.cm THERMAL BLOCK.
 - 2- WINDOWS TO BE DOUBLE REFLECTIVE GLASS

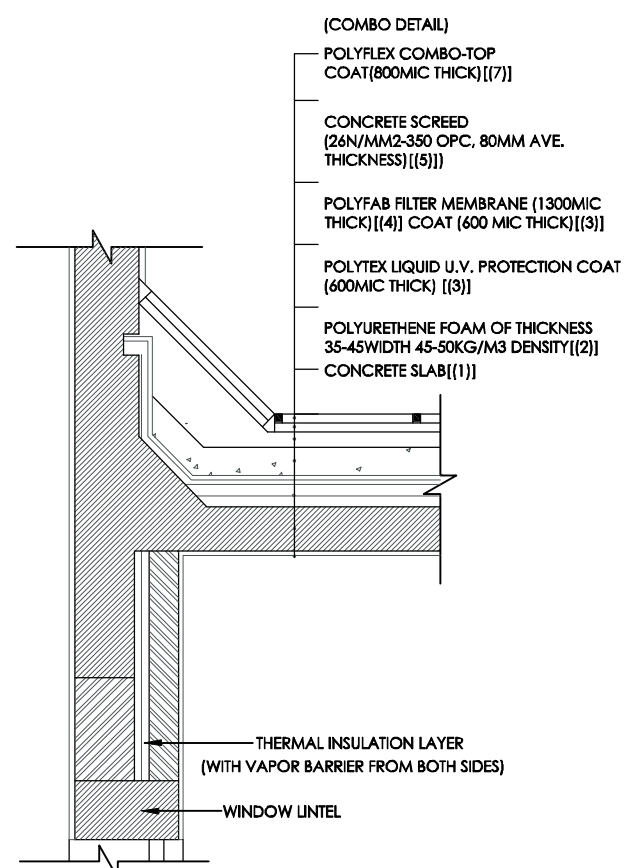

DETAIL 1
(SCALE = 1 : 25)

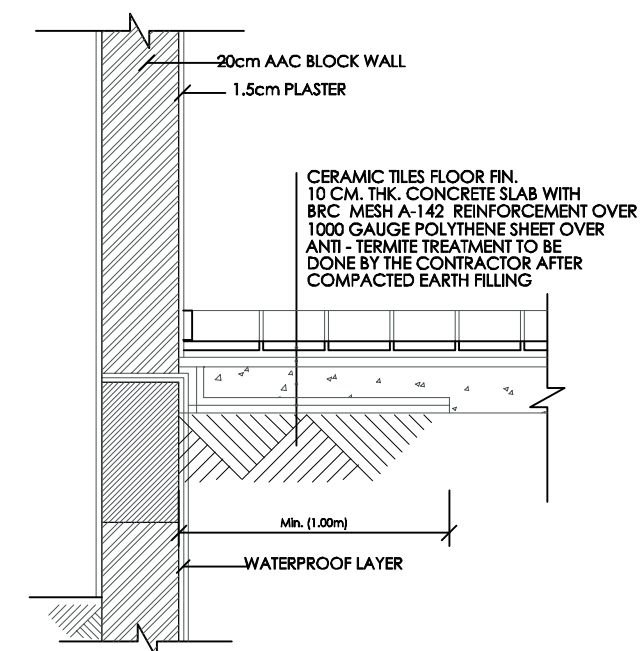

DETAIL 2
(SCALE = 1 : 25)

GENERAL NOTES:

1. IT IS NOT ALLOWED TO REPRODUCE THE SHEETS CONTENTS IN ANY FORM EXCEPT FOR THE PURPOSE FOR WHICH IT IS INTENDED.
2. THESE DRAWINGS ARE DIAGRAMMATIC AND SHALL NOT BE SCALED. ADDITIONAL DATA SHALL BE REQUESTED FROM THE CONSULTANCY THROUGH WRITTEN CLARIFICATION. VERIFY ALL EXISTING CONDITIONS AND DIMENSIONS BEFORE PROCEEDING WITH ANY PORTION OF ANY WORK.
3. NO CHANGES, MODIFICATIONS OR DEVIATIONS SHALL BE WRITTEN PERMISSION FROM **ALMASAH ENGINEERING CONSULTANTS**.
4. ALL WORK AS OUTLINED IN THESE DOCUMENTS, SHALL STRICTLY CONFORM TO ALL APPLICABLE CODES. IN THE EVENT OF A CONFLICT, THE MORE STRINGENT REQUIREMENT SHALL GOVERN AND BE MET.



SIA - SM-01



حكومة الشارقة
دائرة الشؤون الإسلامية

CONSULTANT STAMP



CLIENT:

GOVERNMENT OF SHARJAH -
DEPARTMENT OF ISLAMIC AFFAIRS


PROJECT:

(SIA - SM-01)
PROPOSED MASJID + ABLUTION +
IMAM HOUSE

SHEET TITLE:


SECTIONS

ARCHITECT Arch. Mostafa Ramadan	TYPE ARCHITECTURE
STRUCTURAL Eng : Mohamed Gomaa	SHEET No. A - 08
CHECKED BY Eng : Mohamed Attia	Location : Plot No :
SCALE 1:100	DATE May - 2022
	Project No.

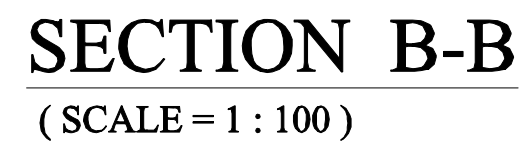


1- ALL EXTERNAL WALLS TO BE 20.cm THERMAL BLOCK.
2- WINDOWS TO BE DOUBLE REFLECTIVE GLASS

ARCHITECT Arch. Mostafa Ramadan		TYPE	ARCHITECTURE
STRUCTURAL Eng : Mohamed Gomaa		SHEET No.	A - 09
CHECKED BY Eng : Mohamed Attia		Location :	
		Plot No :	
SCALE 1:100	DATE May - 2022	Project No.	

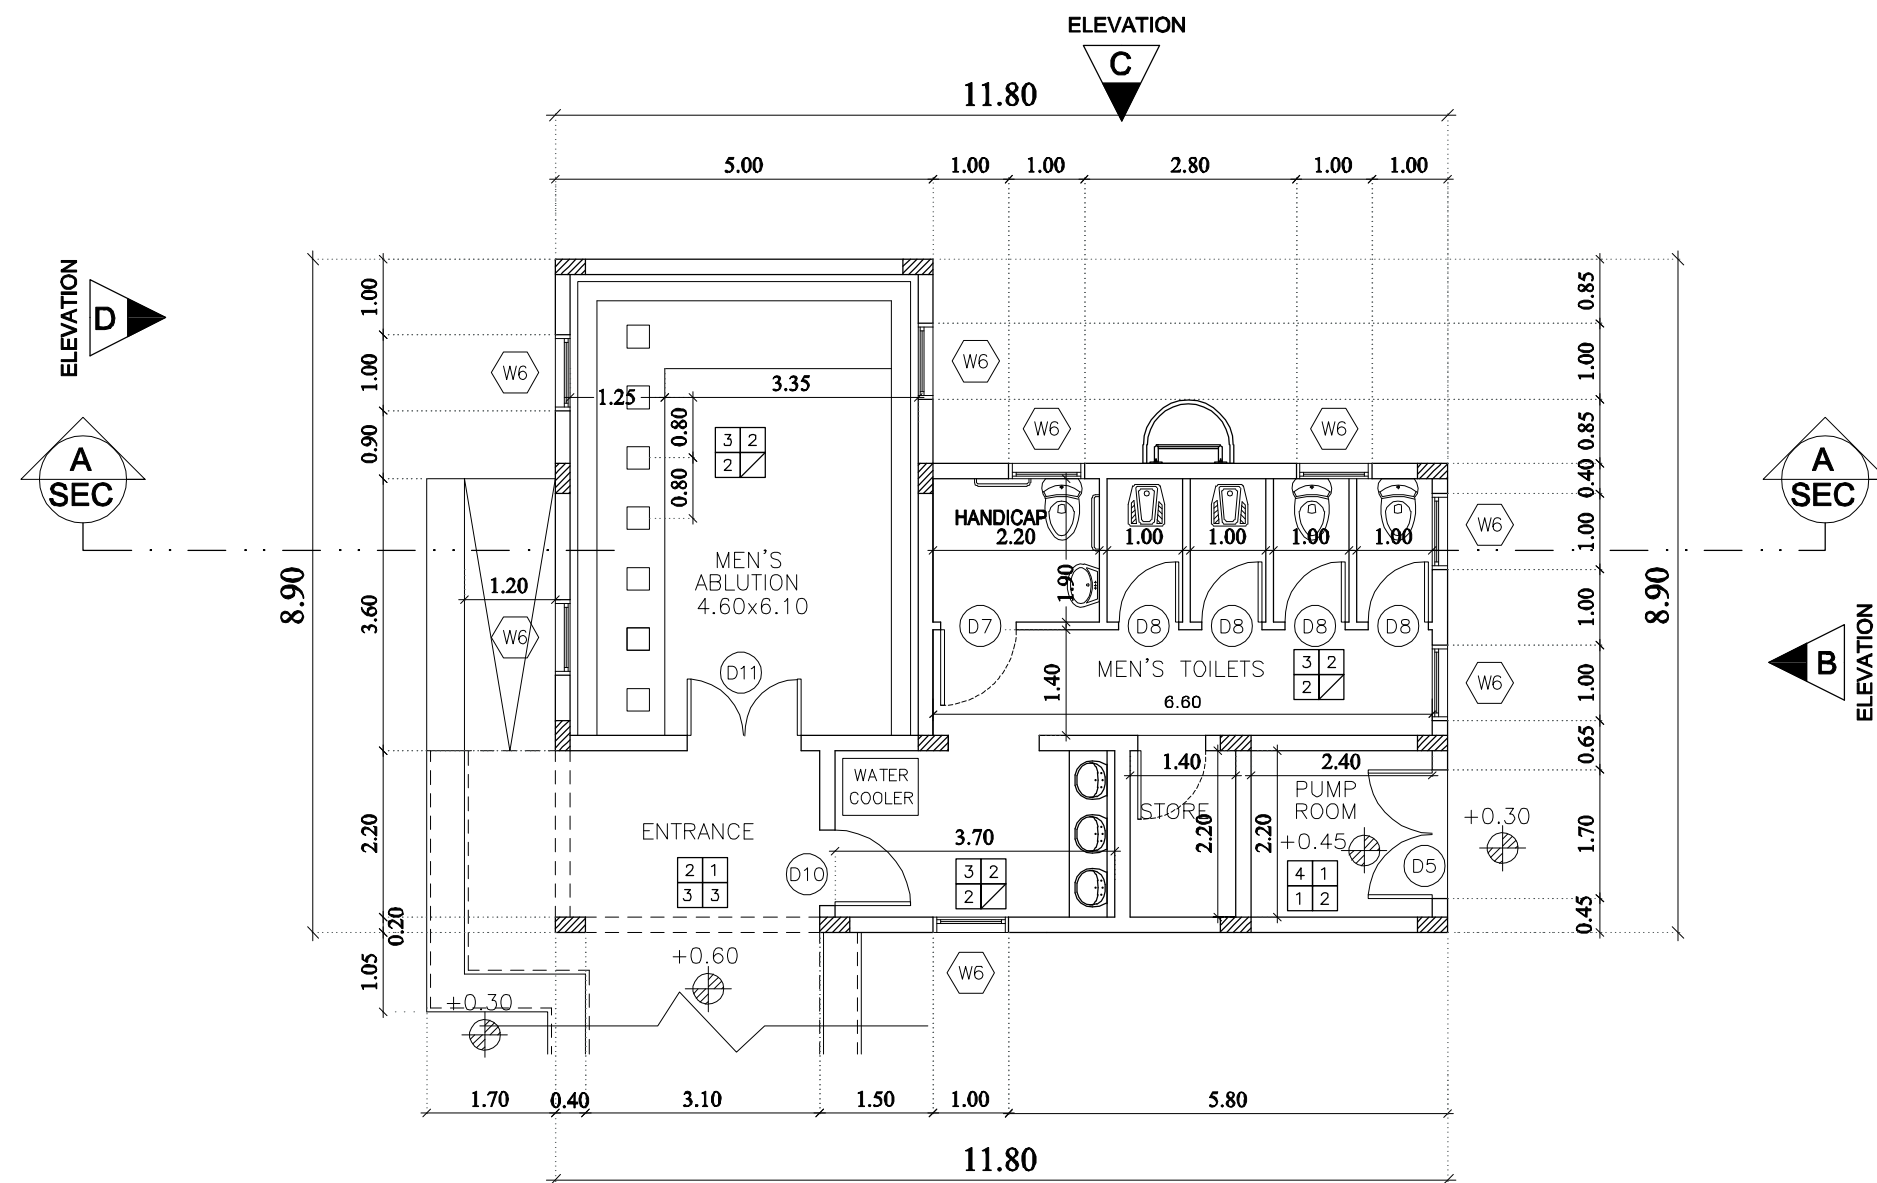

GROUND FLOOR PLAN

(SCALE = 1 : 100)

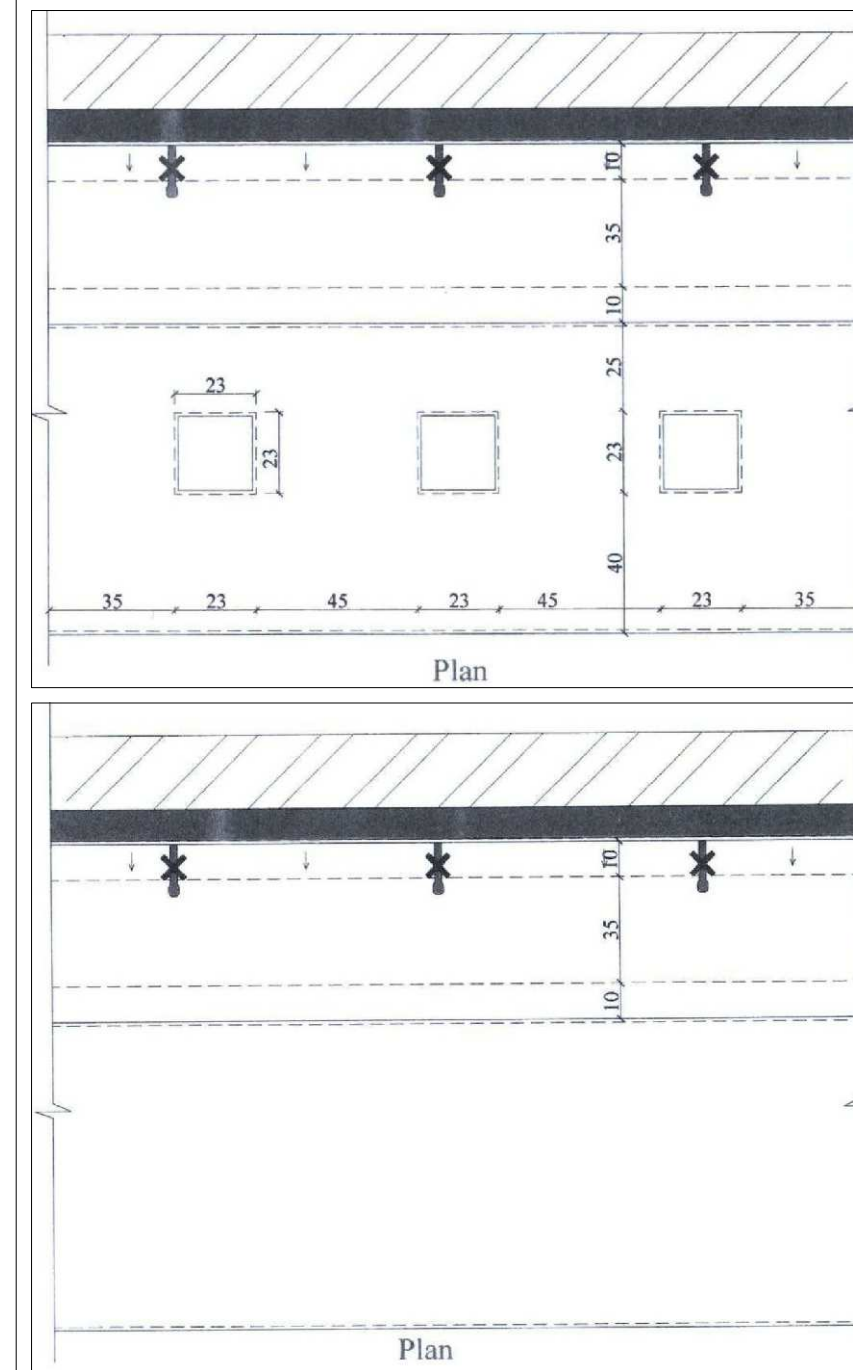

ABLUTION DETAILS

GENERAL NOTES:

1. IT IS NOT ALLOWED TO REPRODUCE THE SHEETS CONTENTS IN ANY FORM EXCEPT FOR THE PURPOSE FOR WHICH IT IS INTENDED.
2. THESE DRAWINGS ARE DIAGRAMMATIC AND SHALL NOT BE SCALED. ADDITIONAL DATA SHALL BE REQUESTED FROM THE CONSULTANCY THROUGH WRITTEN CLARIFICATION. VERIFY ALL EXISTING CONDITIONS AND DIMENSIONS BEFORE PROCEEDING WITH ANY PORTION OF ANY WORK.
3. NO CHANGES, MODIFICATIONS OR DEVIATIONS SHALL BE WRITTEN PERMISSION FROM **ALMASAH ENGINEERING CONSULTANTS**.
4. ALL WORK AS OUTLINED IN THESE DOCUMENTS, SHALL STRICTLY CONFORM TO ALL APPLICABLE CODES. IN THE EVENT OF A CONFLICT, THE MORE STRINGENT REQUIREMENT SHALL GOVERN AND BE MET.




SIA - SM-01



حُكُومَةُ الشَّارِقَة
دائرة الشؤون الإسلامية

CONSULTANT STAMP

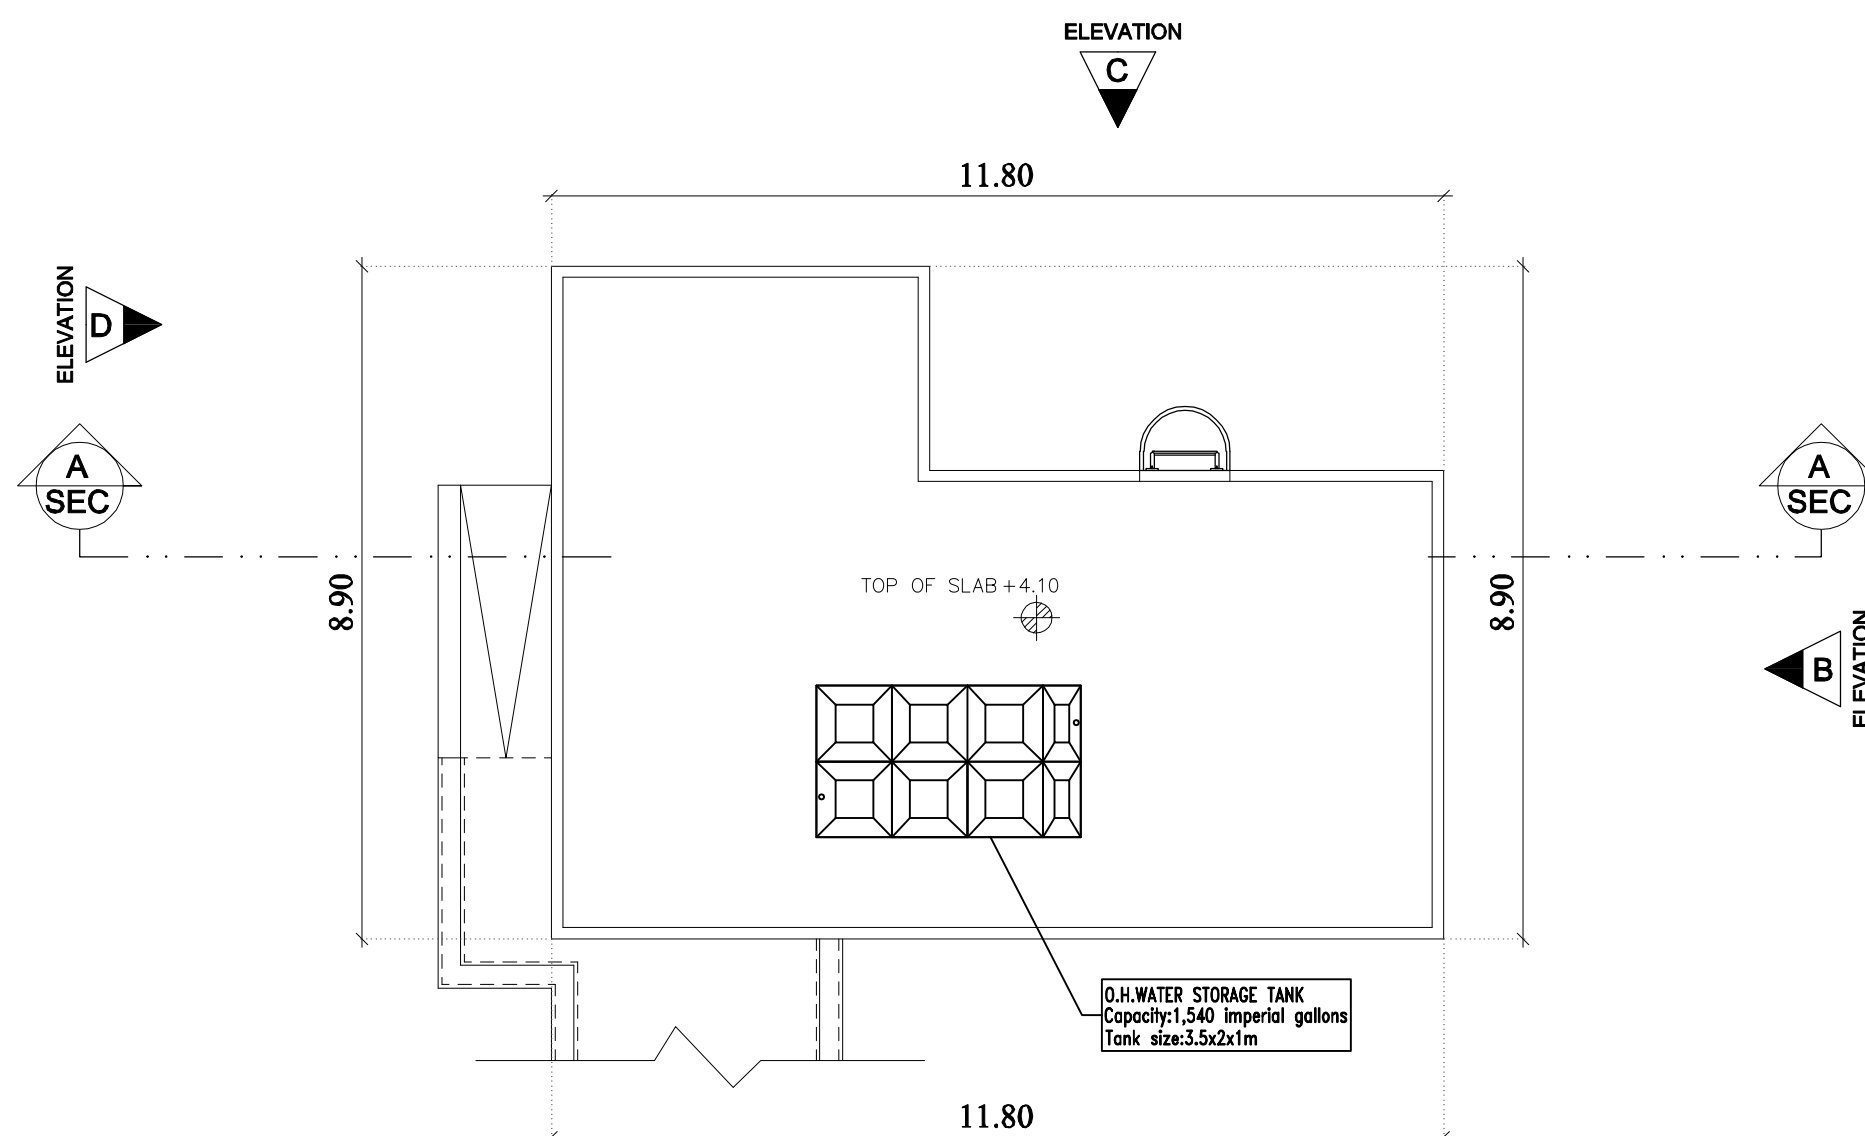

ROOF FLOOR PLAN

(SCALE = 1 : 100)



CLIENT:

GOVERNMENT OF SHARJAH -
DEPARTMENT OF ISLAMIC AFFAIRS


PROJECT:


(SIA - SM-01)
PROPOSED MASJID + ABLUTION +
IMAM HOUSE

SHEET TITLE:


ABLUTION
GROUND & ROOF FLOOR PLAN

ARCHITECT Arch. Mostafa Ramadan	TYPE ARCHITECTURE
STRUCTURAL Eng : Mohamed Gomaa	SHEET No. A - 10
CHECKED BY Eng : Mohamed Attia	Location : Plot No :
SCALE 1:100	DATE May - 2022
	Project No.

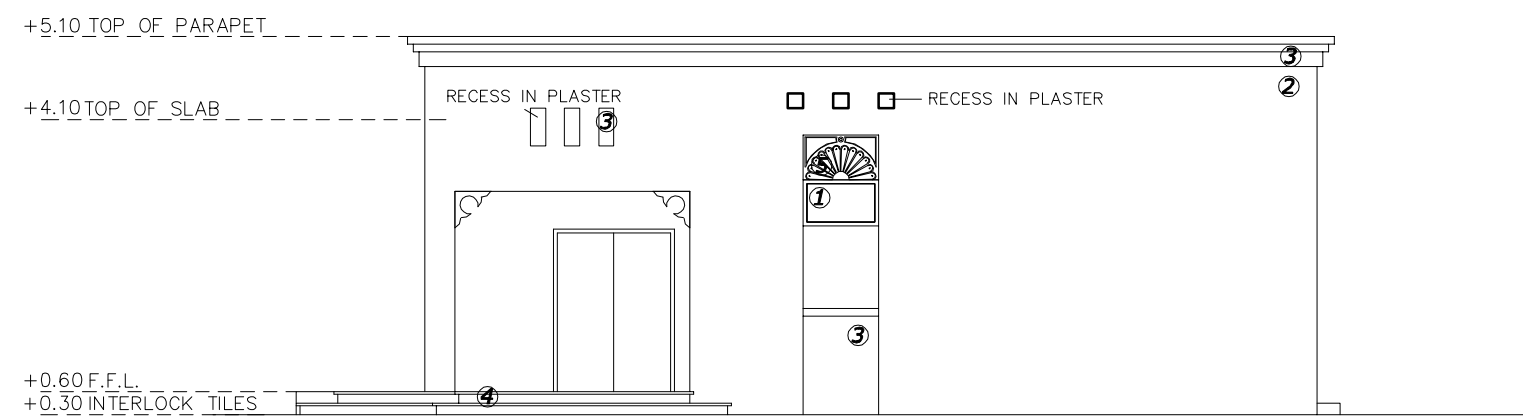

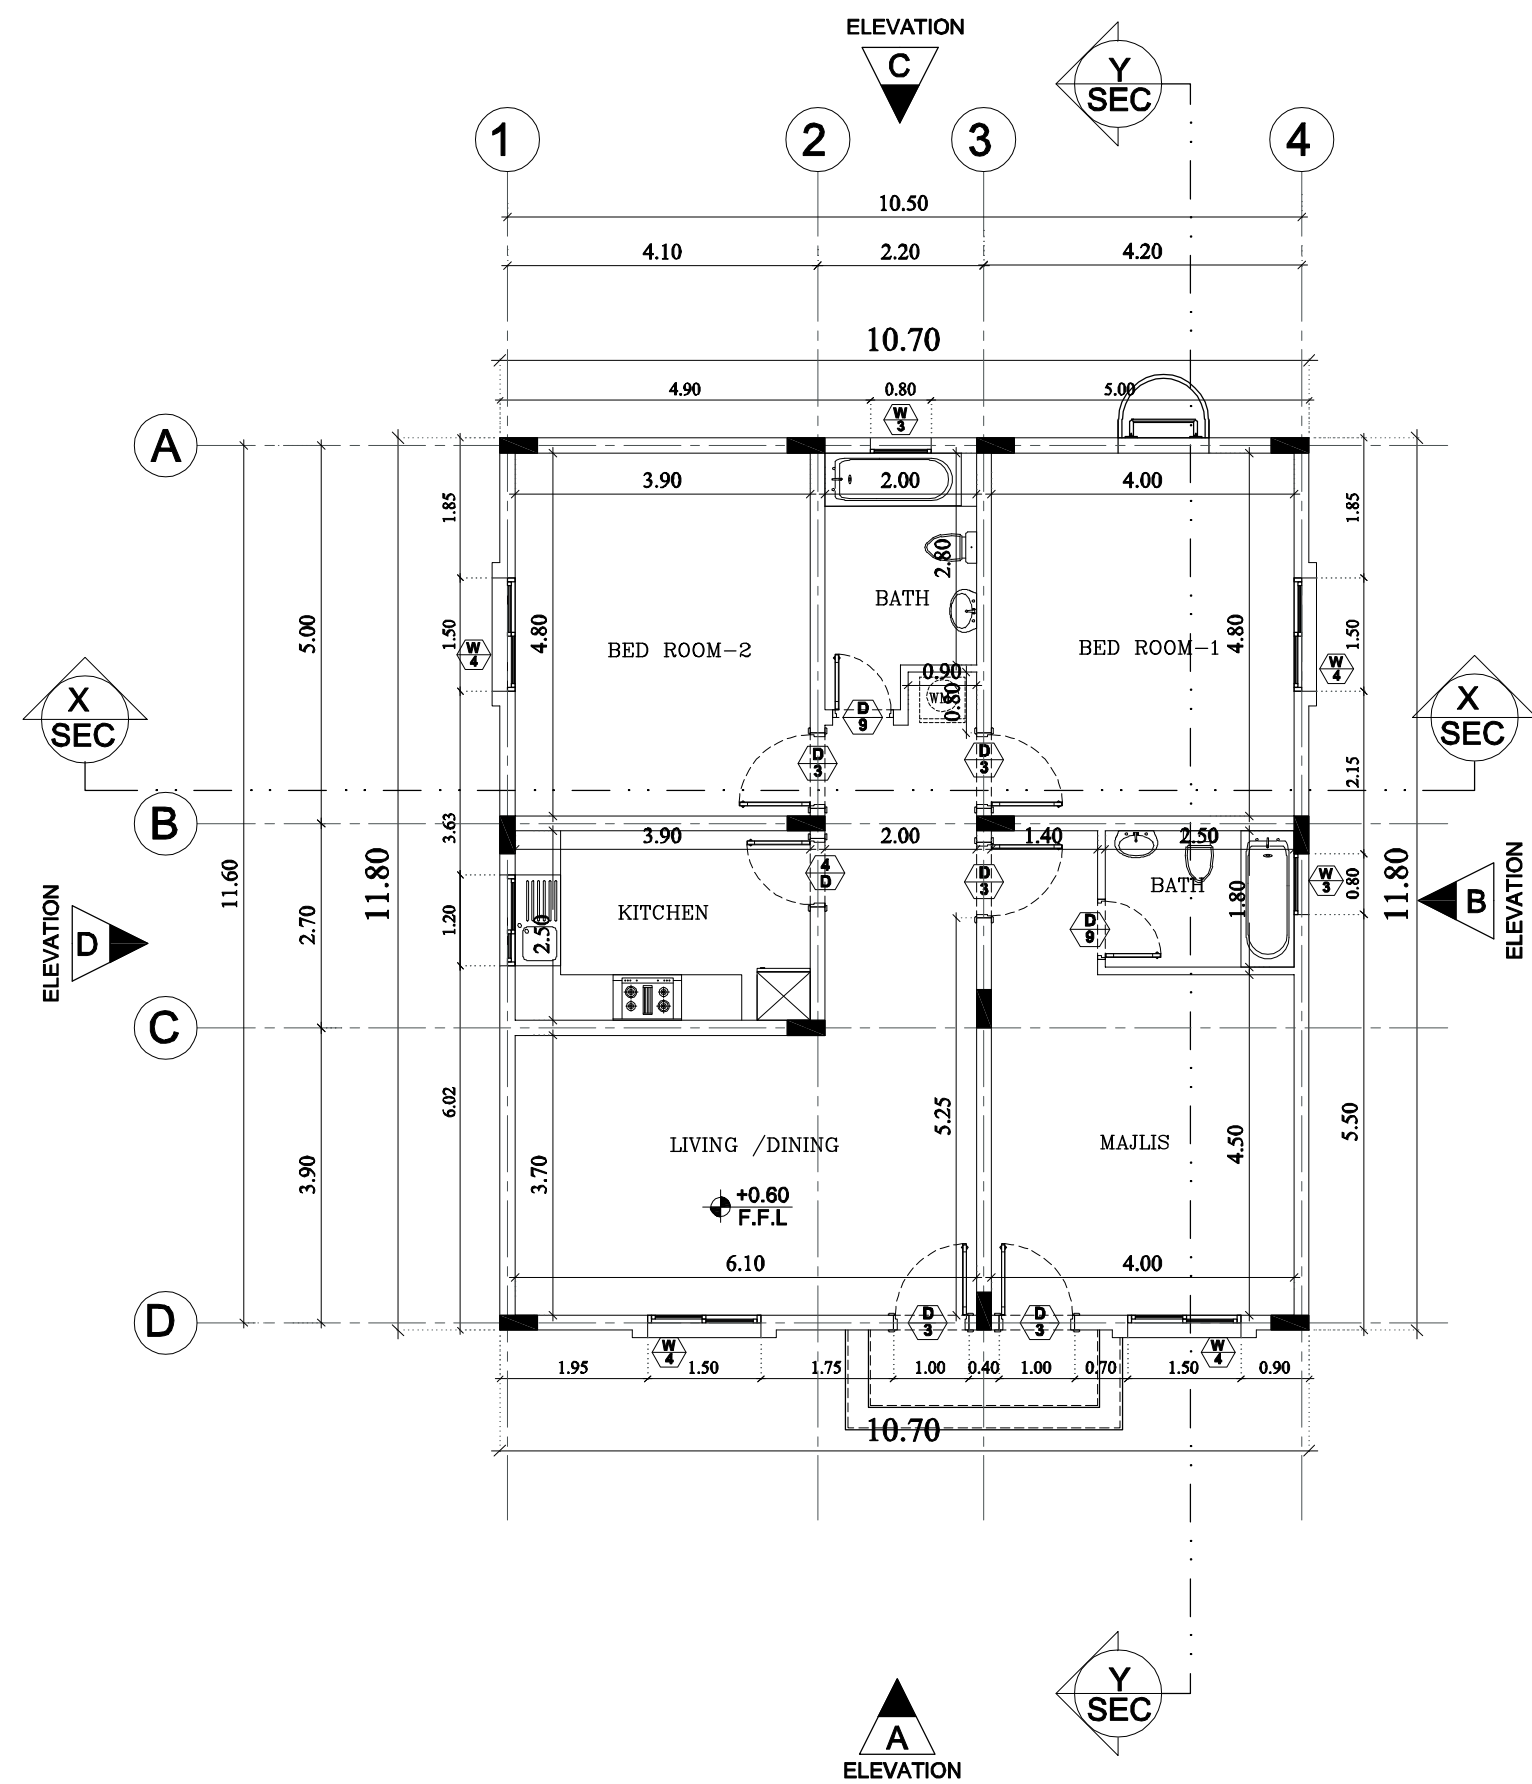

GROUND FLOOR PLAN
(SCALE = 1 : 100)

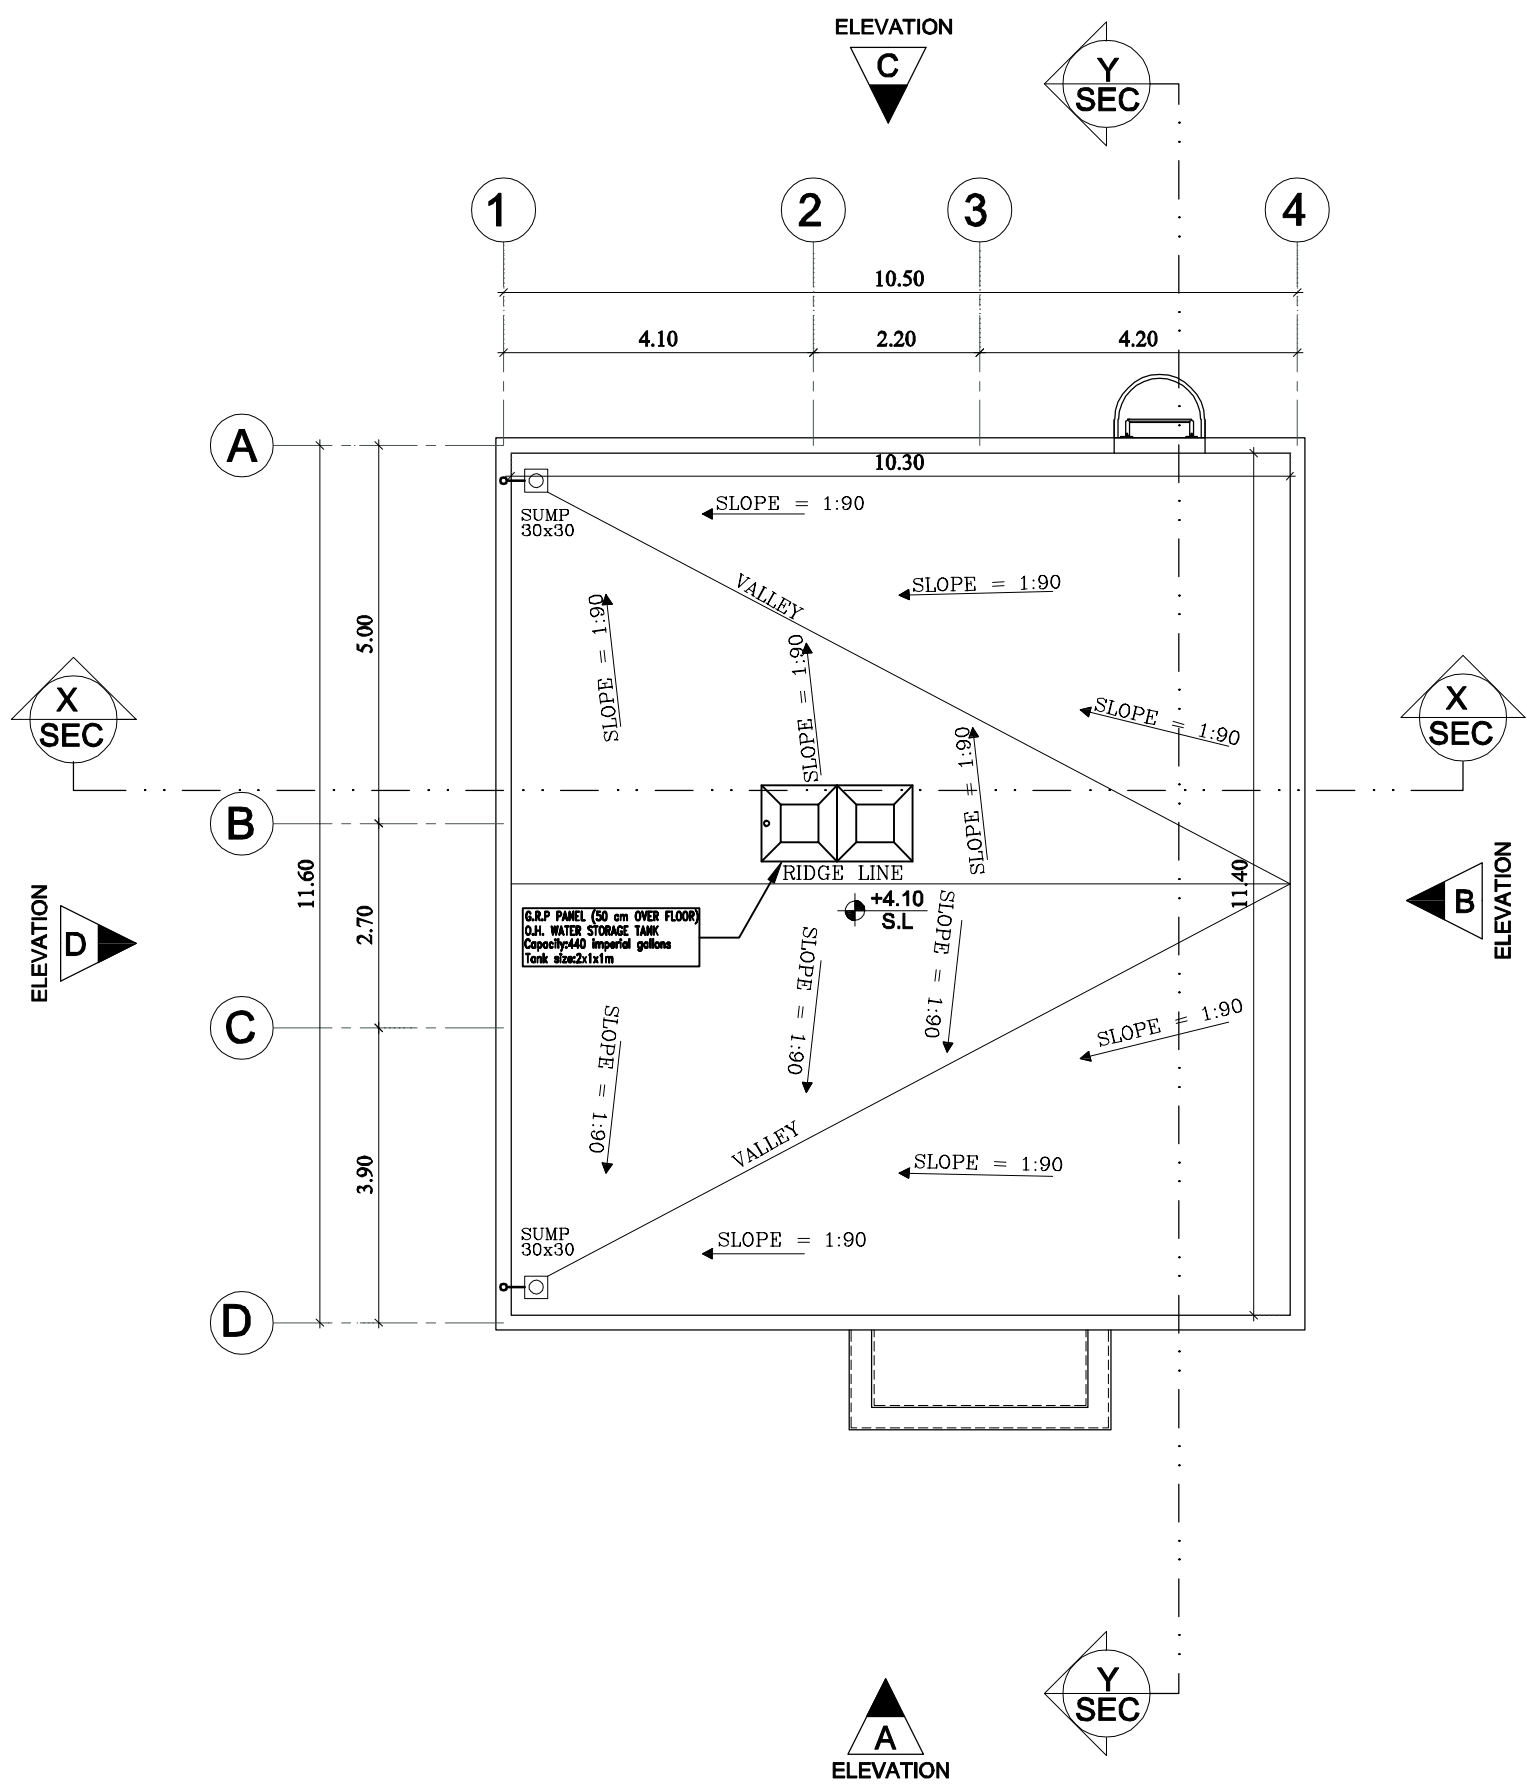


ROOF FLOOR PLAN
(SCALE = 1 : 100)

- GENERAL NOTES:**
1. IT IS NOT ALLOWED TO REPRODUCE THE SHEETS CONTENTS IN ANY FORM EXCEPT FOR THE PURPOSE FOR WHICH IT IS INTENDED.
 2. THESE DRAWINGS ARE DIAGRAMMATIC AND SHALL NOT BE SCALED. ADDITIONAL DATA SHALL BE REQUESTED FROM THE CONSULTANCY THROUGH WRITTEN CLARIFICATION. VERIFY ALL EXISTING CONDITIONS AND DIMENSIONS BEFORE PROCEEDING WITH ANY PORTION OF ANY WORK.
 3. NO CHANGES, MODIFICATIONS OR DEVIATIONS SHALL BE WRITTEN PERMISSION FROM **ALMASAH ENGINEERING CONSULTANTS**.
 4. ALL WORK AS OUTLINED IN THESE DOCUMENTS, SHALL STRICTLY CONFORM TO ALL APPLICABLE CODES. IN THE EVENT OF A CONFLICT, THE MORE STRINGENT REQUIREMENT SHALL GOVERN AND BE MET.




SIA - SM-01

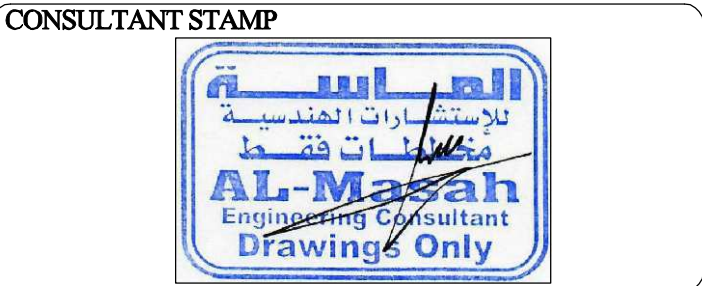


CLIENT: GOVERNMENT OF SHARJAH - DEPARTMENT OF ISLAMIC AFFAIRS			
PROJECT: (SIA - SM-01) PROPOSED MASJID + ABLUTION + IMAM HOUSE			
SHEET TITLE: IMAM HOUSE GROUND & ROOF FLOOR PLAN			
ARCHITECT Arch. Mostafa Ramadan	TYPE	ARCHITECTURE	
STRUCTURAL Eng : Mohamed Goma	SHEET No.	A - 12	
CHECKED BY Eng : Mohamed Attia	Location :		
SCALE 1:100	DATE May - 2022	Plot No :	
		Project No.	




ELEVATION -A
(SCALE = 1 : 100)

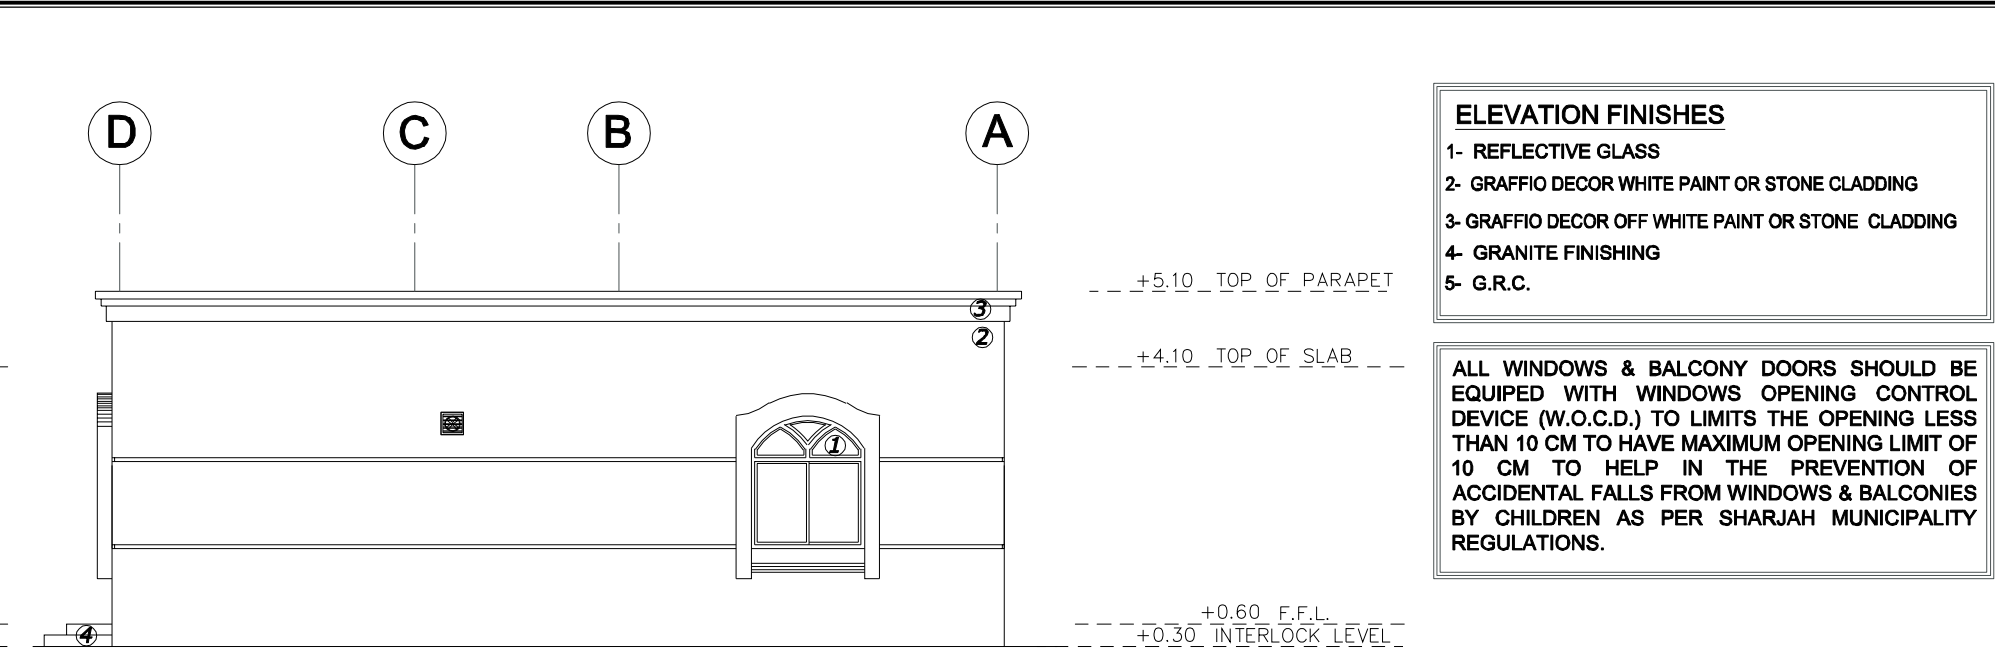


ELEVATION -B
(SCALE = 1 : 100)

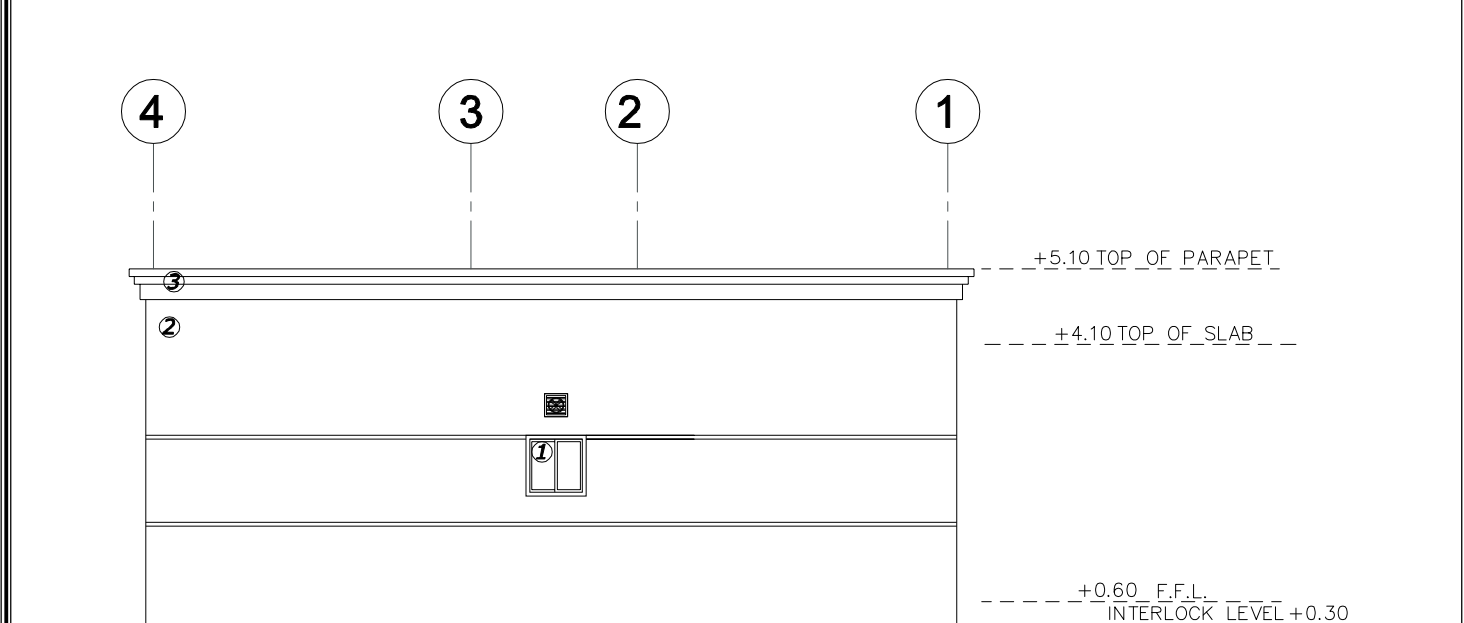


ELEVATION -C
(SCALE = 1 : 100)

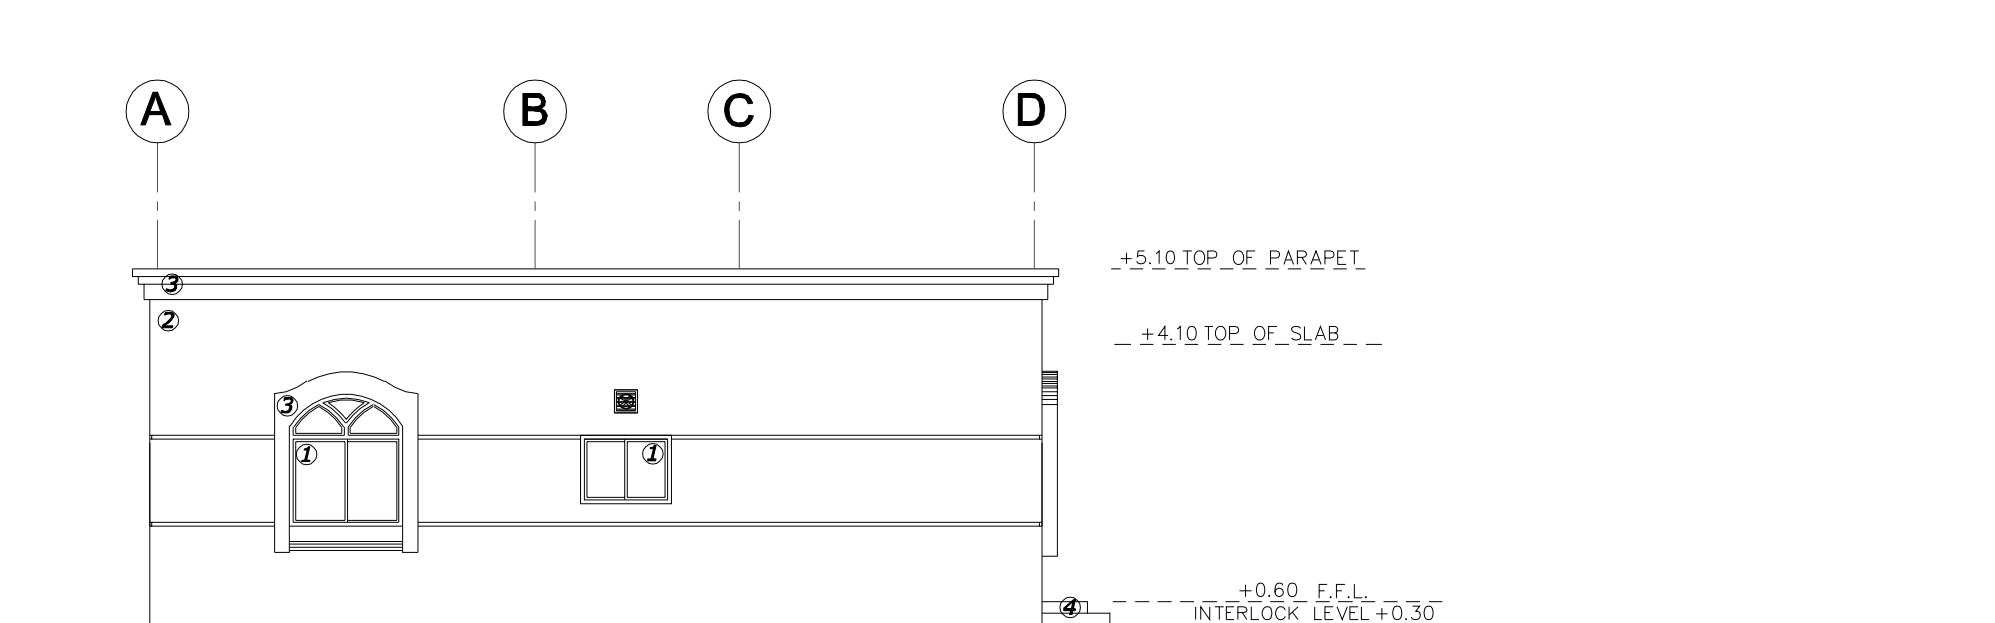

ELEVATION -D
(SCALE = 1 : 100)

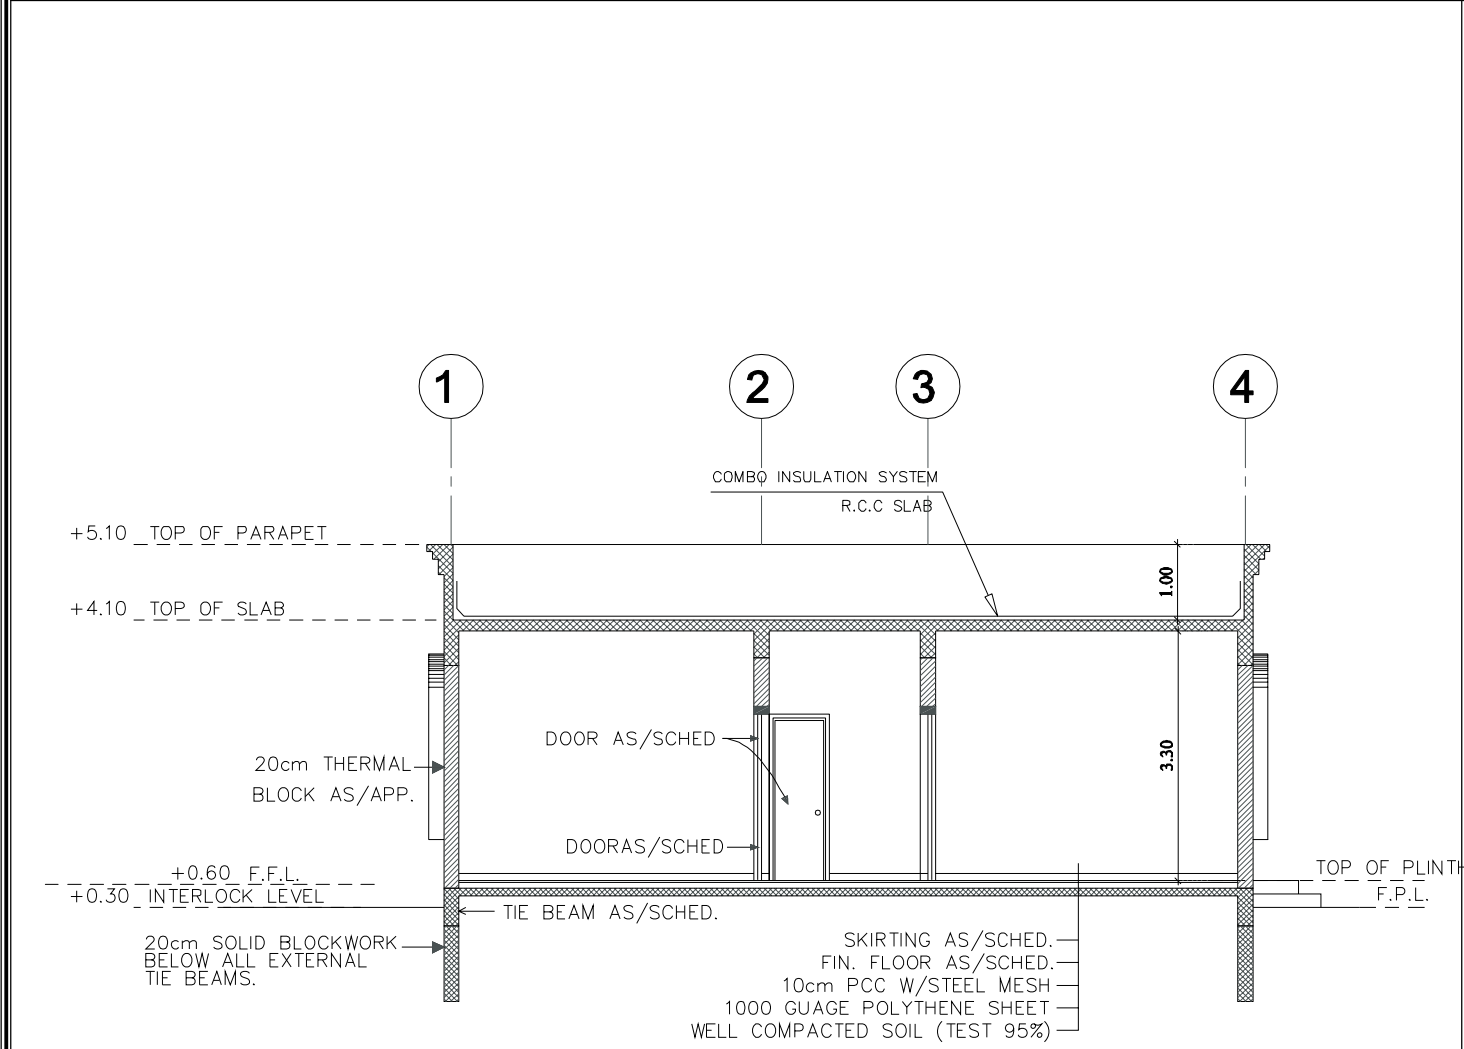

SECTION X-X
(SCALE = 1 : 100)

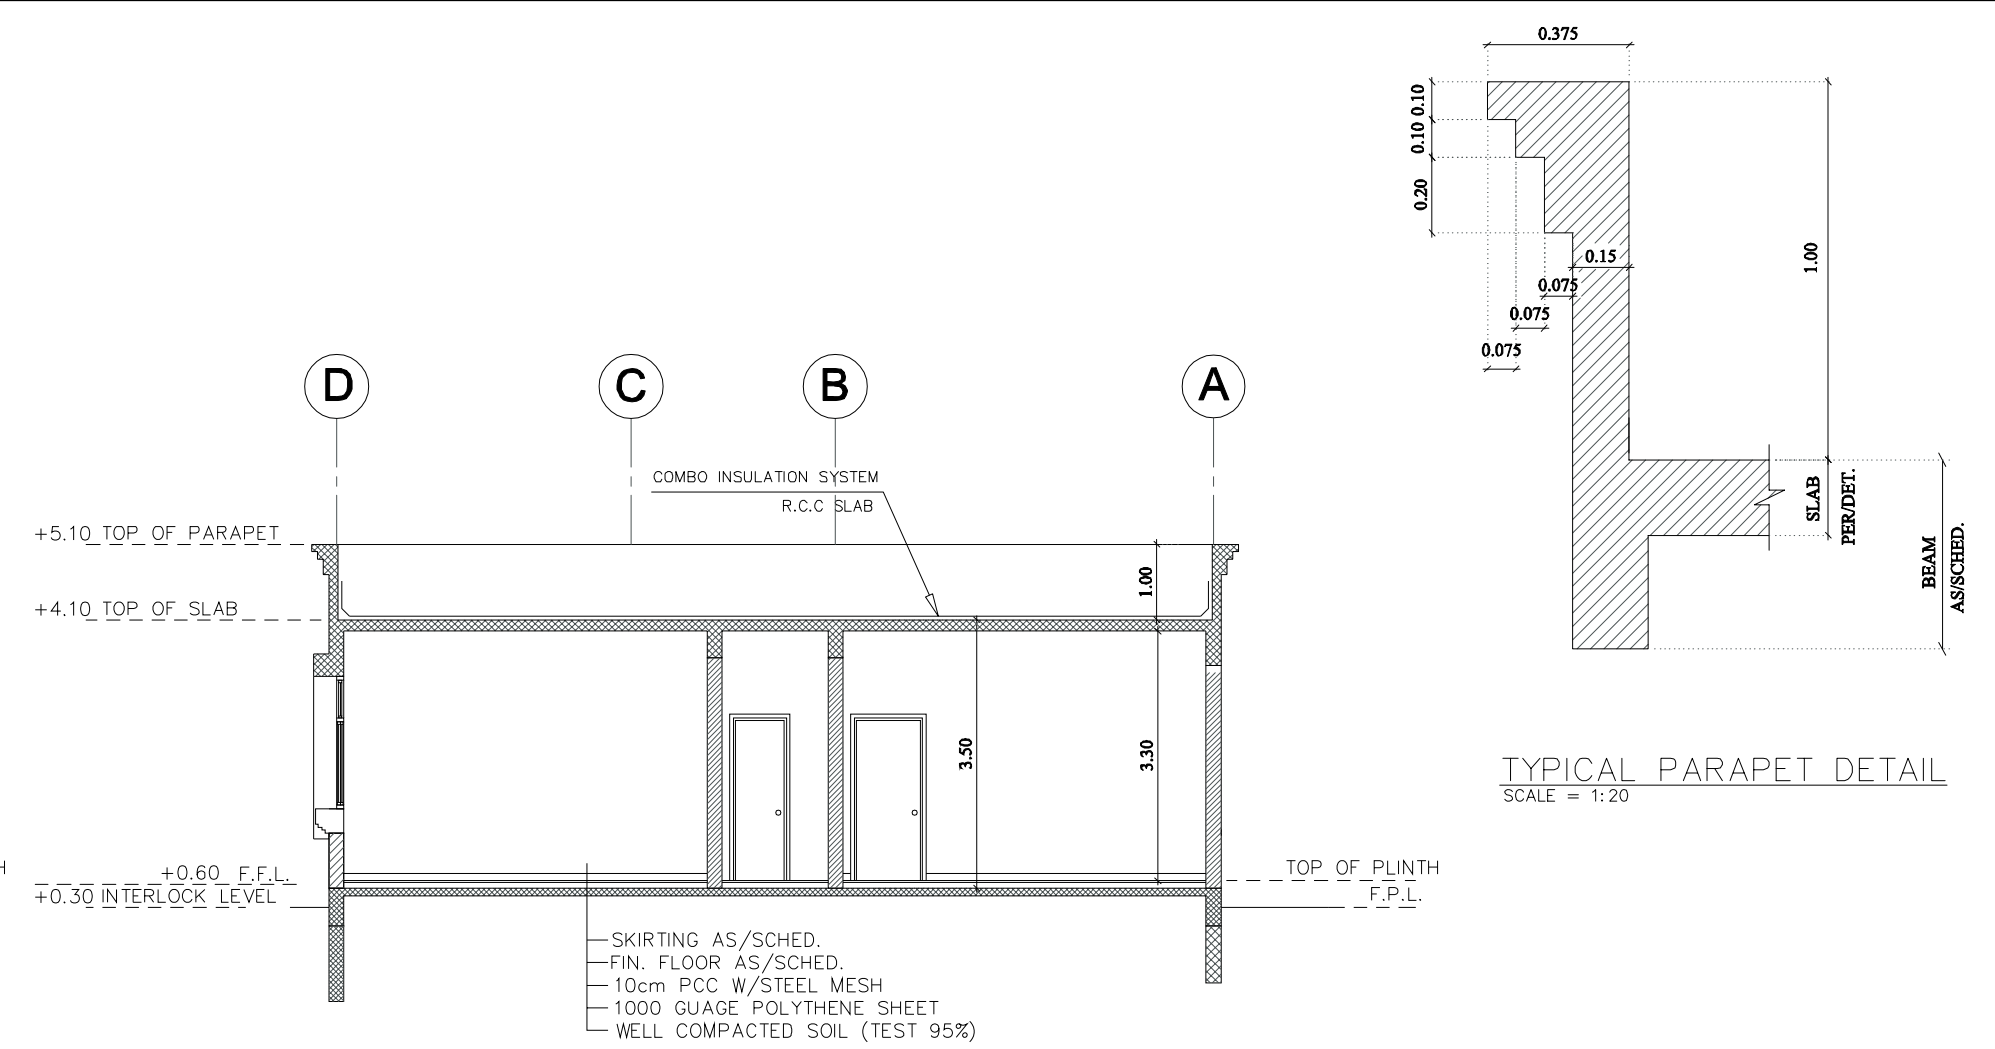

SECTION Y-Y
(SCALE = 1 : 100)

ELEVATION FINISHES

- 1- REFLECTIVE GLASS
- 2- GRAFFIO DECOR WHITE PAINT OR STONE CLADDING
- 3- GRAFFIO DECOR OFF WHITE PAINT OR STONE CLADDING
- 4- GRANITE FINISHING
- 5- G.R.C.

ALL WINDOWS & BALCONY DOORS SHOULD BE EQUIPED WITH WINDOWS OPENING CONTROL DEVICE (W.O.C.D.) TO LIMITS THE OPENING LESS THAN 10 CM TO HAVE MAXIMUM OPENING LIMIT OF 10 CM TO HELP IN THE PREVENTION OF ACCIDENTAL FALLS FROM WINDOWS & BALCONIES BY CHILDREN AS PER SHARJAH MUNICIPALITY REGULATIONS.

GENERAL NOTES:

- 1.IT IS NOT ALLOWED TO REPRODUCE THE SHEETS CONTENTS IN ANY FORM EXCEPT FOR THE PURPOSE FOR WHICH IT IS INTENDED.
2. THESE DRAWINGS ARE DIAGRAMMATIC AND SHALL NOT BE SCALED. ADDITIONAL DATA SHALL BE REQUESTED FROM THE CONSULTANCY THROUGH WRITTEN CLARIFICATION. VERIFY ALL EXISTING CONDITIONS AND DIMENSIONS BEFORE PROCEEDING WITH ANY PORTION OF ANY WORK.
3. NO CHANGES, MODIFICATIONS OR DEVIATIONS SHALL BE WRITTEN PERMISSION FROM **ALMASAH ENGINEERING CONSULTANTS**.
4. ALL WORK AS OUTLINED IN THESE DOCUMENTS, SHALL STRICTLY CONFORM TO ALL APPLICABLE CODES. IN THE EVENT OF A CONFLICT, THE MORE STRINGENT REQUIREMENT SHALL GOVERN AND BE MET.



SIA - SM-01



CONSULTANT STAMP



CLIENT:

GOVERNMENT OF SHARJAH -
DEPARTMENT OF ISLAMIC AFFAIRS

PROJECT:

(SIA - SM-01)
PROPOSED MASJID + ABLUTION +
IMAM HOUSE


SHEET TITLE:

IMAM HOUSE
ELEVATIONS & SECTION

ARCHITECT Arch. Mostafa Ramadan	TYPE ARCHITECTURE
STRUCTURAL Eng : Mohamed Gomaa	SHEET No. A - 13
CHECKED BY Eng : Mohamed Attia	Location : Plot No : Project No.
SCALE 1:100	DATE May - 2022

* NOTES .:

- 1- ALL EXTERNAL WALLS TO BE 20.cm THERMAL BLOCK.
- 2- WINDOWS TO BE DOUBLE REFLECTIVE GLASS

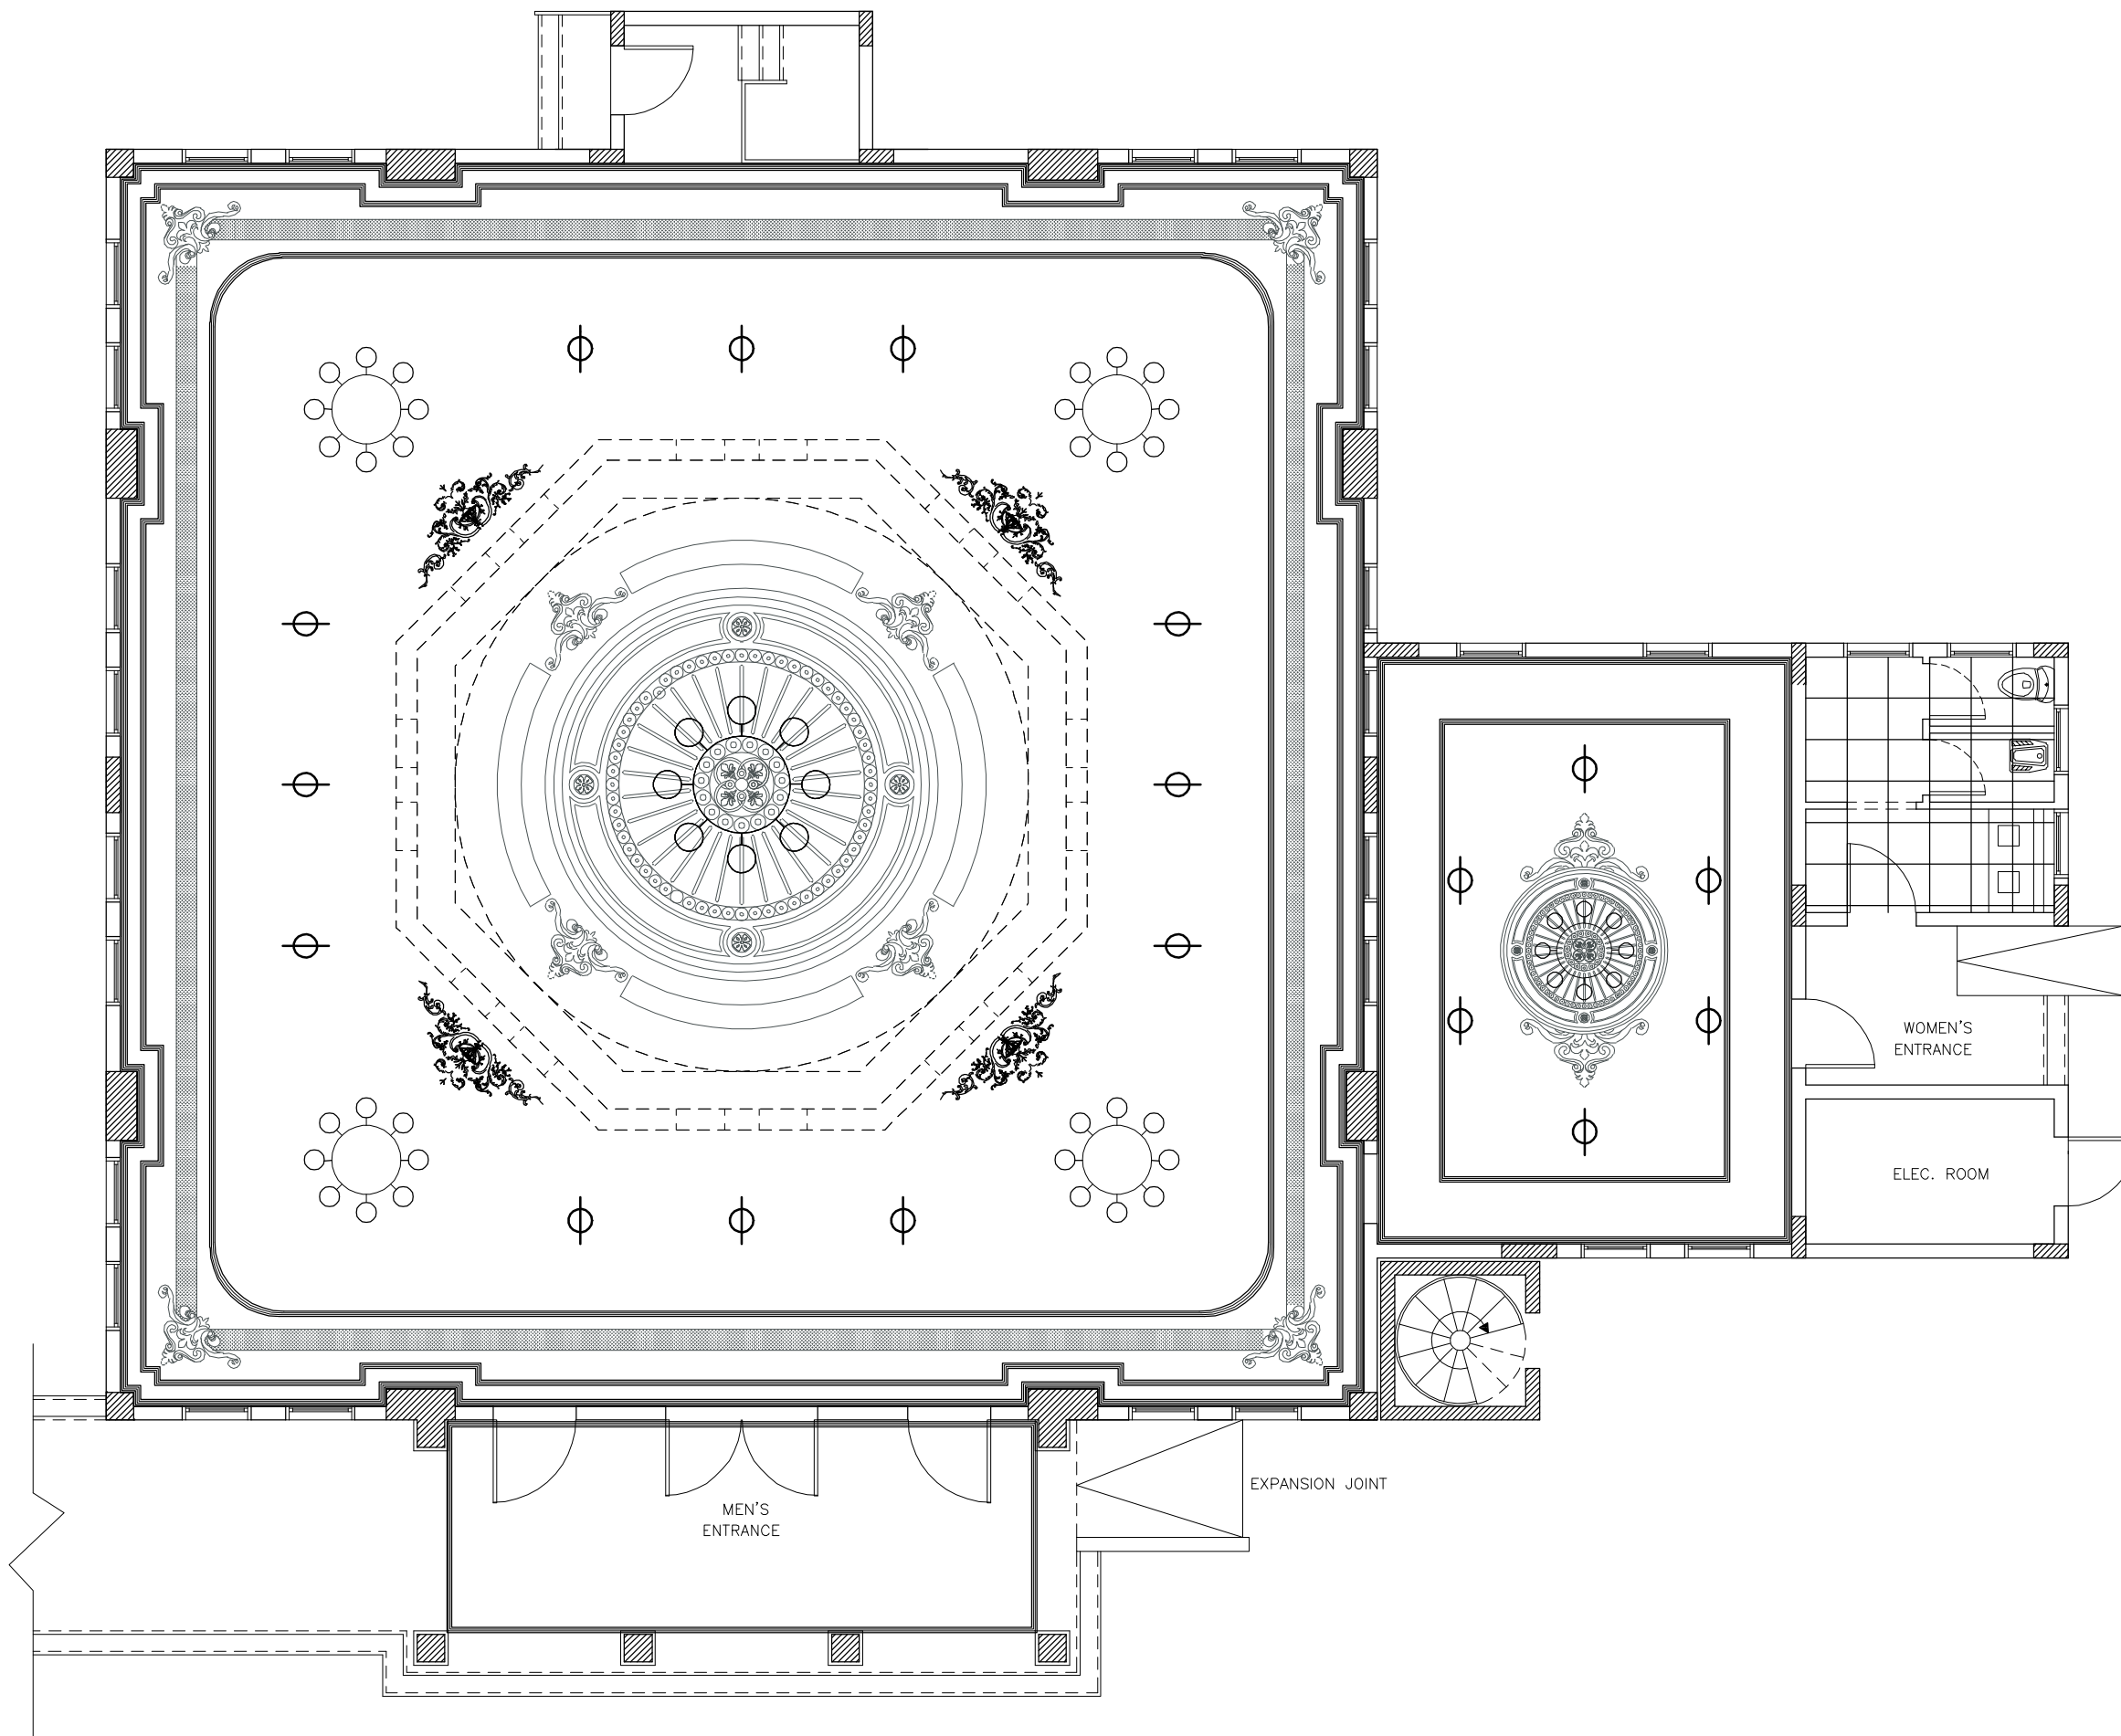

CEILING PLAN
(SCALE = 1 : 100)

- GENERAL NOTES:**
- 1.IT IS NOT ALLOWED TO REPRODUCE THE SHEETS CONTENTS IN ANY FORM EXCEPT FOR THE PURPOSE FOR WHICH IT IS INTENDED.
 2. THESE DRAWINGS ARE DIAGRAMMATIC AND SHALL NOT BE SCALED. ADDITIONAL DATA SHALL BE REQUESTED FROM THE CONSULTANCY THROUGH WRITTEN CLARIFICATION. VERIFY ALL EXISTING CONDITIONS AND DIMENSIONS BEFORE PROCEEDING WITH ANY PORTION OF ANY WORK.
 3. NO CHANGES, MODIFICATIONS OR DEVIATIONS SHALL BE WRITTEN PERMISSION FROM **ALMASAH ENGINEERING CONSULTANTS**.
 4. ALL WORK AS OUTLINED IN THESE DOCUMENTS, SHALL STRICTLY CONFORM TO ALL APPLICABLE CODES. IN THE EVENT OF A CONFLICT, THE MORE STRINGENT REQUIREMENT SHALL GOVERN AND BE MET.

SIA - SM-01



حُكُومَةُ الشَّارِقَةِ
دائرة الشؤون الإسلامية

CONSULTANT STAMP





Sharjah ☎ 06 5 444 521 ☎ 06 5 444 523 📍 Office: 306, Al Fisal 2 Bldg., King Faisal St.

CLIENT: **GOVERNMENT OF SHARJAH -
DEPARTMENT OF ISLAMIC AFFAIRS**

PROJECT: **(SIA - SM-01)
PROPOSED MASJID + ABLUTION +
IMAM HOUSE**

SHEET TITLE: **CEILING PLAN**

ARCHITECT Arch. Mostafa Ramadan	TYPE	ARCHITECTURE
STRUCTURAL Eng : Mohamed Gomaa	SHEET No.	A - 14
CHECKED BY Eng : Mohamed Attia	Location :	
	Plot No :	
SCALE 1:100	DATE May - 2022	Project No.

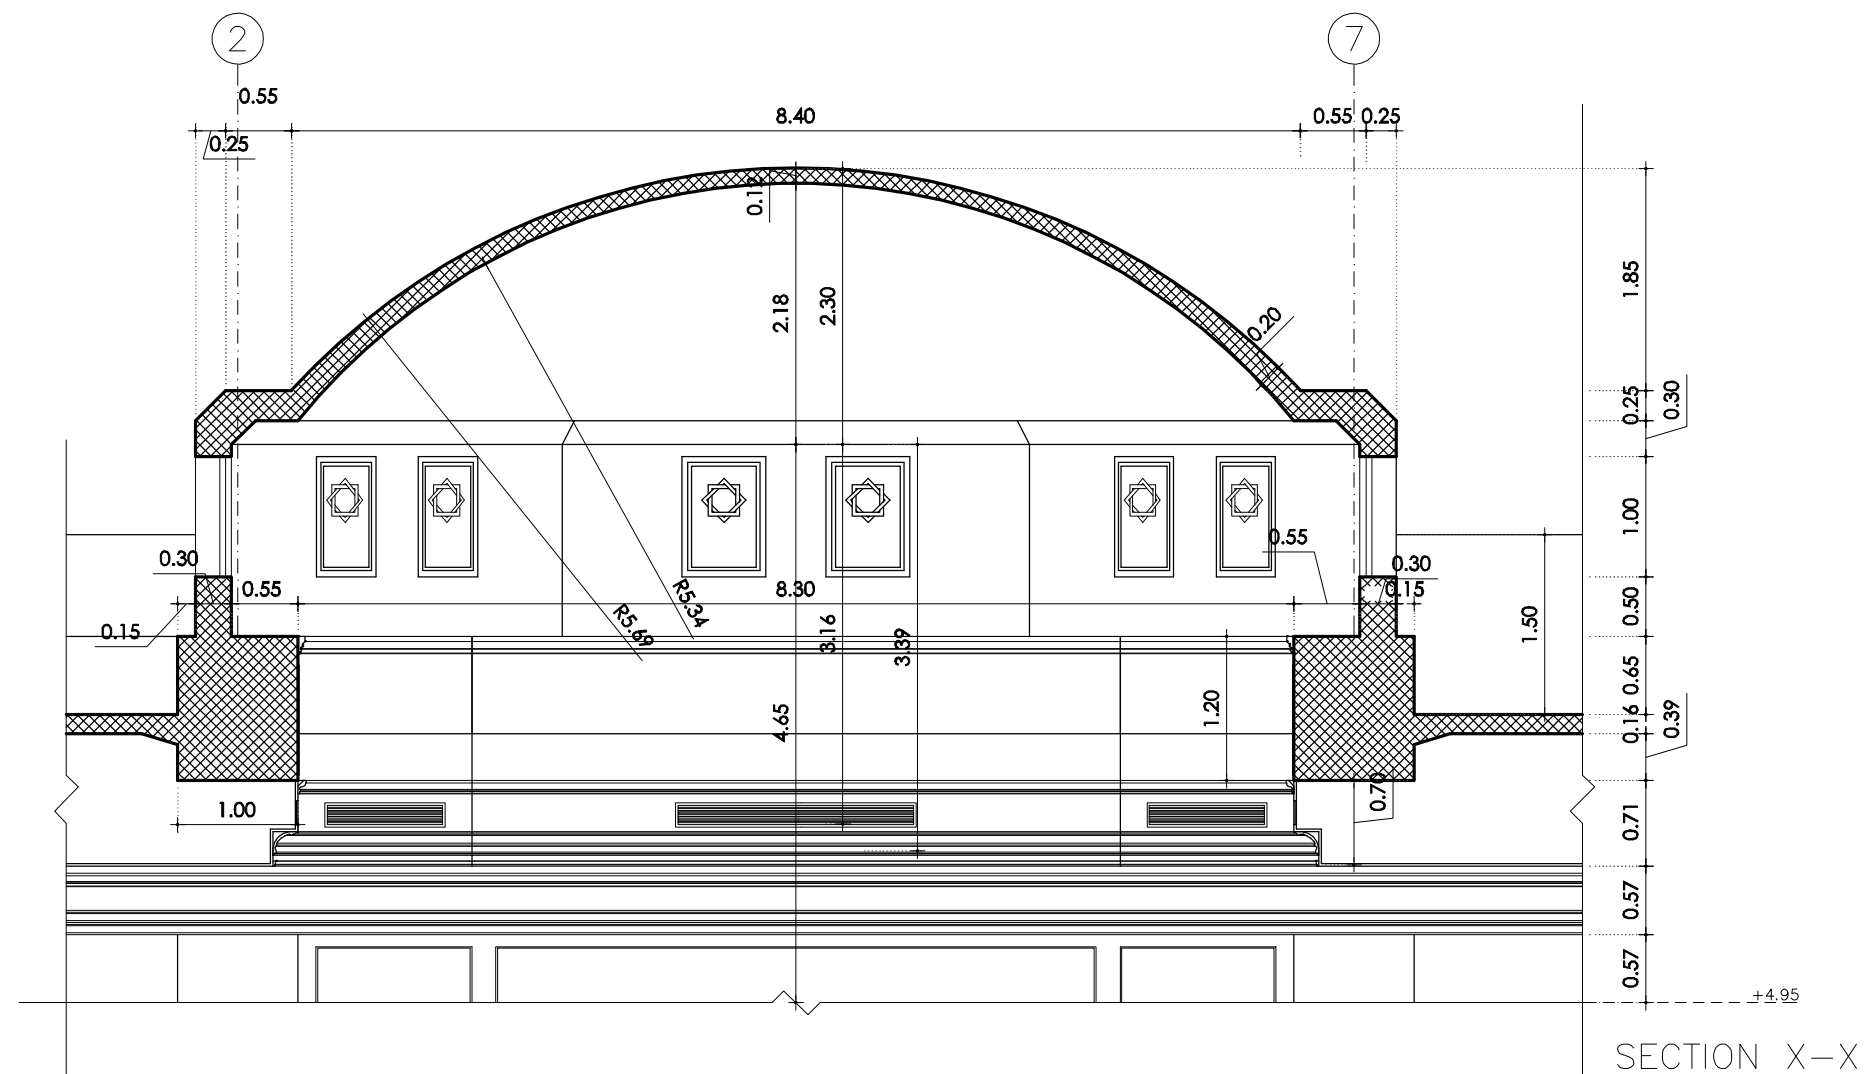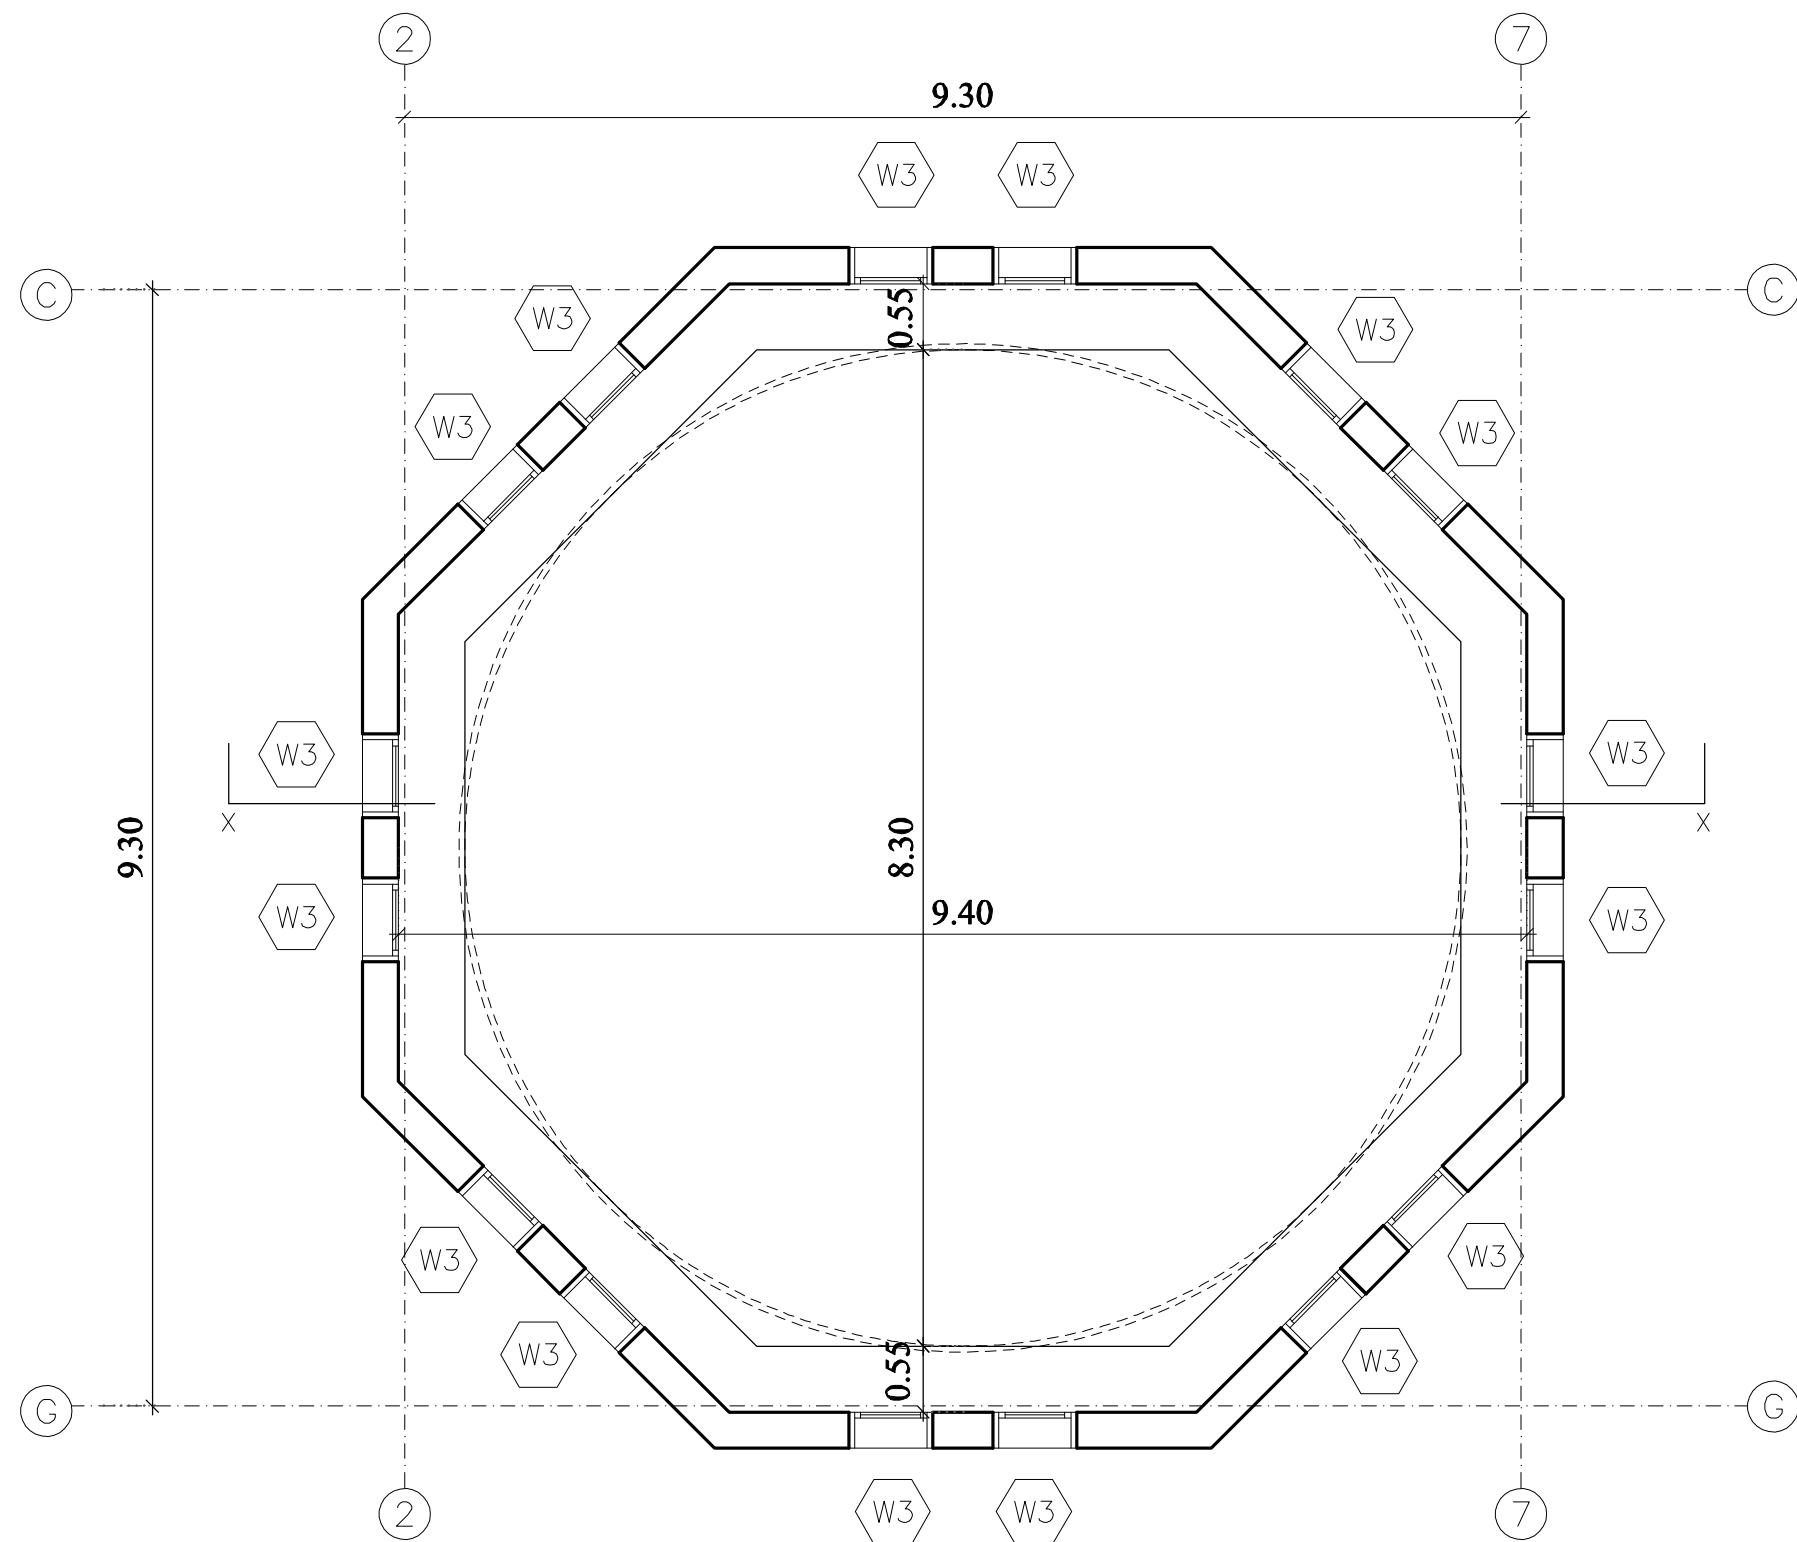


- GENERAL NOTES:**
1. IT IS NOT ALLOWED TO REPRODUCE THE SHEETS CONTENTS IN ANY FORM EXCEPT FOR THE PURPOSE FOR WHICH IT IS INTENDED.
 2. THESE DRAWINGS ARE DIAGRAMMATIC AND SHALL NOT BE SCALED. ADDITIONAL DATA SHALL BE REQUESTED FROM THE CONSULTANCY THROUGH WRITTEN CLARIFICATION. VERIFY ALL EXISTING CONDITIONS AND DIMENSIONS BEFORE PROCEEDING WITH ANY PORTION OF ANY WORK.
 3. NO CHANGES, MODIFICATIONS OR DEVIATIONS SHALL BE WRITTEN PERMISSION FROM **ALMASAH ENGINEERING CONSULTANTS**.
 4. ALL WORK AS OUTLINED IN THESE DOCUMENTS, SHALL STRICTLY CONFORM TO ALL APPLICABLE CODES. IN THE EVENT OF A CONFLICT, THE MORE STRINGENT REQUIREMENT SHALL GOVERN AND BE MET.









SIA - SM-01



حُكُومَةُ الشَّارِقَة
دائرة الشؤون الإسلامية

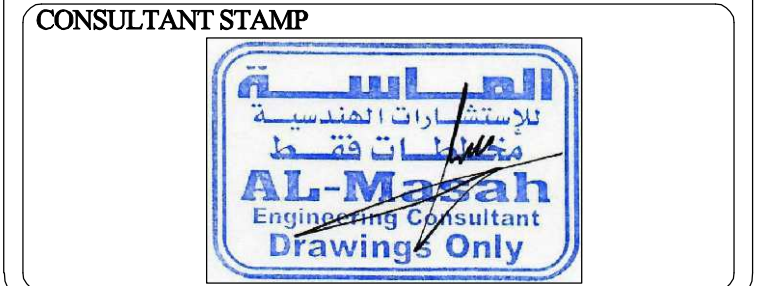

CLIENT: GOVERNMENT OF SHARJAH - DEPARTMENT OF ISLAMIC AFFAIRS			
PROJECT: (SIA - SM-01) PROPOSED MASJID + ABLUTION + IMAM HOUSE			
SHEET TITLE: DOME DETAILS (MASJID)			
ARCHITECT Arch. Mostafa Ramadan	TYPE	ARCHITECTURE	
STRUCTURAL Eng : Mohamed Goma	SHEET No.	A - 15	
CHECKED BY Eng : Mohamed Attia	Location :		
SCALE 1:100	DATE May - 2022	Plot No :	
		Project No.	

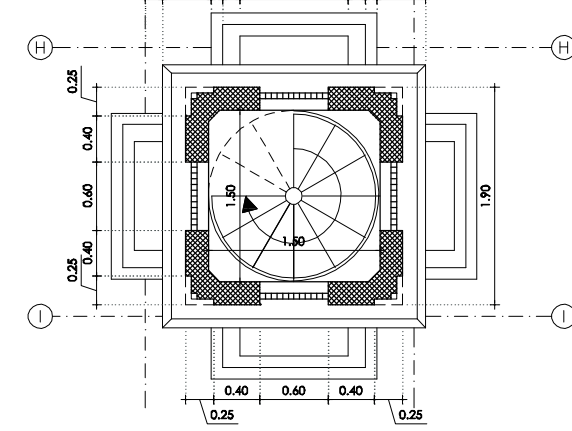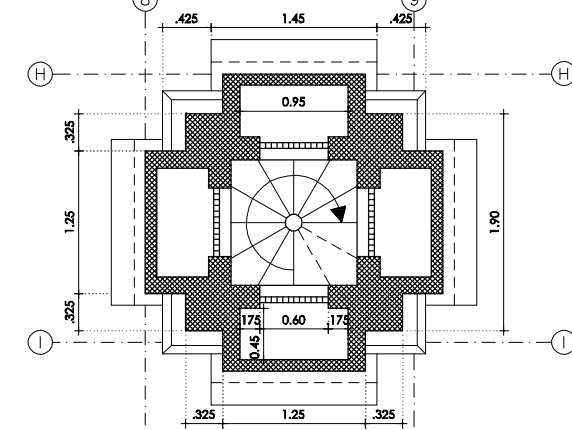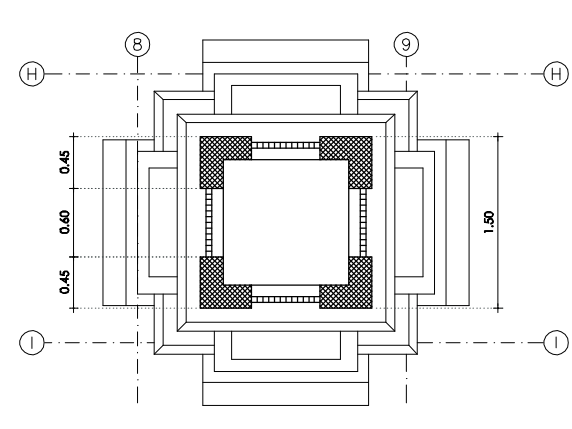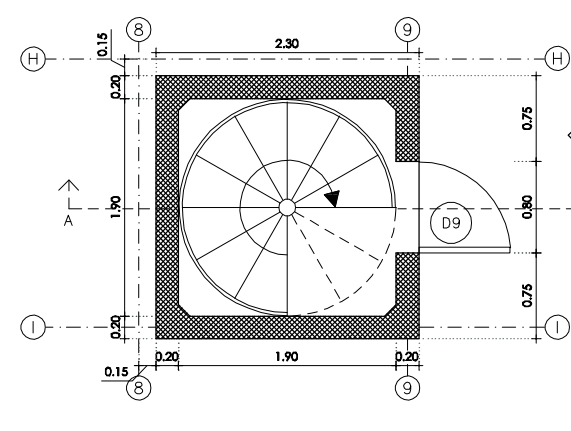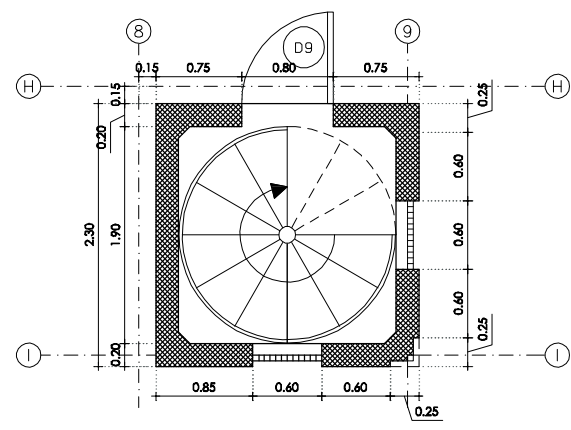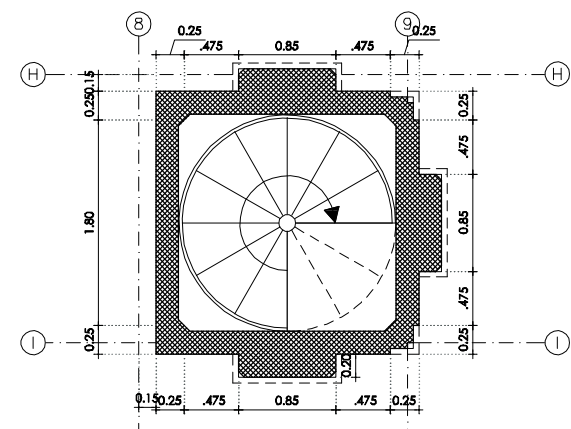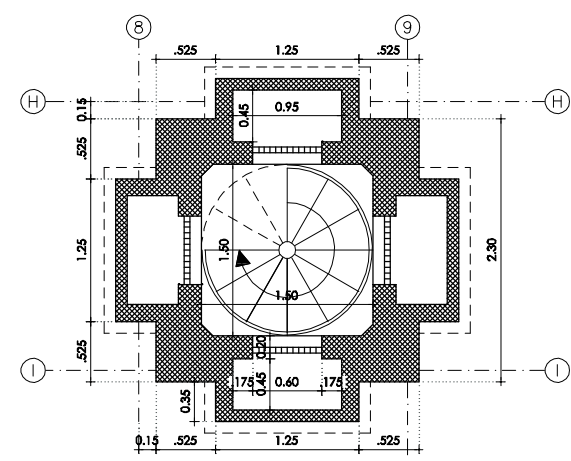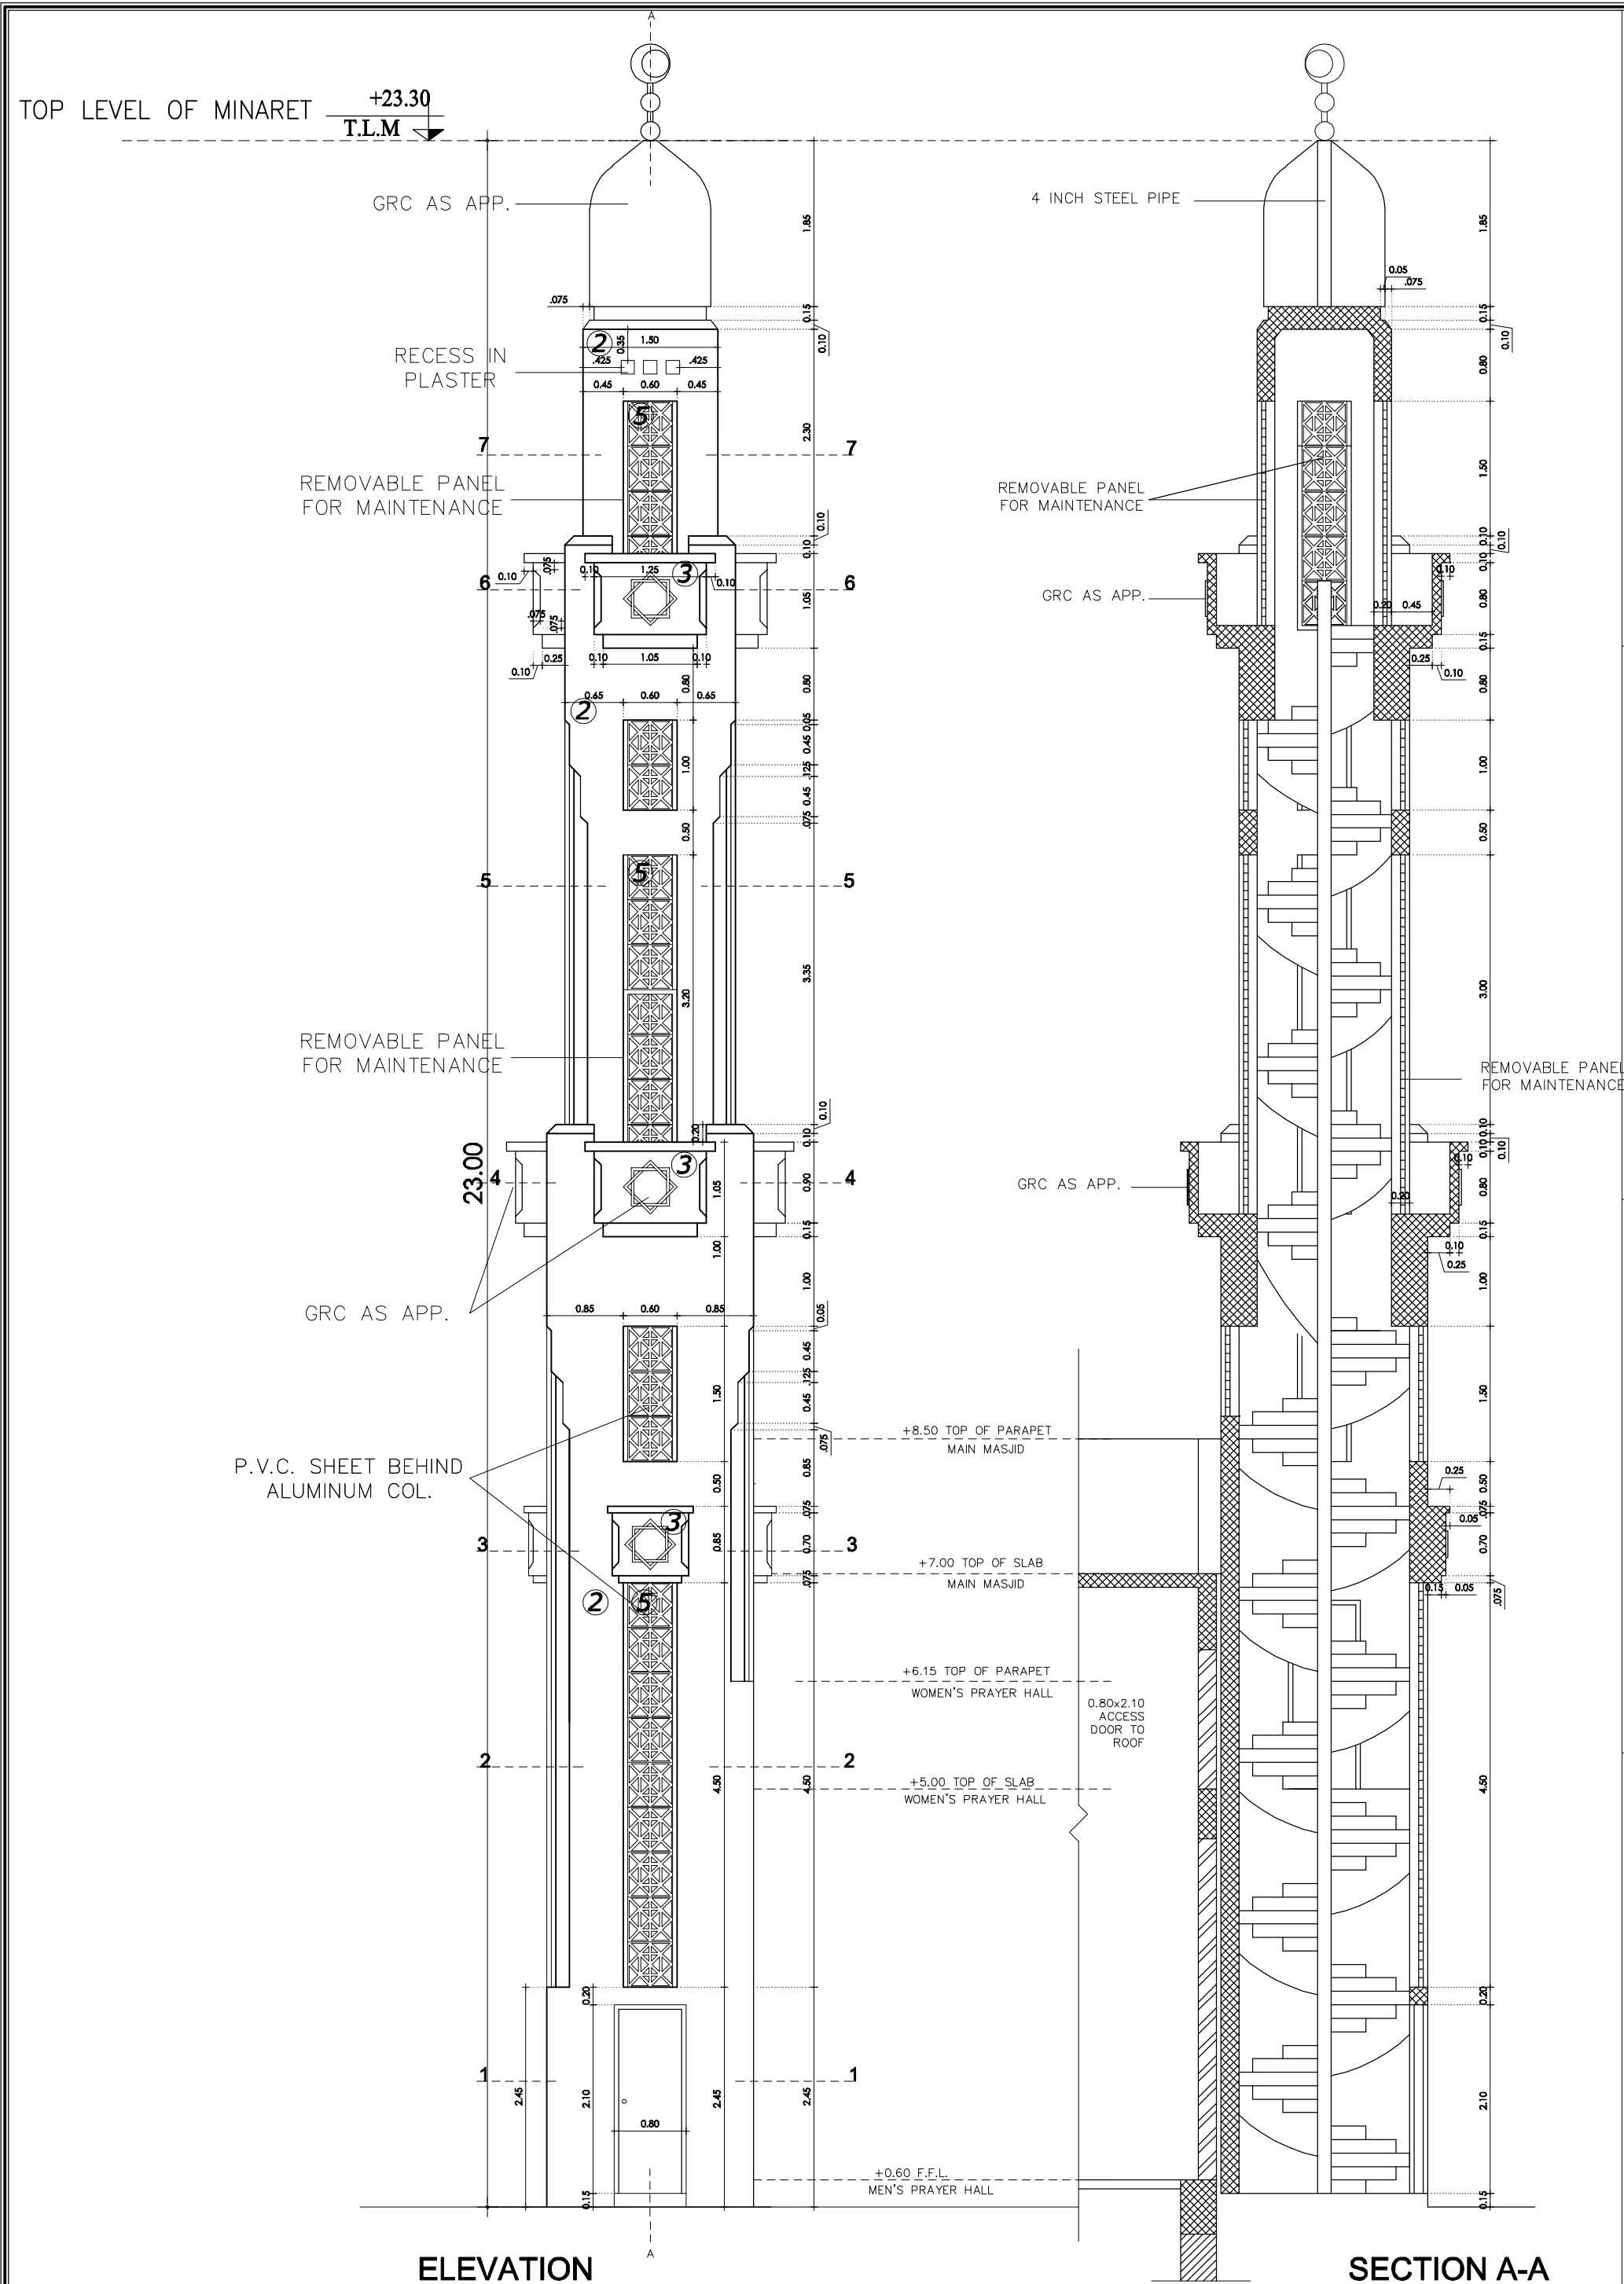

GENERAL NOTES:

1. IT IS NOT ALLOWED TO REPRODUCE THE SHEETS CONTENTS IN ANY FORM EXCEPT FOR THE PURPOSE FOR WHICH IT IS INTENDED.
2. THESE DRAWINGS ARE DIAGRAMMATIC AND SHALL NOT BE SCALED. ADDITIONAL DATA SHALL BE REQUESTED FROM THE CONSULTANCY THROUGH WRITTEN CLARIFICATION. VERIFY ALL EXISTING CONDITIONS AND DIMENSIONS BEFORE PROCEEDING WITH ANY PORTION OF ANY WORK.
3. NO CHANGES, MODIFICATIONS OR DEVIATIONS SHALL BE WRITTEN PERMISSION FROM **ALMASAH ENGINEERING CONSULTANTS**.
4. ALL WORK AS OUTLINED IN THESE DOCUMENTS, SHALL STRICTLY CONFORM TO ALL APPLICABLE CODES. IN THE EVENT OF A CONFLICT, THE MORE STRINGENT REQUIREMENT SHALL GOVERN AND BE MET.


23/05/2022
Architectural Approved
التوقيع

SIA - SM-01


حُكُومَةُ الشَّارِقَةِ
دائرة الشؤون الإسلامية

CONSULTANT STAMP


الماسية
للإستشارات الهندسية
مخططات فقط
AL-MASAH
Engineering Consultant
Drawings Only


الماسية
للإستشارات الهندسية
AL MASAH
Engineering Consultants
Sharjah ☎ 06 5 444 521 ☎ 06 5 444 523 📍 Office: 306, Al Fisal 2 Bldg., King Faisal St.

CLIENT: **GOVERNMENT OF SHARJAH - DEPARTMENT OF ISLAMIC AFFAIRS**

PROJECT: **(SIA - SM-01) PROPOSED MASJID + ABLUTION + IMAM HOUSE**

SHEET TITLE: **MINAR DETAILS**

ARCHITECT Arch. Mostafa Ramadan	TYPE ARCHITECTURE
STRUCTURAL Eng : Mohamed Gomaa	SHEET No. A - 16
CHECKED BY Eng : Mohamed Attia	Location : Plot No :
SCALE 1:100	DATE May - 2022
	Project No.

© ALL COPYRIGHTS IS RESERVED

The image contains two architectural drawings: an elevation and a section.

ELEVATION AT W2/W4

This drawing shows the facade of a building. It features two identical windows, each with a decorative arched pediment. The windows are set into a wall with a recessed plaster area. The elevation includes a horizontal scale at the top with dimensions: 0.20, 0.40, 0.20, 0.40, 0.20, 0.40, 0.20, 0.40, 0.20. The vertical scale on the left shows dimensions: 0.50, 0.55, 0.50, 0.40, 0.40, 1.70, 0.10, 1.30. The horizontal scale at the bottom shows dimensions: 1.00, 0.50, 1.00. The drawing is labeled "ELEVATION AT W2/W4" at the bottom.

SECTION F-F AT W4/W5

This drawing shows a cross-section of the building. It details the structure of the wall, including the parapet, slab, and floor levels. The section includes a vertical scale on the right with dimensions: 1.20, 0.95, 0.10, 0.40, 0.45, 2.35. The drawing is labeled "SECTION F-F AT W4/W5" at the bottom.

Architectural section drawing of a building facade, showing vertical levels and material details. The drawing includes the following elements and dimensions:

- Vertical Levels (from top to bottom):**
 - +6.15 TOP OF PARAPET
 - +4.95 TOP OF SLAB
 - +0.60 FIN. FLOOR LEVEL
 - +0.30 INTERLOCK LEVEL
- Dimensions (from top to bottom):**
 - 1.20 (from +6.15 to +4.95)
 - 0.95 (from +4.95 to 15cm TH: HOLLOW BLOCK)
 - 0.60 (15cm TH: HOLLOW BLOCK)
 - 1.70 (from 15cm TH: HOLLOW BLOCK to WINDOW AS/SCHED.)
 - 0.20 (from WINDOW AS/SCHED. to 20cm TH: HOLLOW BLOCK)
 - 0.90 (20cm TH: HOLLOW BLOCK)
- Materials and Details:**
 - PARAPET AS/DETAIL
 - BEAM AS/SCHED.
 - SLAB AS/SCHED.
 - GYP. DECOR AS/APP.
 - GRC AS APP.
 - 15cm TH: HOLLOW BLOCK
 - WINDOW AS/SCHED.
 - 20cm TH: HOLLOW BLOCK
- Other Labels:**
 - DETAIL D (pointing to a circular detail callout at the top)

[illegible]

PARAPET AS/DETAIL

PARAPET

SLAB

(P.)

1.20

BEAM AS/SCHED.

SLAB AS/SCHED.

1.25

20cm TH: HOLLOW BLOCK

3.10

LEVEL

LEVEL

Architectural section drawing showing a cross-section of a parapet wall and roof structure. Key levels and dimensions are indicated:

- Levels: +6.15 TOP OF PARAPET, +4.70 TOP OF SLAB, +0.60 FIN. FLOOR LEVEL, +0.30 INTERLOCK LEVEL.
- Dimensions: 0.50, 0.55, 0.50, 0.60, 3.40, 0.30, 0.20, 0.25, 0.20, 0.25, 1.20, 0.95, 3.40.
- Labels: PARAPET AS/DETAIL, BEAM AS/SCHED., SLAB AS/SCHED., GYP. DECOR AS/APP., R.C.C., GRC DECOR AS/APP., RECESS IN PLASTER (TYP.).

Architectural elevation drawing of a building facade. The drawing includes the following details:

- Vertical Dimensions (Left Side):** 0.50, 0.85, 0.50, 0.40, 3.10, 0.30.
- Horizontal Dimensions (Top):** 0.20, 0.20, 0.20.
- Horizontal Dimensions (Middle):** 0.75, 0.25, 0.25, 0.75.
- Horizontal Dimensions (Bottom):** 0.40, 2.60, 0.40.
- Vertical Dimensions (Bottom):** 0.40.
- Level Markers (Right Side):**
 - +6.15 TOP OF PARAPET
 - +4.95 TOP OF SLAB
 - +0.60 FIN. FLOOR LEVEL
 - +0.30 INTERLOCK LEVEL
- Material Callouts:**
 - RECESS IN PLASTER
 - RECESS IN PLASTER (TYP.)
 - GRC DECOR AS/APP.
 - GRC DECOR
 - GRANITE CLADDING
- Other Labels:** C (at top and bottom), 1.20, 1.25, 3.10 (on the right side).

SECTION C-C

TYP. DETAIL AT FRONT ENTRANCE - MAIN MOSQUE

1. IT IS NOT ALLOWED TO REPRODUCE THE SHEETS CONTENTS IN ANY FORM EXCEPT FOR THE PURPOSE FOR WHICH IT IS INTENDED.
2. THESE DRAWINGS ARE DIAGRAMMATIC AND SHALL NOT BE SCALED. ADDITIONAL DATA SHALL BE REQUESTED FROM THE CONSULTANCY THROUGH WRITTEN CLARIFICATION. VERIFY ALL EXISTING CONDITIONS AND DIMENSIONS BEFORE PROCEEDING WITH ANY PORTION OF ANY WORK.
3. NO CHANGES, MODIFICATIONS OR DEVIATIONS SHALL BE WRITTEN PERMISSION FROM **ALMASAH ENGINEERING CONSULTANTS**.
4. ALL WORK AS OUTLINED IN THESE DOCUMENTS, SHALL STRICTLY CONFORM TO ALL APPLICABLE CODES. IN THE EVENT OF A CONFLICT, THE MORE STRINGENT REQUIREMENT SHALL GOVERN AND BE MET.

حُكُومَةُ الشَّارِقَةِ
دائرة الشؤون الإسلامية



المسرح
للإستشارات الهندسية
مخططات فقط
AL-Masrah
Engineering Consultant
Drawings Only



GOVERNMENT OF SHARJAH -
DEPARTMENT OF ISLAMIC AFFAIRS

(SIA - SM-01)
PROPOSED MASJID + ABLUTION +
IMAM HOUSE

TITLE: **PROPOSAL - 4**
SECTION A-A , SECTION B-B

ARCHITECT
Arlene M. G. G.

STRUCTURAL

CHECKED BY

Eng : Mohamed

1:100

Mustafa

UKA Chame

Shameo

May

TYPE ARCHITECTURE

SHEET	A 15
-------	------

Plot No :	

Project
No.

The drawings illustrate the architectural details of the Men's Prayer Hall. The plan view shows the layout of the hall, including the location of windows (W1) and bookcases. The elevation at W1 shows the facade with two windows and a central door. The section A-A and G-G show the vertical structure, including the roof, walls, and floor.

PLAN

ELEVATION AT W1

SECTION A-A

SECTION G-G

ELEVATION AT W1

SECTION G-G



1. IT IS NOT ALLOWED TO REPRODUCE THE SHEETS CONTENTS IN ANY FORM EXCEPT FOR THE PURPOSE FOR WHICH IT IS INTENDED.
2. THESE DRAWINGS ARE DIAGRAMMATIC AND SHALL NOT BE SCALED. ADDITIONAL DATA SHALL BE REQUESTED FROM THE CONSULTANCY THROUGH WRITTEN CLARIFICATION. VERIFY ALL EXISTING CONDITIONS AND DIMENSIONS BEFORE PROCEEDING WITH ANY PORTION OF ANY WORK.
3. NO CHANGES, MODIFICATIONS OR DEVIATIONS SHALL BE WRITTEN PERMISSION FROM **ALMASAH ENGINEERING CONSULTANTS**.
4. ALL WORK AS OUTLINED IN THESE DOCUMENTS, SHALL STRICTLY CONFORM TO ALL APPLICABLE CODES. IN THE EVENT OF A CONFLICT, THE MORE STRINGENT REQUIREMENT SHALL GOVERN AND BE MET.

حُكُومَةُ الشَّارِقَةِ
دائرة الشؤون الإسلامية


المباشرة
للإستشارات الهندسية
مخططات فقط
AL-Masah
Engineering Consultant
Drawings Only




PROJECT:	(SIA - SM-01) PROPOSED MASJID + ABLUTION + IMAM HOUSE
----------	---

SHEET TITLE: **PROPOSAL - 4**
SECTION A-A , SECTION B-B


ARCHITECT Arch. Mostafa Ramadan		TYPE	ARCHITECTURE
STRUCTURAL Eng : Mohamed Gomaa		SHEET No.	A - 18
CHECKED BY Eng : Mohamed Attia		Location :	
		Plot No :	
SCALE 1:100	DATE May - 2022	Project No.	

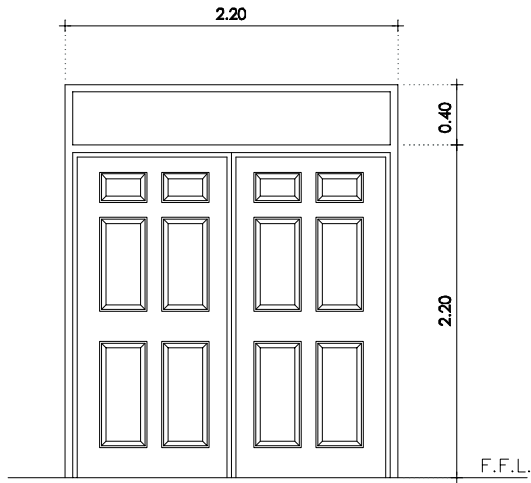


WOODEN DOUBLE LEAF DECORATIVE
SOLID PANEL AS PER APPROVAL

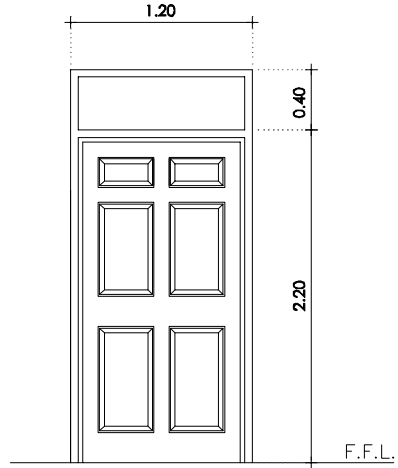


WOODEN SINGLE LEAF DECORATIVE
SOLID PANEL AS PER APPROVAL

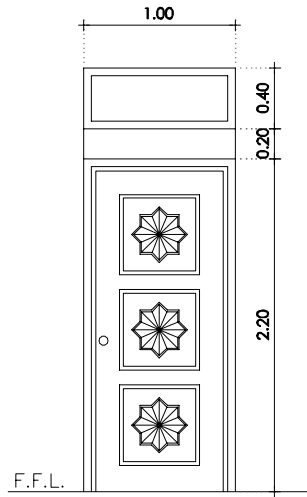


WOODEN SINGLE LEAF DECORATIVE
SOLID PANEL AS PER APPROVAL

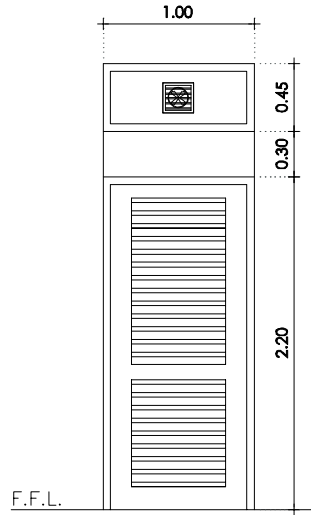


HEAVY SECTION, POWDER COATED,
LOUVERED ALUMINUM DOOR
COLOR AS PER APPROVAL

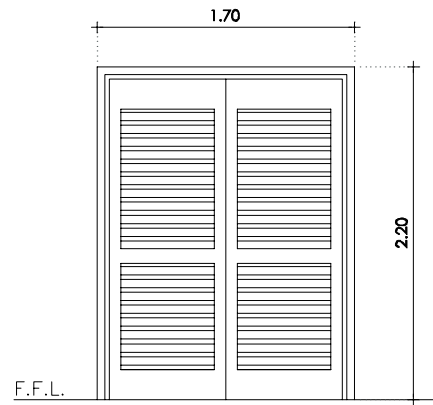


HEAVY SECTION, POWDER COATED,
LOUVERED ALUMINUM DOOR
COLOR AS PER APPROVAL

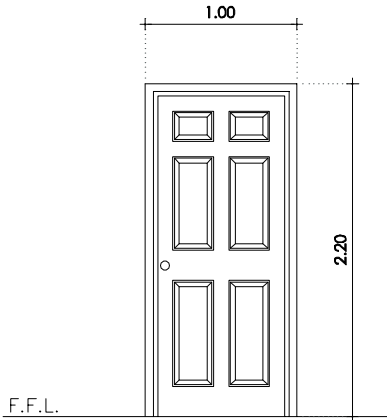


WOODEN SINGLE LEAF DECORATIVE
SOLID PANEL AS PER APPROVAL

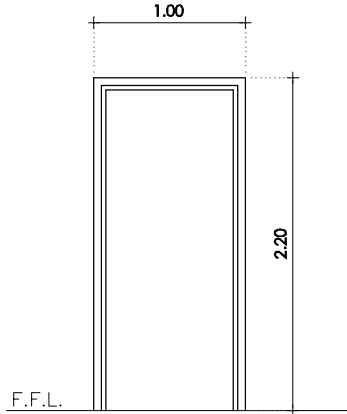


SINGLE LEAF WOODEN FLUSH DOOR
POLISHED WITH LACQUER POLISH AS PER APPROVAL

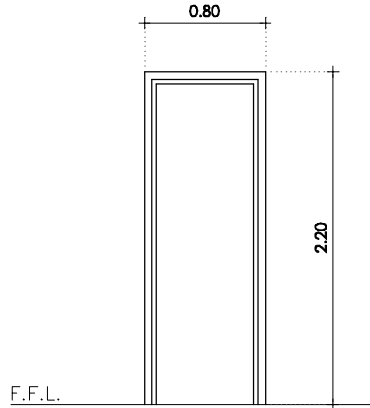


SINGLE LEAF WOODEN FLUSH DOOR
POLISHED WITH LACQUER POLISH AS PER APPROVAL

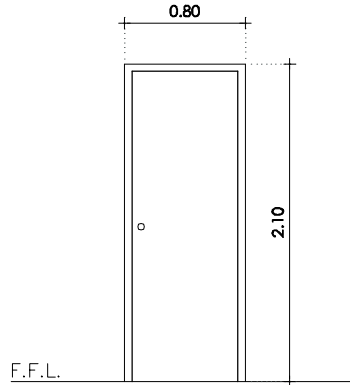

MEDIUM SECTION, POWDER COATED,
LOUVERED ALUMINUM DOOR
COLOR AS PER APPROVAL

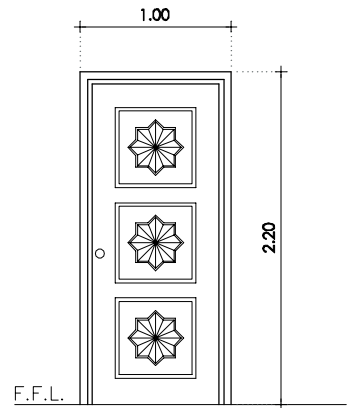

WOODEN SINGLE LEAF DECORATIVE
SOLID PANEL AS PER APPROVAL

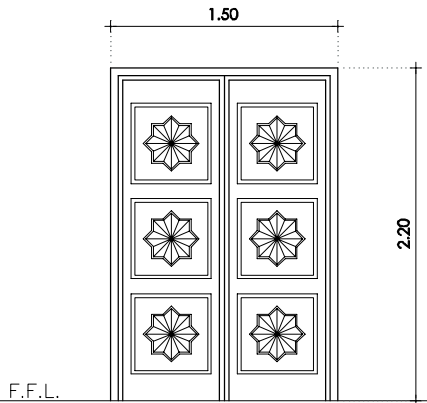

WOODEN DOUBLE LEAF DECORATIVE
SOLID PANEL AS PER APPROVAL

GENERAL DOOR/WINDOW NOTES

- DRAWINGS ARE NOT TO BE SCALED.
- THIS DRAWING IS TO BE READ IN CONJUNCTION WITH ALL OTHER RELEVANT DRAWINGS.
- CONTRACTOR IS TO CONFIRM AND WORK TO ACTUAL EXIST. DIMENSIONS ON SITE.
- ALL DIMENSIONS RELATE TO STRUCTURAL OPENINGS UNLESS OTHERWISE NOTED.
- CONTRACTOR SHALL SUBMIT ALL NECESSARY DOOR/WINDOW SHOP DRAWINGS FOR APPROVAL PRIOR TO FABRICATION AND INSTALLATION.
- ALL WOODEN DOORS TO HAVE ARCHITRAVES ON BOTH SIDES AS PER APPROVAL.
- ALL FLUSH DOOR SHUTTERS SHOULD BE MIN. 75% SOLID INSIDE AS PER APPROVAL.
- ALL ALUMINUM DOORS/WINDOWS TO HAVE ALUMINUM ARCHITRAVE BOTH SIDES AS PER APPROVAL UNLESS NOTED OTHERWISE.
- ALL DOOR CLOSERS ARE TO HAVE 90 DEGREE HOLD OPEN FACILITY.
- ALL EXTERNAL DOORS SHALL HAVE WEATHER SEALS.
- ALL GLAZING BELOW 90cm ABOVE FINISH FLOOR LEVEL SHALL BE WITH TEMPERED GLASS

TIMBER OPENINGS

- ALL DOORS SHALL BE COMPLETE WITH 1-1/2 PAIR OF BRASS HINGES (3 PAIR HEAVY DUTY FOR DOUBLE DOORS) & APPROVED QUALITY LOCKS, CLOSERS, HANDLES, BOLTS AND DOOR STOPS AS NOTED.
- CONTRACTOR SHALL SUBMIT SAMPLES OF ALL IRON MONGERY TO BE USED FOR CONSULTANTS APPROVAL PRIOR TO PLACING AN ORDER.
- DOOR FRAME SHALL BE SECURED TO OPENINGS WITH MIN. 3 No.'s 10mm dia. & 4" LONG EXPANDING BOLTS.
- ALL INSIDE FACES OF TIMBER FRAMES TO BE PAINTED WITH PRESERVATIVE PAINT OF APPROVED QUALITY.
- ALL PANELLED DOORS SHALL HAVE STILES, TOP RAIL & MIDDLE RAIL MIN. 4" WIDE. BOTTOM RAIL MIN. 6" WIDE. DECORATIVE PANELS AS/APPROVED DESIGN.
- PROVIDE 3/4" x 9" OR 5" MARINE PLYWOOD SUBFRAMES TO ALL DOOR OPENINGS.
- ALL FLUSH DOORS TO BE 100% SOLID CORE OR 80% SEMI-SOLID CORE WITH HARDWOOD LIPPING ALL AROUND AS PER SPECIFICATIONS.
- PROVIDE 2" x 9" OR 2" x 5" DECORATIVE RED MERRANTI WOOD FRAME ON BOTH SIDES.

ALUMINUM OPENINGS

- CONTRACTOR SHALL SUBMIT ALL SAMPLES OF ALL ALUM. SECTIONS, GLAZING, LOCKS, HANDLES ETC., FOR APPROVAL OF CONSULTANT PRIOR TO PLACING AN ORDER.
- ALL ALUMINUM OPENINGS TO HAVE .75" MARINE PLY SUB-FRAME OR TREATED RED MERANTI AS/APPROVAL.
- ALL ALUMINUM OPENINGS TO BE SEALED WITH 2 PARTS POLYSULPHIDE SEALANT MIN .25" THICK.
- DRAINAGE WEEP HOLES TO BE PROVIDED AT THE BOTTOMS OF ALL ALUMINUM FRAMES AS PER APPROVAL.
- ALL ALUMINUM DOORS AND WINDOW S SHALL BE COMPLETE WITH APPROPRIATE HANDLES, LOCKS, SLIDING GEAR ETC., WHICH SHALL BE OF APPROVED QUALITY AND DESIGN.
- WHERE EVER MARINE PLY SUBFRAME IS EXPOSED PROVIDE 1/32" THICK RED MERRANTI COVER SLIP (SCREWED) TO CONCEAL THE SAME/EXPOSED SURFACES TO BE TREATED WITH APP. PRESERVATIVE PAINT.
- ALL SILL HEIGHTS ARE FROM FINISH FLOOR LEVEL UNLESS NOTED OTHERWISE.
- FLY MESH SCREENS TO BE FROM INSIDE UNLESS NOTED OTHERWISE

GENERAL NOTES:

- IT IS NOT ALLOWED TO REPRODUCE THE SHEETS CONTENTS IN ANY FORM EXCEPT FOR THE PURPOSE FOR WHICH IT IS INTENDED.
- THESE DRAWINGS ARE DIAGRAMMATIC AND SHALL NOT BE SCALED. ADDITIONAL DATA SHALL BE REQUESTED FROM THE CONSULTANCY THROUGH WRITTEN CLARIFICATION. VERIFY ALL EXISTING CONDITIONS AND DIMENSIONS BEFORE PROCEEDING WITH ANY PORTION OF ANY WORK.
- NO CHANGES, MODIFICATIONS OR DEVIATIONS SHALL BE WRITTEN PERMISSION FROM **ALMASAH ENGINEERING CONSULTANTS**.
- ALL WORK AS OUTLINED IN THESE DOCUMENTS, SHALL STRICTLY CONFORM TO ALL APPLICABLE CODES. IN THE EVENT OF A CONFLICT, THE MORE STRINGENT REQUIREMENT SHALL GOVERN AND BE MET.

SIA - SM-01



حُكُومَةُ الشَّارِقَةِ
دائرة الشؤون الإسلامية

CONSULTANT STAMP



CLIENT:

GOVERNMENT OF SHARJAH -
DEPARTMENT OF ISLAMIC AFFAIRS


PROJECT:

(SIA - SM-01)
PROPOSED MASJID + ABLUTION +
IMAM HOUSE

SHEET TITLE:

DETAIL OF DOORS

ARCHITECT Arch. Mostafa Ramadan	TYPE	ARCHITECTURE
STRUCTURAL Eng : Mohamed Gomaa	SHEET No.	A - 19
CHECKED BY Eng : Mohamed Attia	Location :	
SCALE 1:100	Plot No :	
DATE May - 2022	Project No.	

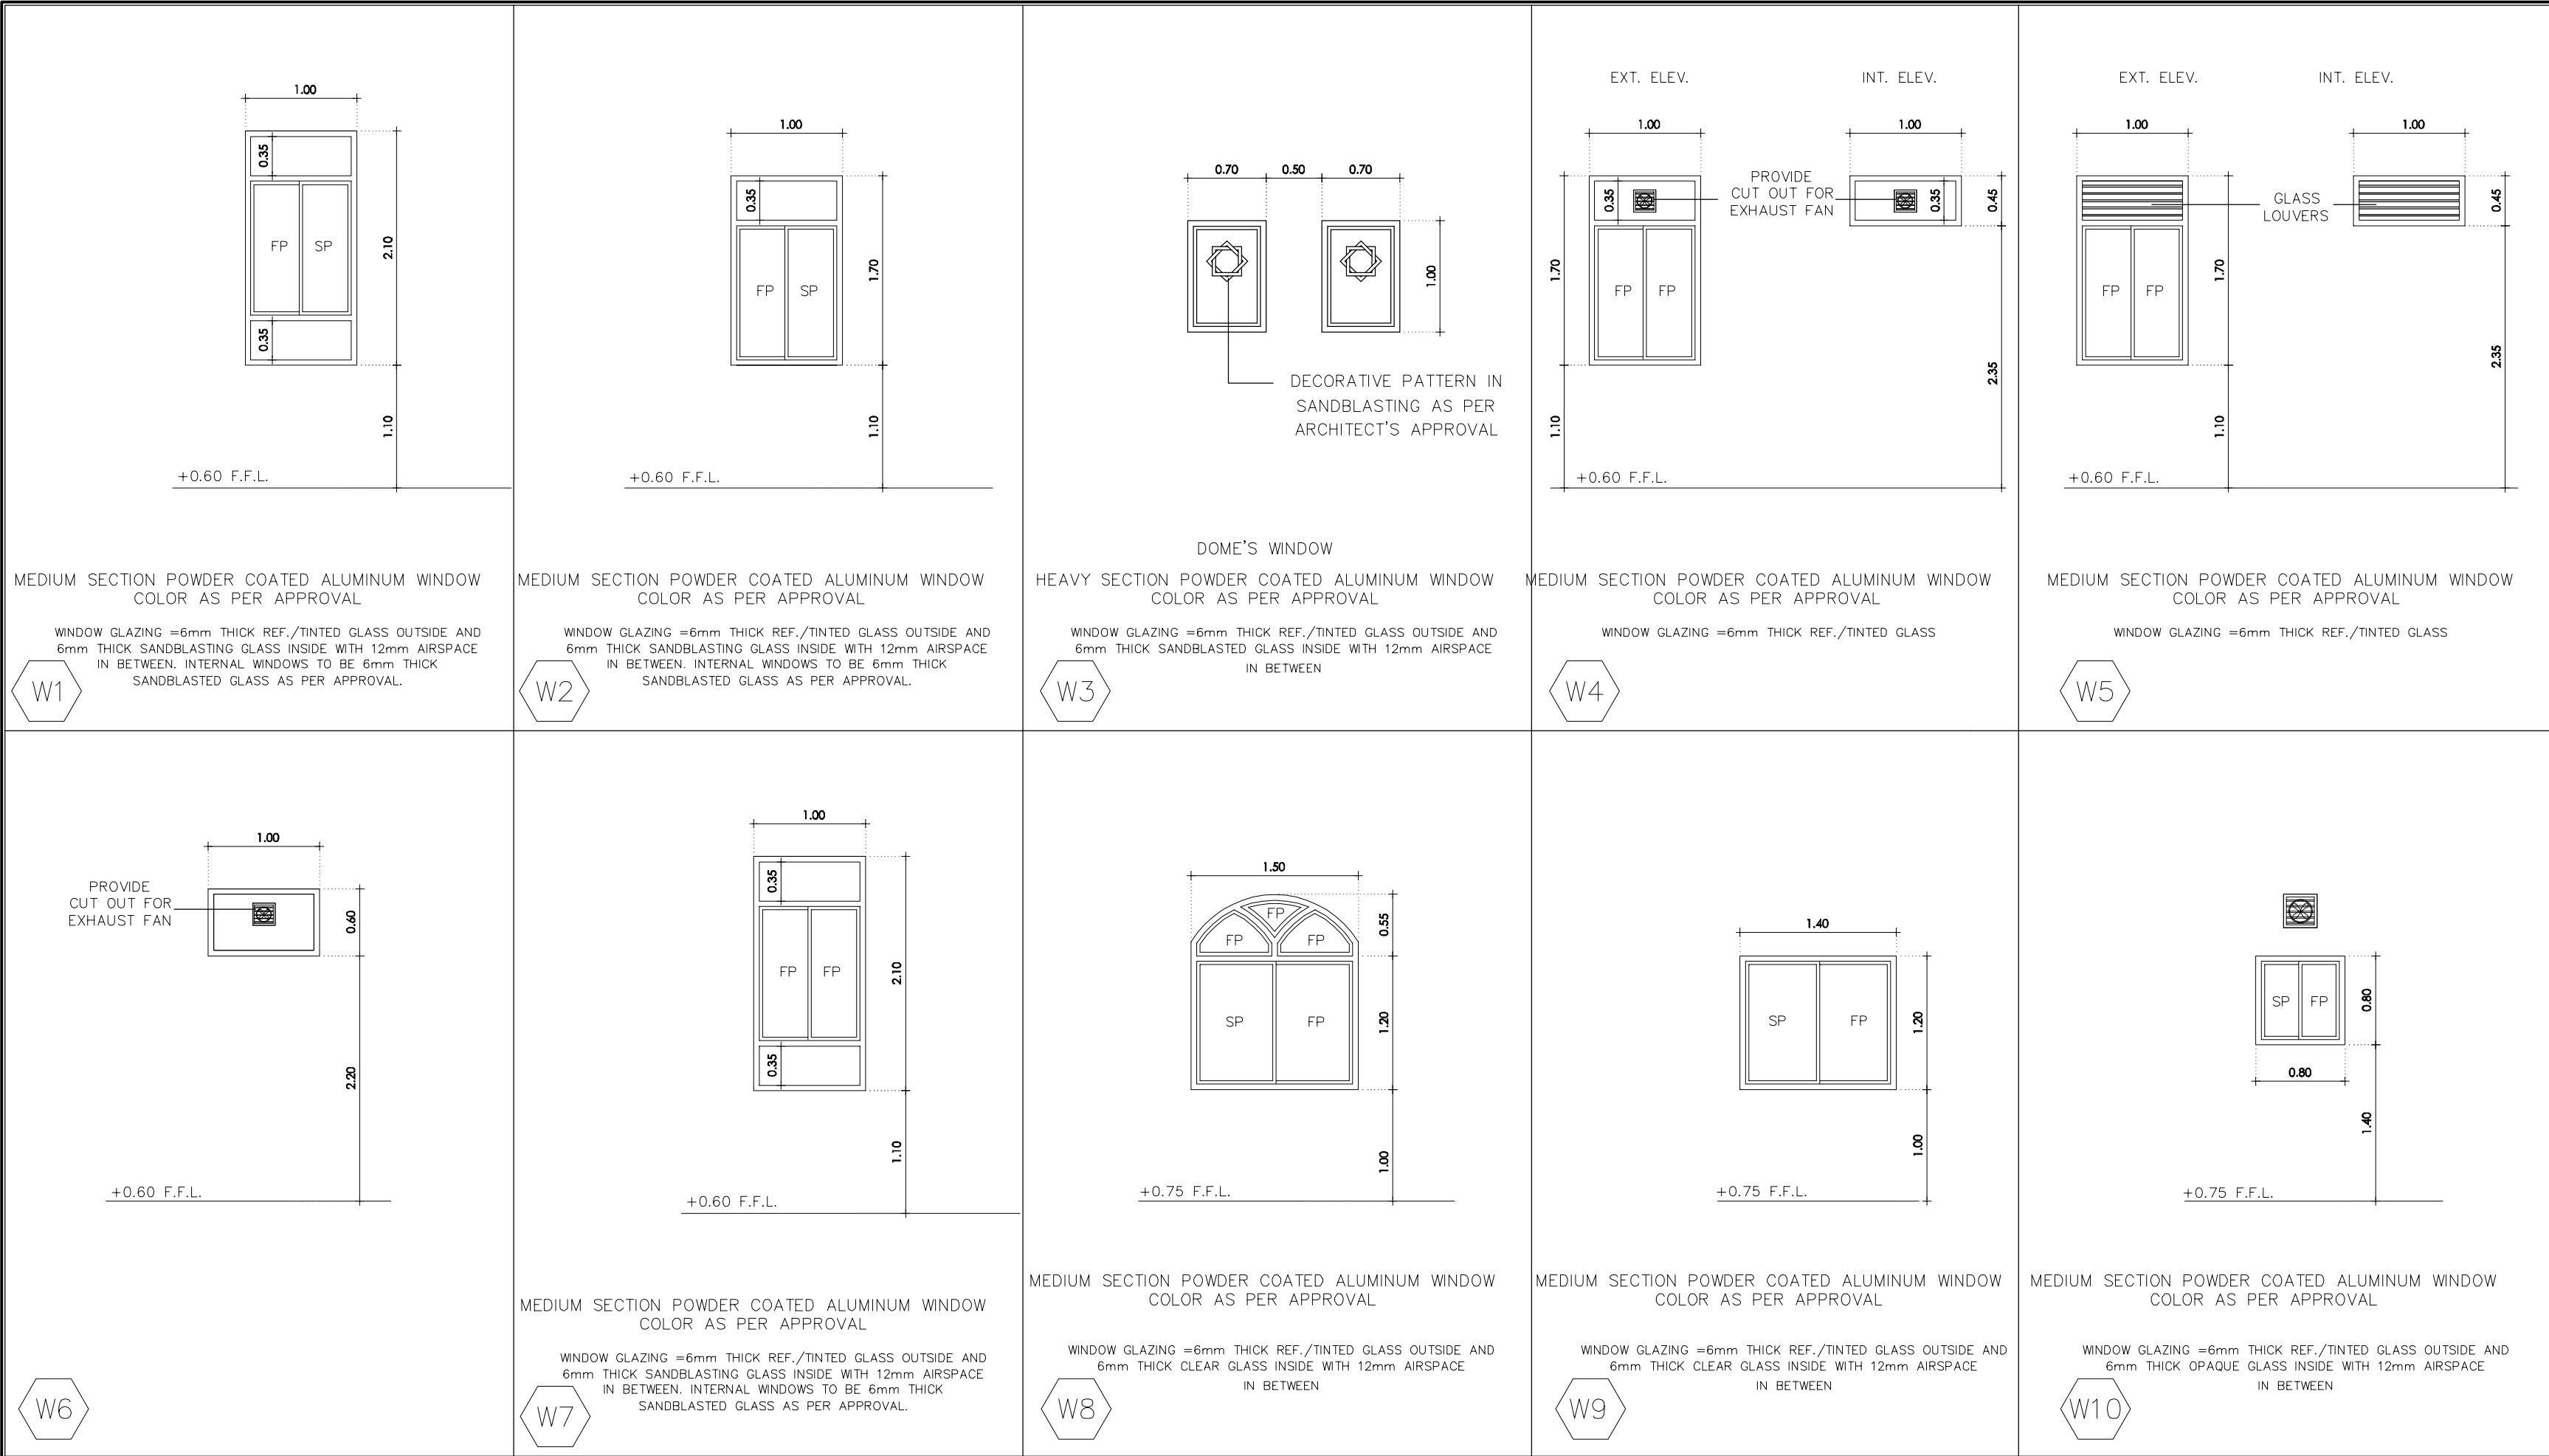

GENERAL NOTES:

1.IT IS NOT ALLOWED TO REPRODUCE THE SHEETS CONTENTS IN ANY FORM EXCEPT FOR THE PURPOSE FOR WHICH IT IS INTENDED.

2. THESE DRAWINGS ARE DIAGRAMMATIC AND SHALL NOT BE SCALED. ADDITIONAL DATA SHALL BE REQUESTED FROM THE CONSULTANCY THROUGH WRITTEN CLARIFICATION. VERIFY ALL EXISTING CONDITIONS AND DIMENSIONS BEFORE PROCEEDING WITH ANY PORTION OF ANY WORK.

3. NO CHANGES, MODIFICATIONS OR DEVIATIONS SHALL BE WRITTEN PERMISSION FROM **ALMASAH ENGINEERING CONSULTANTS**.

4. ALL WORK AS OUTLINED IN THESE DOCUMENTS, SHALL STRICTLY CONFORM TO ALL APPLICABLE CODES. IN THE EVENT OF A CONFLICT, THE MORE STRINGENT REQUIREMENT SHALL GOVERN AND BE MET.

SIA - SM-01



CONSULTANT STAMP



CLIENT: **GOVERNMENT OF SHARJAH -
DEPARTMENT OF ISLAMIC AFFAIRS**

PROJECT: **(SIA - SM-01)
PROPOSED MASJID + ABLUTION +
IMAM HOUSE**

SHEET TITLE: **DETAIL OF WINDOWS**

ARCHITECT Arch. Mostafa Ramadan	TYPE	ARCHITECTURE
STRUCTURAL Eng : Mohamed Gomaa	SHEET No.	A - 20
CHECKED BY Eng : Mohamed Attia	Location :	
SCALE 1:100	DATE May - 2022	Project No.

GENERAL DOOR/WINDOW NOTES

- 1- DRAWINGS ARE NOT TO BE SCALED.
- 2- THIS DRAWING IS TO BE READ IN CONJUNCTION WITH ALL OTHER RELEVANT DRAWINGS.
- 3- CONTRACTOR IS TO CONFIRM AND WORK TO ACTUAL EXIST. DIMENSIONS ON SITE.
- 4- ALL DIMENSIONS RELATE TO STRUCTURAL OPENINGS UNLESS OTHERWISE NOTED.
- 5- CONTRACTOR SHALL SUBMIT ALL NECESSARY DOOR/WINDOW SHOP DRAWINGS FOR APPROVAL PRIOR TO FABRICATION AND INSTALLATION.
- 6- ALL WOODEN DOORS TO HAVE ARCHITRAVES ON BOTH SIDES AS PER APPROVAL.
- 7- ALL FLUSH DOOR SHUTTERS SHOULD BE MIN. 75% SOLID INSIDE AS PER APPROVAL.
- 8- ALL ALUMINUM DOORS/WINDOWS TO HAVE ALUMINUM ARCHITRAVE BOTH SIDES AS PER APPROVAL UNLESS NOTED OTHERWISE.
- 9- ALL DOOR CLOSERS ARE TO HAVE 90 DEGREE HOLD OPEN FACILITY.
- 10- ALL EXTERNAL DOORS SHALL HAVE WEATHER SEALS.
- 11- ALL GLAZING BELOW 90cm ABOVE FINISH FLOOR LEVEL SHALL BE WITH TEMPERED GLASS

TIMBER OPENINGS

- 1- ALL DOORS SHALL BE COMPLETE WITH 1-1/2 PAIR OF BRASS HINGES (3 PAIR HEAVY DUTY FOR DOUBLE DOORS) & APPROVED QUALITY LOCKS, CLOSERS, HANDLES, BOLTS AND DOOR STOPS AS NOTED.
- 2- CONTRACTOR SHALL SUBMIT SAMPLES OF ALL IRON MONGERY TO BE USED FOR CONSULTANTS APPROVAL PRIOR TO PLACING AN ORDER.
- 3- DOOR FRAME SHALL BE SECURED TO OPENINGS WITH MIN. 3 No.'s 10mm dia. & 4" LONG EXPANDING BOLTS.
- 4- ALL INSIDE FACES OF TIMBER FRAMES TO BE PAINTED WITH PRESERVATIVE PAINT OF APPROVED QUALITY.
- 5- ALL PANELLED DOORS SHALL HAVE STILES, TOP RAIL & MIDDLE RAIL MIN. 4" WIDE. BOTTOM RAIL MIN. 8" WIDE. DECORATIVE PANELS AS/APPROVED DESIGN.
- 6- PROVIDE 3/4" x 9" OR 5" MARINE PLYWOOD SUBFRAMES TO ALL DOOR OPENINGS.
- 7- ALL FLUSH DOORS TO BE 100% SOLID CORE OR 80% SEMI-SOLID CORE WITH HARDWOOD LIPPING ALL AROUND AS PER SPECIFICATIONS.
- 8- PROVIDE 2" x 9" OR 2" x 5" DECORATIVE RED MERRANTI WOOD FRAME ON BOTH SIDES.

ALUMINUM OPENINGS

- 1- CONTRACTOR SHALL SUBMIT ALL SAMPLES OF ALL ALUM. SECTIONS, GLAZING, LOCKS, HANDLES ETC., FOR APPROVAL OF CONSULTANT PRIOR TO PLACING AN ORDER.
- 2- ALL ALUMINUM OPENINGS TO HAVE .75" MARINE PLY SUB-FRAME OR TREATED RED MERANTI AS/APPROVAL.
- 3- ALL ALUMINUM OPENINGS TO BE SEALED WITH 2 PARTS POLYSULPHIDE SEALANT MIN .25" THICK.
- 4- DRAINAGE WEEP HOLES TO BE PROVIDED AT THE BOTTOMS OF ALL ALUMINUM FRAMES AS PER APPROVAL.
- 5- ALL ALUMINUM DOORS AND WINDOW S SHALL BE COMPLETE WITH APPROPRIATE HANDLES, LOCKS, SLIDING GEAR ETC., WHICH SHALL BE OF APPROVED QUALITY AND DESIGN.
- 6- WHERE EVER MARINE PLY SUBFRAME IS EXPOSED PROVIDE 1/32" THICK RED MERRANTI COVER SLIP (SCREWED) TO CONCEAL THE SAME/EXPOSED SURFACES TO BE TREATED WITH APP. PRESERVATIVE PAINT.
- 7- ALL SILL HEIGHTS ARE FROM FINISH FLOOR LEVEL UNLESS NOTED OTHERWISE.
- 8- FLY MESH SCREENS TO BE FROM INSIDE UNLESS NOTED OTHERWISE

